
Схема наружных сетей и генплана (предварительная, М 1:250)

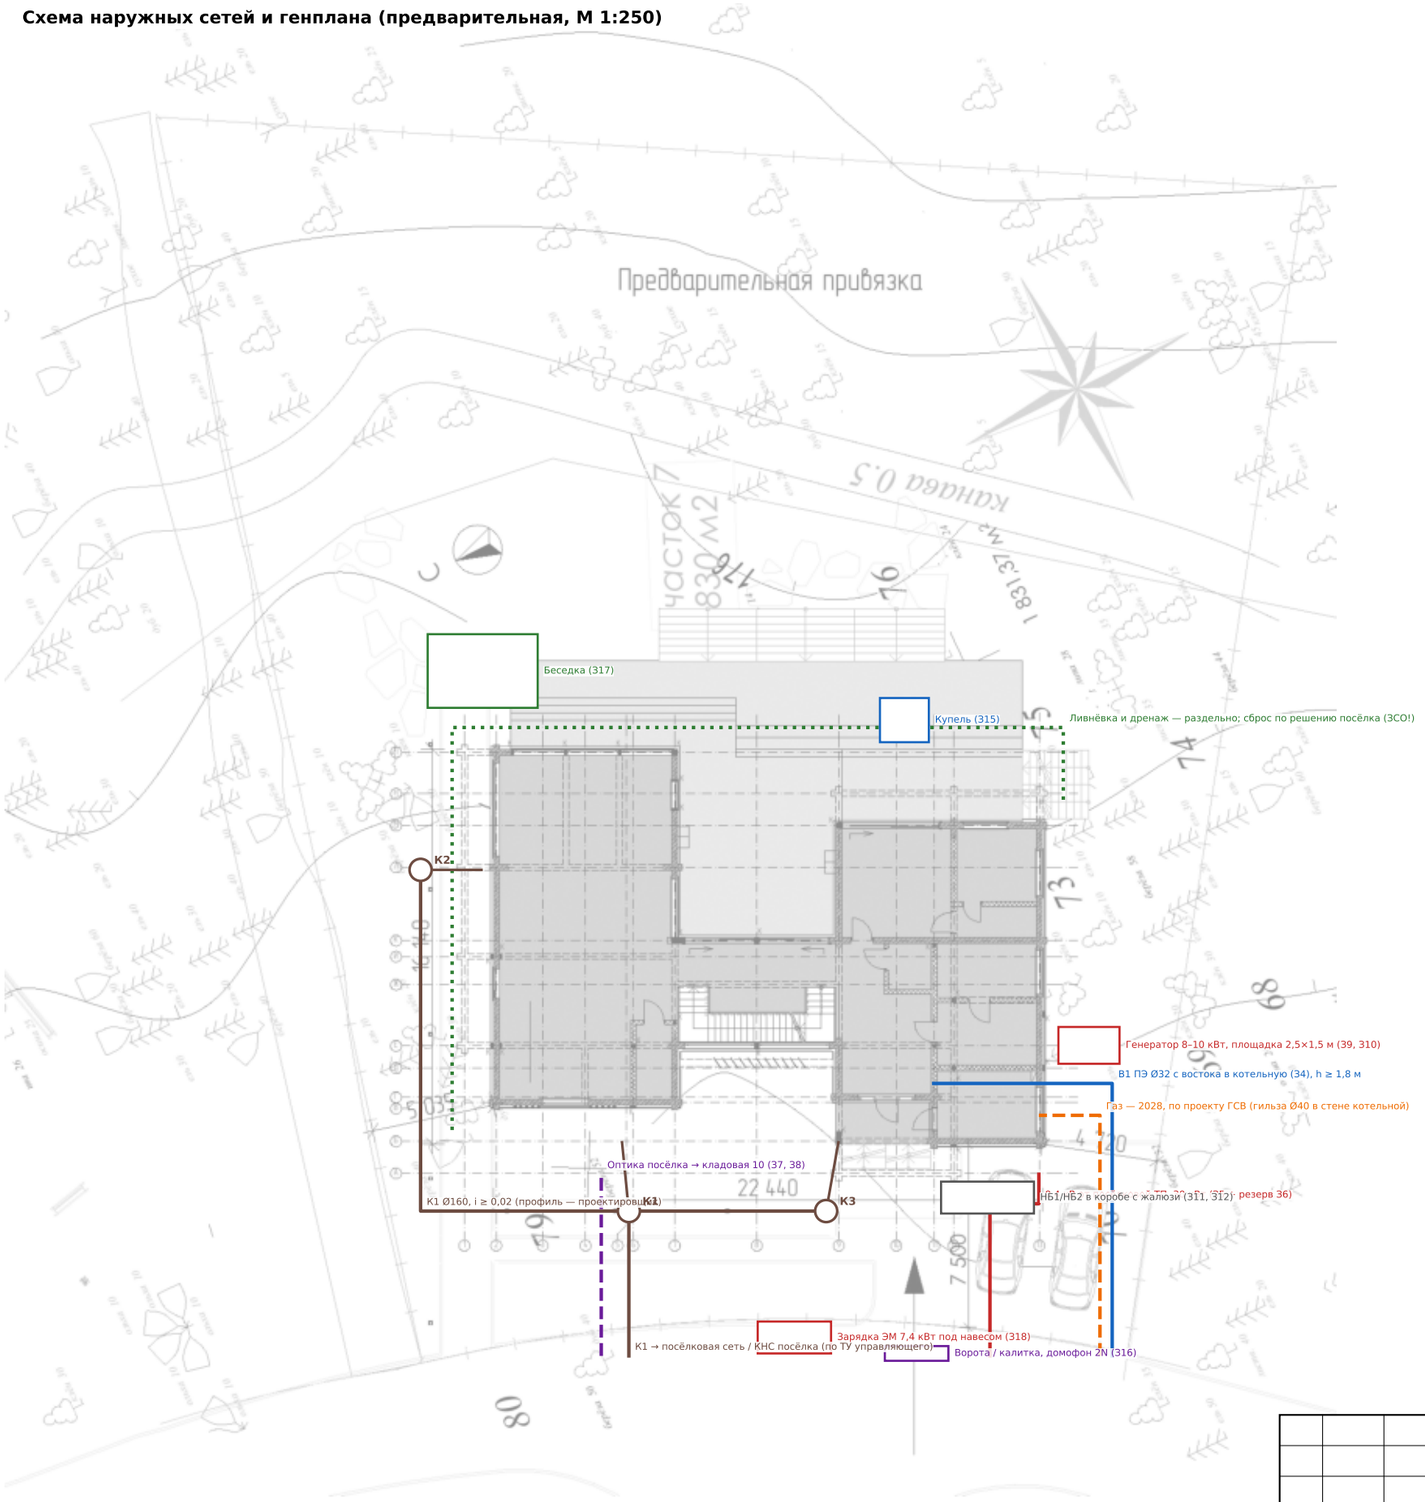

Условные обозначения

- Канализация бытовая
- Водопровод
- Кабель электроснабжения 0,4 кВ
- Слаботочные сети
- Газопровод (этап 2)
- Дренаж / ливневая канализация

Примечания

1. Концепт заказчика. Все ТУ (вода, канализация, 0,4 кВ) выдаёт управляющий посёлком; договоров пока нет. Трассы — до ТУ и топосъёмки с отметками.

2. Рельеф понижается от дороги (≈ 80) к дому (76–79) и к канаве (68–73); перепад по участку ≈ 2,5 м. Самотёк от выпусков — по профилю от каждого выпуска (проектировщик).

3. Колодцы К1–К3 и выпуски — по 291-ВК. КНС — посёлковая в хоззоне; своя — только если профиль не даёт самотёка.

4. 1-й пояс ЗСО Истринского гидроузла — 100 м от уреза: трубопроводы и сброс стоков запрещены. Трассы и ливнёвку согласовать с посёлком.

5. Контур заземления — за отмосткой, h ≥ 0,7 м, до обратной засыпки (291-МЗ.ПС).

6. Закладные в плите — по ведомости БР-ЗК (31–322).

Изм.	Кол.уч	Лист	№док.	Подп.	Дата
Разраб.					
Проверил					
ГИП					
Н.контр.					

291-НС

Индивидуальный жилой дом «Ромарио»
Московская обл., г. о. Истра, посёлок «Берта», участок 1

Схема наружных сетей и генплана (предварительная)

Стадия	Лист	Листов
Э	1	2

Формат А3

Ведомость наружных сетей (предварительная)

Сеть	От	До	Материал, Ø	Длина ≈, м	Что нужно для проекта
К1 бытовая	3 выпуска Ø160 (31–33)	К1–К3 → посёлковая сеть / КНС	ПП Ø160	≈ 45	ТУ управляющего, отметки лотков; профиль от каждого выпуска
В1 водопровод	Посёлковая сеть	Котельная, ввод с востока (34 Ø110)	ПЭ100 SDR11 Ø32	≈ 20	Давление и анализ воды — запрос управляющему
Электро 0,4 кВ	Посёлковая ТП	ГРЩ в котельной (35 Ø110 + 36 Ø50)	по ТУ (мин. 4×35 Al)	≈ 20	Лимит на дом (принято 30 кВт), ТУ к 16.11
Генератор	Площадка у восточного фасада	ГРЩ, АВР (39, 310)	ВБбШв в ПНД	≈ 10	Мощность 8–10 кВт; посёлковый резерв — по решению
Слаботочка	Оптика посёлка, ворота	Стойка в кладовой 10 (37, 38, 316)	ПНД Ø50	≈ 40	Провайдер: Истранет / Ростелеком
Газ (2028)	Сеть посёлка после ПРГ	Котельная (гильза Ø40)	ПЭ / сталь	≈ 15	Проект ГСВ после пуска ПРГ
Ливнёвка / дренаж	Водостоки, дренаж	По схеме посёлка	ПВХ Ø110–160	≈ 90	Сброс — с учётом ЗСО; вертикальная планировка до 30.11
Прочее	Купель, беседка, ЭМ, полив	315, 317, 318, 313, 314	ПНД Ø50	—	Решения 18.10

Что нужно для рабочего проекта наружных сетей и генплана

1. Топосъёмка М 1:500 с отметками рельефа и существующими сетями (на листе 3 АПР есть горизонтали — нужна исполнительная съёмка в DWG).
2. Зоны с особыми условиями: ЗСО гидроузла (100 м), канава 0,5 м у участка; отступы по генплану.
3. ТУ управляющего посёлком: вода (давление), канализация (отметки), 0,4 кВ (лимит на дом).
4. Единая схема водоотведения и вертикальная планировка посёлка — до 30.11.2026.

Изм.	Кол.уч	Лист	№док.	Подп.	Дата
Разраб.					
Проверил					
ГИП					

291-НС

Пояснения и ведомость сетей

Стадия	Лист	Листов
Э	2	

Формат А3