STROYHOUSE

ДЕРЕВЯННЫЕ ДОМА

Проект дома "Берта Ромарио"



Москва 2026 г.

ООО "Строй Хауз"
Москва, Новорижское шоссе14 км,
д. Веледниково, ул. Живописная д 25.

Ведомость листов		
Лист	Наименование	Примечание
1	Титульный лист	
2	Общие данные	
3	Схема размещения	
4	план 1 этажа	
5	План 2 этажа	
6	План чердака	
7	План кровли	
8	Разрез 1-1	
9	Разрез 2-2	
10	Разрез 3-3	
11	Разрез 4-4	
12	Разрез 5-5	
13	Разрез 6-6	
14	Разрез 7-7	
15	Разрез 8-8	
16	Фасад 1-13	
17	Фасад 13-1	
18	Фасад А-П	
19	Фасад П-А	
20	Перспективное изображение	
21	Перспективное изображение	
22	Перспективное изображение	
23	Перспективное изображение	
24	Перспективное изображение	
25	Перспективное изображение	
26	Перспективное изображение	
27	Перспективное изображение	
28	Перспективное изображение	
29	Перспективное изображение	
30	Перспективное изображение	
31	Перспективное изображение	
32	Перспективное изображение	

1. Объемно-планировочное решение:

Дом запроектирован, как двухэтажное здание.

Высота этажей в чистоте:

1 этаж – 3,70 м.

2 этаж – 3,40 м. (см. разрезы)

За отметку 0,000 принята отмета чистого пола 1 этажа.

2. Конструктивные решения:

Фундамент здания – Ж/Б плита, забивные сваи

Наружние стены – клееный брус, толщина 240 мм.

Внутренние несущие стены – клееный брус, толщина 240 мм.

Покрытие крыши – клик фальц

3. Окна и двери:

Заполнение оконны проемов приянто по ГОСТ.

ГОСТ 24700-99 для деревянных окон.

ГОСТ 30674-99 для пластиковых окон.

Заполнение дверных проемов принято по ГОСТ 6629-88.

Оконные и балконные блоки индивидуальные пластиковые со стеклопакетами и откидными створками.

Наружние двери металлические.

Внутренние двери деревянные филенчатые.

4. Технико-экономические показатели:

Этажность: 2 этажа

Наличие цоколя : Нет

Наличие мансарды : Нет

Габаритные размеры здания : 16,14х22,44 м.


Архитектурная высота здания от нулевой отметки: 9,79 м

Площадь здания : 488 м^2 *

Площадь застройки : 250 м^2 *

* – Площади расчитаны по СП 54.13330.2016 Приложение А

						Проект дома "Берта Ромарио"		АР
Изм.	Кол.уч.	Лист	№док.	Подп.	Дата			
Разраб.		Шолатов И.В.			23.07.2026	Жилой дом по индивидуальному проекту	Стадия / Лист / Листов	
ГИП		Баннов Е.А.			23.07.2026		П / 2 / 32	
						Общие данные	ООО"Строй Хауз" 111000, Москва, улица дом , офис 4,16,Тел: 14.99)645-44-30 Сайт www.s-h.ru STROYHOUSE	

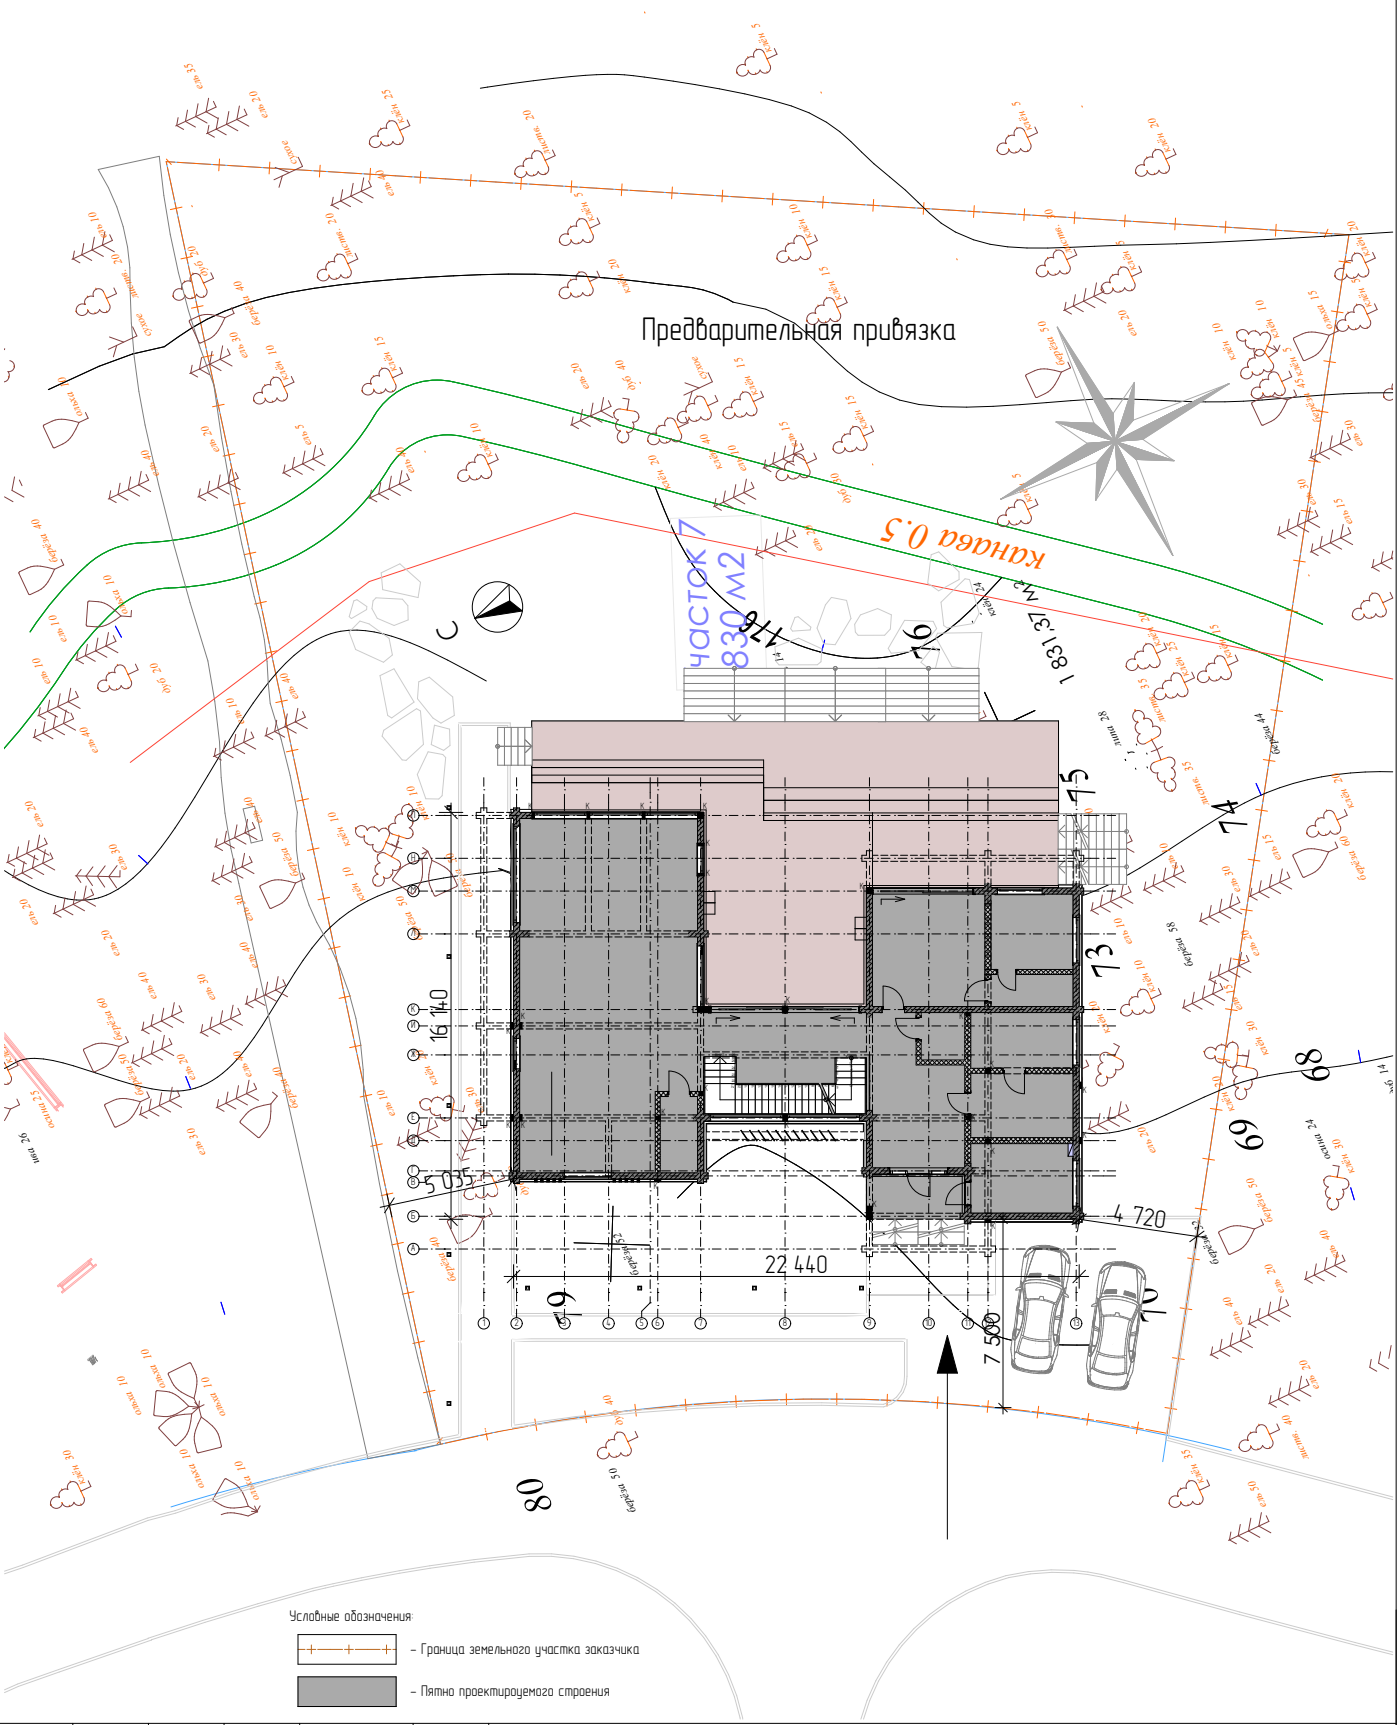

Условные обозначения:

– Граница земельного участка заказчика

– Пятно проектируемого строения

Изм.	Кол.уч.	Лист	№док.	Подп.	Дата	Проект дома "Берта Ромарио"		АР
Разраб.		Шолатов И.В.			23.07.2026			
ГИП		Баннов Е.А.			23.07.2026	Жилой дом по индивидуальному проекту	Стадия / Лист / Листов	
							П / 3 / 32	
						Схема размещения	ООО"Строй Хауз"	

111000, Москва, улица Доп., офис 4,16,Тел: 14.99)645-44-30
Сайт www.s-h.ru

STROYHOUSE

A4

Экспликация помещений 1-го этажа		
Номер	Наименование	Измеренная Площадь
1	Параданое крыльцо	7,02
2	Прихожая	18,53
3	Гардеробная	10,35
4	Постирочная	9,00
5	Котельная	11,21
6	С/У	3,25
7	Холл - лестница	26,97
8	Кухня столовая	50,77
9	Гостиная	43,06
10	Кладовая	4,48
11	Сауна	8,54
12	Зона отдыха	19,89
13	Душевые	4,14
		217,21 м²

Летняя кухня, настилы ,патио, пергола и прочие элементы МАФ отображены условно и разрабатываются отдельно , совместно с проектом обустройства участка

Проем под окно в парной выпиливается по месту

Проем под окно в парной выпиливается по месту

Канализационный короб

дымоход

дымоход

Печь электрич.

Стекла декор

Панели от солнца декор

1 850 декор

Условные обозначения:


Ширина 1 800 | Высота 800 | h от пола 1 600

- Вентиляционный короб
- Брусовые стены
- Каркасные стены
- К — Колонны
- Балки брусовые
- Балка клееная — Балки клееные
- 0,000 — Отметка пола


Примечание :
За отметку ±0,000, принять чистовую отметку первого этажа.
Размеры дверей и окон даны по коробке.
Все декоративные элементы, показаны условно.
Камин и дымоход показаны условно, размеры уточняются после выбора определенной позиции.

Пр-т	Проект дома "Берта Ромарио"		Дата	план 1 этажа	Лист
Разраб.	Шолотов И.В.		23.07.2026		4
ГИП	Баннов Е.А.		23.07.2026		

Экспликация помещений 2-го этажа		
Номер	Наименование	Измеренная Площадь
1	Лестничный холл	12,35
2	Холл	9,50
3	Мастер-спальня	25,69
4	Гардеробная	18,78
5	С/У	16,17
6	Кладовая	8,82
7	Спальня гостевая	22,12
8	С/У	9,00
9	Холл	13,00
10	Спальня детская	21,40
11	С/У	6,55
12	Спальня детская	21,40
13	С/У	6,25
14	Спальня детская	23,01
15	С/У	6,25
16	Постирочная	7,58
		227,87 м²

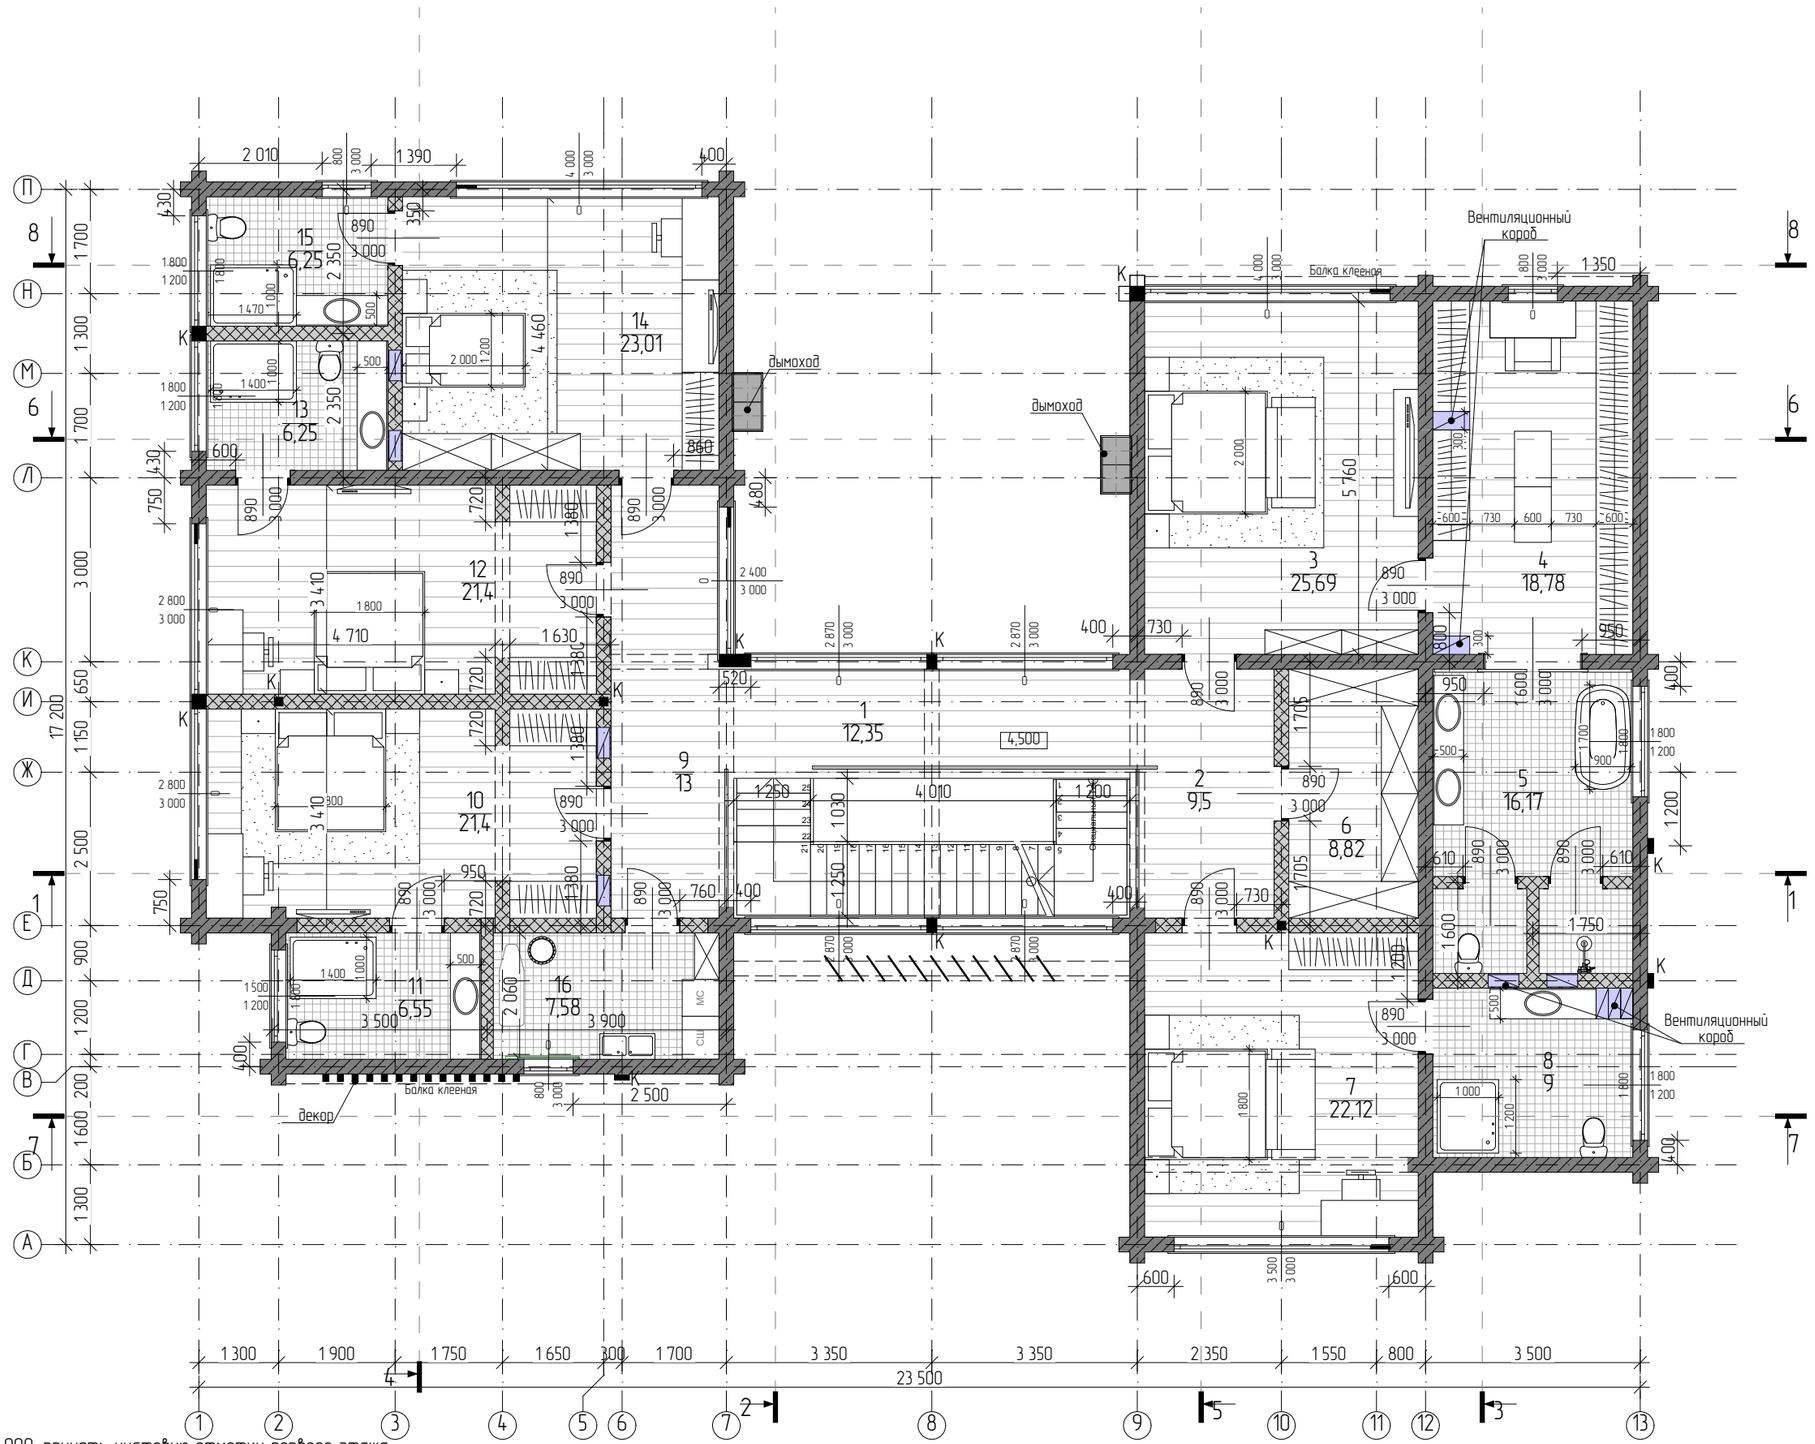


Условные обозначения:

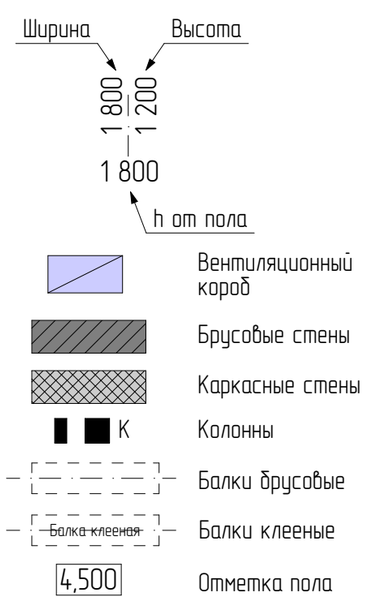


Примечание :
За отметку ±0,000, принять чистовую отметку первого этажа.
Размеры дверей и окон даны по коробке.
Все декоративные элементы, показаны условно.
Камин и дымоход показаны условно, размеры уточняются после выбора определенной позиции.

Пр-т	Проект дома "Берта Ромарио"		Дата	План 2 этажа
Разраб.	Шолотов И.В.		23.07.2026	Лист 5
ГИП	Баннов Е.А.		23.07.2026	

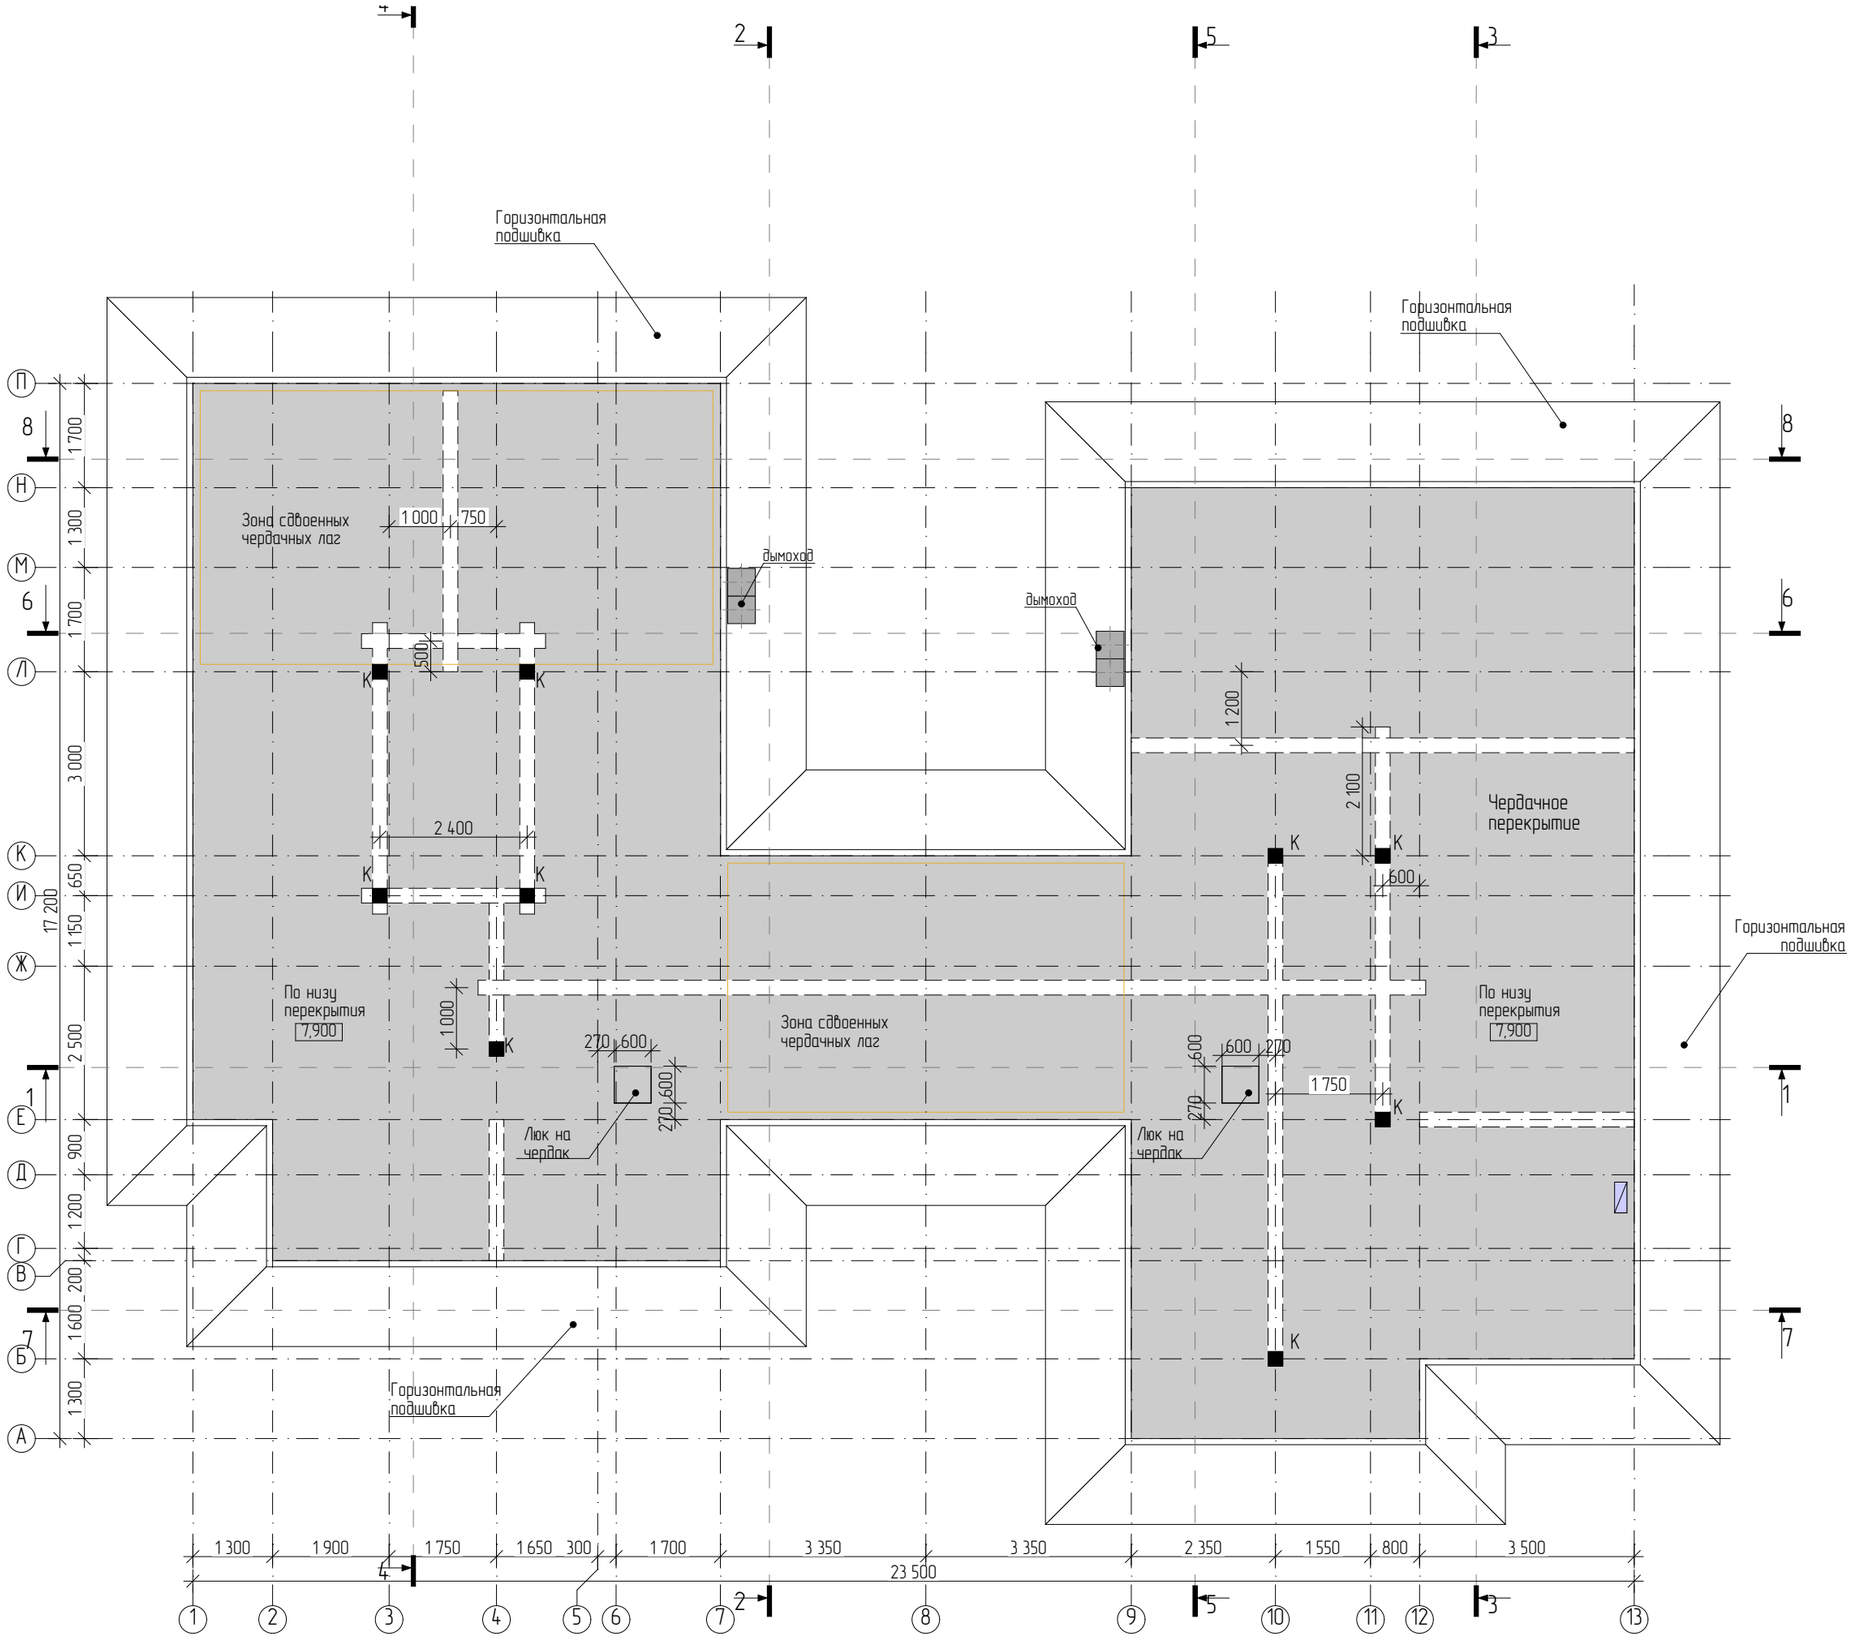

Пр-т	Проект дома "Берта Ромарио"		Дата	План чердака	Лист
Разраб.	Шолотов И.В.		23.07.2026		6
ГИП	Баннов Е.А.		23.07.2026		

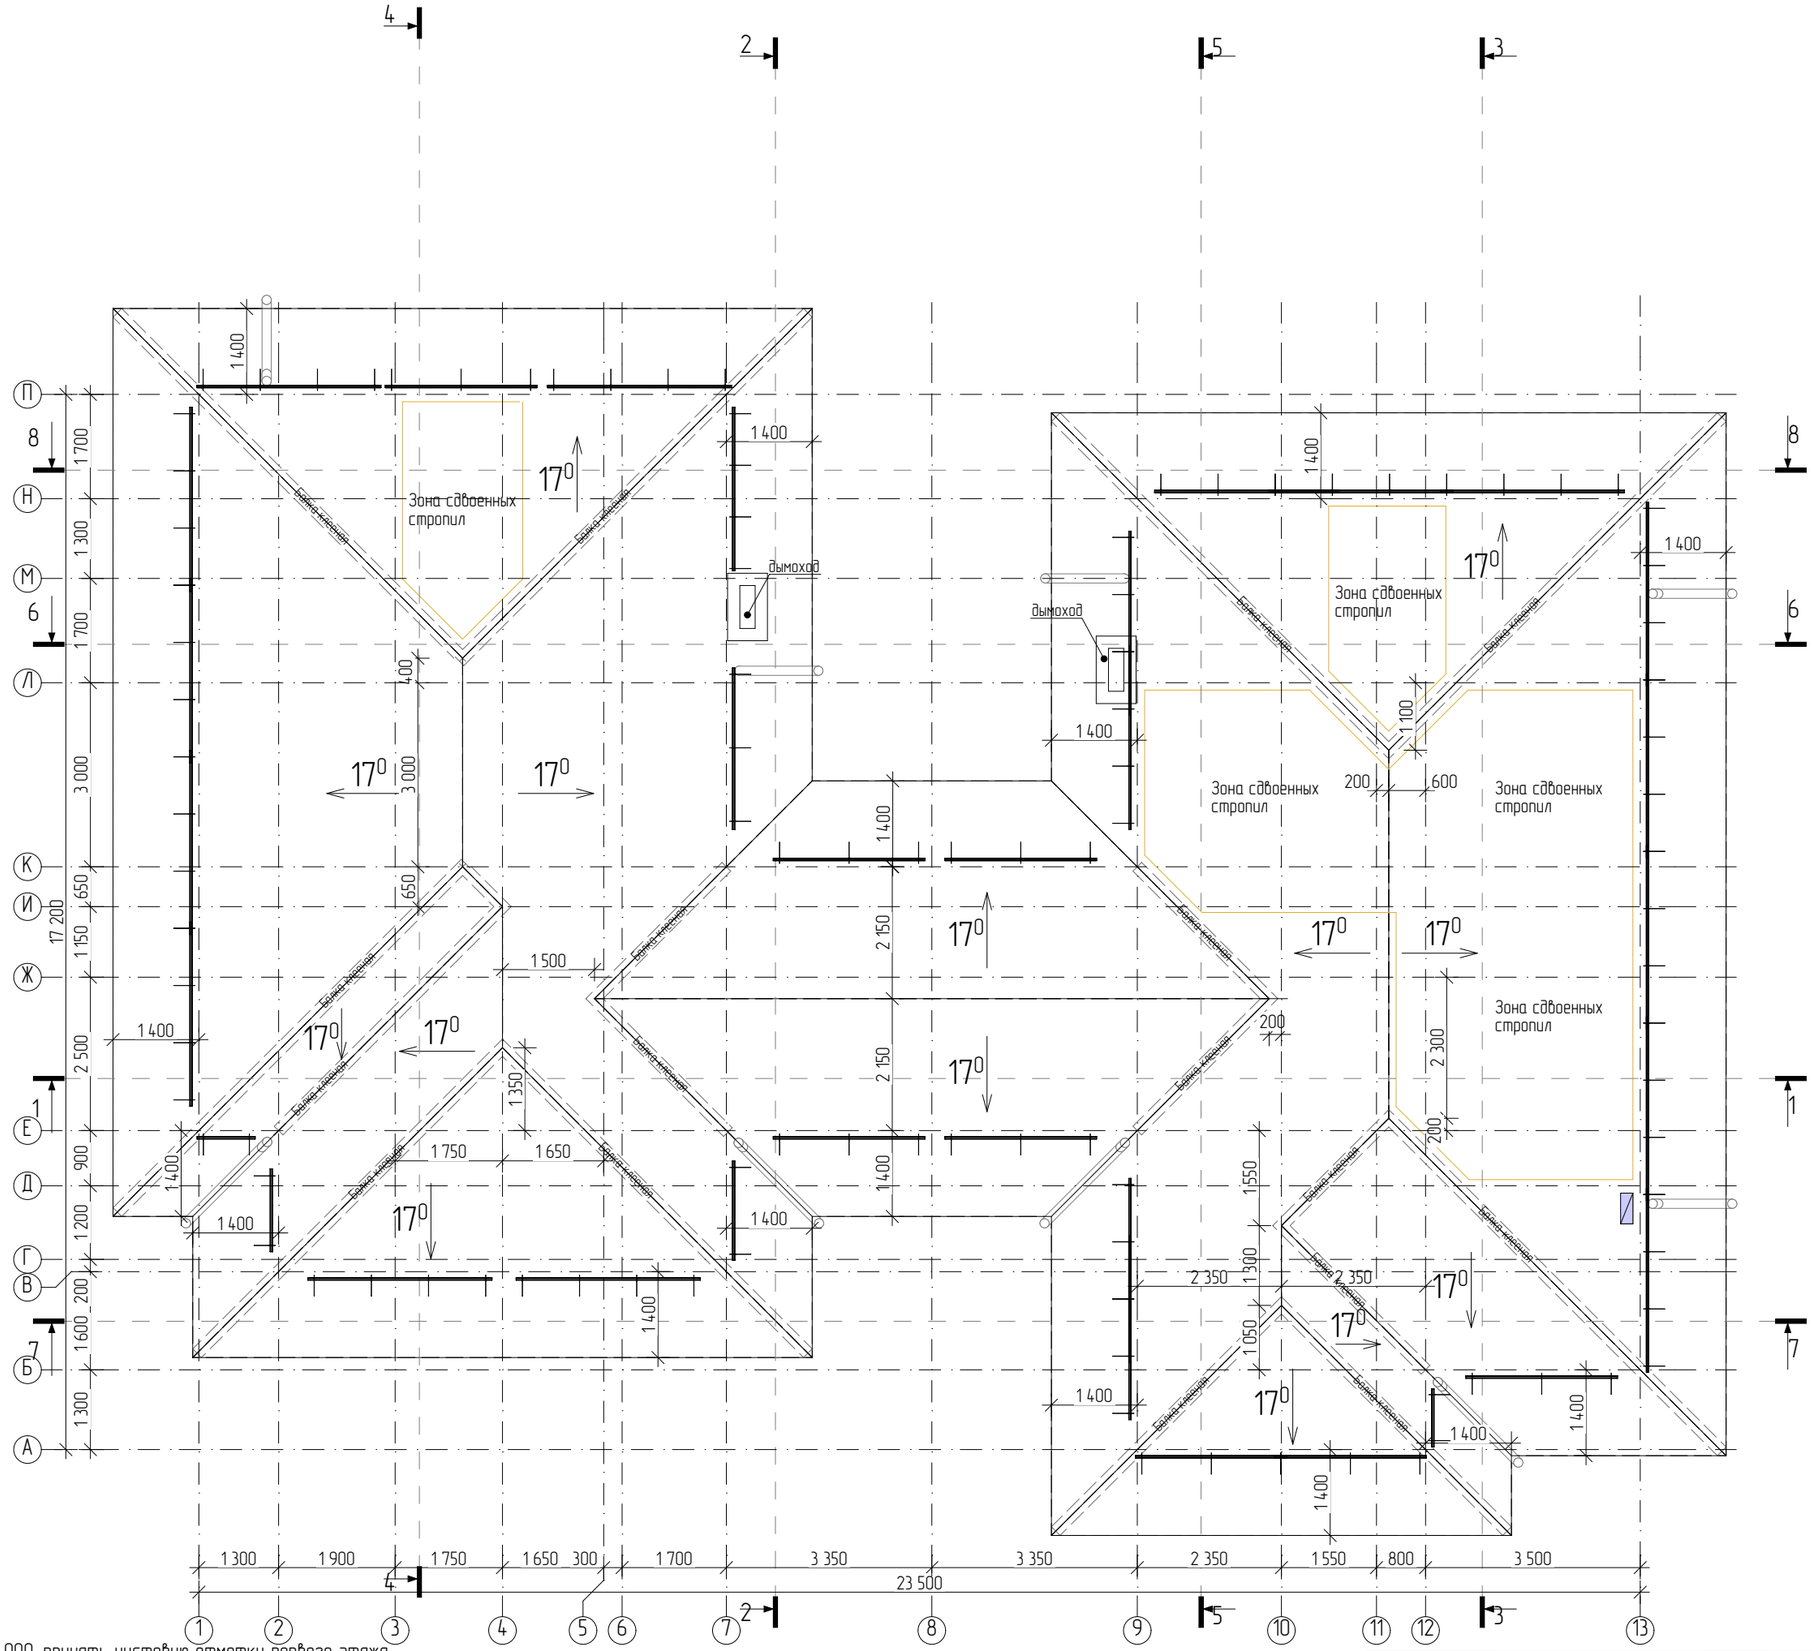


Условные обозначения:

- Вентиляционный короб
- Балка клееная — Балки клееные
- Зона сдвоенных стропил
- 17^0 — Направление уклона кровли

Примечание :
За отметку ±0,000, принять чистовую отметку первого этажа.
Размеры дверей и окон даны по коробке.
Все декоративные элементы, показаны условно.
Камин и дымоход показаны условно, размеры уточняются после выбора определенной позиции.

Пр-т	Проект дома "Берта Ромария"		Дата	План кровли	Лист
Разраб.	Шолотов И.В.		23.07.2026		7
ГИП	Банков Е.А.		23.07.2026		

Разрез 1–1

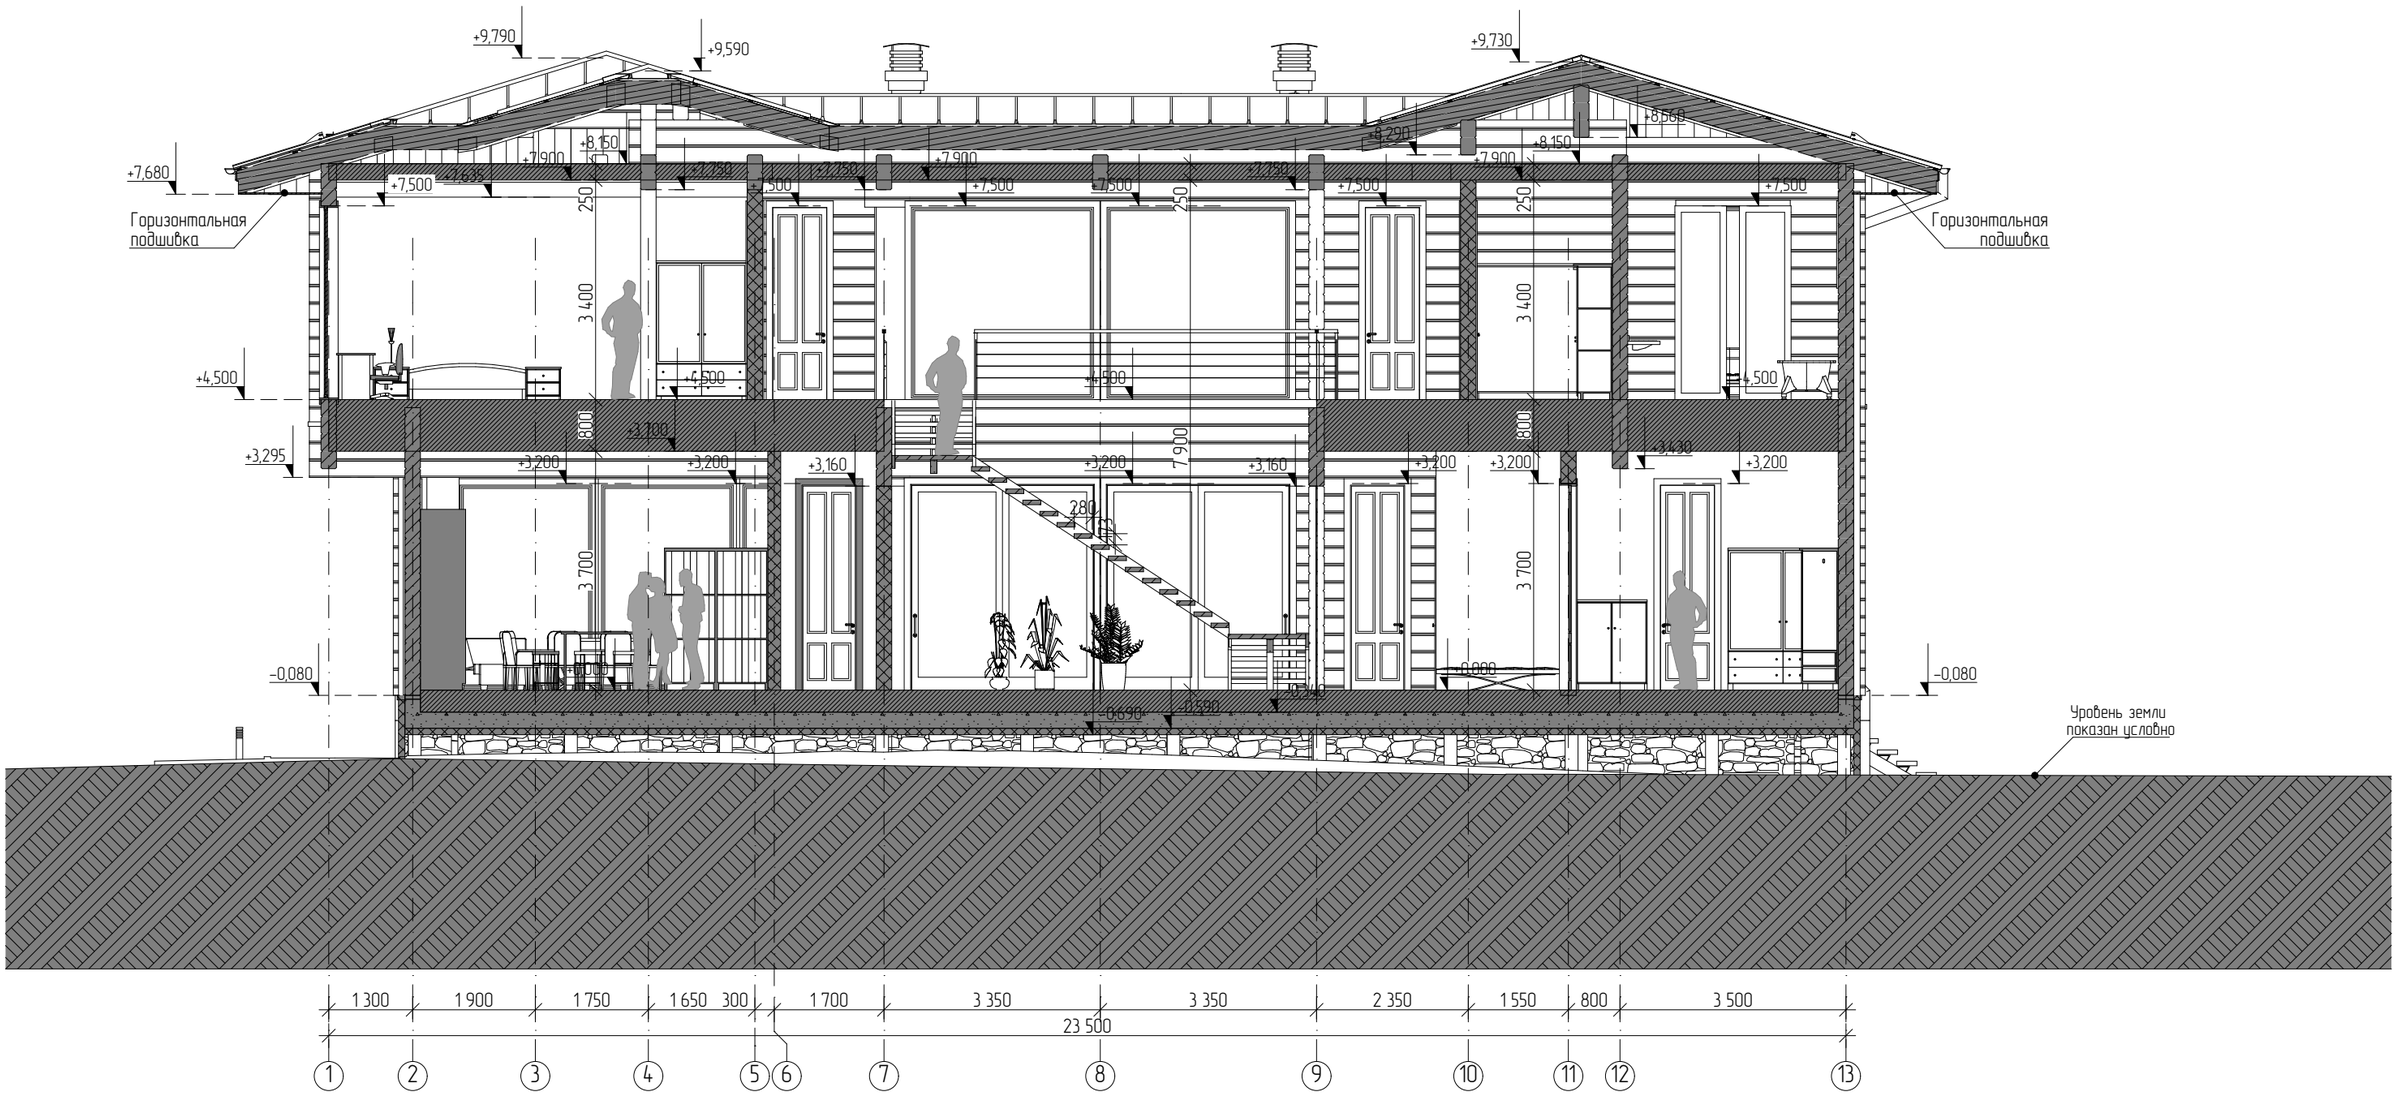


Условные обозначения

±0,000 Высотные отметки

Примечание :
За отметку ±0,000, принять чистовую отметку первого этажа.
Размеры дверей и окон даны по коробке.
Все декоративные элементы, показаны условно.
См. совместно с листами 3,4,5,6

Пр–т	Проект дома "Берта Ромарио"		Дата	Разрез 1–1	Лист
Разраб.	Шолотов И.В.		23.07.2026		8
ГИП	Баннов Е.А.		23.07.2026		

Разрез 2-2

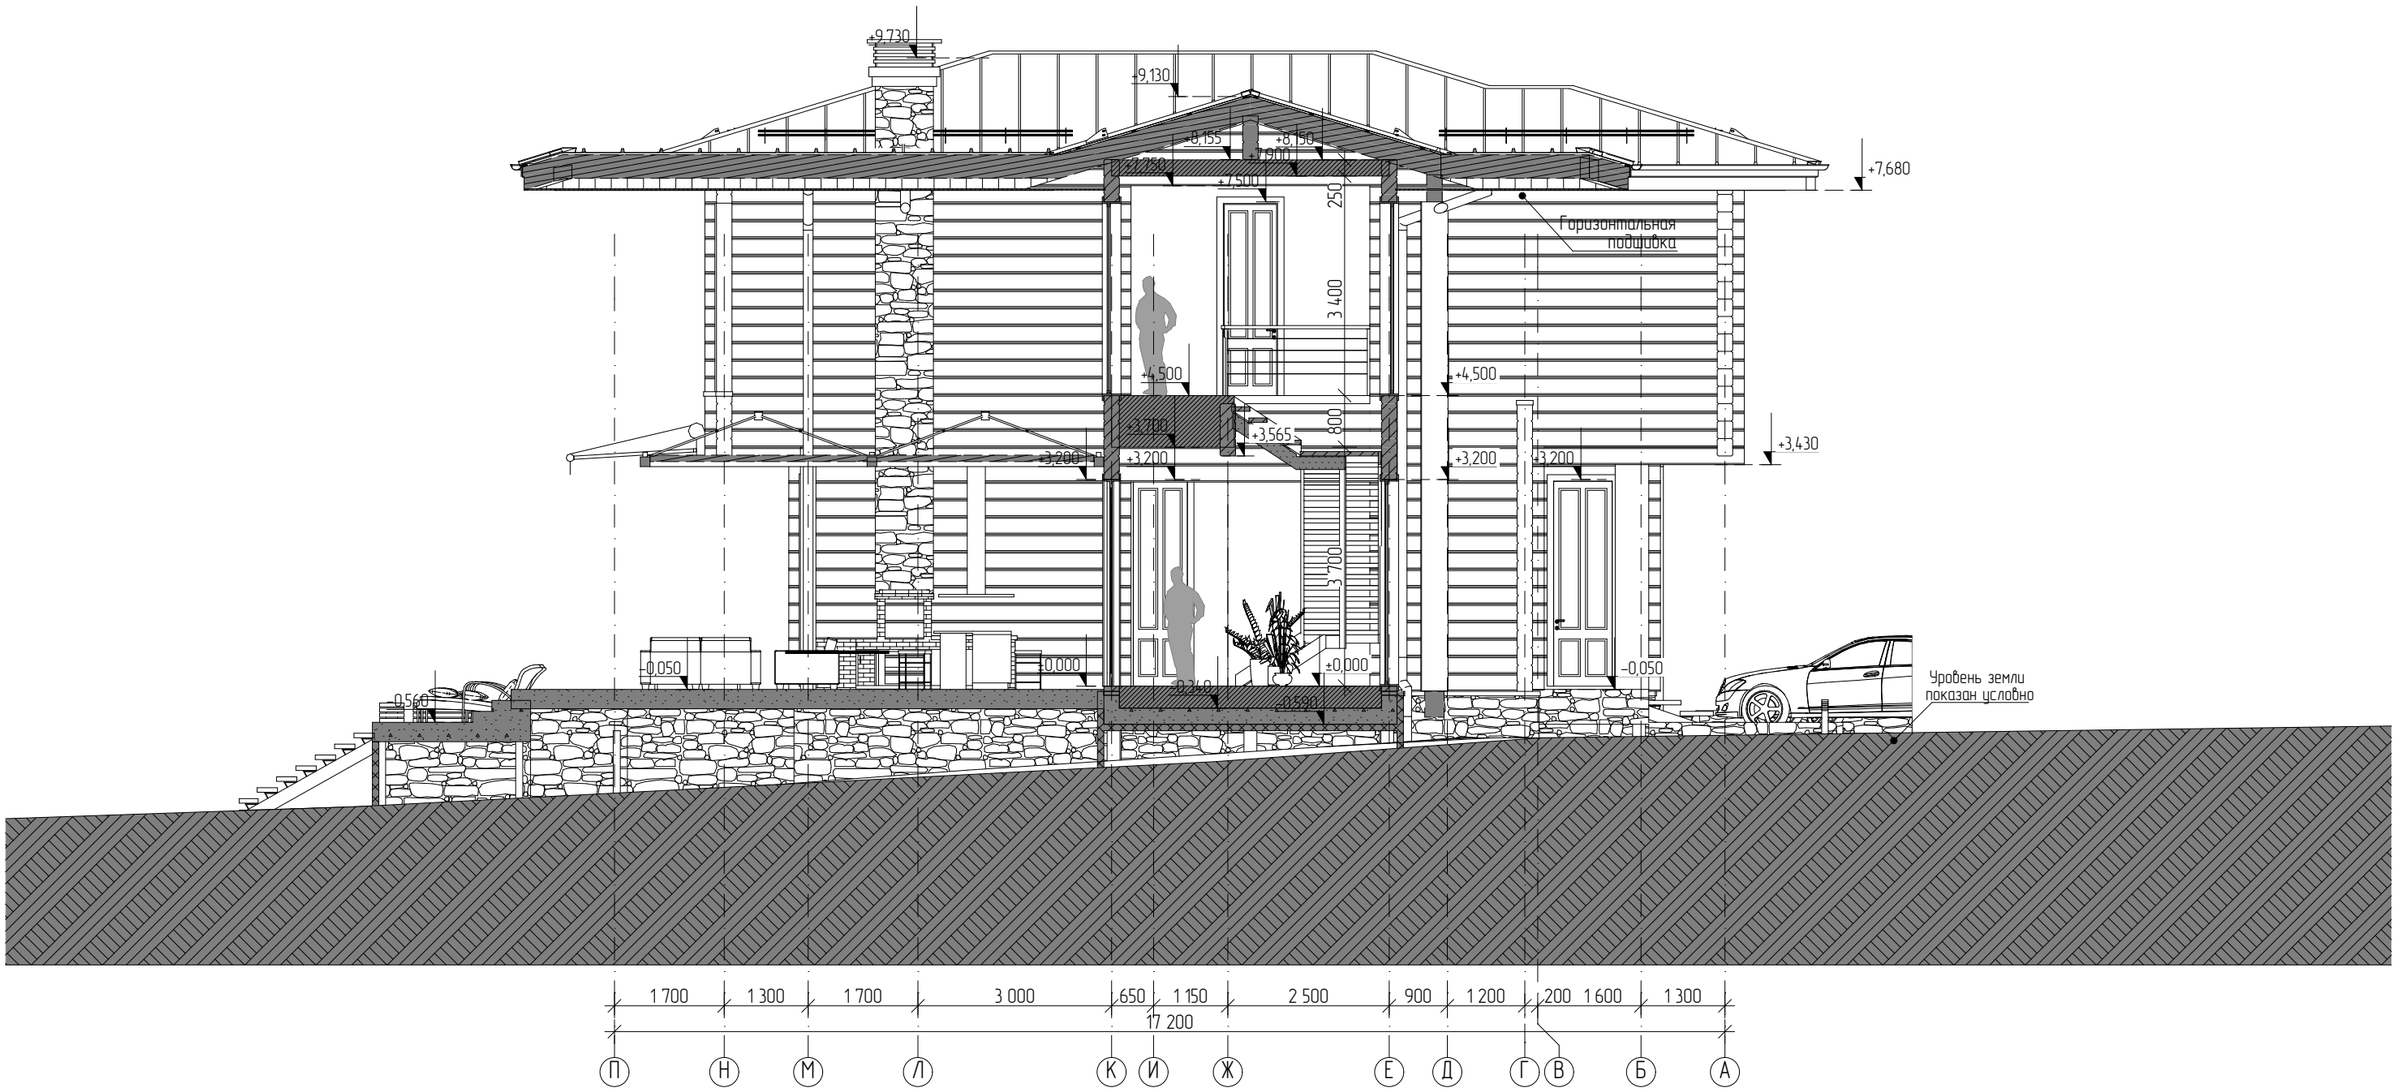


Условные обозначения

±0,000 Высотные отметки

Примечание :
За отметку ±0,000, принять чистовую отметку первого этажа.
Размеры дверей и окон даны по коробке.
Все декоративные элементы, показаны условно.
См. совместно с листами 3,4,5,6

Пр-т	Проект дома "Берта Ромарио"		Дата	Разрез 2-2	Лист
Разраб.	Шолотов И.В.		23.07.2026		9
ГИП	Баннов Е.А.		23.07.2026		

Разрез 3-3

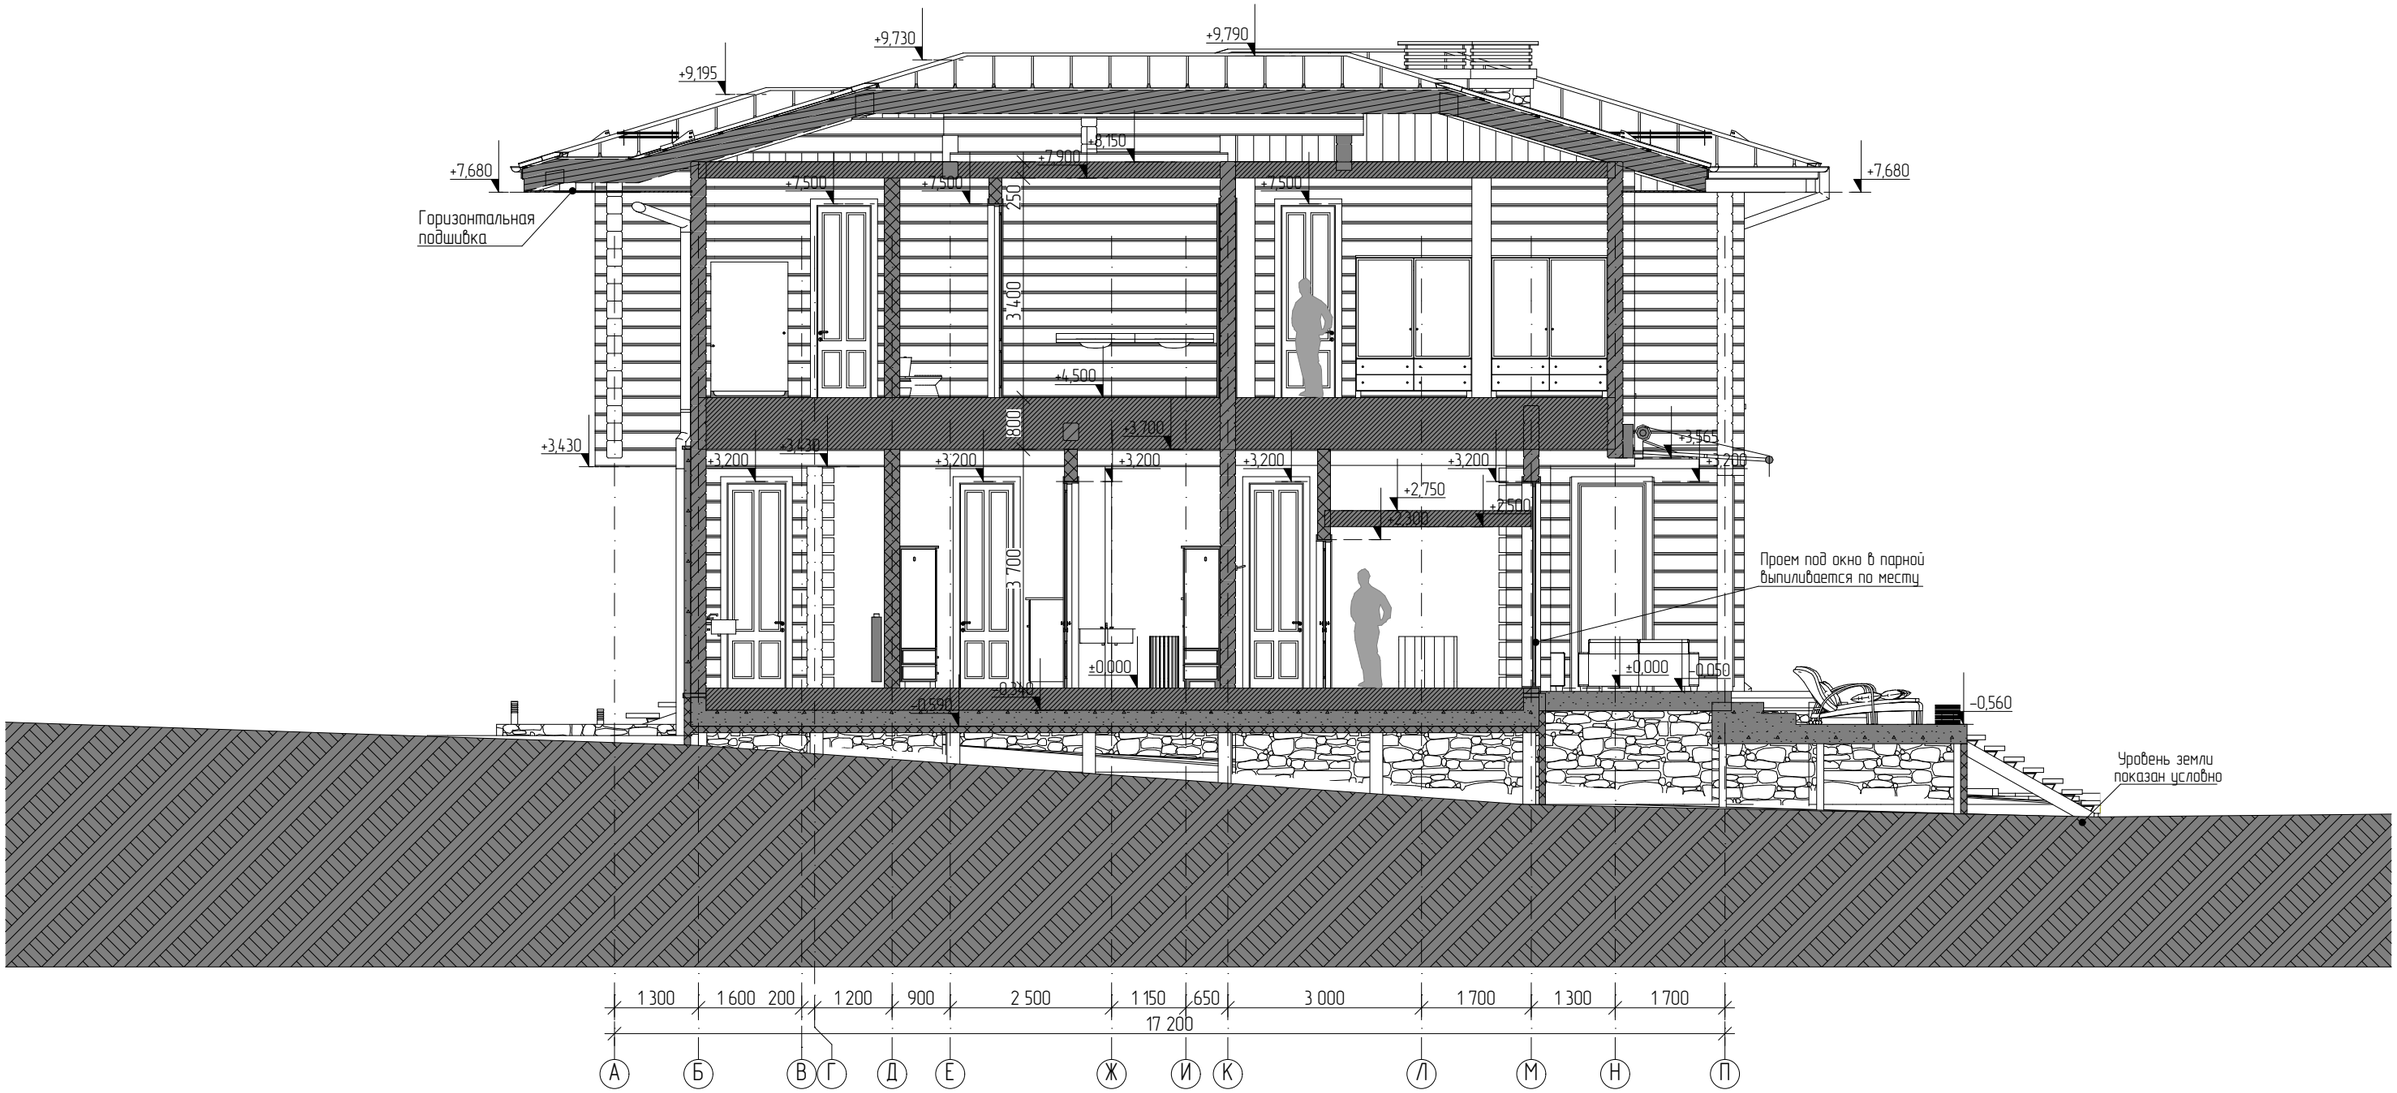


Условные обозначения

±0,000 Высотные отметки

Примечание :
За отметку ±0,000, принять чистовую отметку первого этажа.
Размеры дверей и окон даны по коробке.
Все декоративные элементы, показаны условно.
См. совместно с листами 3,4,5,6

Пр-т	Проект дома "Берта Ромарио"		Дата	Разрез 3-3	Лист
Разраб.	Шолотов И.В.		23.07.2026		10
ГИП	Банков Е.А.		23.07.2026		

Разрез 4-4

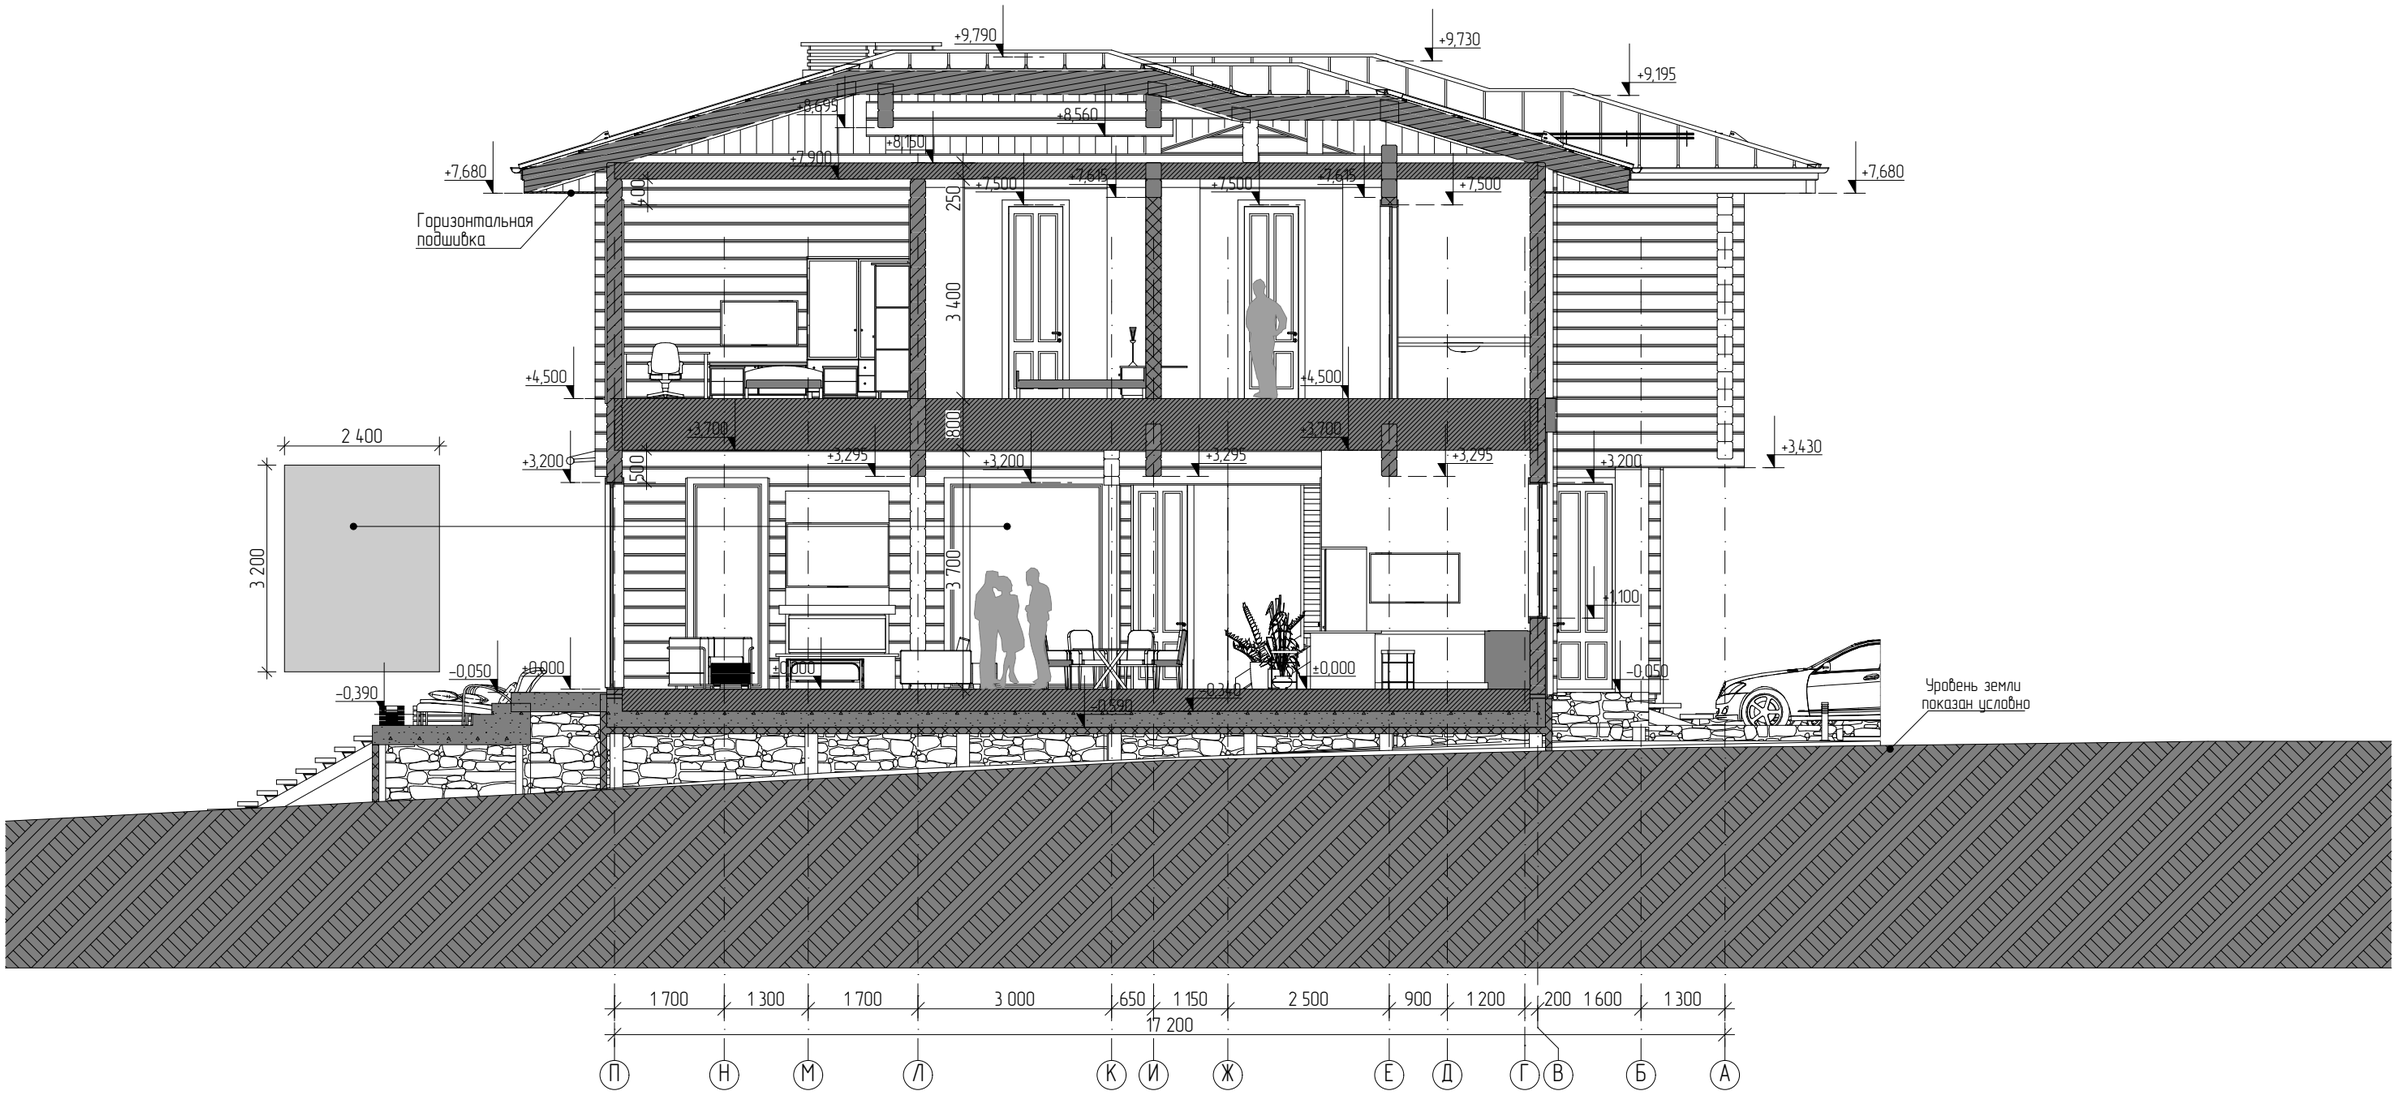

Условные обозначения

±0,000 Высотные отметки

Примечание :
За отметку ±0,000, принять чистовую отметку первого этажа.
Размеры дверей и окон даны по коробке.
Все декоративные элементы, показаны условно.
См. совместно с листами 3,4,5,6

Пр-т	Проект дома "Берта Ромарио"		Дата	Разрез 4-4	Лист
Разраб.	Шолотов И.В.		23.07.2026		11
ГИП	Баннов Е.А.		23.07.2026		

Разрез 5-5



Условные обозначения

±0,000 Высотные отметки

Примечание :
За отметку ±0,000, принять чистовую отметку первого этажа.
Размеры дверей и окон даны по коробке.
Все декоративные элементы, показаны условно.
См. совместно с листами 3,4,5,6

Пр-т	Проект дома "Берта Ромарио"		Дата	Разрез 5-5	Лист
Разраб.	Шолотов И.В.		23.07.2026		12
ГИП	Баннов Е.А.		23.07.2026		

Разрез 6-6




Условные обозначения

±0,000 Высотные отметки

Примечание :
За отметку ±0,000, принять чистовую отметку первого этажа.
Размеры дверей и окон даны по коробке.
Все декоративные элементы, показаны условно.
См. совместно с листами 3,4,5,6

Пр-т	Проект дома "Берта Ромария"		Дата	Разрез 6-6	Лист
Разраб.	Шолотов И.В.		23.07.2026		13
ГИП	Банков Е.А.		23.07.2026		

Разрез 7-7

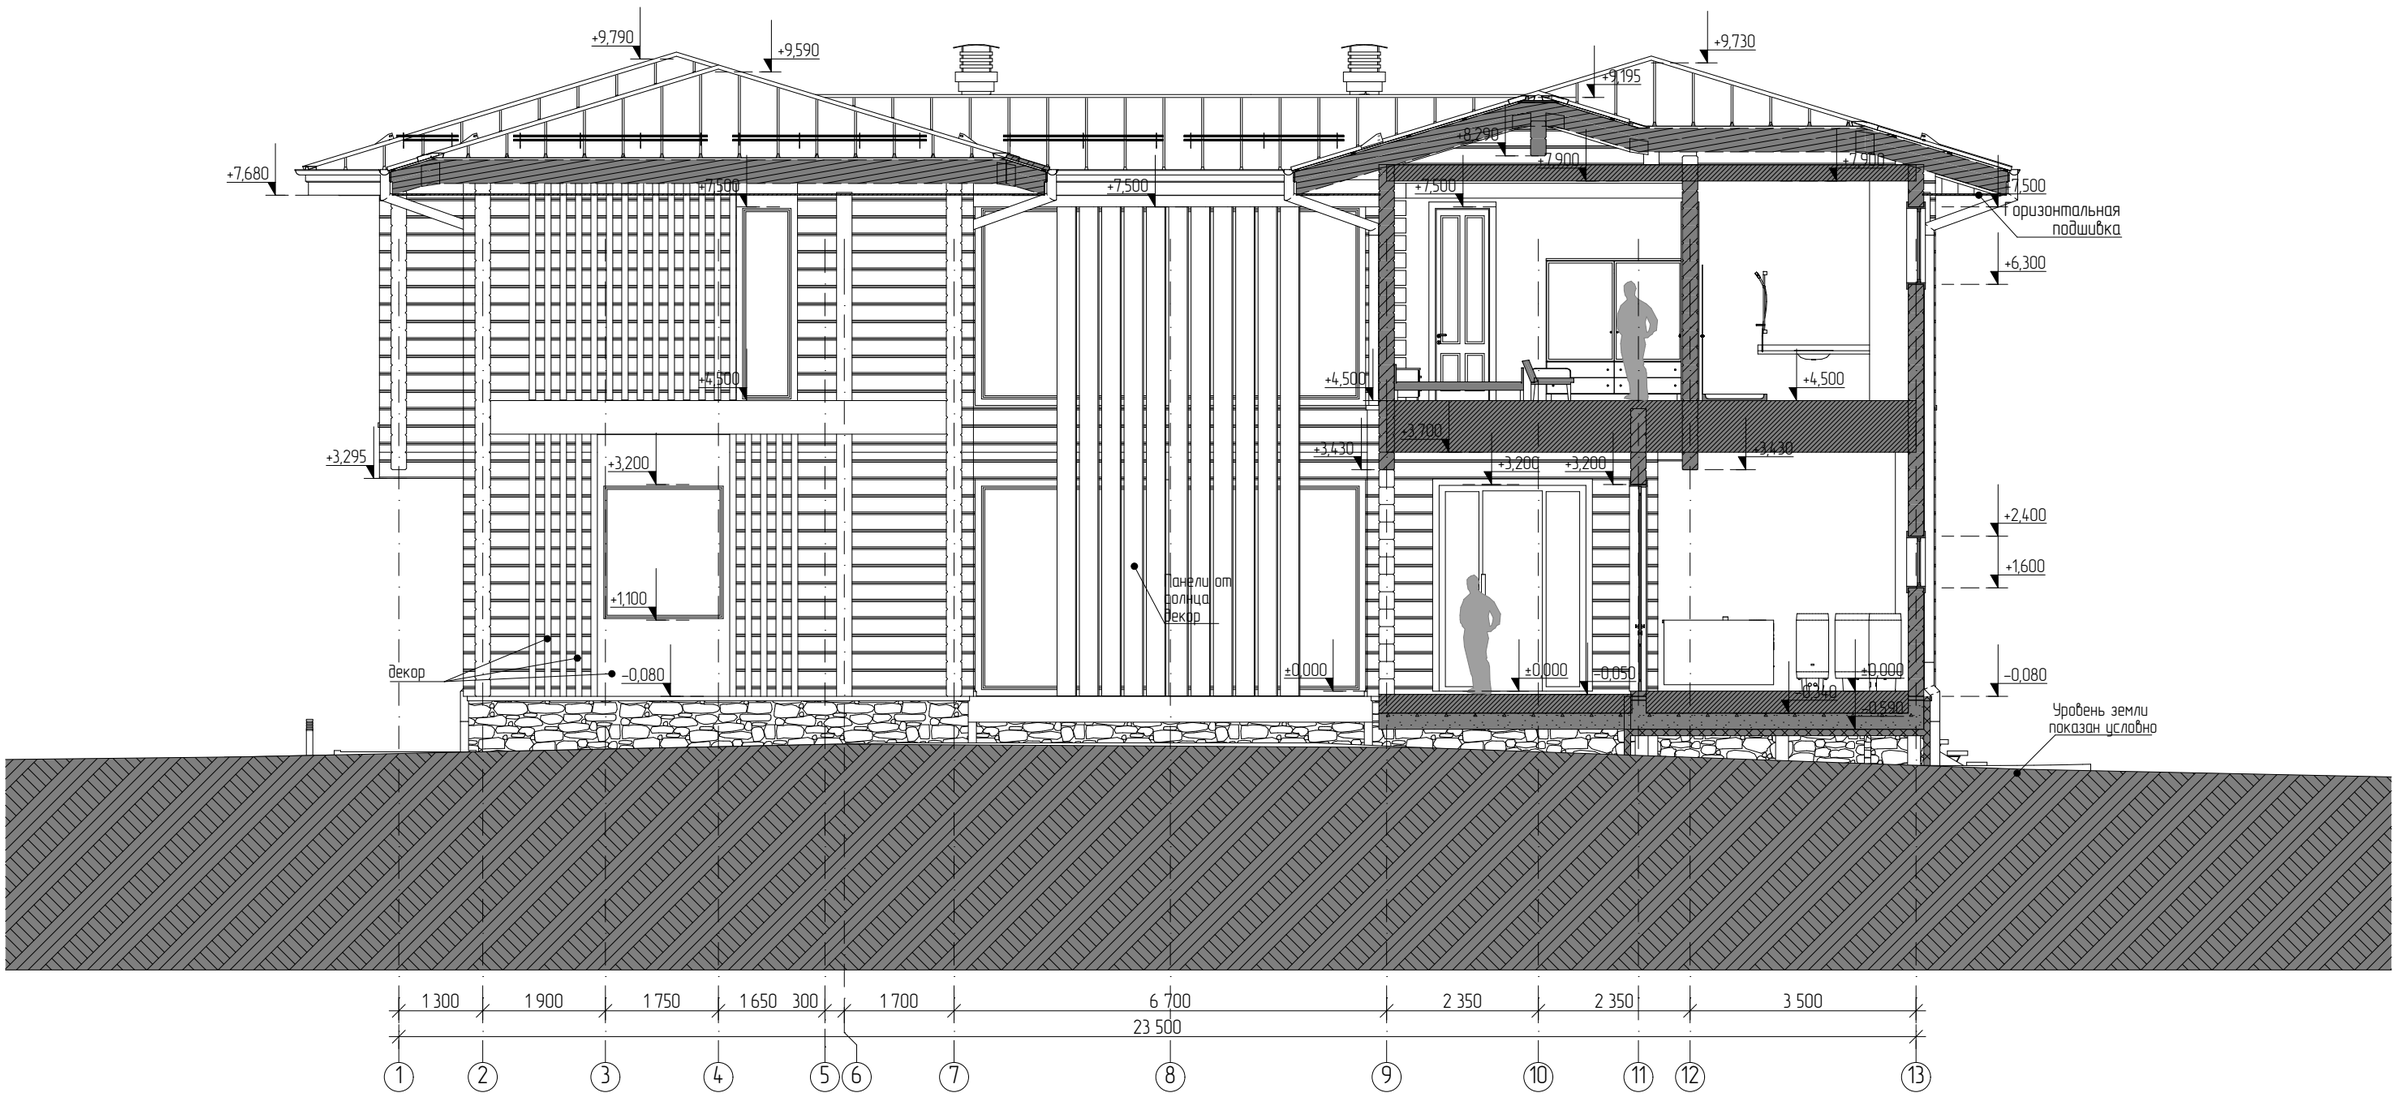

Условные обозначения

±0,000 Высотные отметки

Примечание :
За отметку ±0,000, принять чистовую отметку первого этажа.
Размеры дверей и окон даны по коробке.
Все декоративные элементы, показаны условно.
См. совместно с листами 3,4,5,6

Пр-т	Проект дома "Берта Ромария"		Дата	Разрез 7-7	Лист
Разраб.	Шолотов И.В.		23.07.2026		14
ГИП	Баннов Е.А.		23.07.2026		

Разрез 8-8




Условные обозначения

±0,000 Высотные отметки

Примечание :
За отметку ±0,000, принять чистовую отметку первого этажа.
Размеры дверей и окон даны по коробке.
Все декоративные элементы, показаны условно.
См. совместно с листами 3,4,5,6

Пр-т	Проект дома "Берта Ромария"		Дата	Разрез 8-8	Лист
Разраб.	Шолотов И.В.		23.07.2026		15
ГИП	Банков Е.А.		23.07.2026		

Фасад 1–13

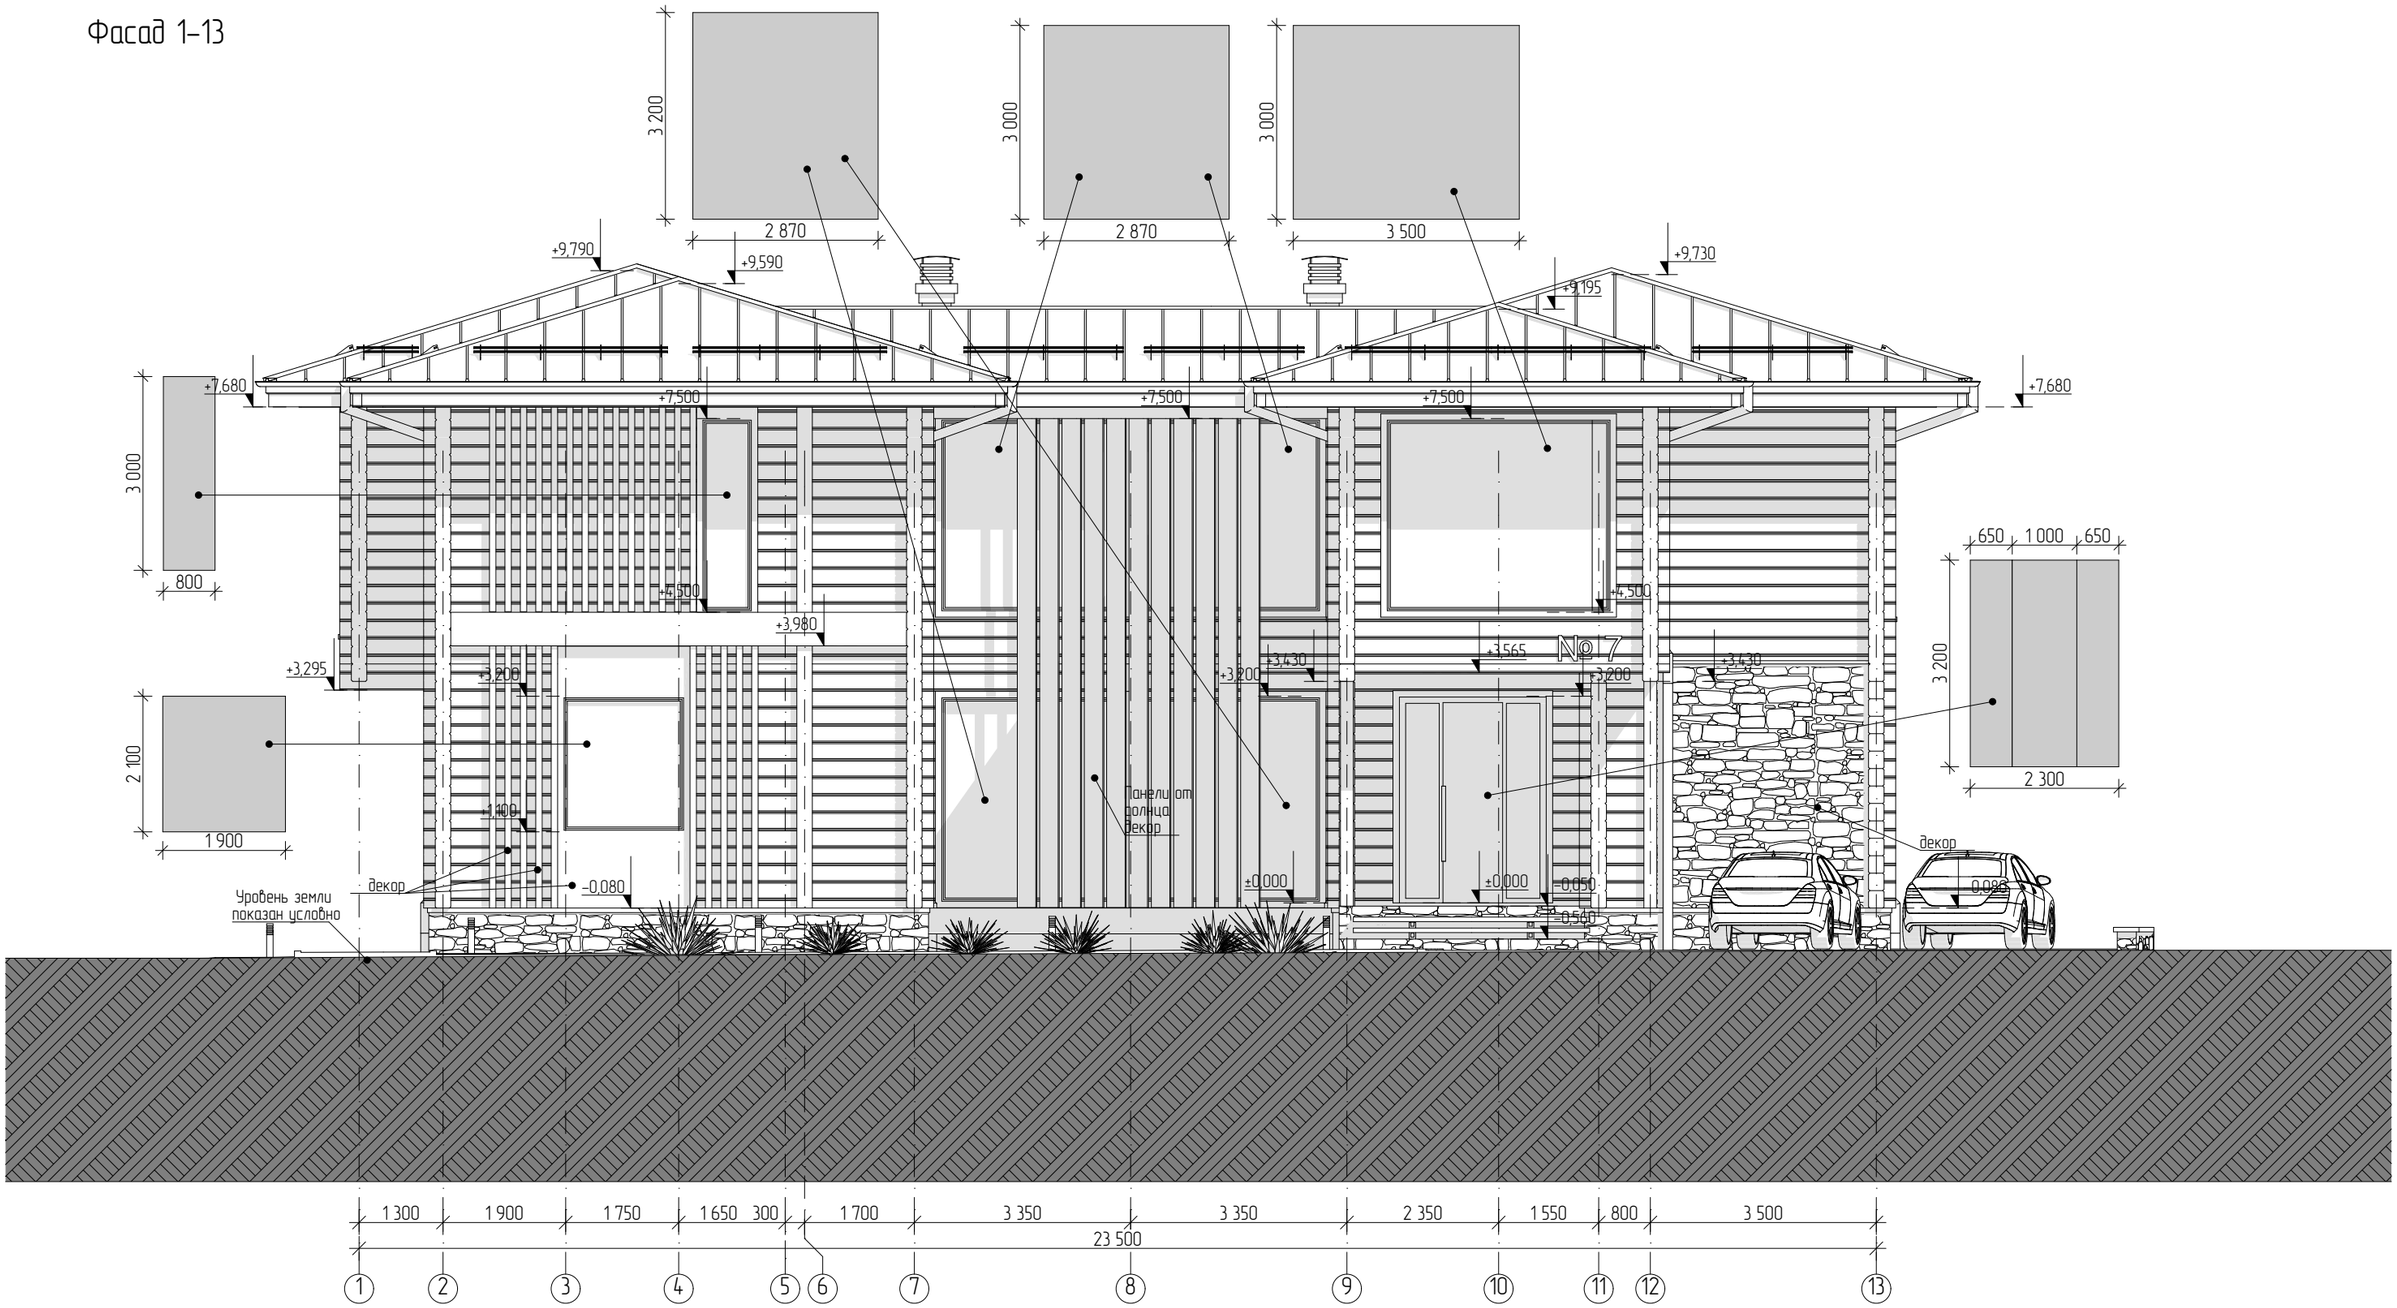


Условные обозначения

±0,000 Высотные отметки

Примечание :
За отметку ±0,000, принять чистовую отметку первого этажа.
Размеры дверей и окон даны по коробке.
Все декоративные элементы, показаны условно.
См. совместно с листами 3,4,5,6

Пр–т	Проект дома "Берта Ромарио"		Дата	Фасад 1–13	Лист
Разраб.	Шолотов И.В.		23.07.2026		16
ГИП	Банков Е.А.		23.07.2026		

Фасад 13-1

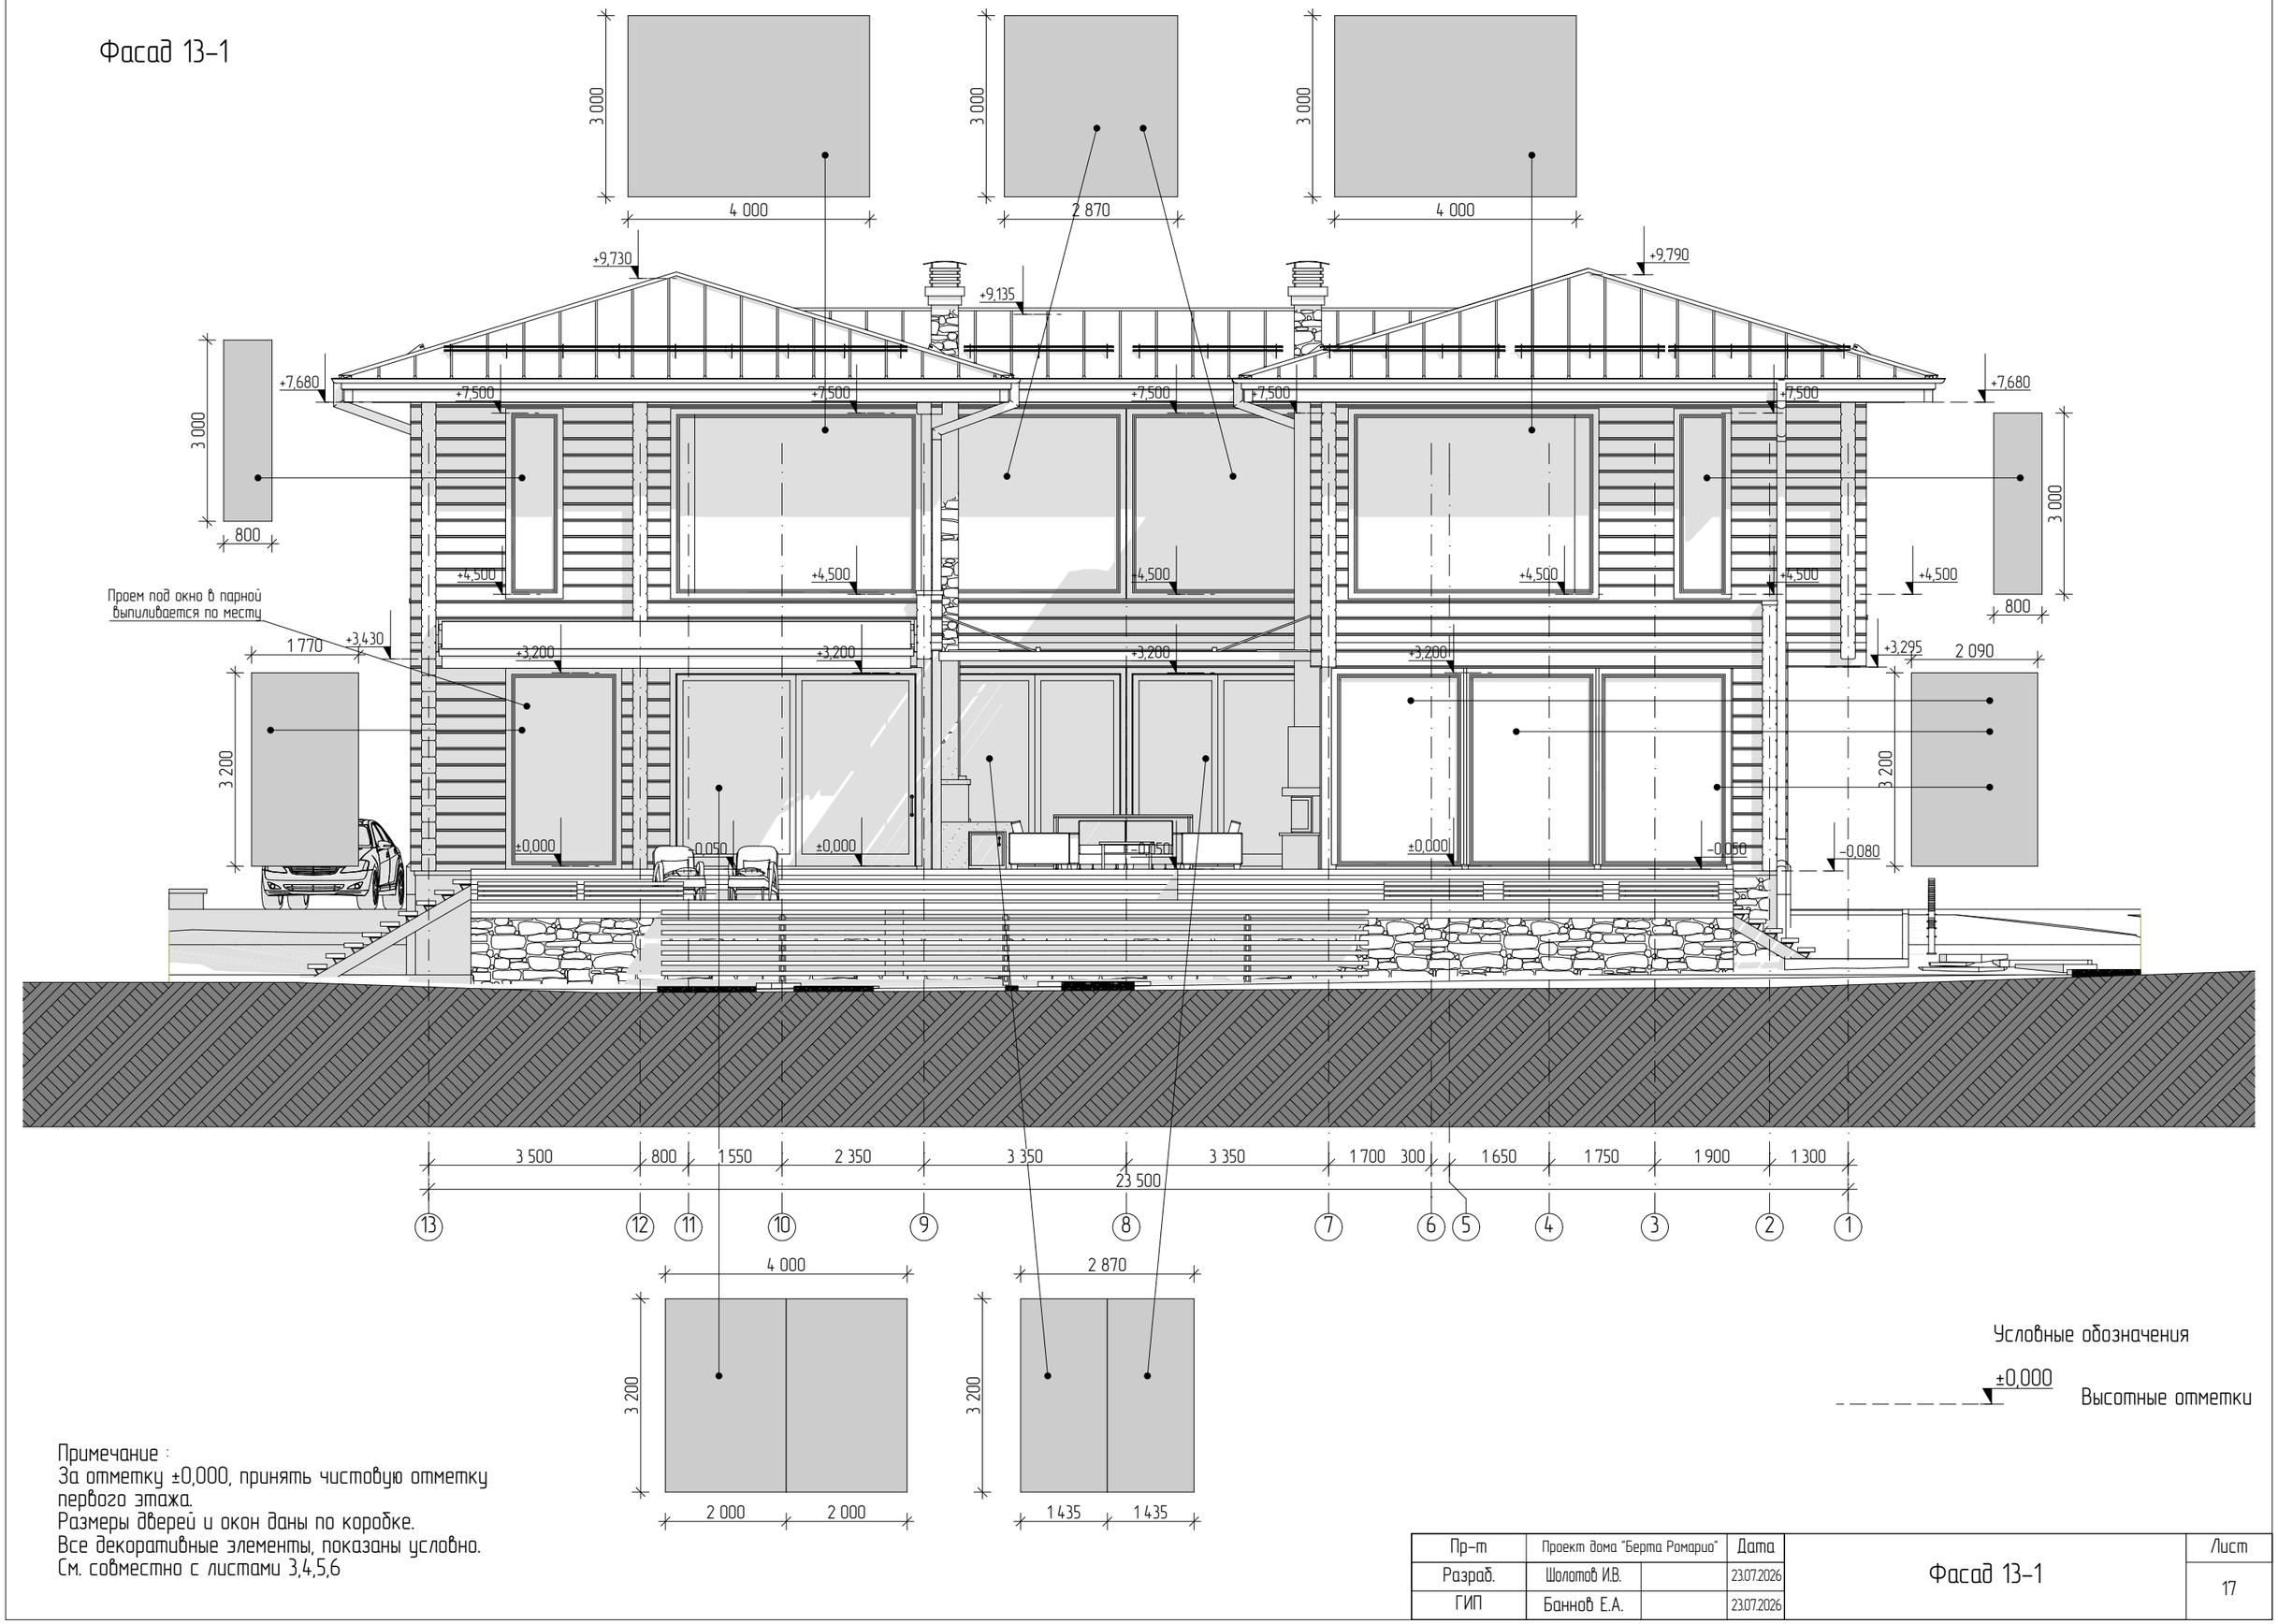


Условные обозначения

±0,000 — Высотные отметки

Примечание :
За отметку ±0,000, принять чистовую отметку первого этажа.
Размеры дверей и окон даны по коробке.
Все декоративные элементы, показаны условно.
См. совместно с листами 3,4,5,6

Пр-т	Проект дома "Берта Ромарио"		Дата	Фасад 13-1	Лист
Разраб.	Шолотов И.В.		23.07.2026		17
ГИП	Баннов Е.А.		23.07.2026		

Фасад А-П

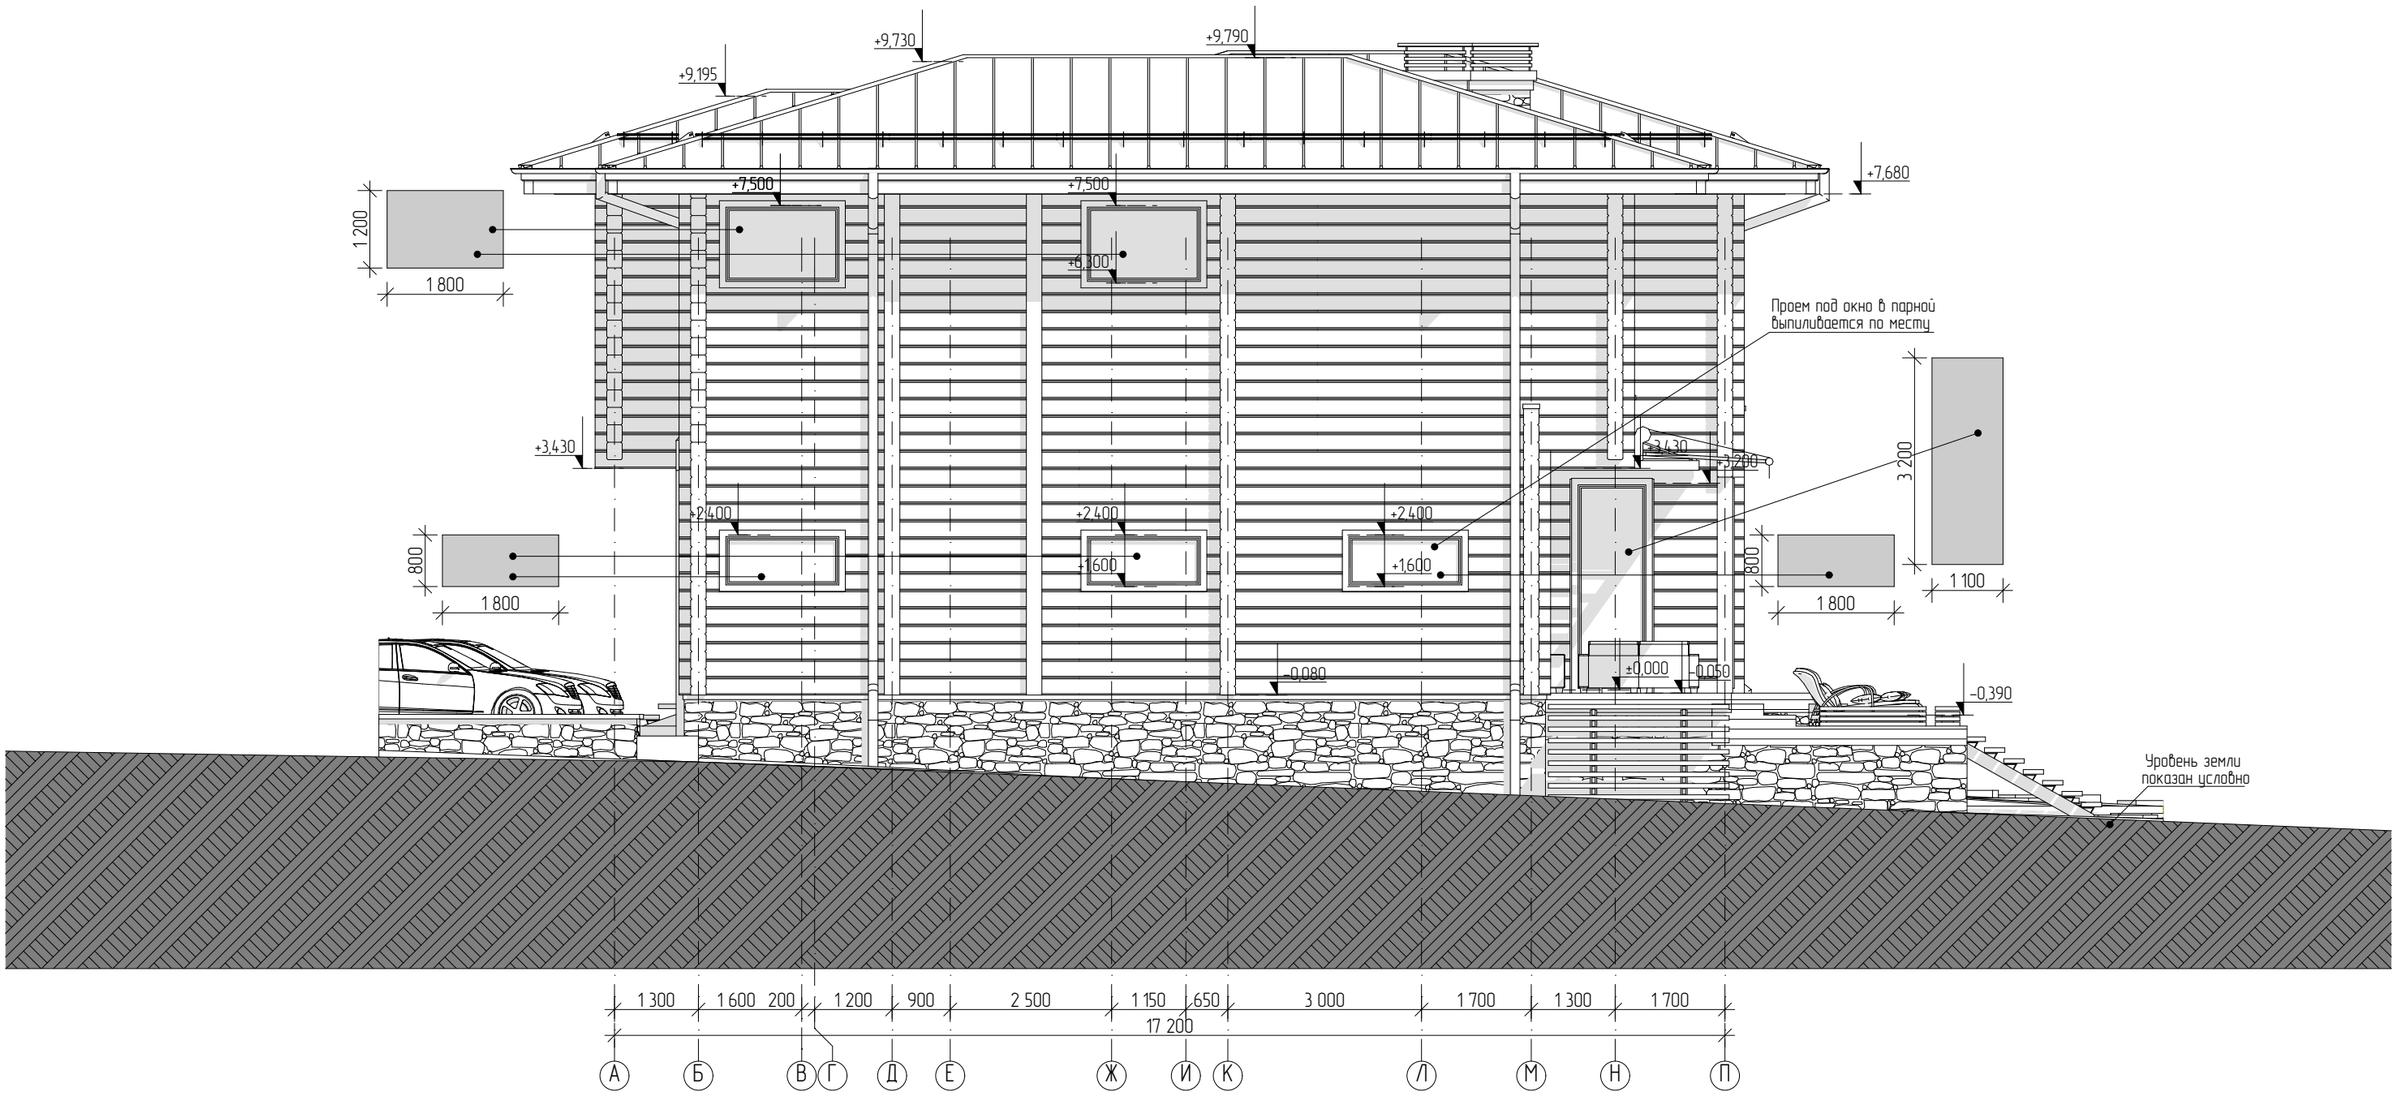


Условные обозначения

±0,000 Высотные отметки

Примечание :
За отметку ±0,000, принять чистовую отметку первого этажа.
Размеры дверей и окон даны по коробке.
Все декоративные элементы, показаны условно.
См. совместно с листами 3,4,5,6

Пр-т	Проект дома "Берта Ромарио"		Дата	Фасад А-П	Лист
Разраб.	Шолотов И.В.		23.07.2026		18
ГИП	Банков Е.А.		23.07.2026		

Фасад П–А

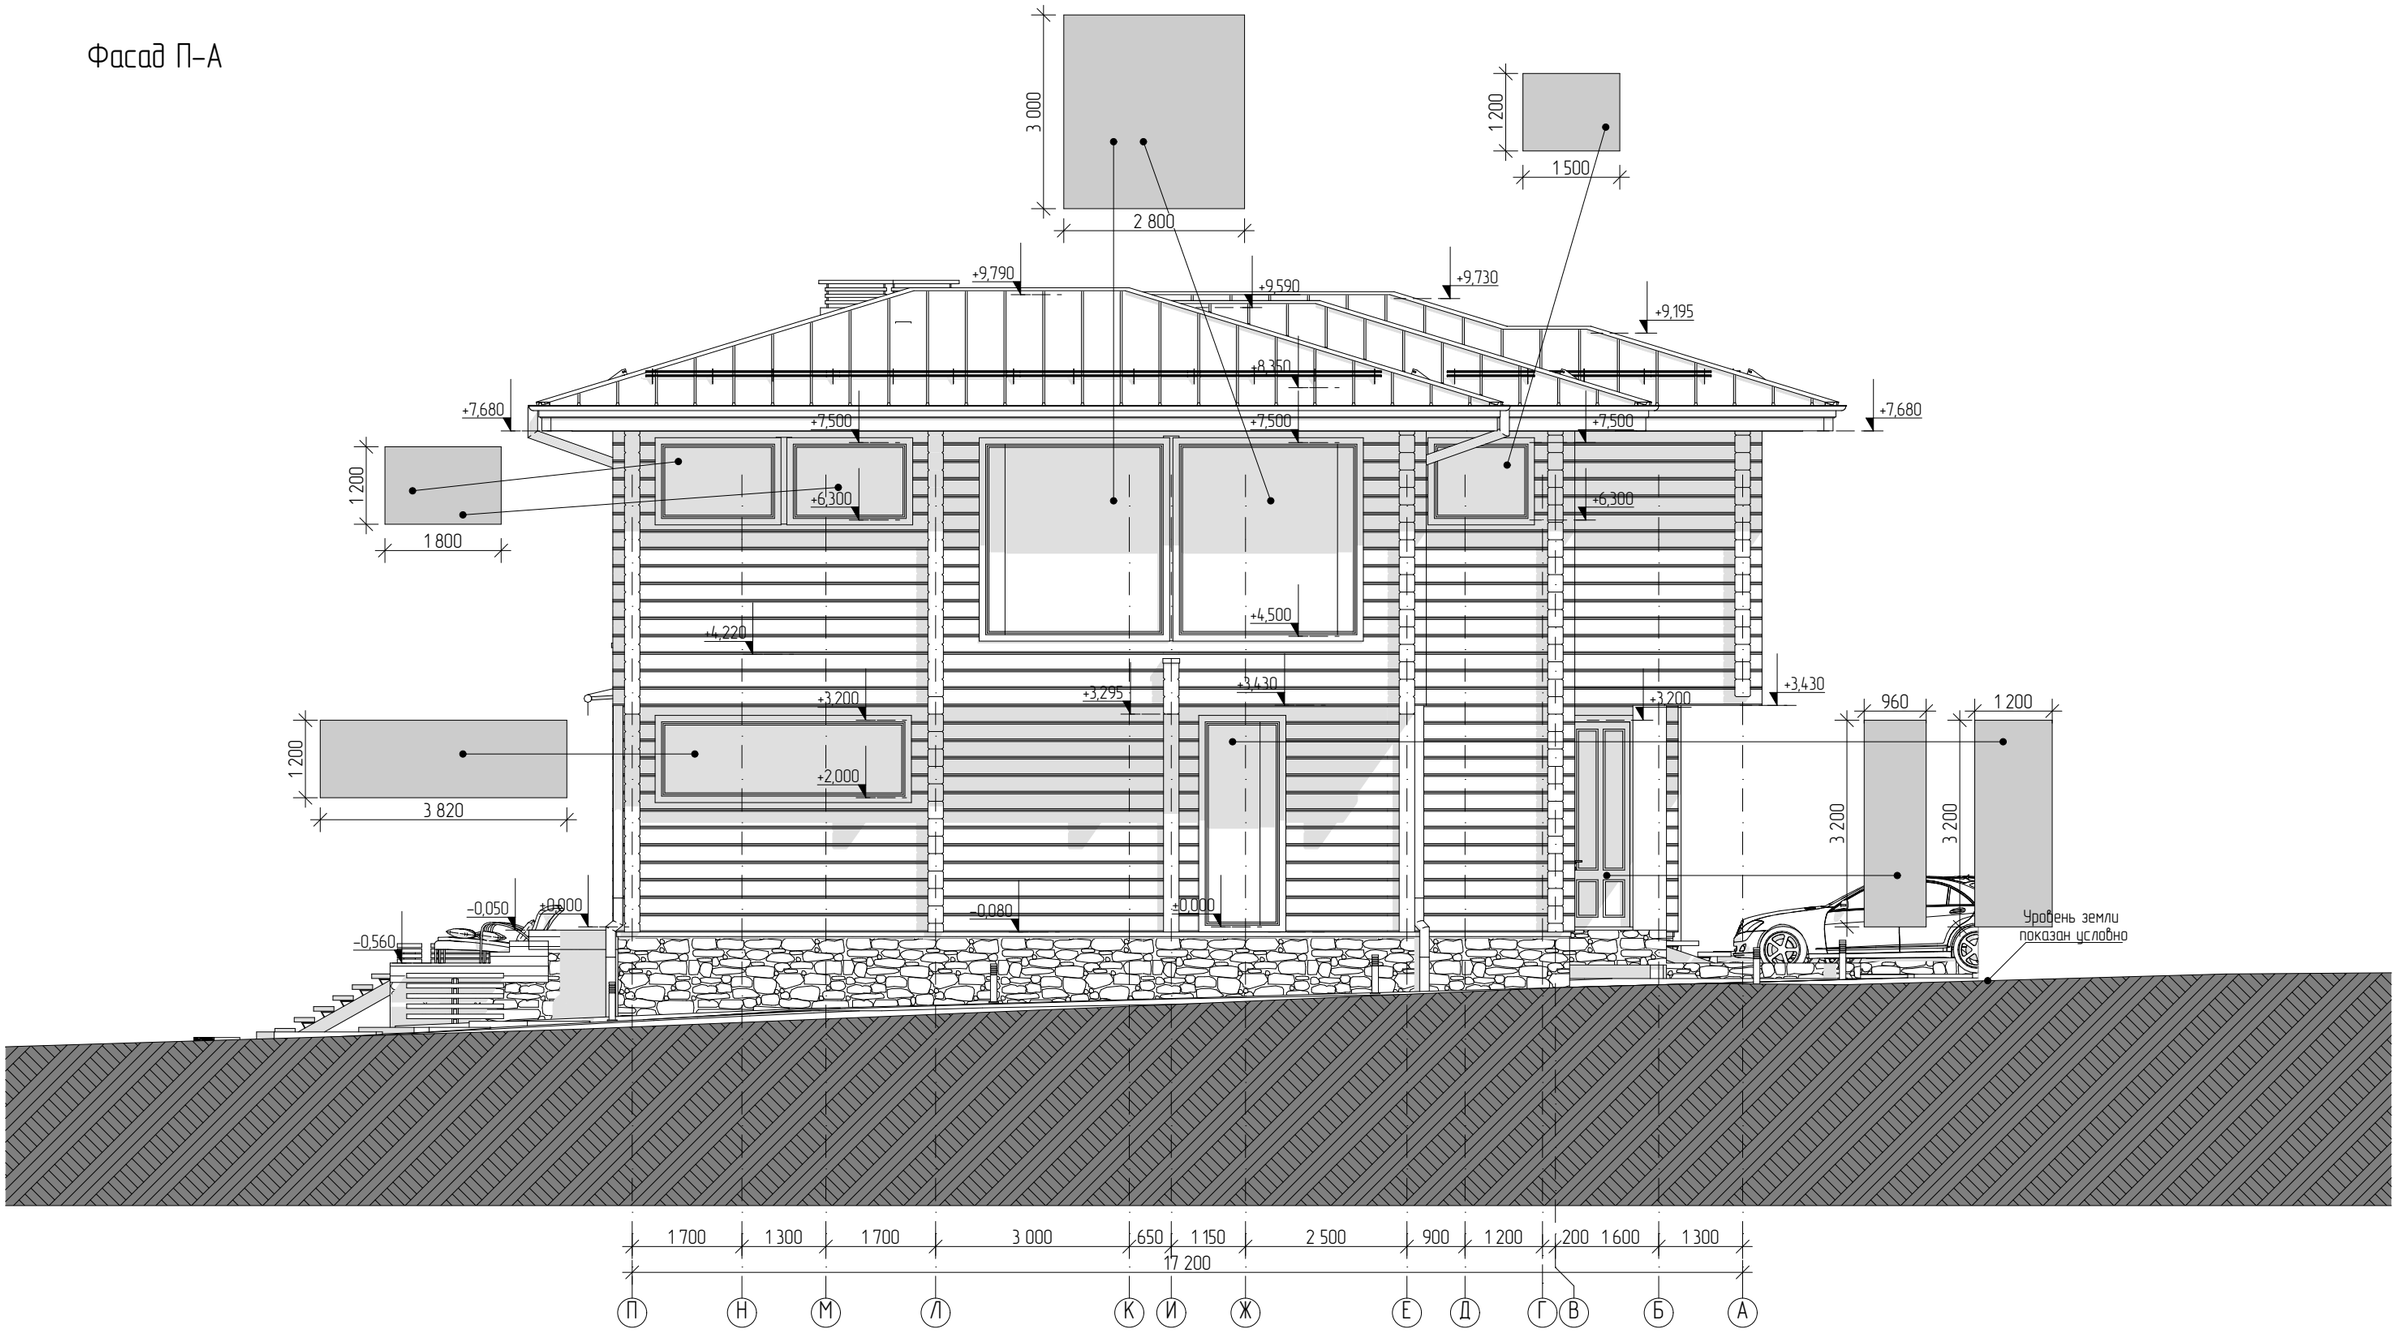

Условные обозначения

±0,000 — Высотные отметки

Примечание :
За отметку ±0,000, принять чистовую отметку первого этажа.
Размеры дверей и окон даны по коробке.
Все декоративные элементы, показаны условно.
См. совместно с листами 3,4,5,6

Пр–т	Проект дома "Берта Ромарио"		Дата	Фасад П–А	Лист
Разраб.	Шолотов И.В.		23.07.2026		19
ГИП	Баннов Е.А.		23.07.2026		



Все декоративные элементы, показаны условно.
Визуализация может отличаться от реализованного проекта.
Цветовое решение дома дано схематично, краска подбирается заказчиком самостоятельно.

Пр–т	Проект дома "Берта Ромарио"		Дата	Перспективное изображение	Лист
Разраб.	Шолотов И.В.		23.07.2026		20
ГИП	Банков Е.А.		23.07.2026		



Все декоративные элементы, показаны условно.
Визуализация может отличаться от реализованного проекта.
Цветовое решение дома дано схематично, краска подбирается заказчиком самостоятельно.

Пр-т	Проект дома "Берта Ромарио"		Дата	Перспективное изображение	Лист
Разраб.	Шолотов И.В.		23.07.2026		21
ГИП	Баннов Е.А.		23.07.2026		



Все декоративные элементы, показаны условно.
Визуализация может отличаться от реализованного проекта.
Цветовое решение дома дано схематично, краска подбирается заказчиком самостоятельно.

Пр-т	Проект дома "Берта Ромария"		Дата	Перспективное изображение	Лист
Разраб.	Шолотов И.В.		23.07.2026		22
ГИП	Банков Е.А.		23.07.2026		



Все декоративные элементы, показаны условно.
Визуализация может отличаться от реализованного проекта.
Цветовое решение дома дано схематично, краска подбирается заказчиком самостоятельно.

Пр-т	Проект дома "Берта Ромарио"		Дата	Перспективное изображение	Лист
Разраб.	Шолотов И.В.		23.07.2026		23
ГИП	Баннов Е.А.		23.07.2026		



Все декоративные элементы, показаны условно.
Визуализация может отличаться от реализованного проекта.
Цветовое решение дома дано схематично, краска подбирается заказчиком самостоятельно.

Пр-т	Проект дома "Берта Ромарио"		Дата	Перспективное изображение	Лист
Разраб.	Шолотов И.В.		23.07.2026		24
ГИП	Баннов Е.А.		23.07.2026		



Все декоративные элементы, показаны условно.
Визуализация может отличаться от реализованного проекта.
Цветовое решение дома дано схематично, краска подбирается заказчиком самостоятельно.

Пр-т	Проект дома "Берта Ромарио"		Дата	Перспективное изображение	Лист
Разраб.	Шолотов И.В.		23.07.2026		25
ГИП	Баннов Е.А.		23.07.2026		



Все декоративные элементы, показаны условно.
Визуализация может отличаться от реализованного проекта.
Цветовое решение дома дано схематично, краска подбирается заказчиком самостоятельно.

Пр-т	Проект дома "Берта Ромарио"		Дата	Перспективное изображение	Лист
Разраб.	Шолотов И.В.		23.07.2026		26
ГИП	Баннов Е.А.		23.07.2026		



Все декоративные элементы, показаны условно.
Визуализация может отличаться от реализованного проекта.
Цветовое решение дома дано схематично, краска подбирается заказчиком самостоятельно.

Пр-т	Проект дома "Берта Ромария"		Дата	Перспективное изображение	Лист
Разраб.	Шолотов И.В.		23.07.2026		27
ГИП	Баннов Е.А.		23.07.2026		



Все декоративные элементы, показаны условно.
Визуализация может отличаться от реализованного проекта.
Цветовое решение дома дано схематично, краска подбирается заказчиком самостоятельно.

Пр-т	Проект дома "Берта Ромарио"		Дата	Перспективное изображение	Лист
Разраб.	Шолотов И.В.		23.07.2026		28
ГИП	Баннов Е.А.		23.07.2026		



Все декоративные элементы, показаны условно.
Визуализация может отличаться от реализованного проекта.
Цветовое решение дома дано схематично, краска подбирается заказчиком самостоятельно.

Пр-т	Проект дома "Берта Ромарио"		Дата	Перспективное изображение	Лист
Разраб.	Шолотов И.В.		23.07.2026		29
ГИП	Баннов Е.А.		23.07.2026		



Все декоративные элементы, показаны условно.
Визуализация может отличаться от реализованного проекта.
Цветовое решение дома дано схематично, краска подбирается заказчиком самостоятельно.

Пр-т	Проект дома "Берта Ромария"		Дата	Перспективное изображение	Лист
Разраб.	Шолотов И.В.		23.07.2026		30
ГИП	Банков Е.А.		23.07.2026		



Все декоративные элементы, показаны условно.
Визуализация может отличаться от реализованного проекта.
Цветовое решение дома дано схематично, краска подбирается заказчиком самостоятельно.

Пр-т	Проект дома "Берта Ромария"		Дата	Перспективное изображение	Лист
Разраб.	Шолотов И.В.		23.07.2026		31
ГИП	Баннов Е.А.		23.07.2026		



Все декоративные элементы, показаны условно.
Визуализация может отличаться от реализованного проекта.
Цветовое решение дома дано схематично, краска подбирается заказчиком самостоятельно.

Пр-т	Проект дома "Берта Ромарио"		Дата	Перспективное изображение	Лист
Разраб.	Шолотов И.В.		23.07.2026		32
ГИП	Баннов Е.А.		23.07.2026		