Общие данные

1. Интернет — оптический ввод от провайдера (ОНТ) в слаботочный шкаф (СШ) у ГРЩ, пом. 3; кабель в земле — в трубе ПНД Ø50 через закладные КЖ0 (10×Ø50).

2. СКС: кабель U/UTP cat.6 звездой от СШ к каждой розетке RJ45 и точке Wi-Fi (PoE).

3. Wi-Fi: 5 потолочных точек на этаж (Wi-Fi 6/7, PoE), бесшовный роуминг; на чердаке — питание от PoE-коммутатора.

4. Видеонаблюдение: 8 IP-камер 4 Мп с ИК-подсветкой по фасадам и у входа/ворот, видеорегистратор (NVR) на 8–16 каналов в СШ, хранение ≥ 14 сут.

5. Домофон: вызывная панель у калитки (IP, с камерой) — кабель в земле в трубе ПНД; мониторы в прихожей и на 2 этаже, приложение на смартфоне.


6. Охрана и пожарная сигнализация — общая радиоканальная централь (291-МЗ.ПС): датчики открытия на входных дверях и витражах 1 этажа, датчики движения в холлах.

7. Умный дом: контроллер в СШ, интеграция по Modbus/KNX/Wi-Fi: котельная (каскад, погодозависимость), тёплые полы (термостаты по комнатам), вентиляция П1В1 (режимы, CO_2), кондиционеры (шлюз VRF), защита от протечек, освещение (сценарии), сауна (дистанционное включение — с ограничением по времени).

8. Все слаботочные кабели в брусе — по тем же каналам «Эл» (291-ЭОМ, листы 9, 10) в отдельной трубе; совместная прокладка с силовыми — запрещена.

9. Питание СШ — отдельная группа ГРЩ С10 + ИБП 1 кВА (≥ 30 мин для роутера, NVR, централи).


Структурная схема

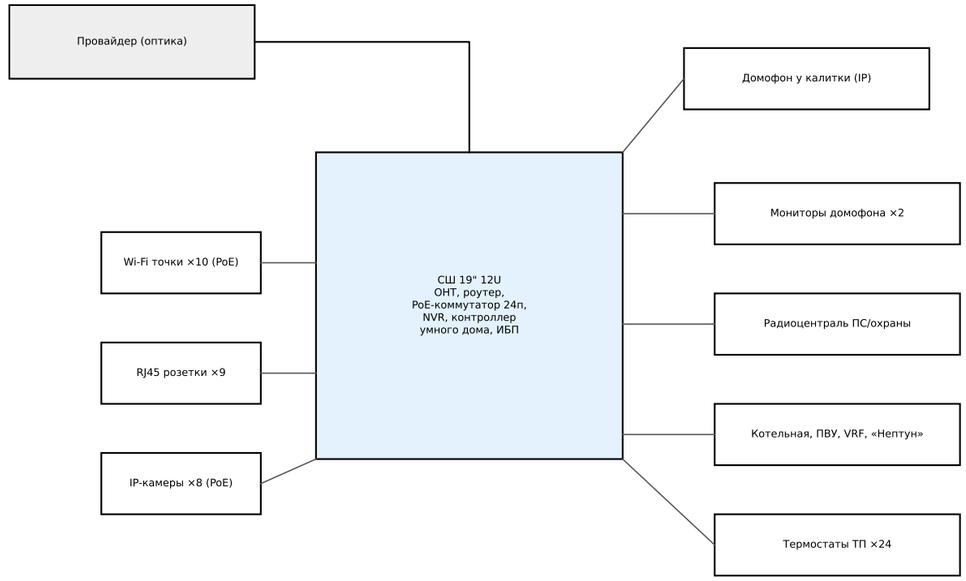

						291-СС
						Индивидуальный жилой дом «Берта Ромарио» Московская обл., Истринский р-н, д. Веледниково, ул. Живописная, д. 25
Изм.	Кол.уч	Лист	№док.	Подп.	Дата	
Разраб.						Общие данные. Структурная схема
Проверил						Стадия: Р; Лист: 1; Листов: 4
ГИП						
Н.контр.						

Формат А3

План 1 этажа. Слаботочные системы (М 1:100)

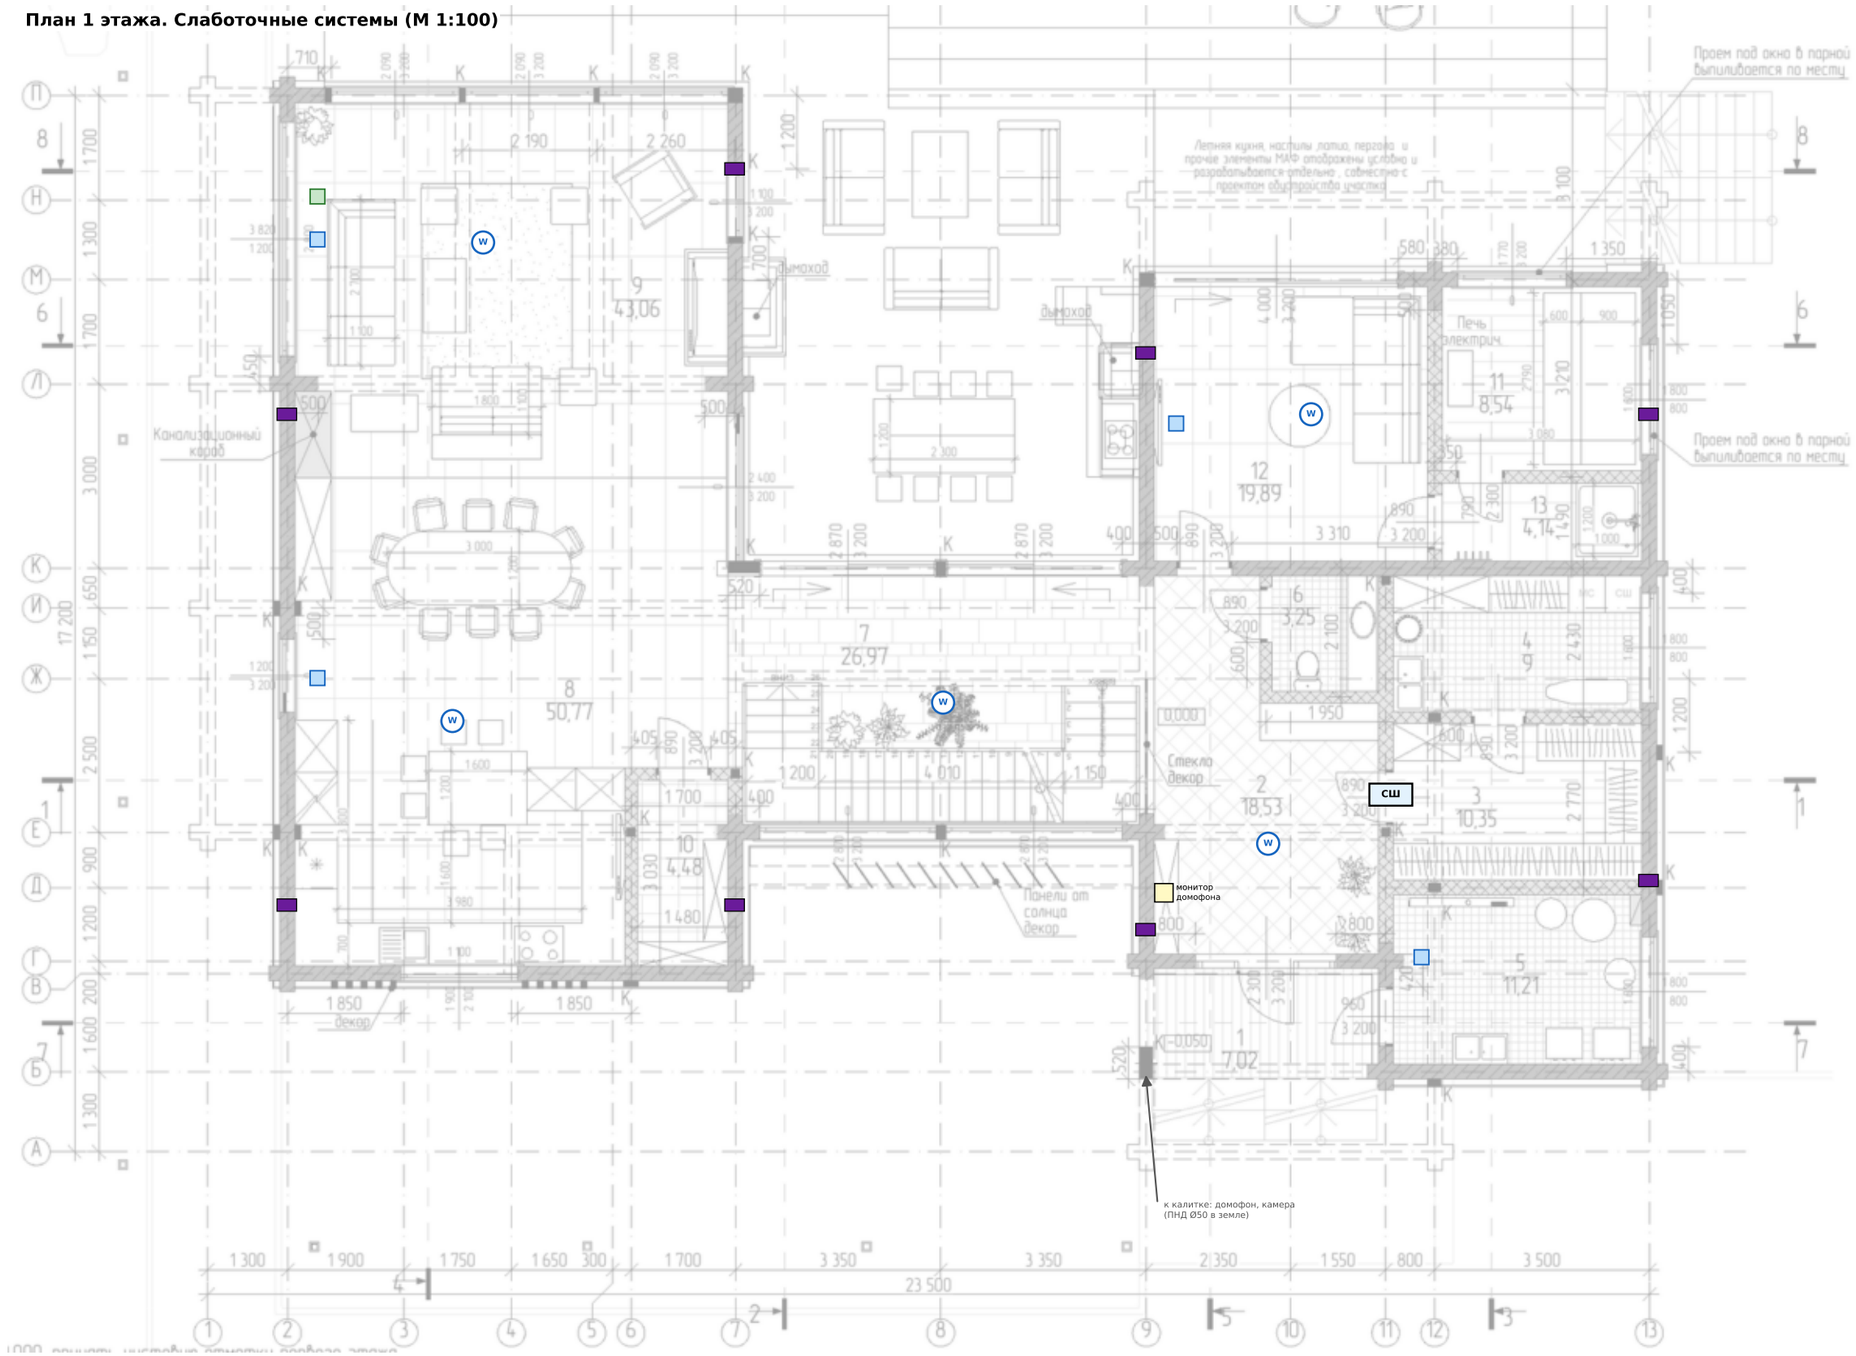

Условные обозначения

- Точка доступа Wi-Fi потолочная (PoE)
- Розетка RJ45 cat.6 (2 порта)
- Розетка ТВ/HDMI-over-IP
- IP-камера (наружная)
- Слаботочный шкаф

Примечания

1. Кабели — U/UTP cat.6 звездой от СШ, в отдельных трубах/металлорукаве.
2. Точки на брусовых стенах — по каналам «Эл» (291-ЭОМ) с отдельной трубой.
3. Места точек доступа — по центру зон, между балками, без металлических экранов.

Изм.	Кол.уч	Лист	№док.	Подп.	Дата
Разраб.					
Проверил					
ГИП					


291-СС

План 1 этажа. Слаботочные системы

Стадия	Лист	Листов
Р	2	

Формат А3

План 2 этажа и чердака. Слаботочные системы (М 1:100)

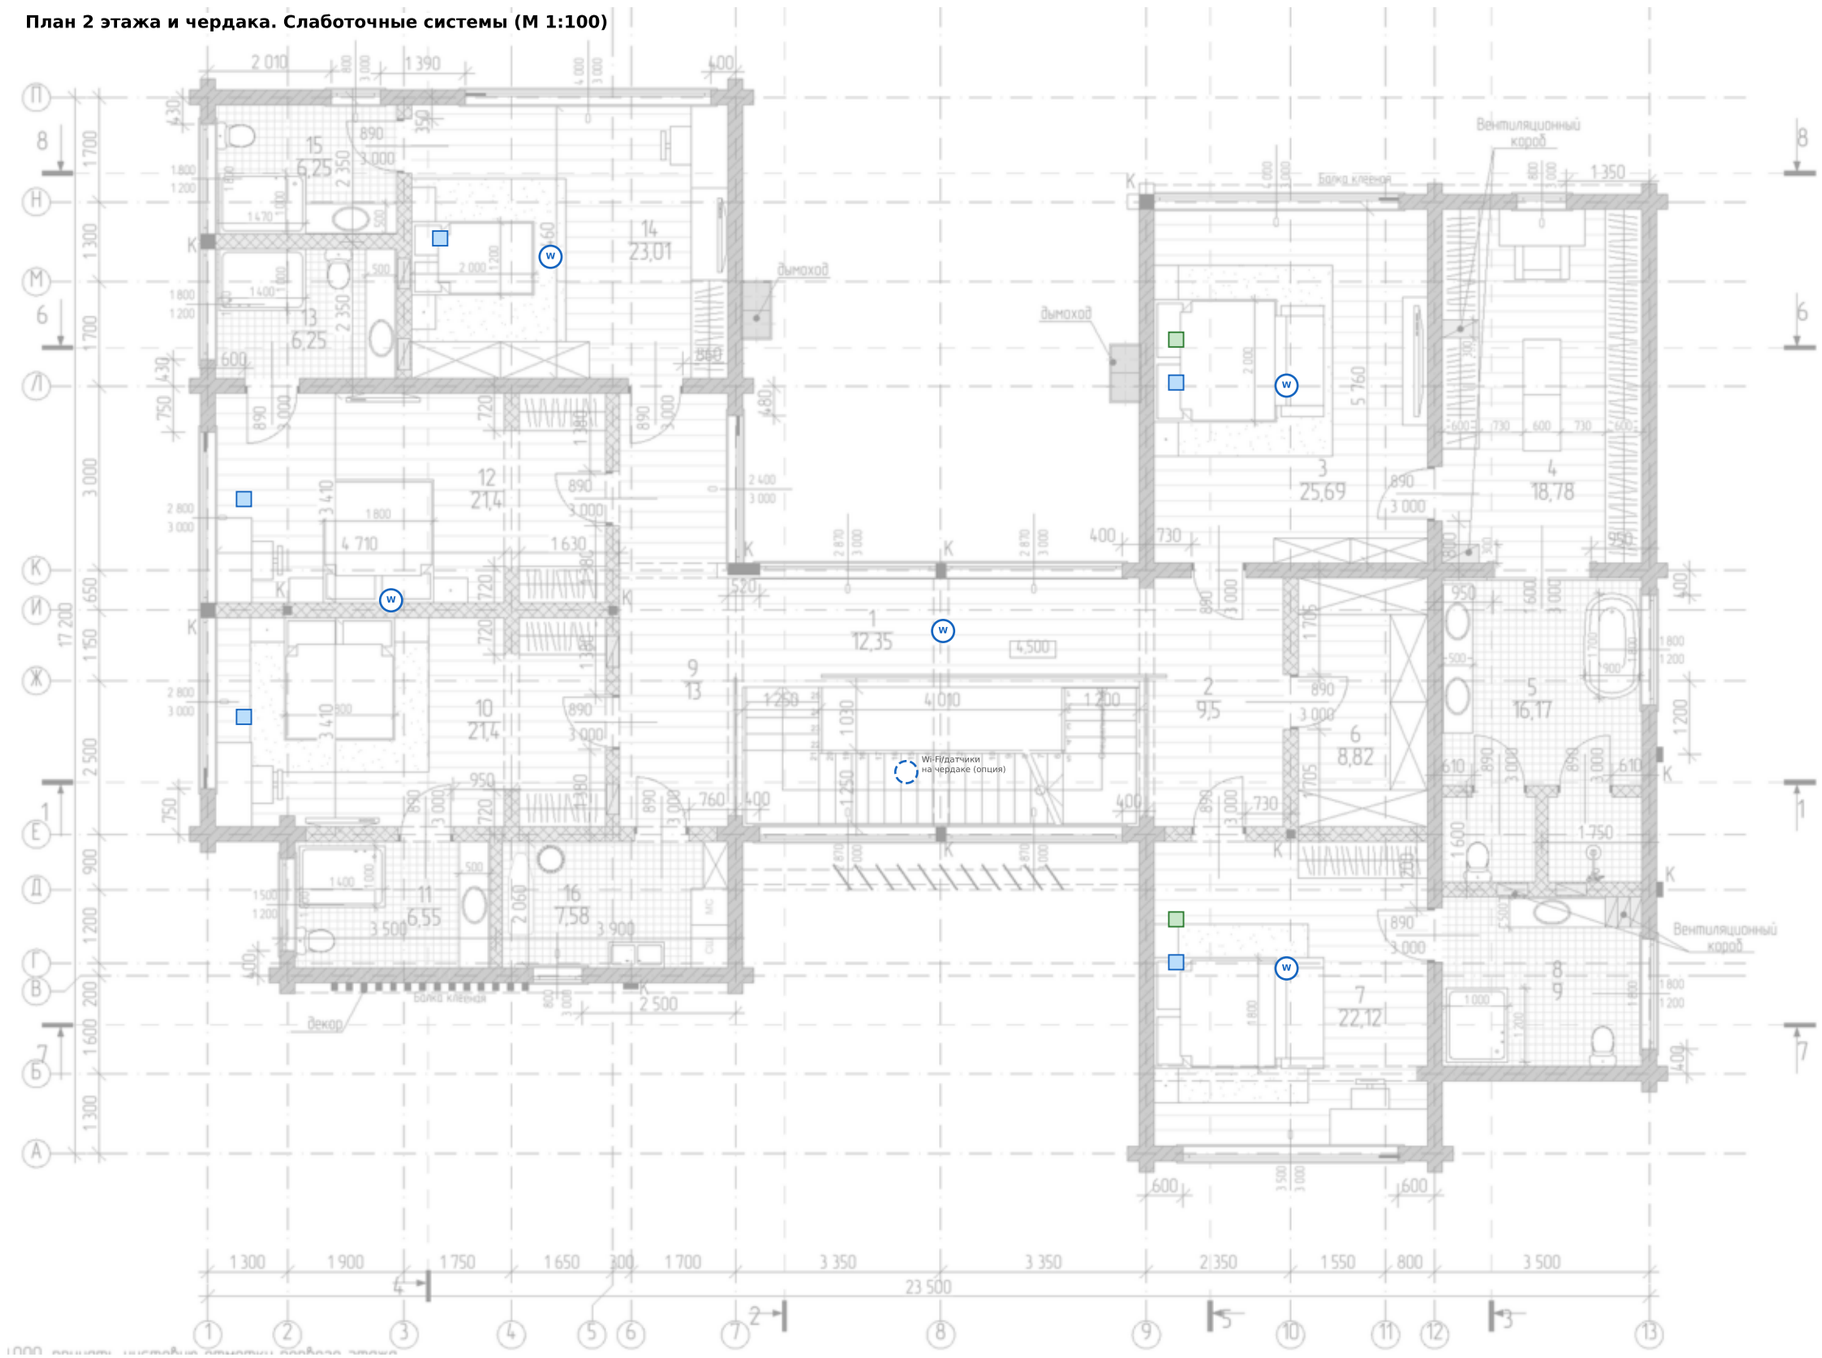

Условные обозначения

- Точка доступа Wi-Fi потолочная (PoE)
- Розетка RJ45 cat.6 (2 порта)
- Розетка ТВ/HDMI-over-IP
- IP-камера (наружная)
- Слаботочный шкаф

Примечания

1. Кабели — U/UTP cat.6 звездой от СШ, в отдельных трубах/металлорукаве.
2. Точки на брусовых стенах — по каналам «Эл» (291-ЭОМ) с отдельной трубой.
3. Места точек доступа — по центру зон, между балками, без металлических экранов.

Изм.	Кол.уч	Лист	№док.	Подп.	Дата
Разраб.					
Проверил					
ГИП					

291-СС

План 2 этажа и чердака. Слаботочные системы

Стадия	Лист	Листов
Р	3	

Формат А3

Спецификация оборудования и материалов

Поз.	Наименование	Тип, марка	Ед.	Кол.	Примечание
	Слаботочный шкаф и активное оборудование				
СШ	Шкаф 19" 12U настенный с вентиляцией и полками		шт.	1	
	Оптический терминал провайдера (ОНТ)	провайдер	шт.	1	
	Маршрутизатор с поддержкой резервного LTE-канала		шт.	1	
	Коммутатор PoE+ 24 порта, управляемый		шт.	1	
	Видеорегистратор (NVR) 16 каналов, HDD 2×4 ТБ		компл.	1	
	Контроллер «умного дома» с модулями Modbus/KNX, шлюз VRF		компл.	1	
	ИБП 1 кВА онлайн		шт.	1	
	Конечные устройства				
	Точка доступа Wi-Fi 6/7 потолочная, PoE		шт.	10	
	IP-камера 4 Мп уличная, ИК 30 м, PoE		шт.	8	
	Вызывная панель IP с камерой, электрозамок калитки		компл.	1	
	Монитор домофона IP 7"		шт.	2	
	Розетка RJ45 cat.6 двойная		шт.	9	
	Розетка TB/HDMI-over-IP		шт.	3	
	Датчики открытия/движения (к централи 291-МЗ.ПС)		шт.	14	
	Кабели и трассы				
	Кабель U/UTP cat.6 LSZH		м	900	Ориентир.
	Кабель U/UTP cat.6 наружный (в земле — в трубе)		м	120	
	Труба ПНД Ø50 (ввод, калитка)		м	80	
	Металлорукав / гофра Ø20 для слаботочки		м	600	

						291-СС
Изм.	Кол.уч	Лист	№док.	Подп.	Дата	
Разраб.						Спецификация оборудования и материалов
Проверил						
ГИП						

Стадия	Лист	Листов
Р	4	

Формат А3