ООО "Строй Хауз"

Берта Ромарио

КД1.Разбрусовка

2026

ООО "Строй Хауз"

Берта Ромарио

КД1.Разбрусовка

Разработал	Москалюк А.
Проверил	Баннов Е.
Конструктор	
ГИП	Баннов Е.
Н.контроль	

2026

Лист 1. Общие данные

№ Листа	Наименование	Примечание
1	Общие данные	
2	Вид 1	
3	Вид 2	
4	Планы этажей 0,000	
5	План кровли	
6	Развертка по стене (оси) 1	
7	Развертка по стене (оси) 2	
8	Развертка по стене (оси) 3А	
9	Развертка по стене (оси) 3Б	
10	Развертка по стене (оси) 3В	
11	Развертка по стене (оси) 3ч	
12	Развертка по стене (оси) 4	
13	Развертка по стене (оси) 4ч	
14	Развертка по стене (оси) 5	
15	Развертка по стене (оси) 7	
16	Развертка по стене (оси) 9	
17	Развертка по стене (оси) 10	
18	Развертка по стене (оси) 11	
19	Развертка по стене (оси) 11ч	
20	Развертка по стене (оси) 12	
21	Развертка по стене (оси) 13	
22	Развертка по стене (оси) А	
23	Развертка по стене (оси) Б	
24	Развертка по стене (оси) В	
25	Развертка по стене (оси) Г	
26	Развертка по стене (оси) Е	
27	Развертка по стене (оси) Еч	
28	Развертка по стене (оси) Ж	
29	Развертка по стене (оси) И	
30	Развертка по стене (оси) К	
31	Развертка по стене (оси) Кч	
32	Развертка по стене (оси) Л	
33	Развертка по стене (оси) Лч	
34	Развертка по стене (оси) М	
35	Развертка по стене (оси) Н	
36	Развертка по стене (оси) П	

Ведомость основных комплектов рабочих чертежей

Обозначение	Наименование	Примечание
- АР		
- АС		

ОБЩИЕ ДАННЫЕ

1. Данный комплект чертежей выполнен на основании архитектурно-планировочных решений
2. Проект разработан для площадки со следующими природно-климатическими условиями:
- ветровой район - I;
- снеговой район - III;
- нормативная глубина сезонного промерзания:
- глина или суглинок - 1,03м;
- супесь, пески пылеватые или мелкие - 1,25м;
- песок средней крупности, крупный или гарвелистый - 1,34м;
3. За относительную отметку ±0,000 принят уровень чистого пола 1 этажа.
4. Посадку сооружения смотри чертежи генплана.
5. Отклонения в размерах конструкций не должны превышать предельных значений, приведенных в табл.4.11 СП 70.13330.2012 "Несущие и ограждающие конструкции ".

						- АР
Изм.	Кол. уч.	Лист	№ док.	Подпись	Дата	
Разработал		Москалюк А.				Берта Ромарио
Проверил		Баннов Е.				Стадия: Р; Лист: 1.1; Листов: 2
Конструктор						ООО "Строй Хауз"
ГИП		Баннов Е.				
Н.контроль						

6. Стеновой брус выполен сечением 240х320h (310h).

Необходимо соблюдать следующие требования хранения клееного материала:
- клееные деревянные брусья допускается складировать под открытым небом при условии их защиты от солнца, осадков и сырости грунта;
- под нижний ряд штабеля или под нижний транспортный пакет должны быть уложены опоры высотой не менее 100 мм при хранении в складских помещениях и не менее 500 мм - при хранении под навесом или на открытой площадке. При краткосрочном хранении на строительной площадке допускается 100 мм при хранении под навесом. Укладка конструкций и элементов непосредственно на грунт не допускается. Для обеспечения достаточной устойчивости и предотвращения деформаций при хранении слегами расстояние между ними должно быть не более 1,5 м;
- не допускается образования луж под клееными деревянными брусьями;
- не допускается использование прозрачной пленки в качестве тента для укрытия складируемого бруса;
- не допускается намокание уплотнителя в ходе сборки комплекта (выступающие куски уплотнителя, во избежание намокания, срезают в течение рабочего дня);
- возводимые конструкции закрывают во время сборки от длительных дождей. При этом необходимо обеспечивать достаточную циркуляцию воздуха под тентом.

ОБЩИЕ УКАЗАНИЯ по сборке стен из бруса.


Крепление первого венца к подвенечному окладу осуществляется нагелями. Диаметры отверстий под нагель должны быть на 1мм меньше диаметра нагеля. Нагель должен заходить с натягом. Соединение венцов по вертикали осуществляется шпильками через заранее подготовленные отверстия. Шпильки затягиваются через два или три венца в зависимости от высоты бруса. Перемычки над простенками оконными, дверными и прочими проемами затягиваются сразу после их укладки. При сборке простенков их необходимо крепить нагелями в разбежку, а шпильки затягивать только на уложенной перемычке.

						- АР	Лист
Изм.	Кол. уч.	Лист	№ док.	Подпись	Дата		2

Условные обозначения:

 или Ш - отверстие под шпильку

 или Н - отверстие под нагель

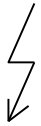 или Эл - отверстие под электропроводку

 - Т-образное крепление (Т1, Т2, Т3, Т4)

Г - Т-образное крепление на глухарь

 - стягивание венцов глухарями

 - отверстие под закладную для домкрата (ЗД1, ЗД2)

Л - крепление затяжки к колонне


 - клееная балка, см. РД “Клееный материал”

Все видимые брусовые балки прострогать снизу на 20мм


В дверных и оконных проемах гребневый паз доработать вручную на площадке до проектных отметок

Крепление брусовой стены к подвенечному окладу, начиная

с целого бруса

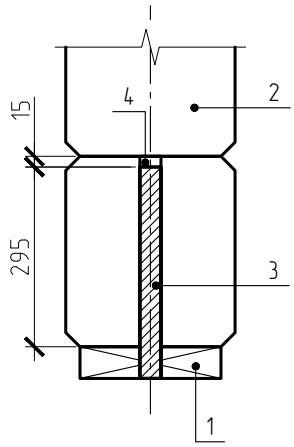

с половинчатого бруса

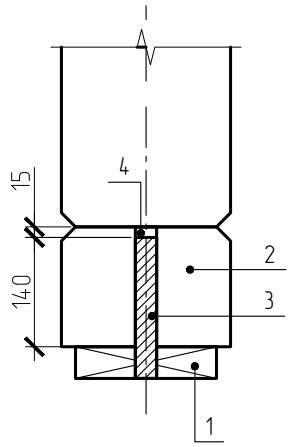


Обозн-е	Наименование	Обозн-е	Наименование
1	Подвенечный оклад, устройство и сечение см. КД3	3	Нагель L=200мм, шаг 800
2	Брусовая стена	4	Отверстие под нагель


Изм.	Лист	№ докум.	Подп.	Дата	Крепление к подвенечному окладу	Лист

Формат А4


Уплотнение внешних чашек

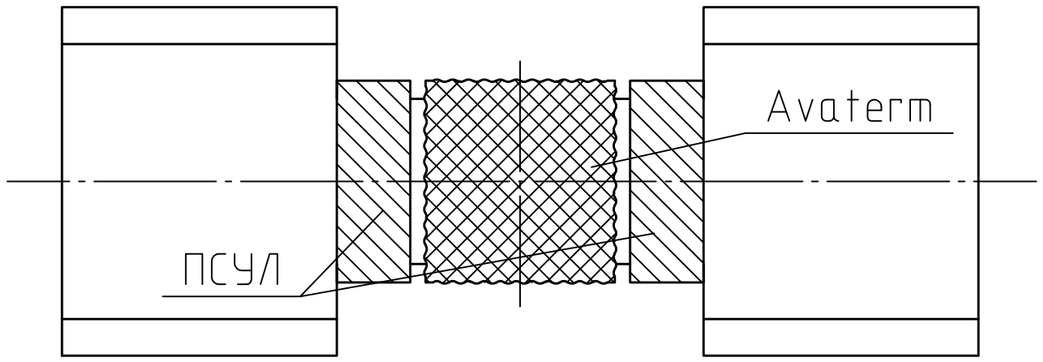


Вид сверху

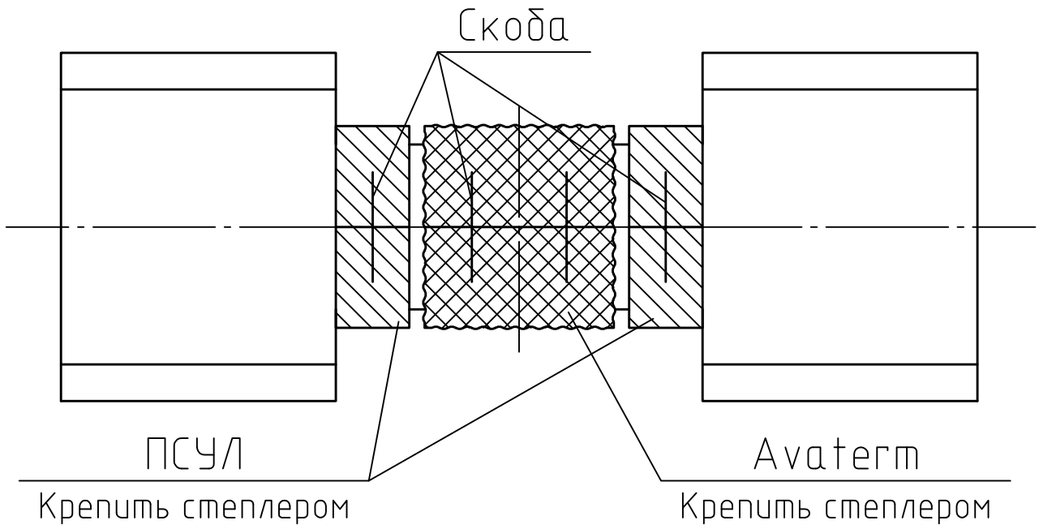


Уплотнение внутренних чашек

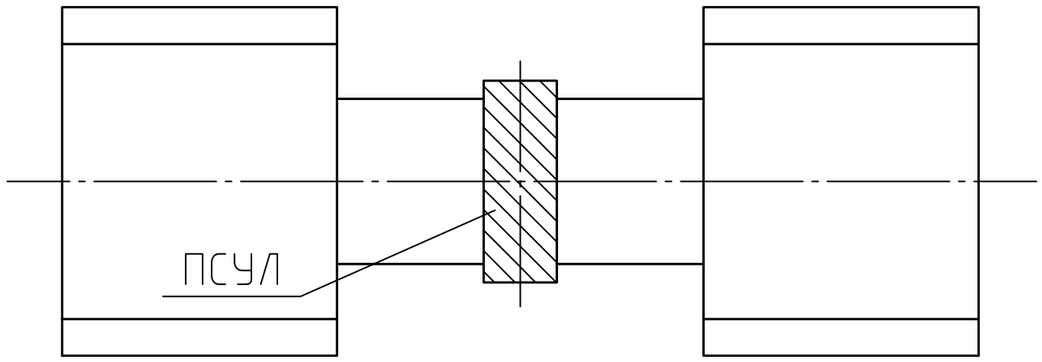


Вид сверху

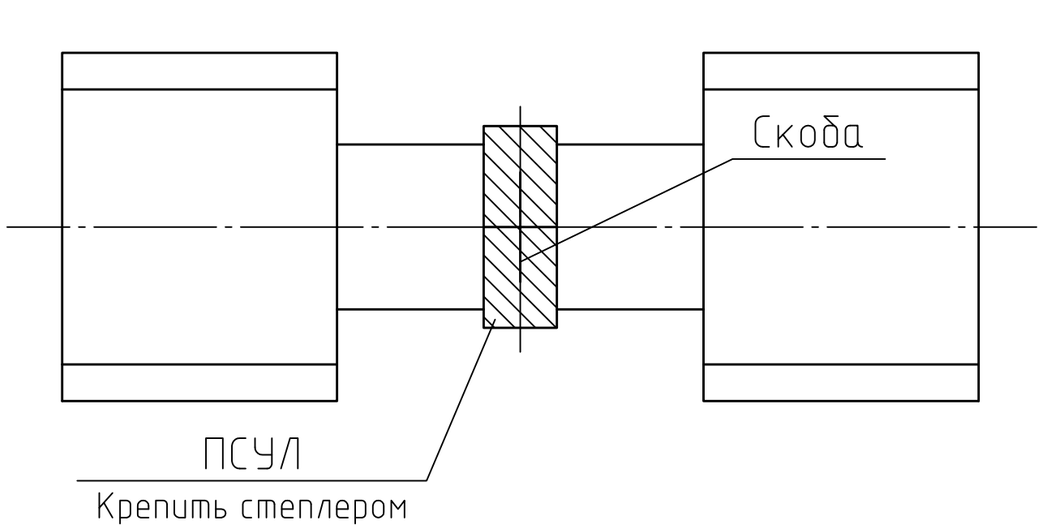


Изм	Лист	№ докум.	Подп.	Дата	Схема утепления чашек	Лист

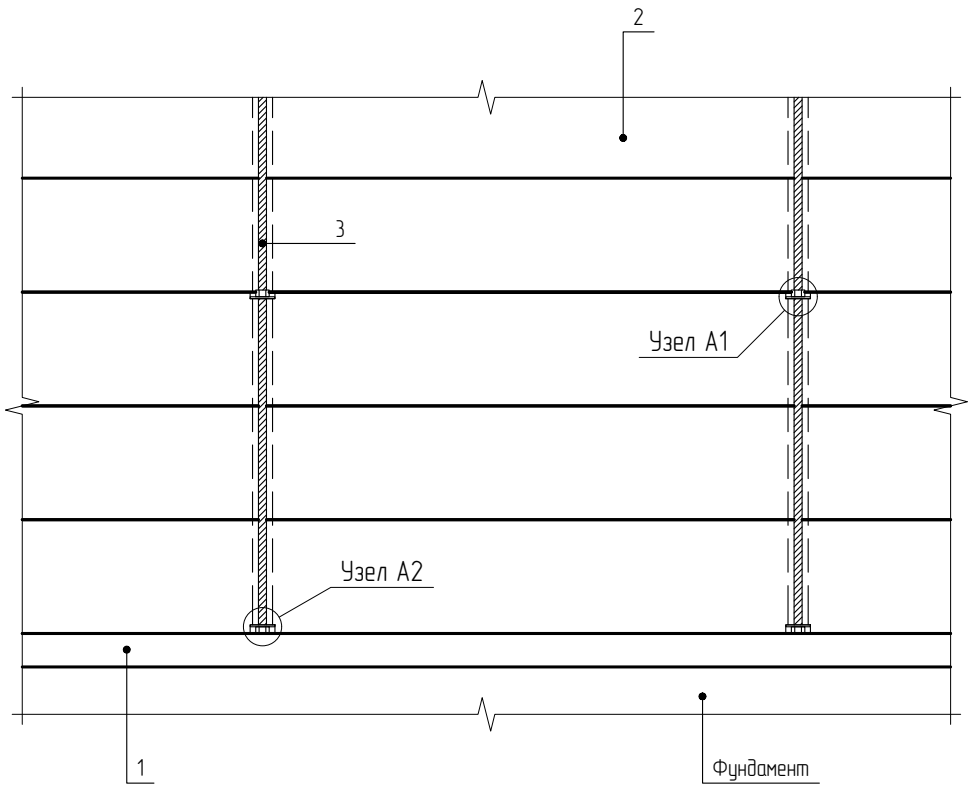

Узел А1

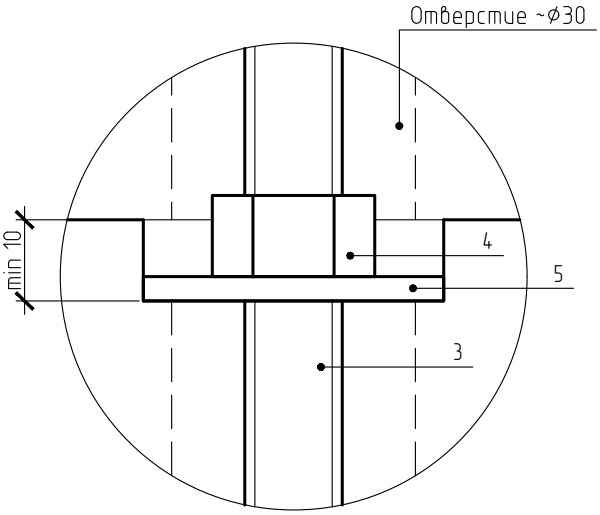

Узел А2

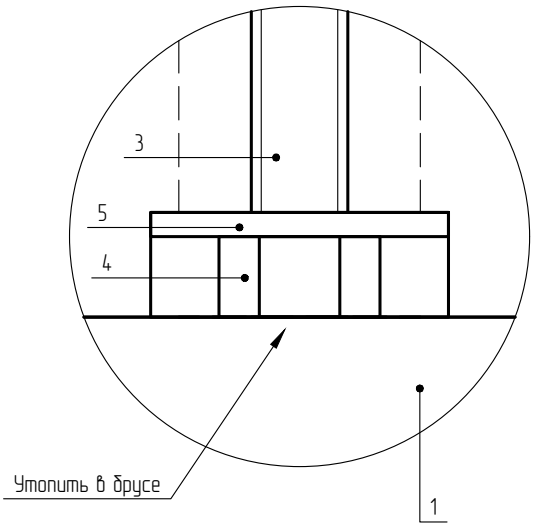


1. При hбр < 200мм стягивать по узлу А1 каждые 3 венца, при hбр > 200мм – каждые 2 венца

Обозн-е	Наименование	Обозн-е	Наименование
1	Подвенечный оклад строганый	4	Гайка М12 оц. усиленная
2	Брусовая стена	5	Шайба оц. усиленная, вн.диаметр ф37
3	Шпилька М12	6	

Изм.	Лист	№ докум.	Подп.	Дата	Устройство брусовых стен	Лист

Формат А4

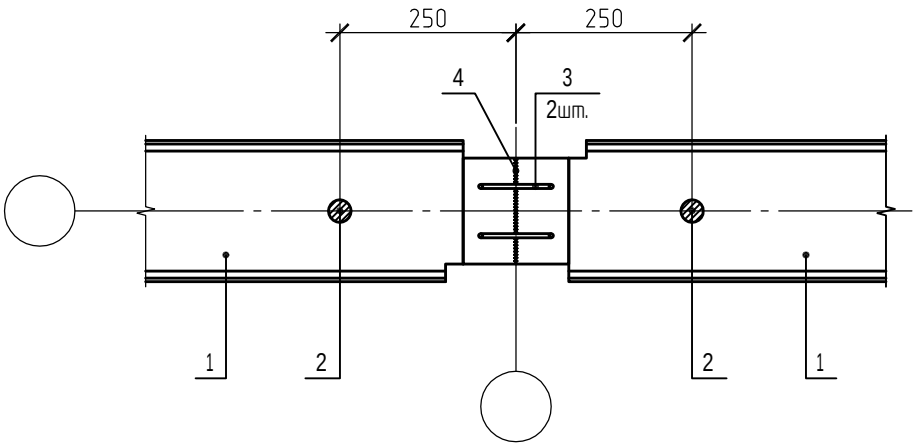


Стандартное уплотнение чашек Avaterm'ом и ПСУЛ условно не показано. Уплотнение чашек выполнять согласно "Схеме утепления чашек."


Обозн-е	Наименование	Обозн-е	Наименование
1	Брус	4	Уплотнитель Avaterm
2	Нагель ф30-32		
3	Соединительная скоба L=110-140мм		


					Соединение по длине	Лист
Изм.	Лист	№ докум.	Подп.	Дата		


Формат А4


Узел применяется только для проемов окон и внешних дверей

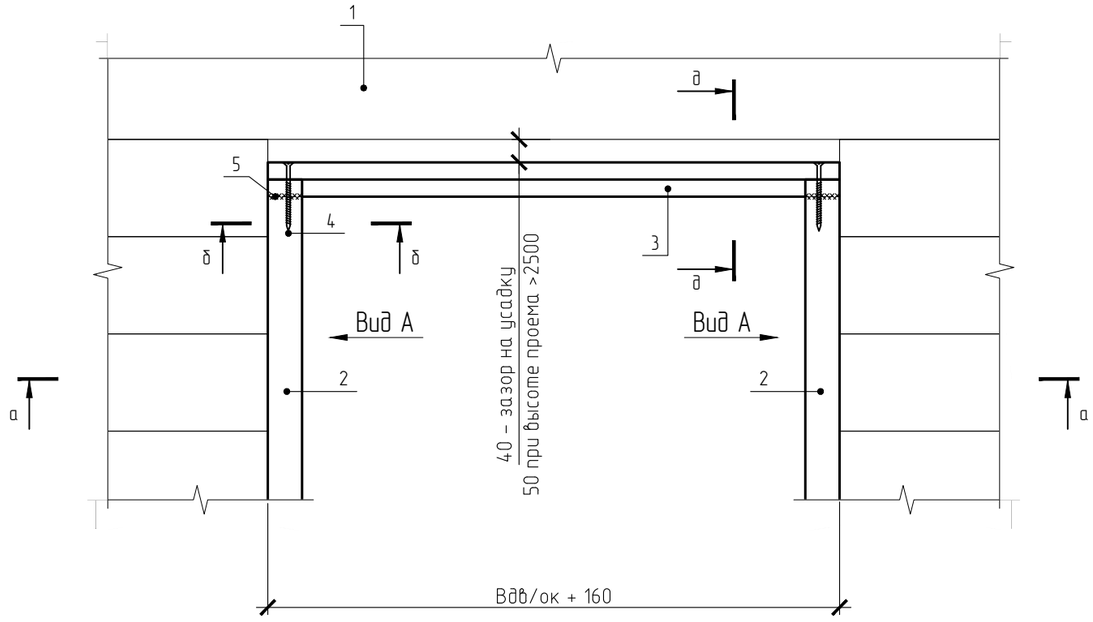


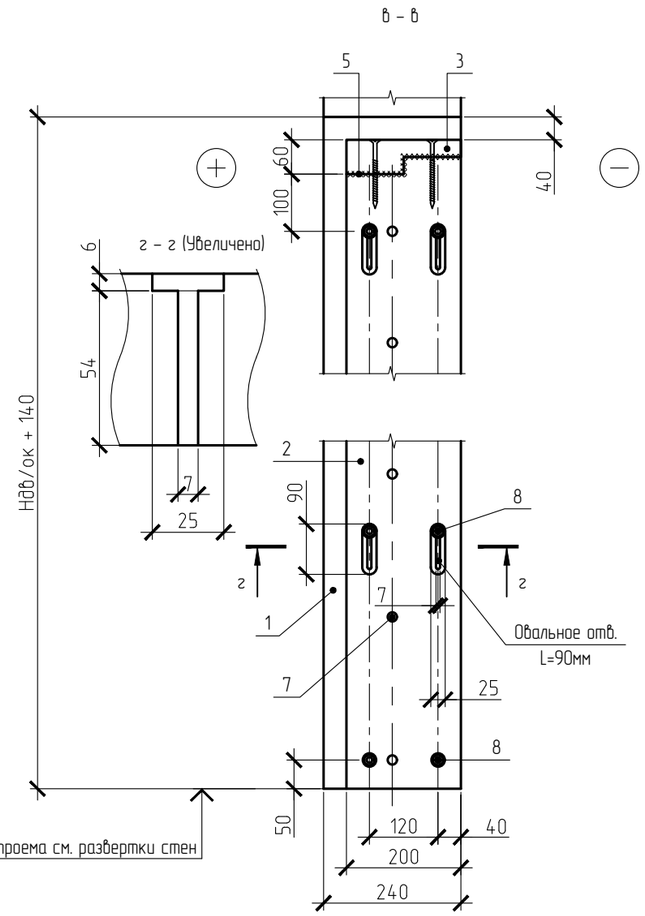

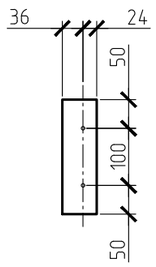

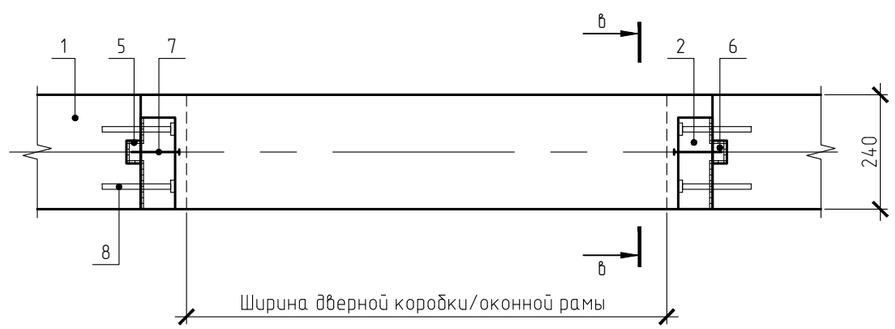

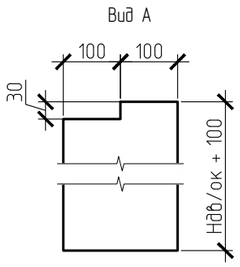

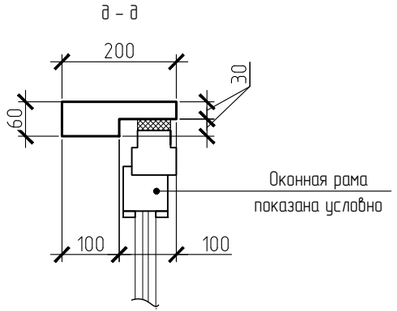

Примечания.


1. Данный узел используется только для обустройства обсадных коробок проемов для наружних дверей и окон;
2. Обсадная коробка собирается заранее на стройплощадке. Затем монтируется в соответствующий проем.


Обозн-е	Наименование	Обозн-е	Наименование
1	Брусовая стена	7	Саморез L=80мм шаг 250, крепить строго к бруску
2	Клееная обсадная 60х200 (боковая)	8	Глухарь 6х120 с шайбой шаг 400, не затягивать до конца
3	Клееная обсадная 60х200 (перемычка)		
4	Саморез с/н "потай" 6х140 по 2шт.		
5	Уплотнитель AVATERM		
6	Брусок		


Изм.	Лист	№ докум.	Подп.	Дата	Крепление клееных обсадных	Лист

Формат А3

Узел применяется только для проемов межкомнатных дверей

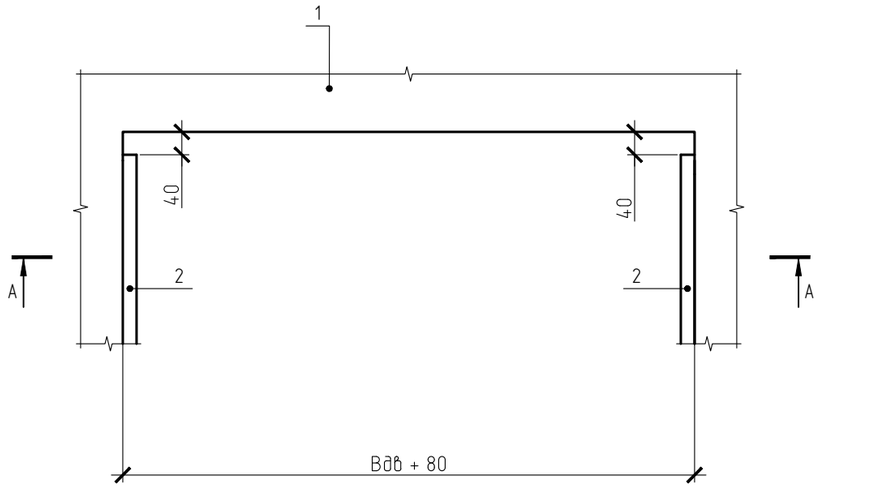

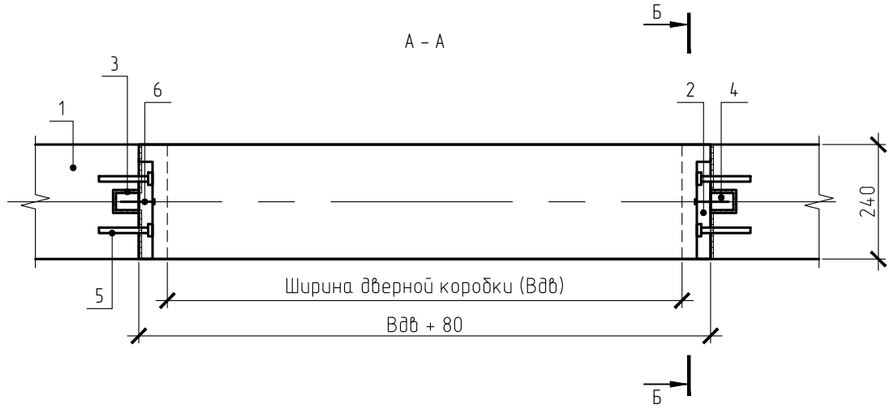


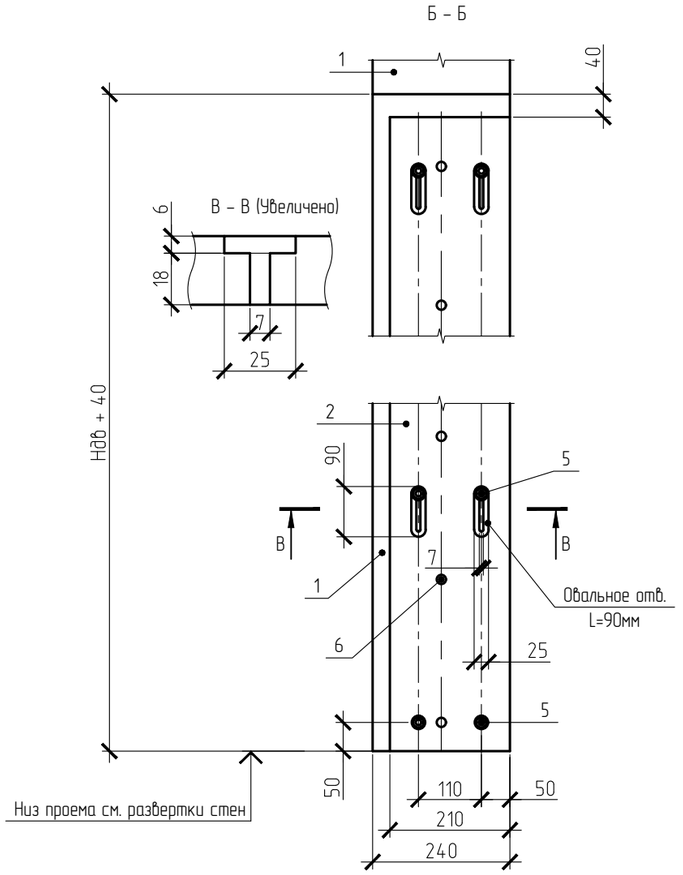


Обозн-е	Наименование	Обозн-е	Наименование
1	Брусовая стена		
2	Фанера =24мм шириной 210мм		
3	Уплотнитель AVATERM		
4	Брусок		
5	Глухарь 6х100 с шайбой шаг 400, не затягивать до конца		
6	Саморез L=60мм шаг 250, крепить строго к бруску		

Изм.	Лист	№ докум.	Подп.	Дата	Крепление обсадных из фанеры	Лист

Формат А3

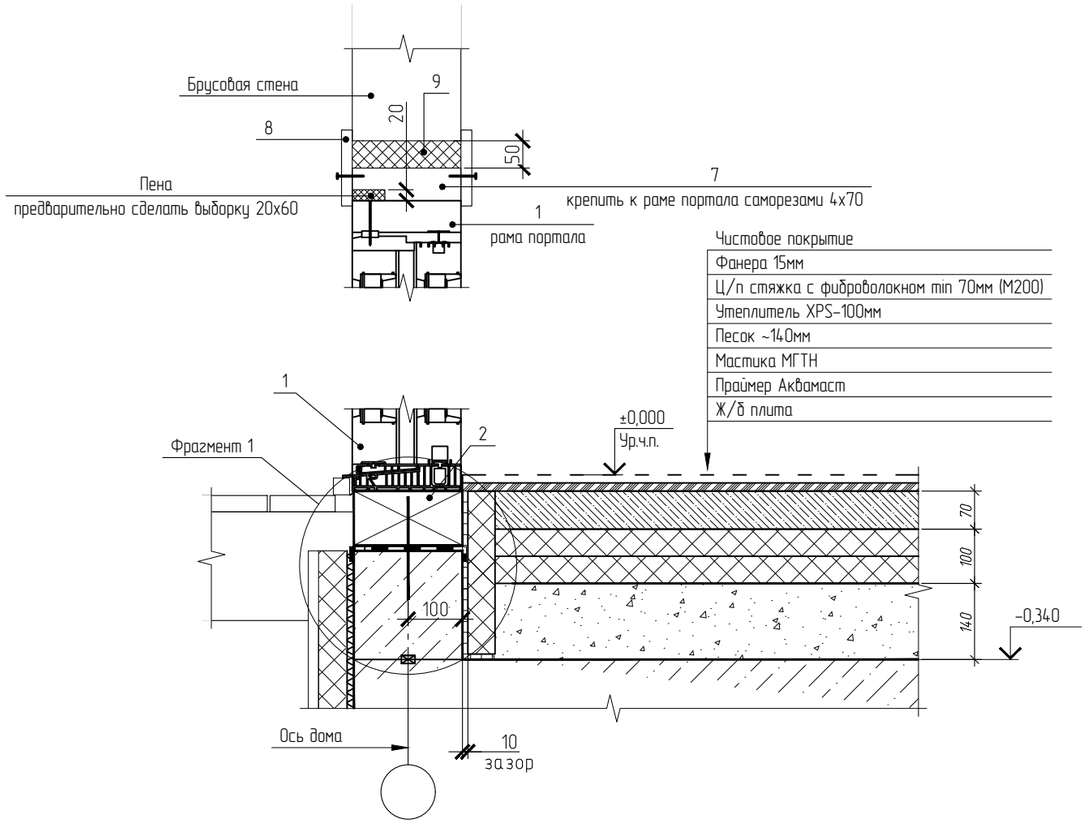

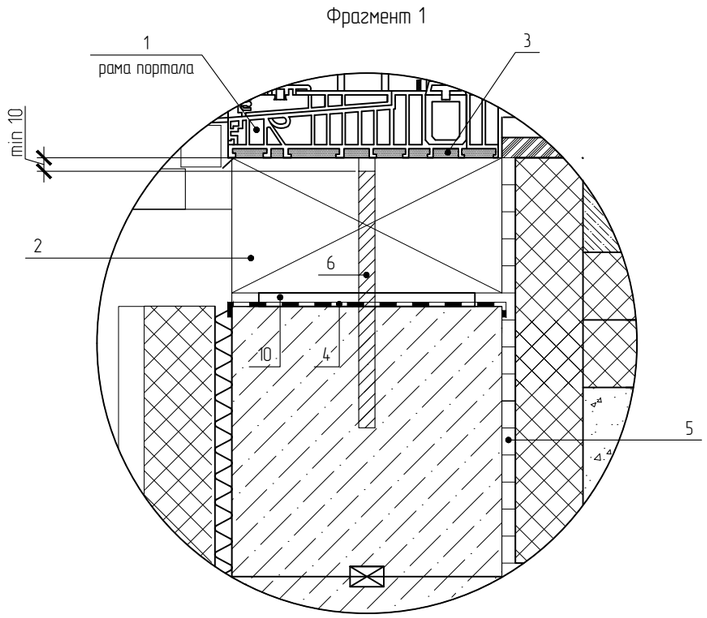


Обозн-е	Наименование	Обозн-е	Наименование
1	Сдвижной портал	6	Анкер ⌀12А500С L=190мм, с шагом по фанере
2	Клееный подвенечный оклад 200х100h (240/160х100h)	7	Клееная перемычка 200х60h (240х60h)
3	Уплотнитель Велотен t=10мм	8	Наличник
4	Техноэласт, клеить мастикой	9	Утеплитель (элестичная пена)
5	Демпферный шов, пенофол t=10мм	10	Ламинированная фанера t=12мм шаг 150, торцы обмазать мастикой

Примечания:
1. Зазор между подвенечным окладом и фундаментом по внешнему периметру заполнить пеной (на основе пенополиуритана) путем нагнетания пены, нагнетать следует по всей плоскости зазора без воздушных пустот и мешков. После окончательного отвердения пены, выступающие наплывы срезать. Не допускается запенивать зазоры до сборки коробки сооружения. Пена должна соответствовать по температуре применения в летнее или зимнее время.


Изм.	Лист	№ докум.	Подп.	Дата	Устройство сдвижного портала	Лист

Формат А3


Узел Б. Стягивание венцов

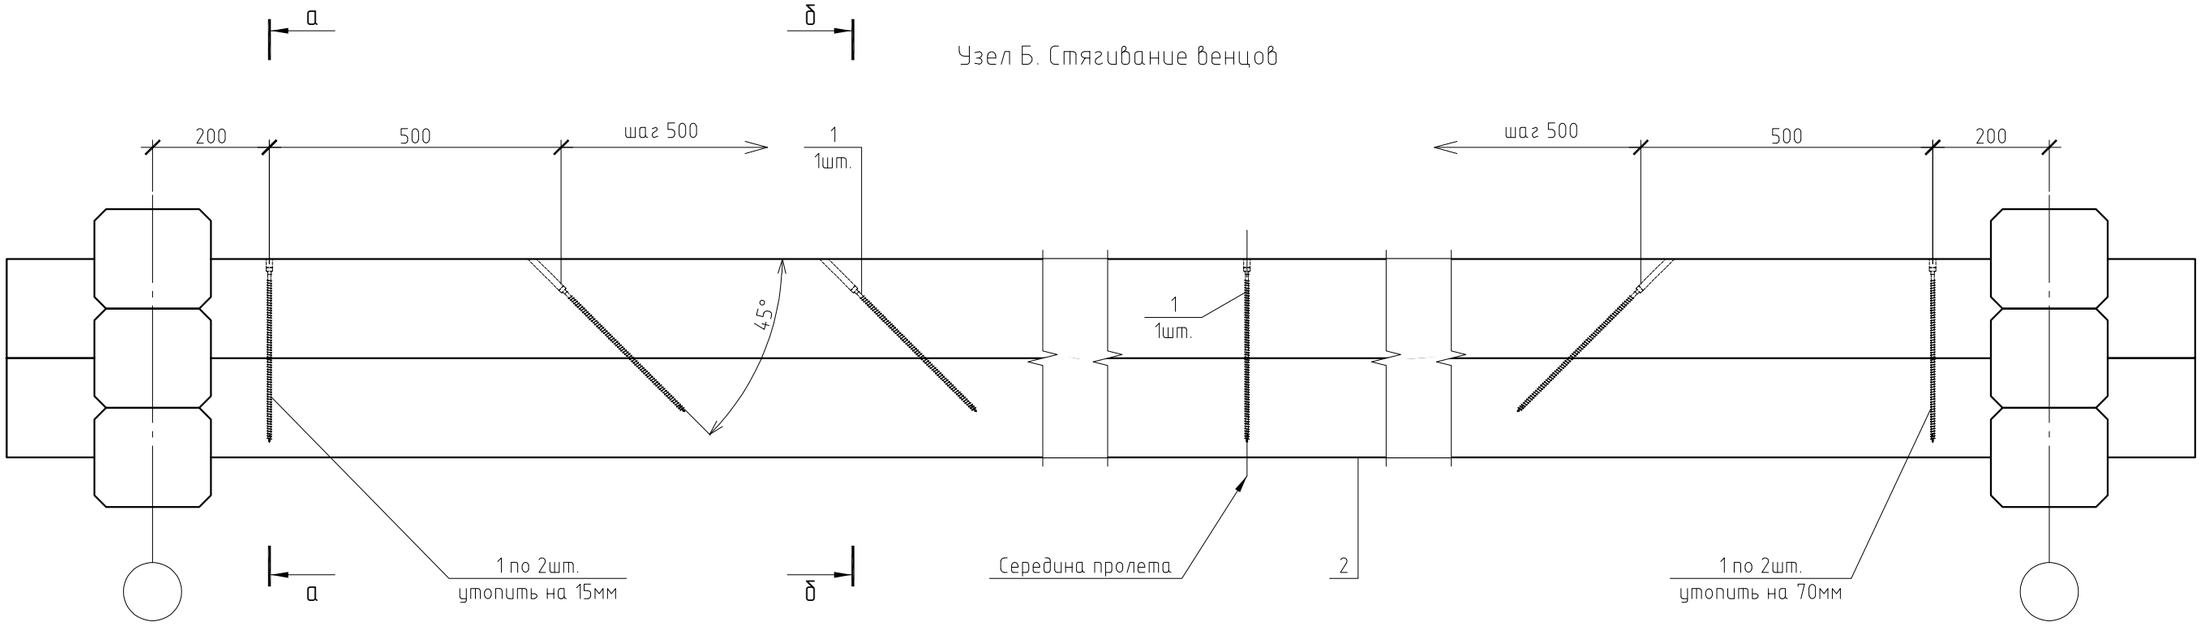

а - а

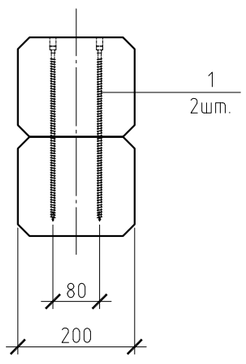

б - б

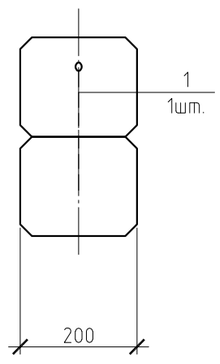

Примечания:

1. Саморезы вкручивать в предварительно просверленные отверстия ф5.


Обозн-е	Наименование
1	Полнорезьбовой саморез 8х300 при высоте клееного бруса h<200, Полнорезьбовой саморез 8х400 при высоте клееного бруса h>200
2	Клееный брус

Изм.	Лист	№ докум.	Подп.	Дата	Узел Б. Стягивание венцов	Лист


Формат А3

PDF создан с пробной версией pdfFactory Pro www.pdffactory.com

Узел Г

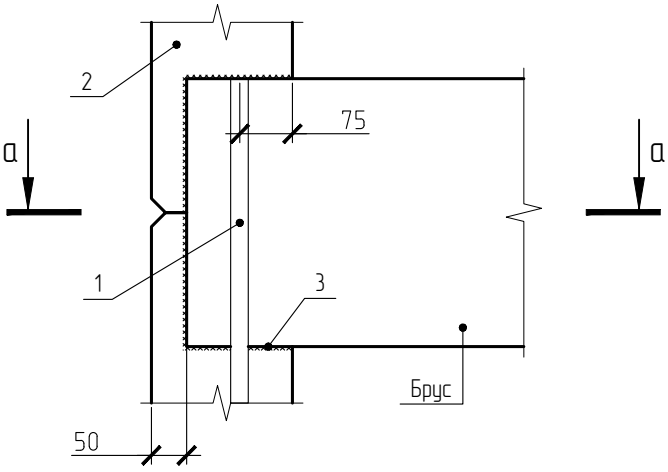

а – а

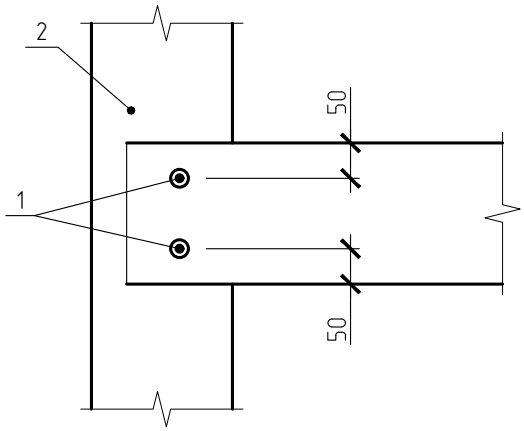


Обозн-е	Наименование	Обозн-е	Наименование
1	Нагель ф20 L=550мм, 2шт.	3	Уплотнитель Avaterm
2	Брусовая балка		


Изм.	Лист	№ докум.	Подп.	Дата	Узел Г	Лист

Формат А4

Узел Т

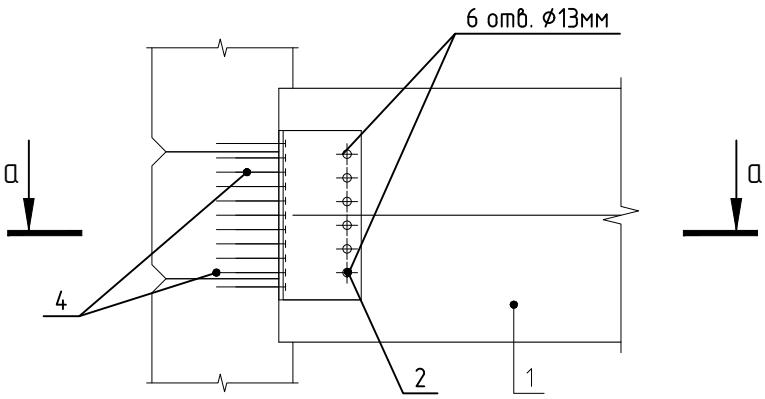

а – а

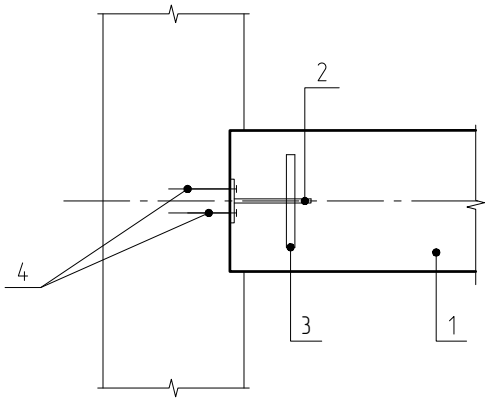


Обозн-е	Высота кронштейна	Кол-во гвоздей 4,2х90	Кол-во дюбелей ф12
Т120	120	20	2
Т160	160	28	3
Т200	200	36	4
Т240	240	44	5
Т320	320	60	7
Т400	400	76	9
Т480	480	92	11

Обозн-е	Наименование	Обозн-е	Наименование
1	Балка брусовая	4	Гвозди ершеные 4,2х90 (кол-во штук с каждой стороны
2	Т-образный кронштейн (высоту см. таблицу)		см. таблицу)
3	Стальной дюбель ф12мм, (кол-во штук см. таблицу)		

Изм.	Лист	№ докум.	Подп.	Дата	Узел Т	Лист

Формат А4

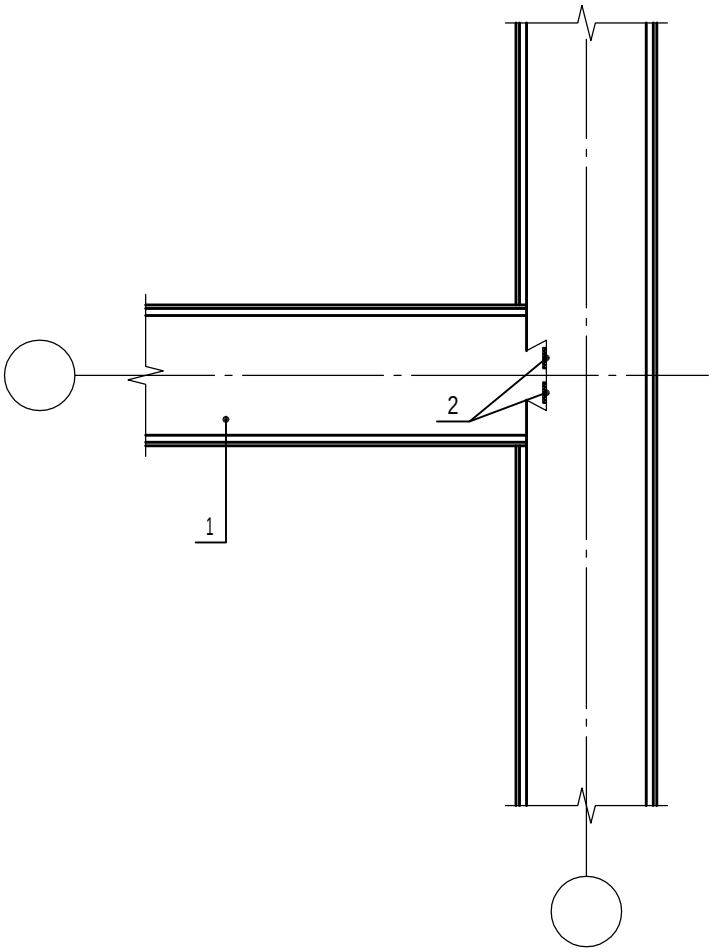


Обозн-е	Наименование	Обозн-е	Наименование
1	Брус		
2	ПСУЛ		

Изм.	Лист	№ докум.	Подп.	Дата	Соединение "Ласточкин хвост"	Лист

Формат А4


Бд

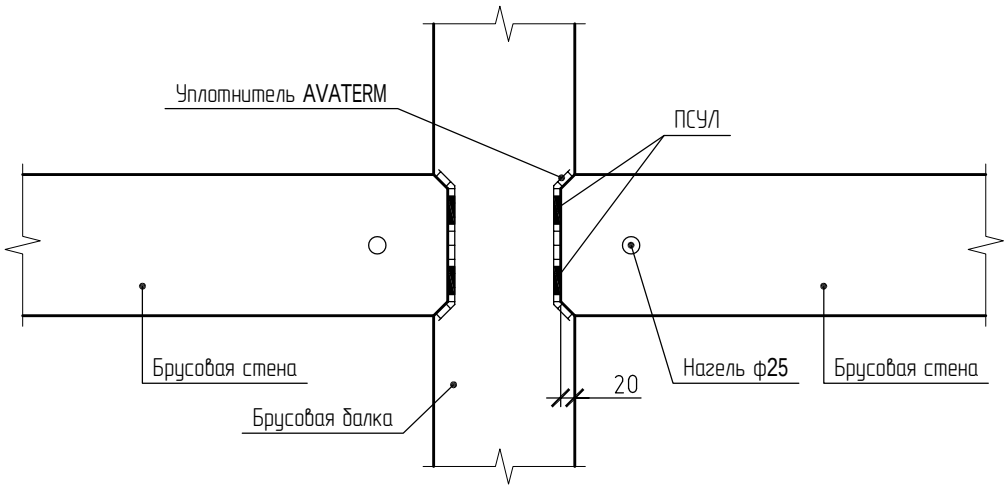


					Узел Бд	Лист
Изм.	Лист	№ докум.	Подп.	Дата		

Формат А4

Стягивание брусовых фронтонов глухарями

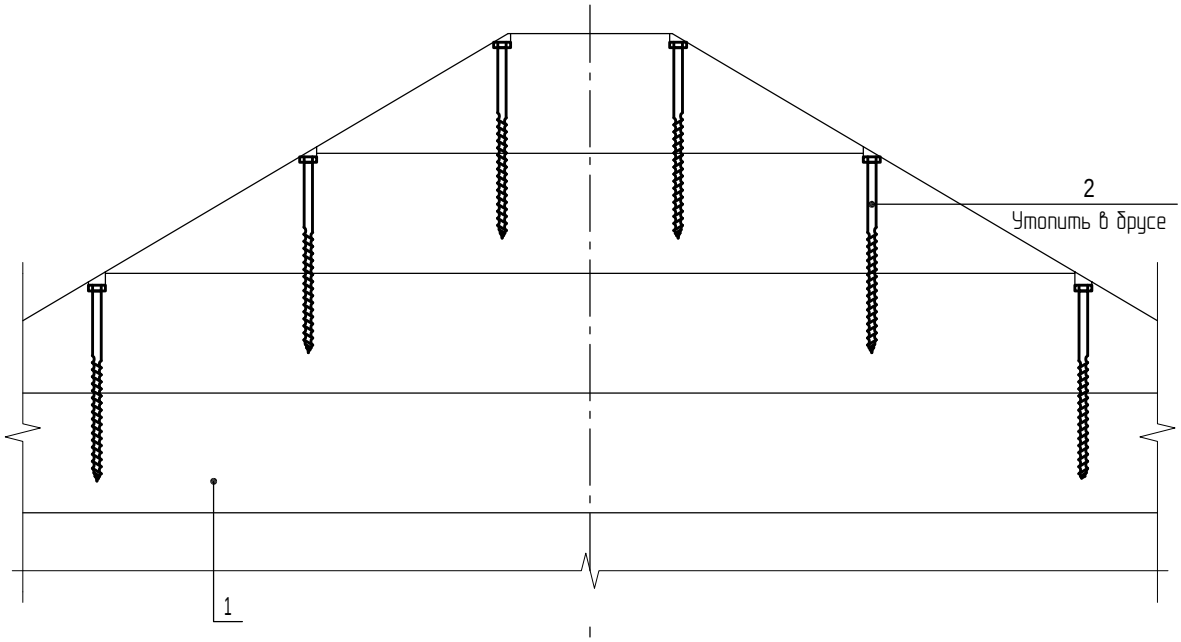

Устройство нагелей в брусовой стене
(данный узел используется по умолчанию кроме мест указанных особо)

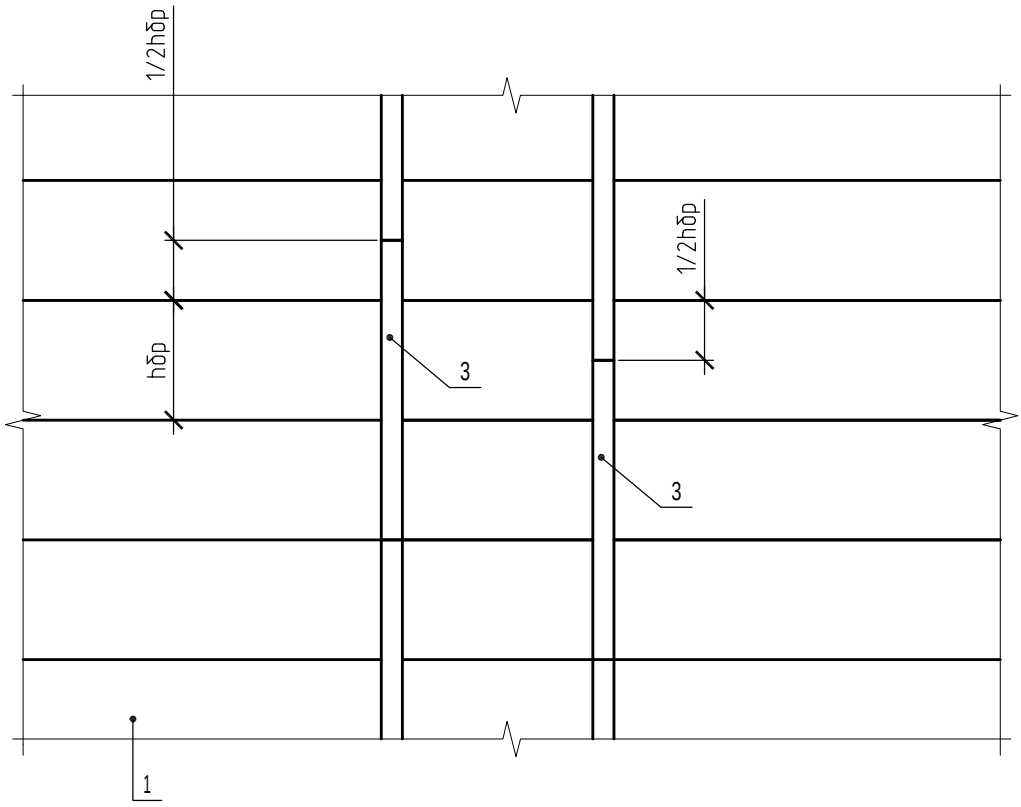


Обозн-е	Наименование	Обозн-е	Наименование
1	Брусовая стена	3	Нагель деревянный
2	Глухарь М12х300 с шайбой, при hбр>230мм		
	использовать глухарь М8х400		


Изм.	Лист	№ докум.	Подп.	Дата	Стягивание фронтонов, устройство нагелей	Лист

Формат А4

Снятие нижних пазов с видимой части бруса

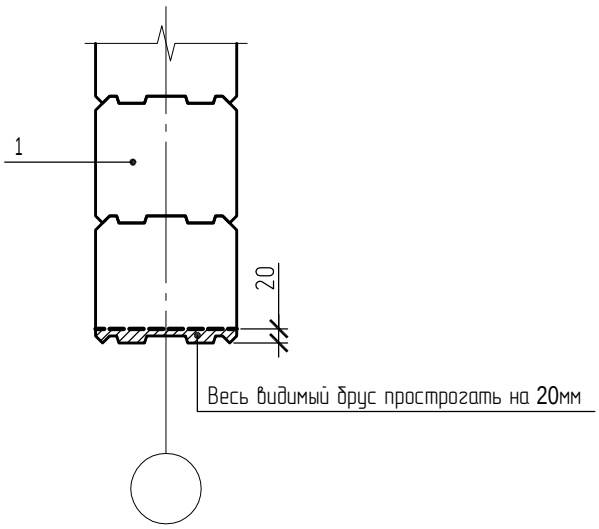

Подрезка бруса выше уровня чистого пола

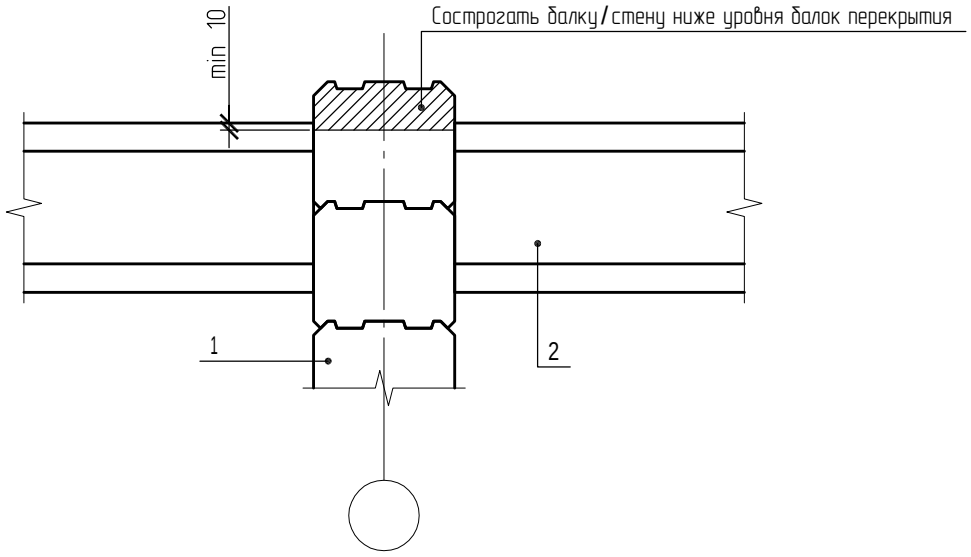


Пирог пола условно не показан

Обозн-е	Наименование	Обозн-е	Наименование
1	Клееный брус		
2	Двутавровая балка		

Изм.	Лист	№ докум.	Подп.	Дата	Узлы финишной обработки бруса	Лист


Формат А4

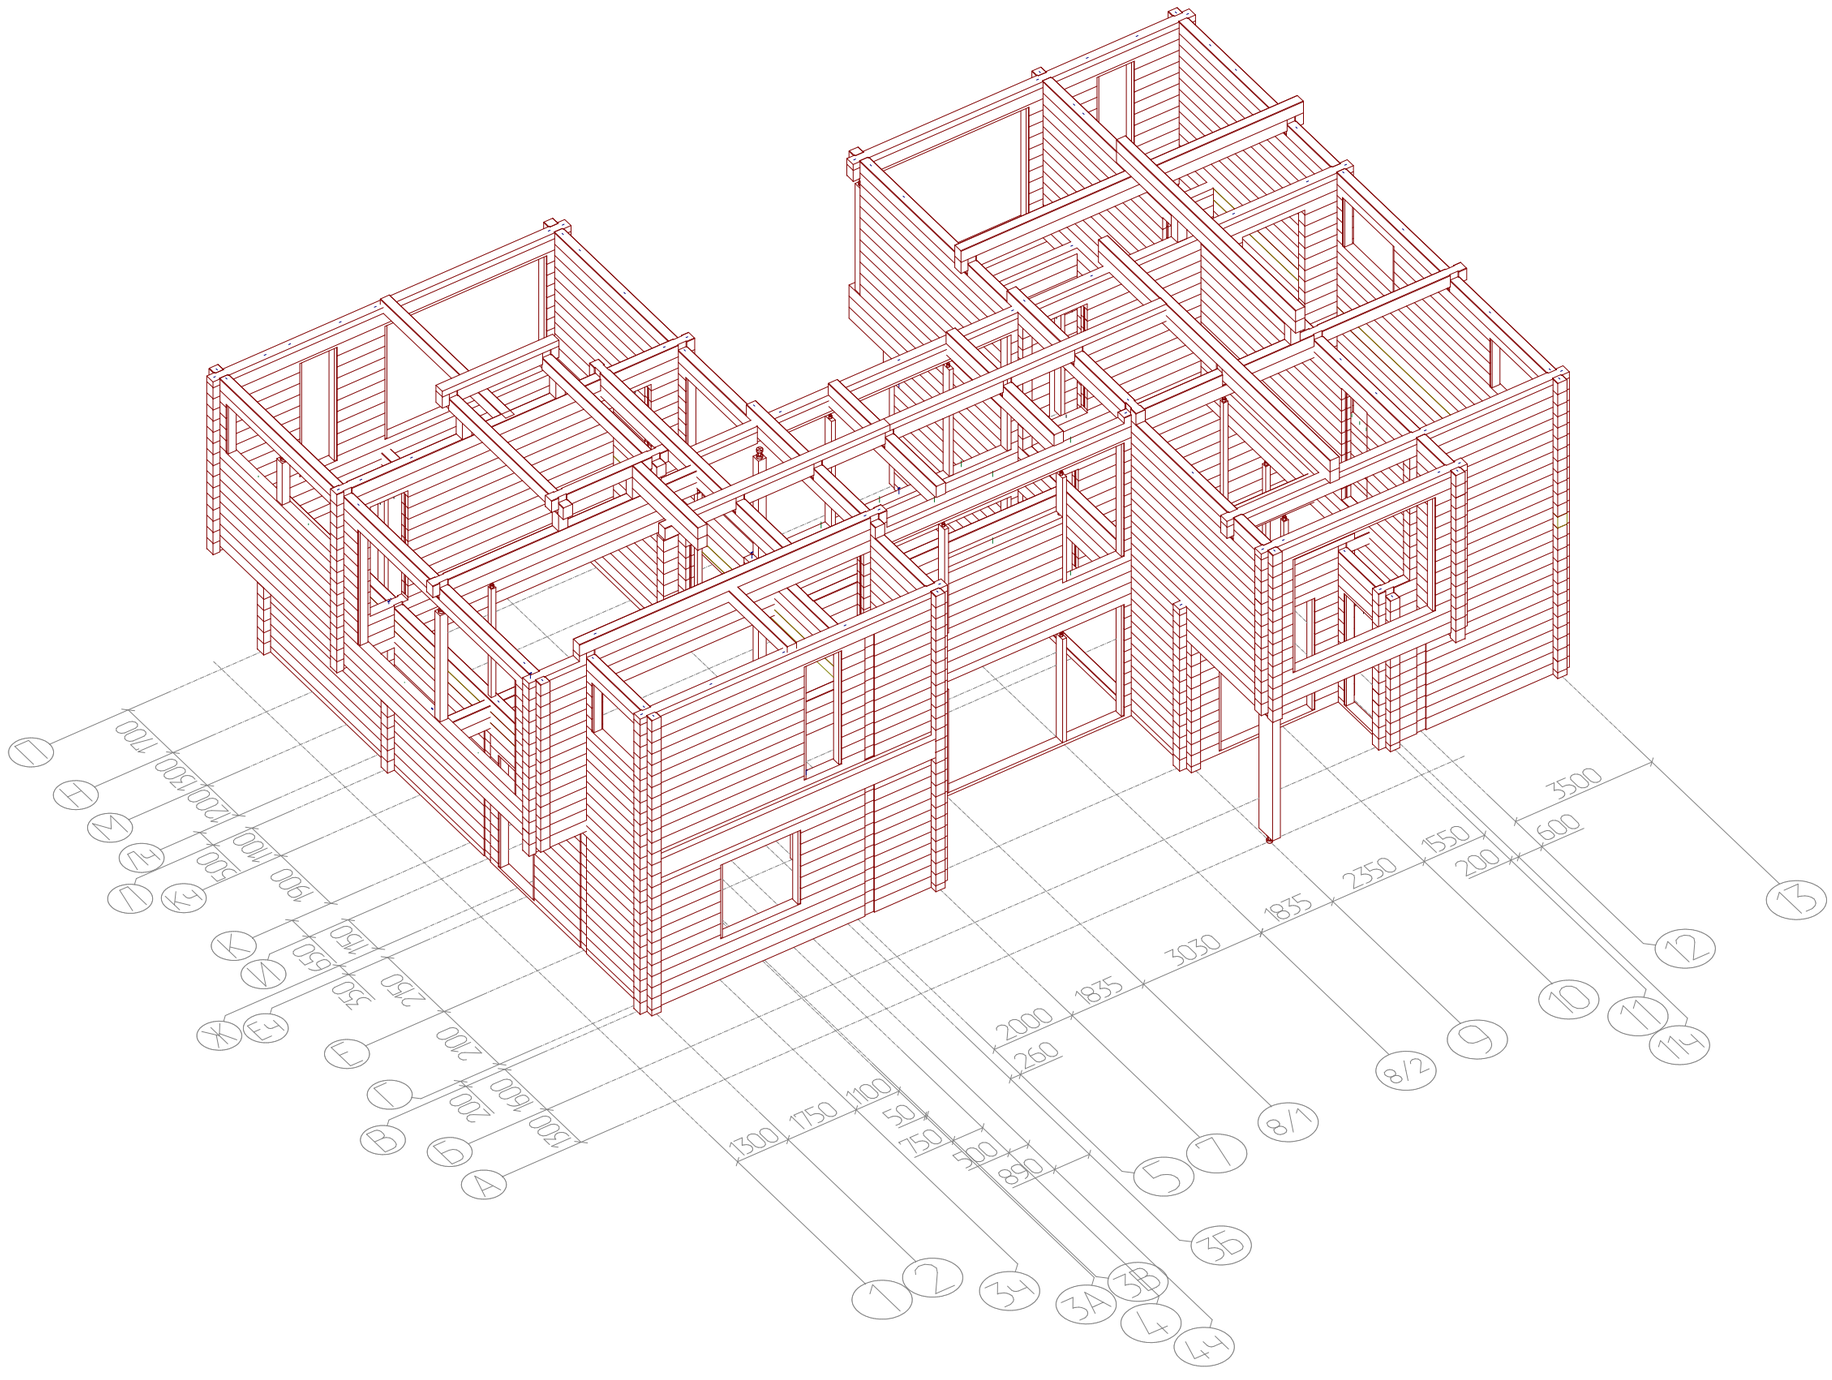

						- АС
Изм.	Кол. уч.	Лист	№ док.	Подпись	Дата	
Разработал		Москалюк А.				Берта Ромарио
Проверил		Баннов Е.				
Конструктор						
ГИП		Баннов Е.				Вид 1
Н.контроль						

Стадия	Лист	Листов
Р	2	


ООО "Строй Хауз"

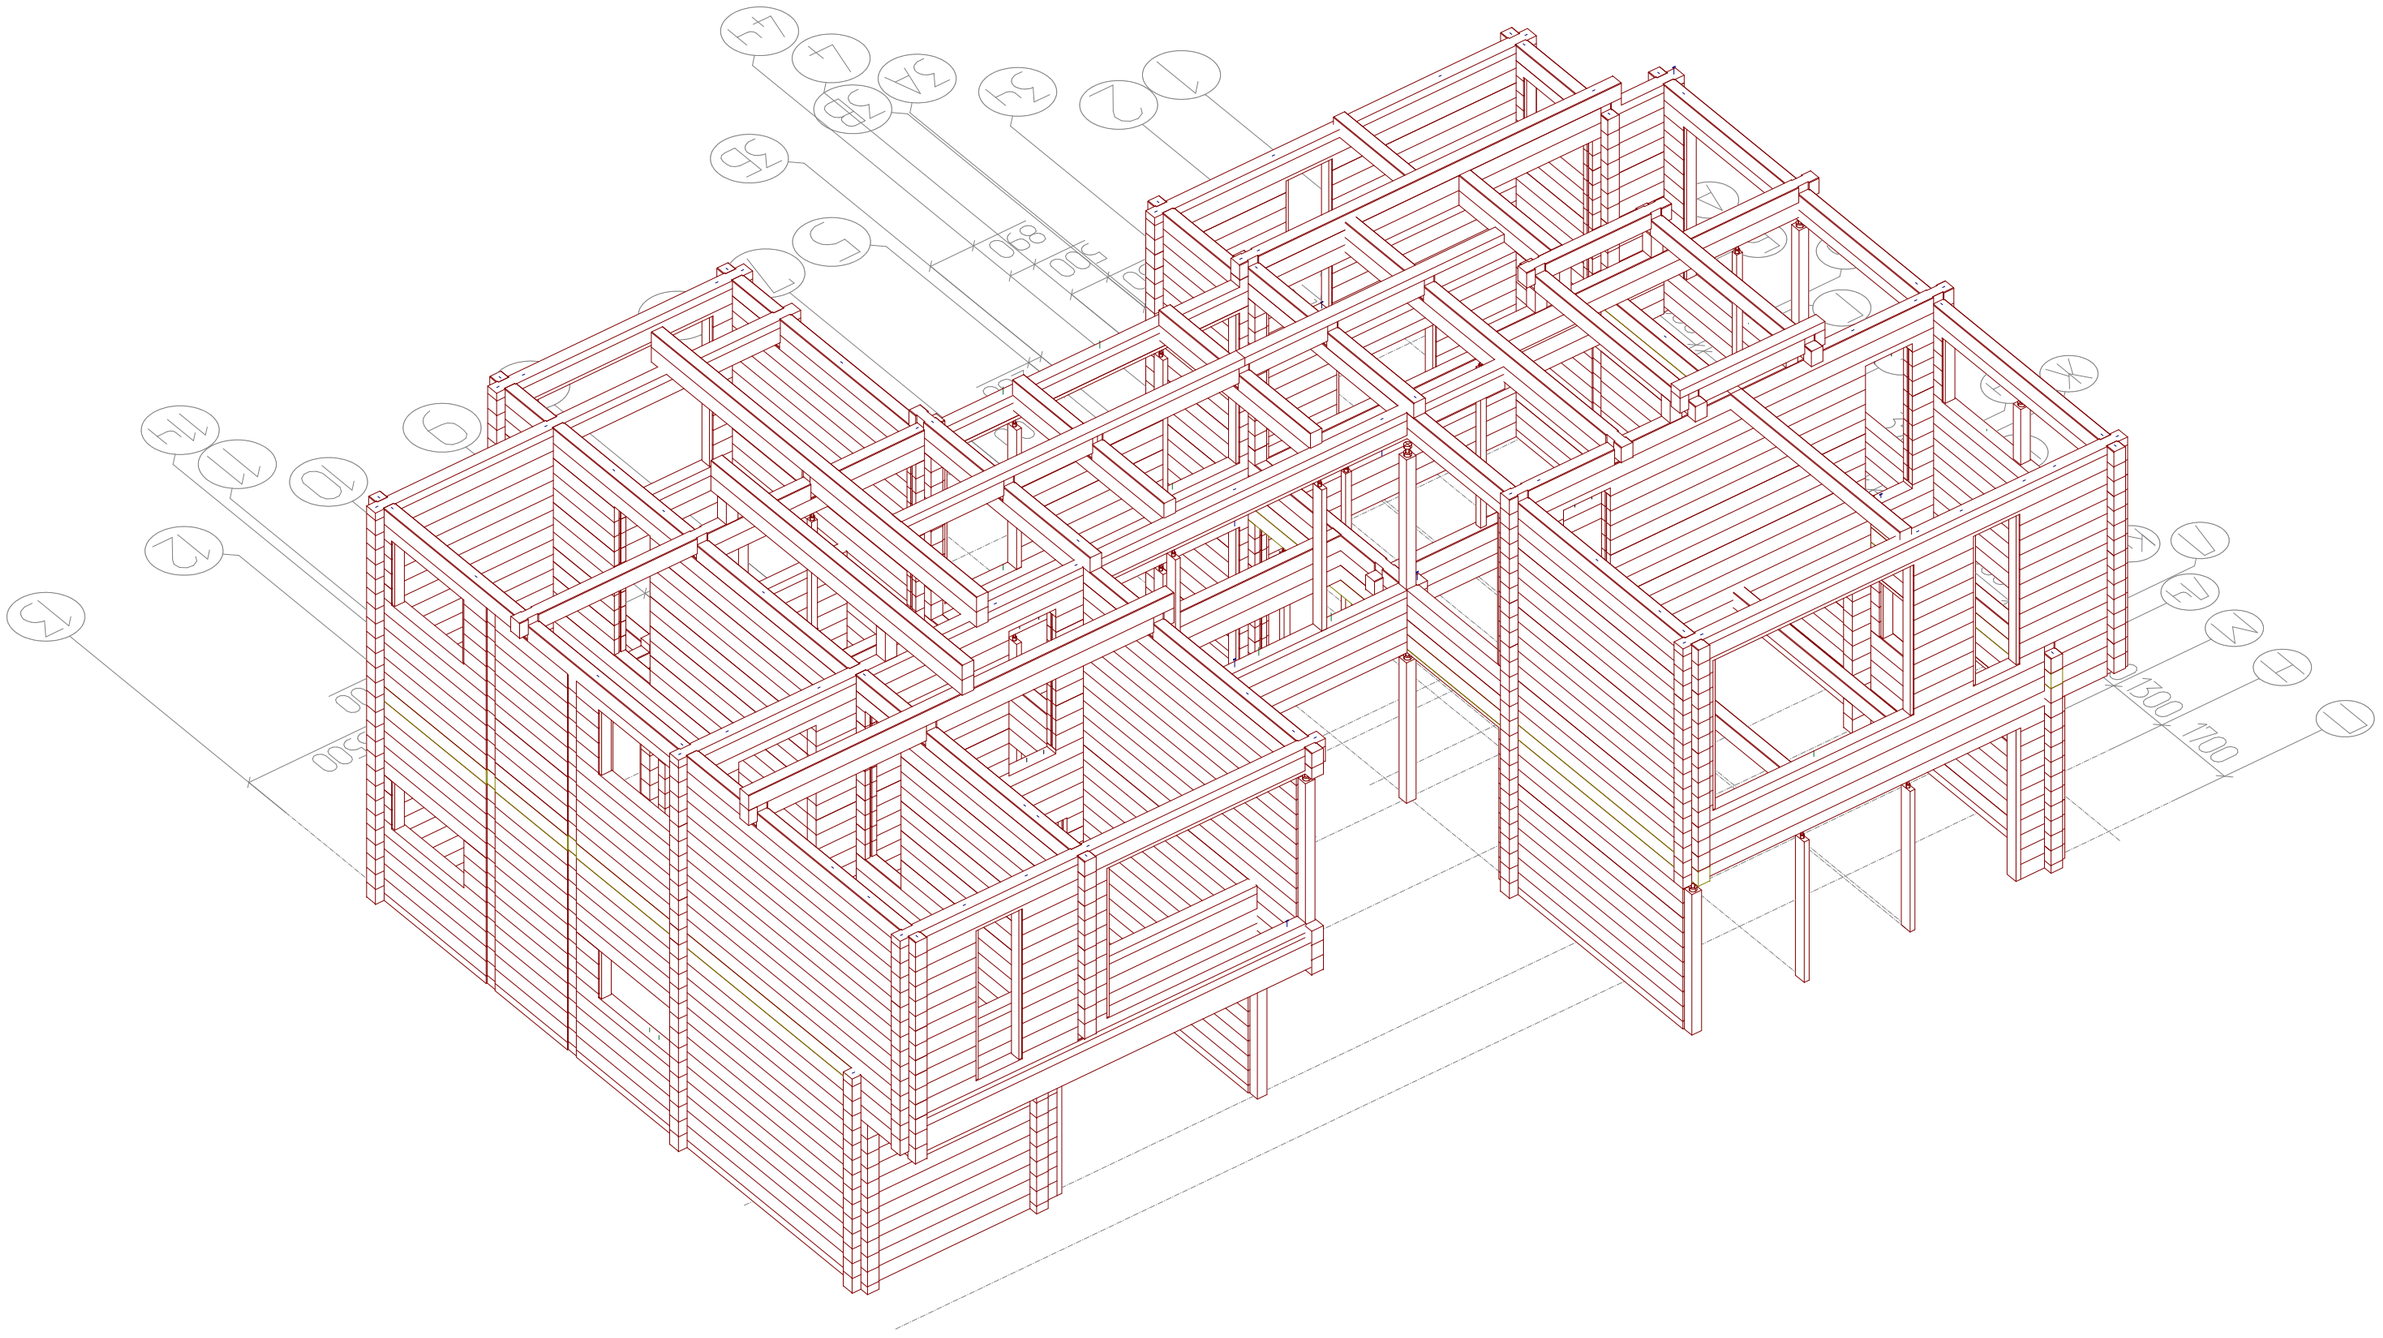

						- АС
Изм.	Кол. уч.	Лист	№ док.	Подпись	Дата	
Разработал		Москалюк А.				Берта Ромарио
Проверил		Баннов Е.				
Конструктор						
ГИП		Баннов Е.				Вид 2
Н.контроль						

Стадия	Лист	Листов
Р	3	


ООО "Строй Хауз"

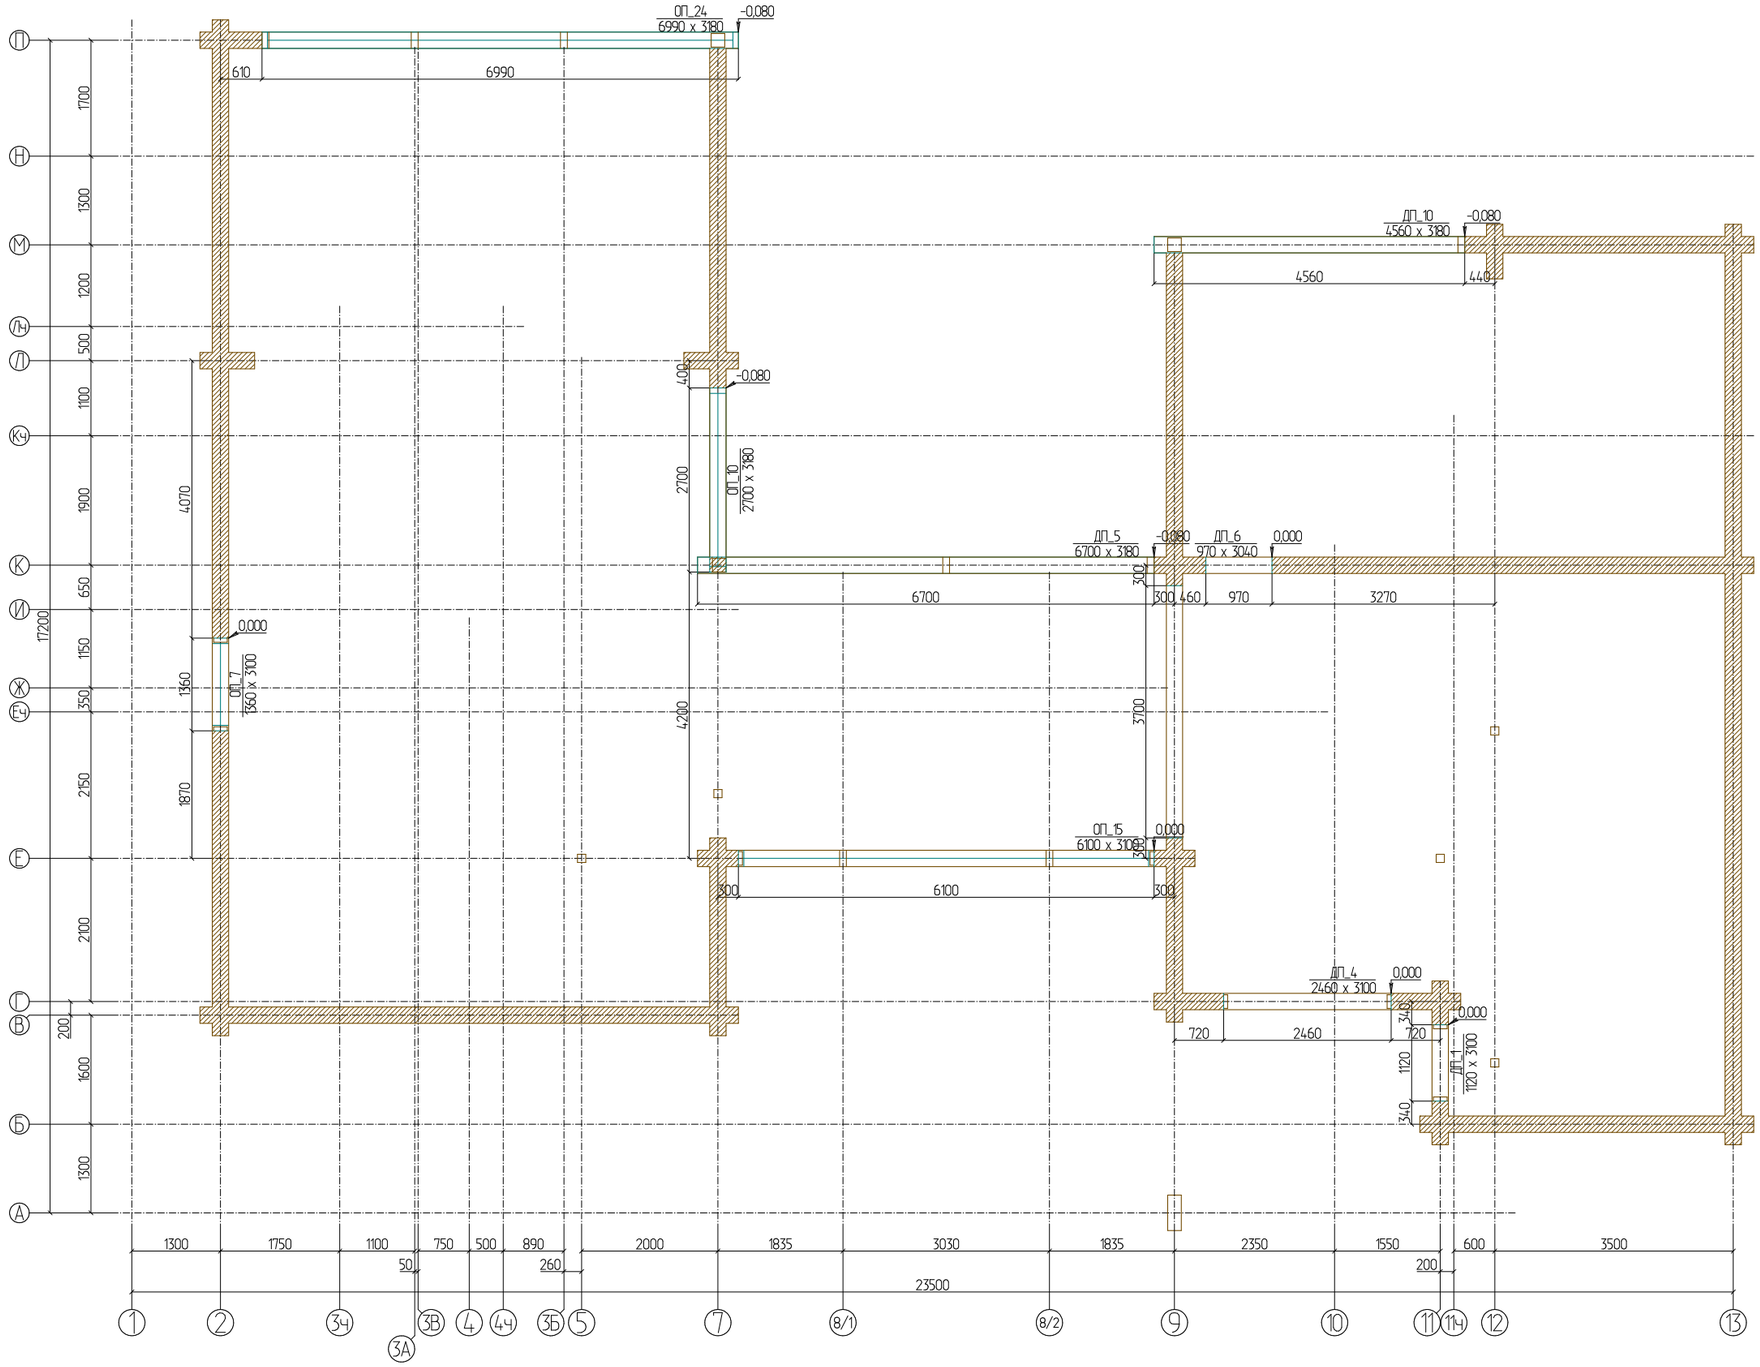

						- АР
Изм.	Кол. уч.	Лист	№ док.	Подпись	Дата	
Разработал		Москалюк А.				Берта Ромарио
Проверил		Баннов Е.				
Конструктор						
ГИП		Баннов Е.				Планы этажей 0,000
Н.контроль						

Стадия	Лист	Листов
Р	4	

ООО "Строй Хауз"

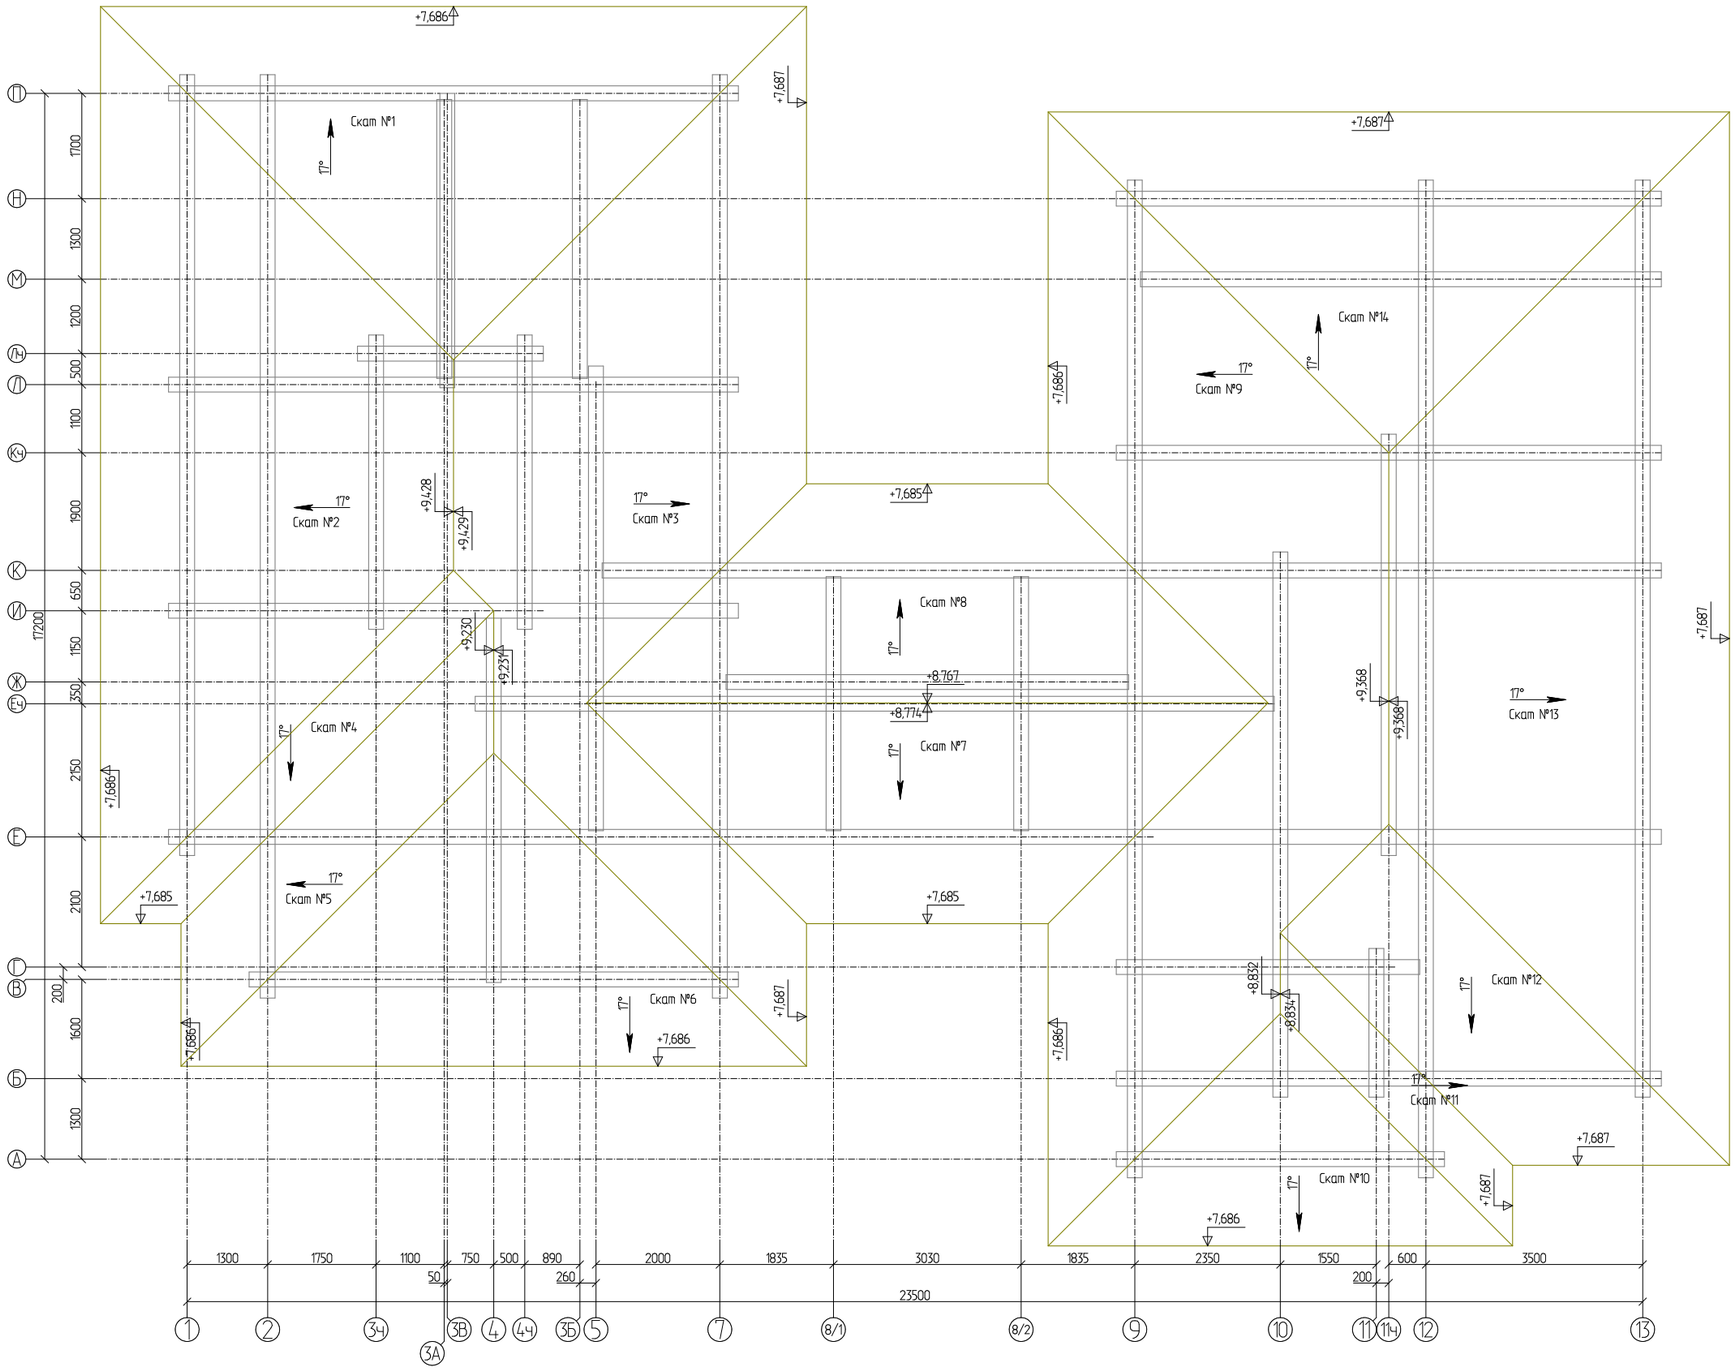


						- АР
Изм.	Кол. уч.	Лист	№ док.	Подпись	Дата	
Разработал		Москалюк А.				Берта Ромарио
Проверил		Баннов Е.				
Конструктор						
ГИП		Баннов Е.				План кровли
Н.контроль						

Стадия	Лист	Листов
Р	5	

ООО "Строй Хауз"

Развертка по стене (оси) 1

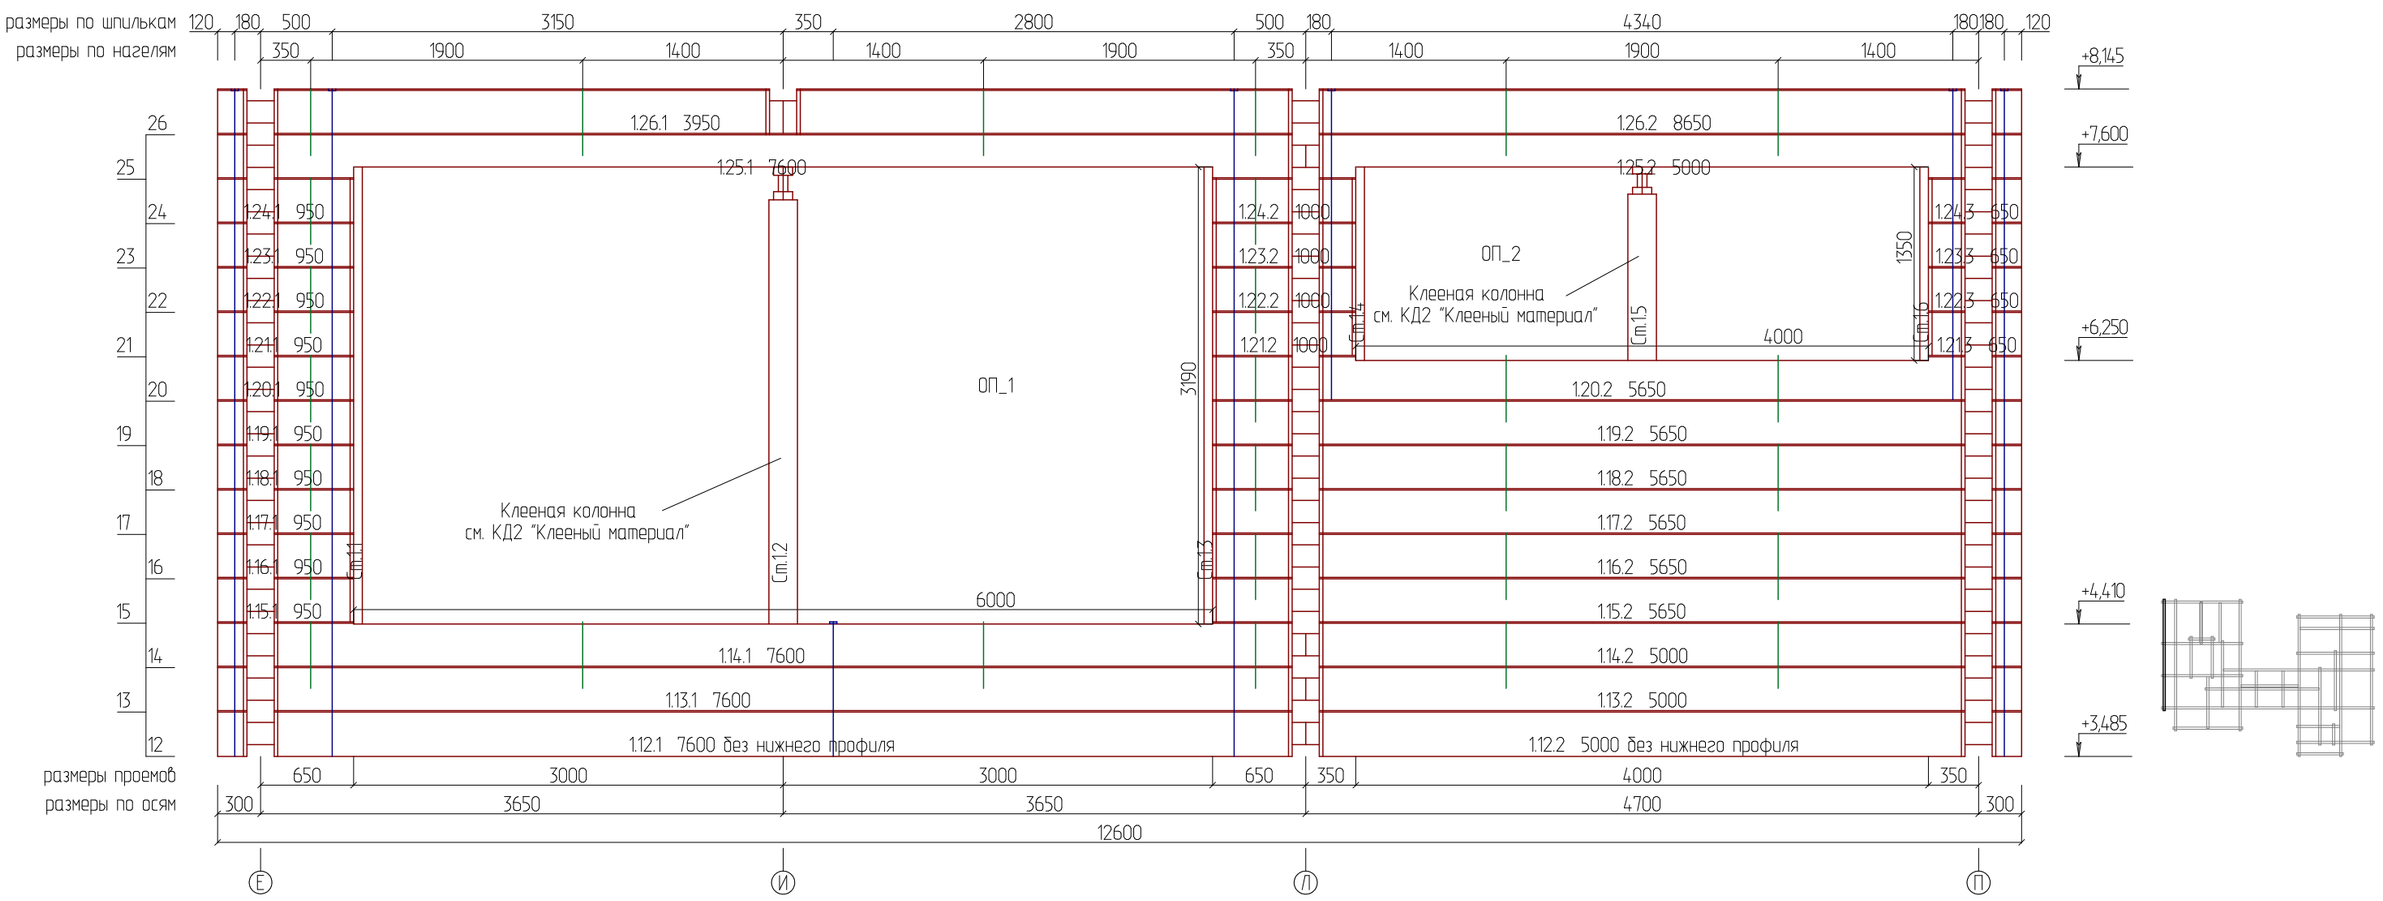


						- АС
Изм.	Кол. уч.	Лист	№ док.	Подпись	Дата	
Разработал		Москалюк А.				Берта Ромарио
Проверил		Баннов Е.				
Конструктор						
ГИП		Баннов Е.				Развертка по стене (оси) 1
Н.контроль						

Стадия	Лист	Листов
Р	6	

ООО "Строй Хауз"

Развертка по стене (оси) 2

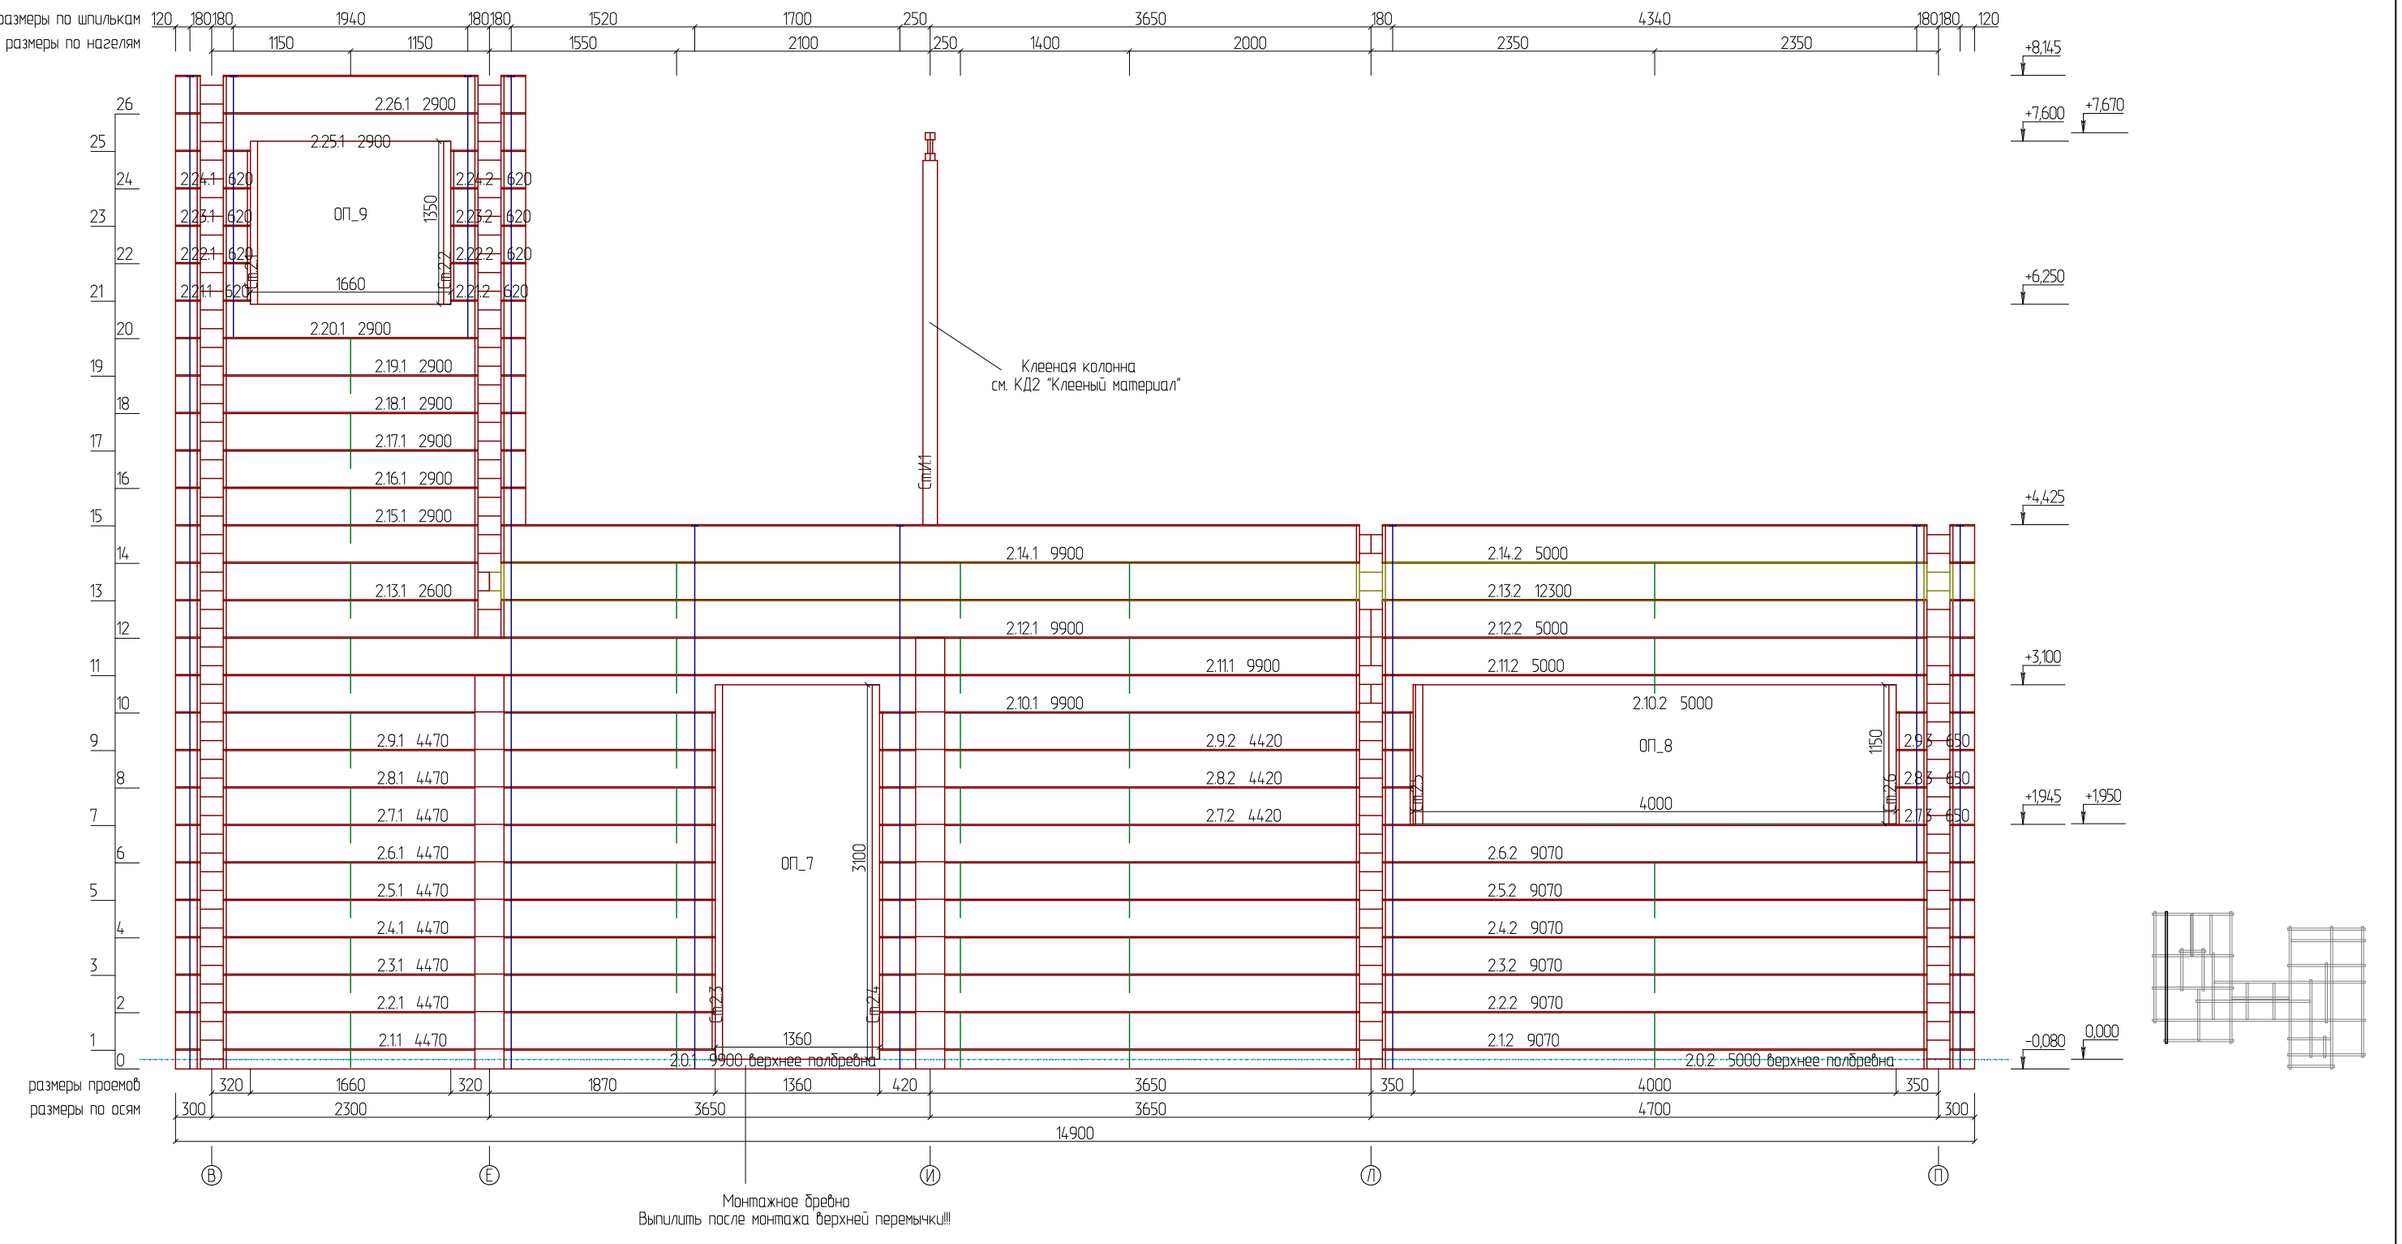



						- АС
Изм.	Кол. уч.	Лист	№ док.	Подпись	Дата	
Разработал		Москалюк А.				Берта Ромарио
Проверил		Баннов Е.				
Конструктор						
ГИП		Баннов Е.				
Н.контроль						Развертка по стене (оси) 2

Стадия	Лист	Листов
Р	7	

ООО "Строй Хауз"

Развертка по стене (оси) 3А

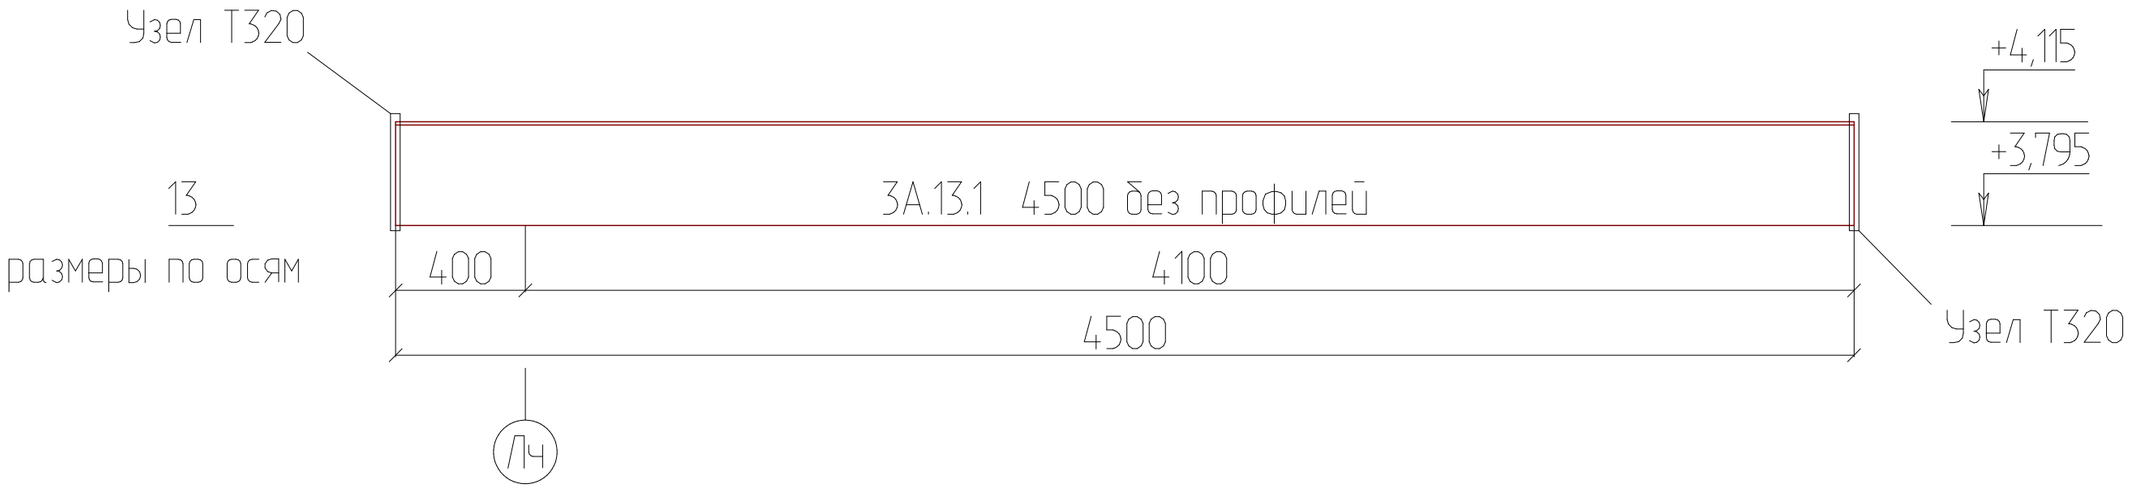

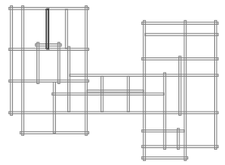


						- АС
Изм.	Кол. уч.	Лист	№ док.	Подпись	Дата	
Разработал		Москалюк А.				Берта Ромарио
Проверил		Баннов Е.				
Конструктор						
ГИП		Баннов Е.				Развертка по стене (оси) 3А
Н.контроль						

Стадия	Лист	Листов
Р	8	

ООО "Строй Хауз"

Развертка по стене (оси) 3Б

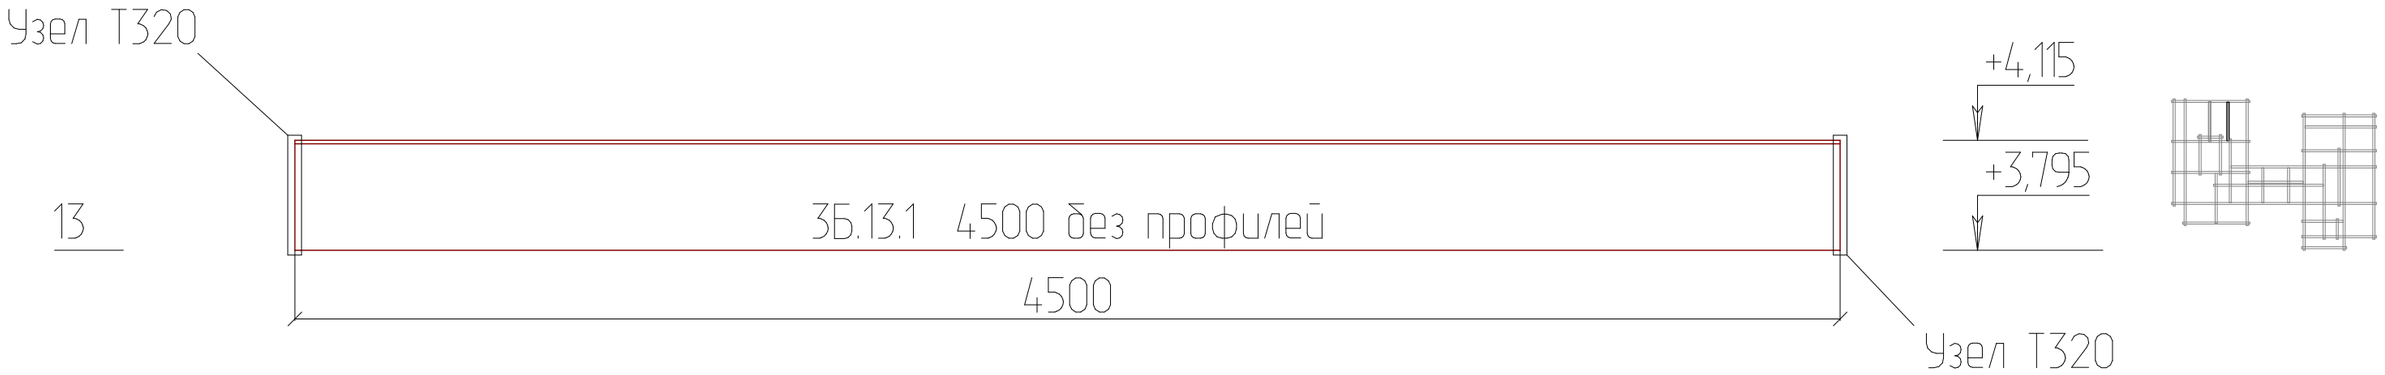


						- АС
Изм.	Кол. уч.	Лист	№ док.	Подпись	Дата	
Разработал		Москалюк А.				Берта Ромарио
Проверил		Баннов Е.				
Конструктор						
ГИП		Баннов Е.				Развертка по стене (оси) 3Б
Н.контроль						

Стадия	Лист	Листов
Р	9	

ООО "Строй Хауз"

Развертка по стене (оси) 3В

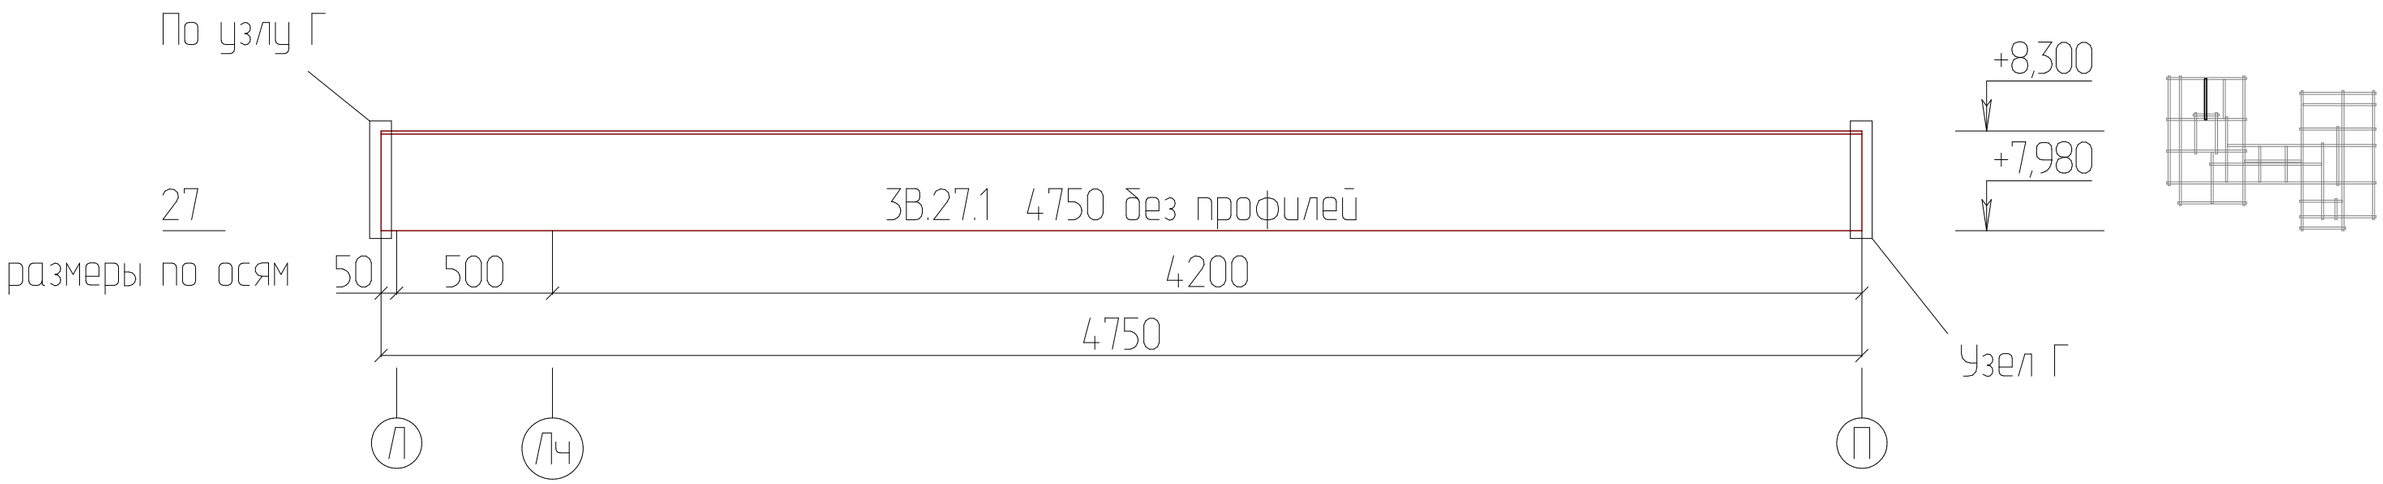


						- АС
Изм.	Кол. уч.	Лист	№ док.	Подпись	Дата	
Разработал		Москалюк А.				Берта Ромарио
Проверил		Баннов Е.				
Конструктор						
ГИП		Баннов Е.				Развертка по стене (оси) 3В
Н.контроль						

Стадия	Лист	Листов
Р	10	

ООО "Строй Хауз"

Развертка по стене (оси) 3ч

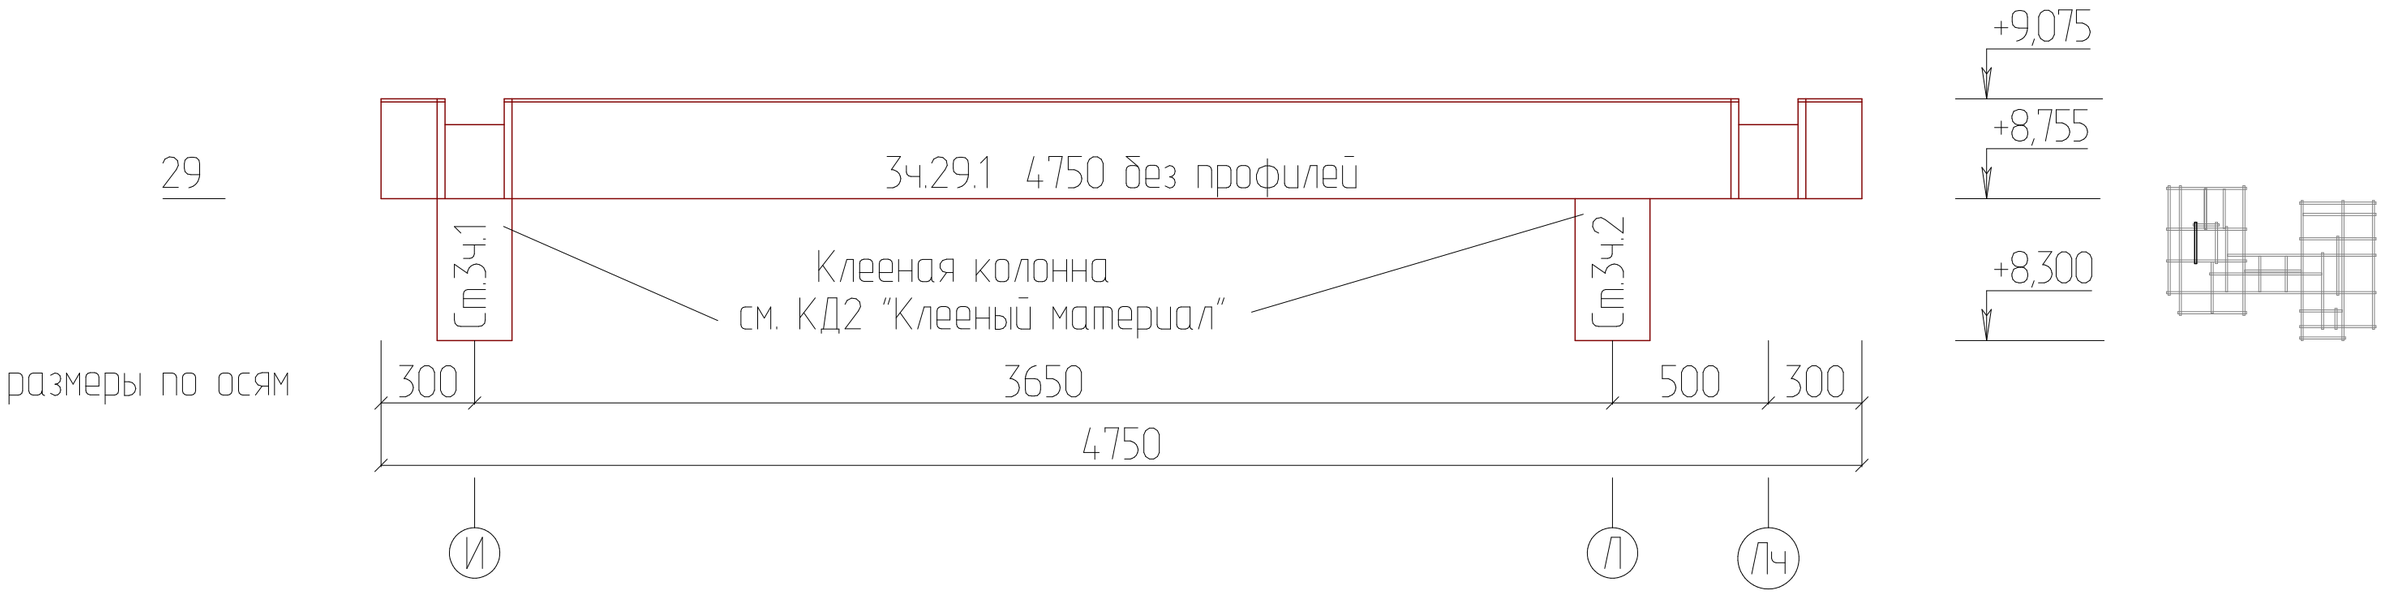


						- АС
Изм.	Кол. уч.	Лист	№ док.	Подпись	Дата	
Разработал		Москалюк А.				Берта Ромарио
Проверил		Баннов Е.				
Конструктор						
ГИП		Баннов Е.				Развертка по стене (оси) 3ч
Н.контроль						

Стадия	Лист	Листов
Р	11	

ООО "Строй Хауз"

Развертка по стене (оси) 4

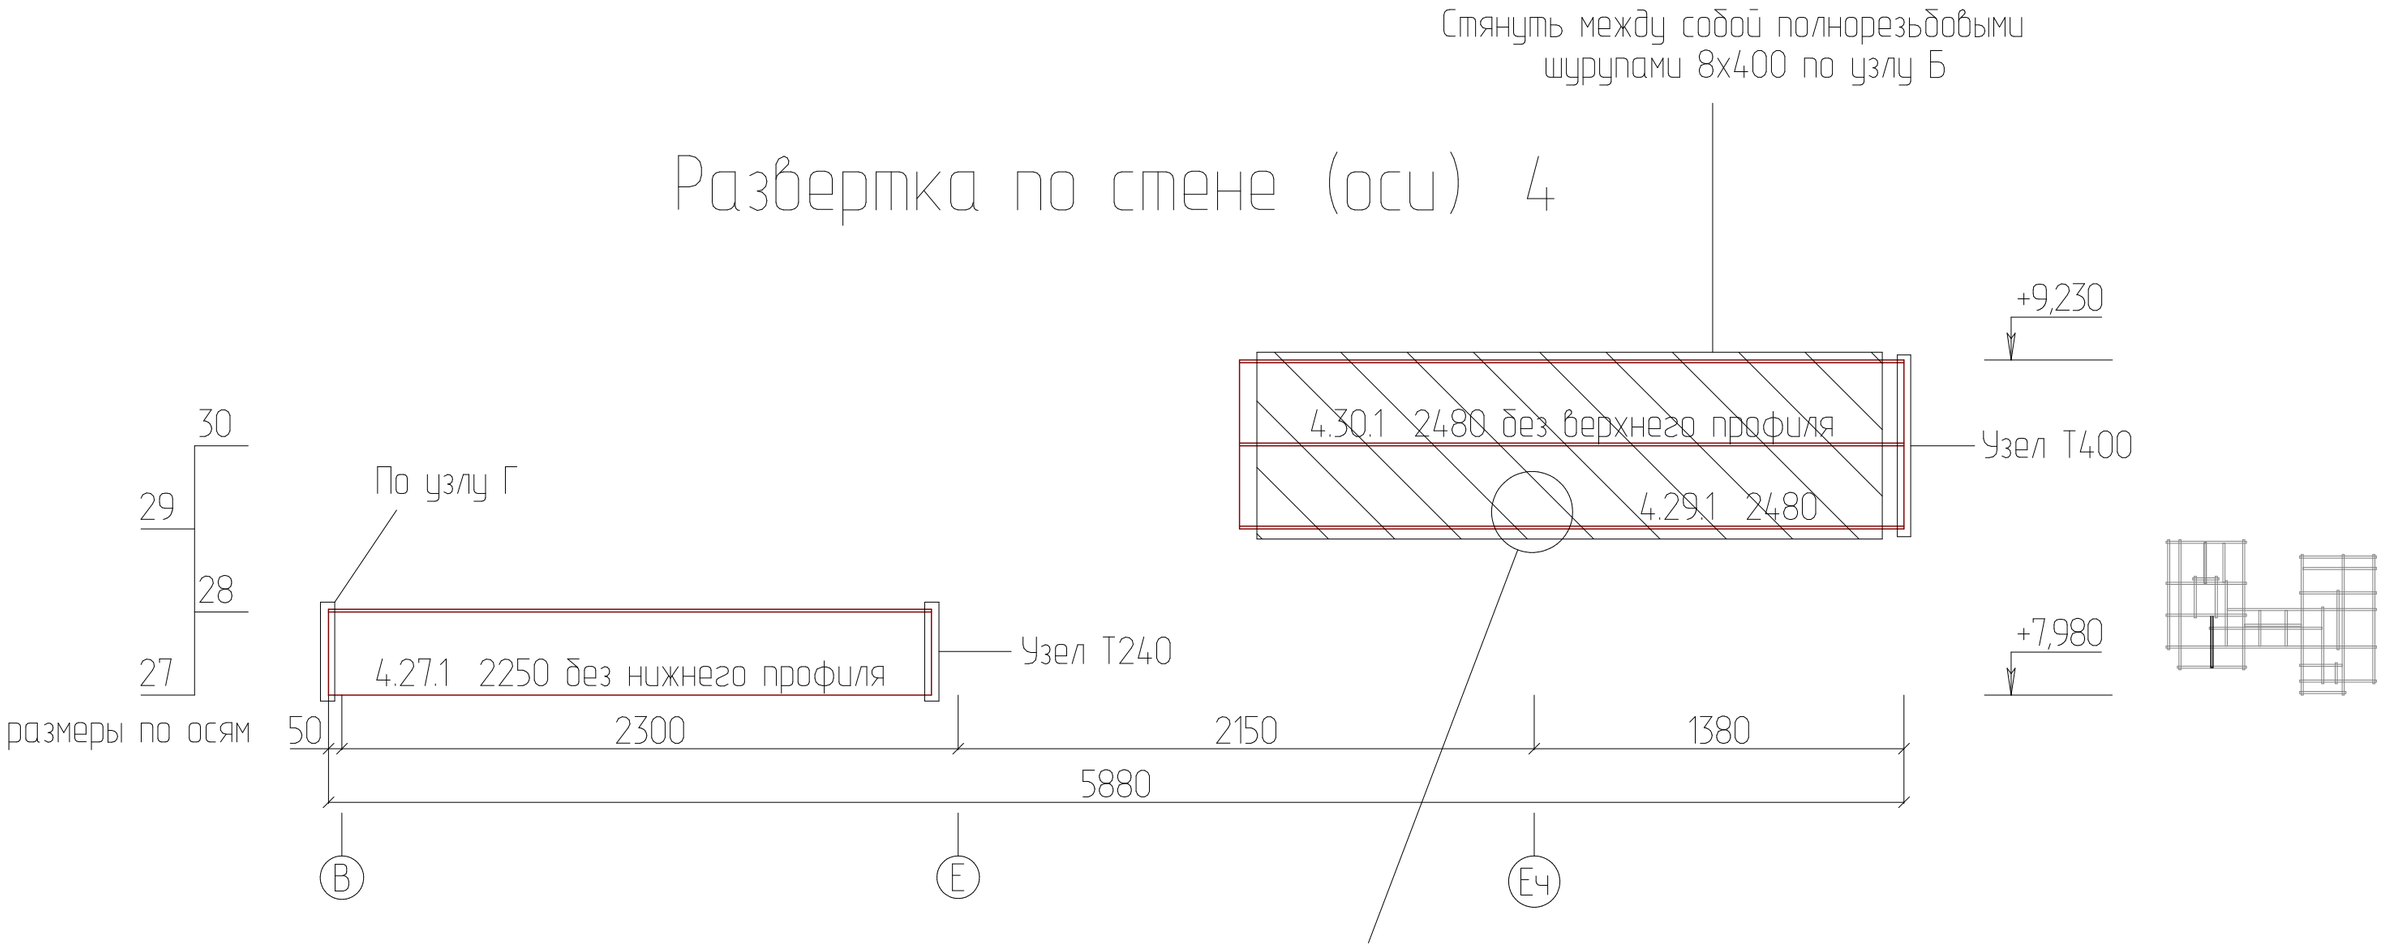


						- АС
Изм.	Кол. уч.	Лист	№ док.	Подпись	Дата	
Разработал		Москалюк А.				Берта Ромарио
Проверил		Баннов Е.				
Конструктор						
ГИП		Баннов Е.				Развертка по стене (оси) 4
Н.контроль						

Стадия	Лист	Листов
Р	12	

ООО "Строй Хауз"

Развертка по стене (оси) 4ч

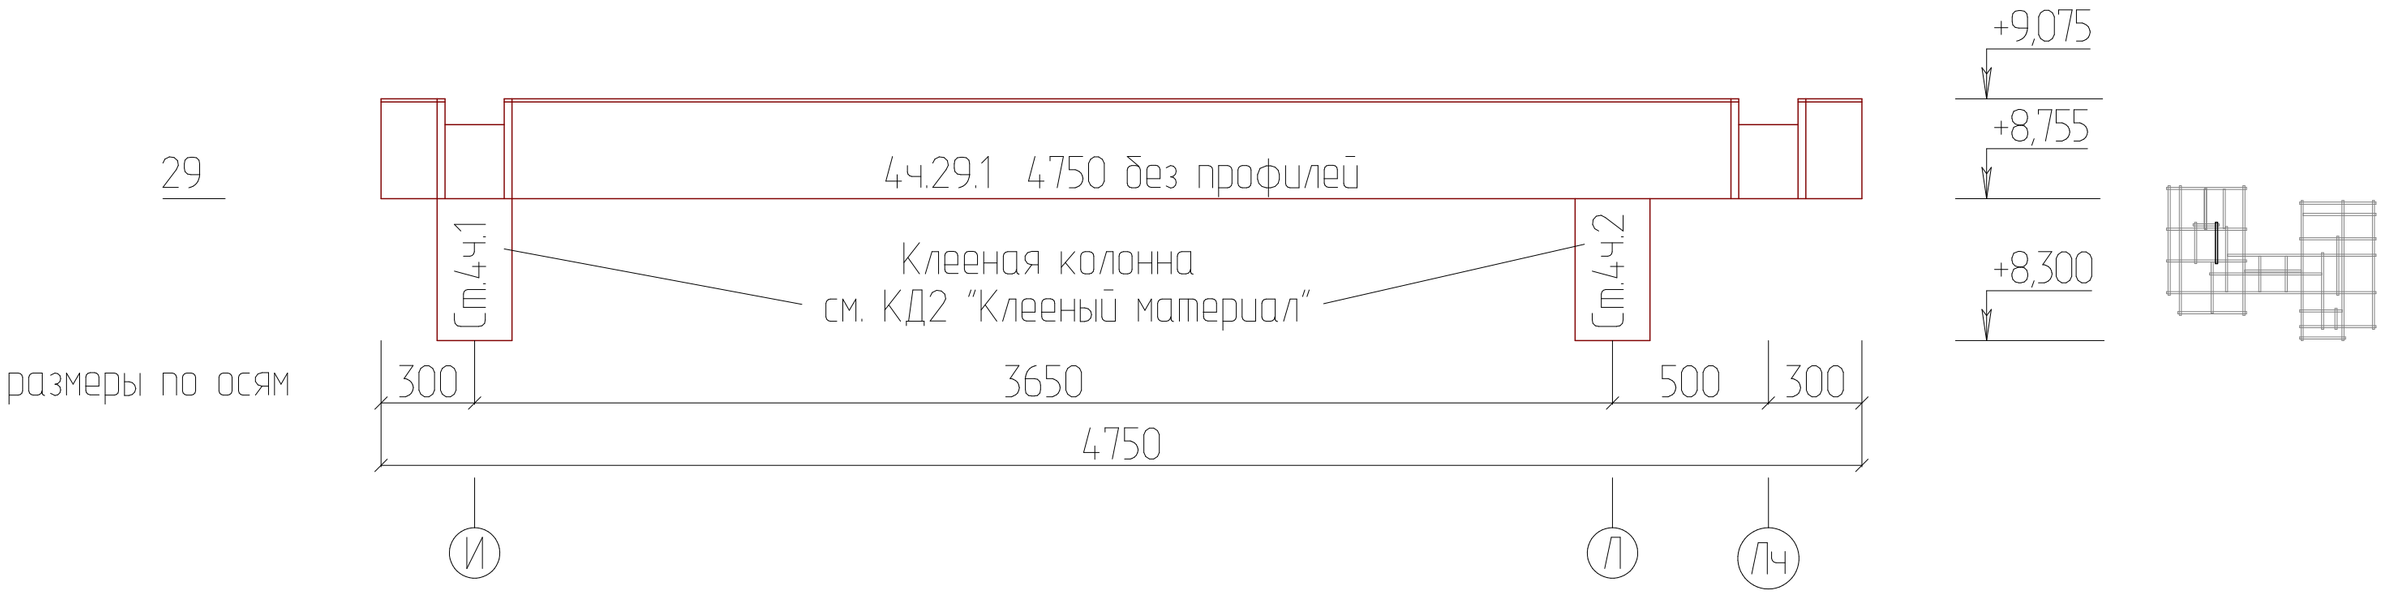


						- АС
Изм.	Кол. уч.	Лист	№ док.	Подпись	Дата	
Разработал		Москалюк А.				Берта Ромарио
Проверил		Баннов Е.				
Конструктор						
ГИП		Баннов Е.				Развертка по стене (оси) 4ч
Н.контроль						

Стадия	Лист	Листов
Р	13	


ООО "Строй Хауз"

Развертка по стене (оси) 5

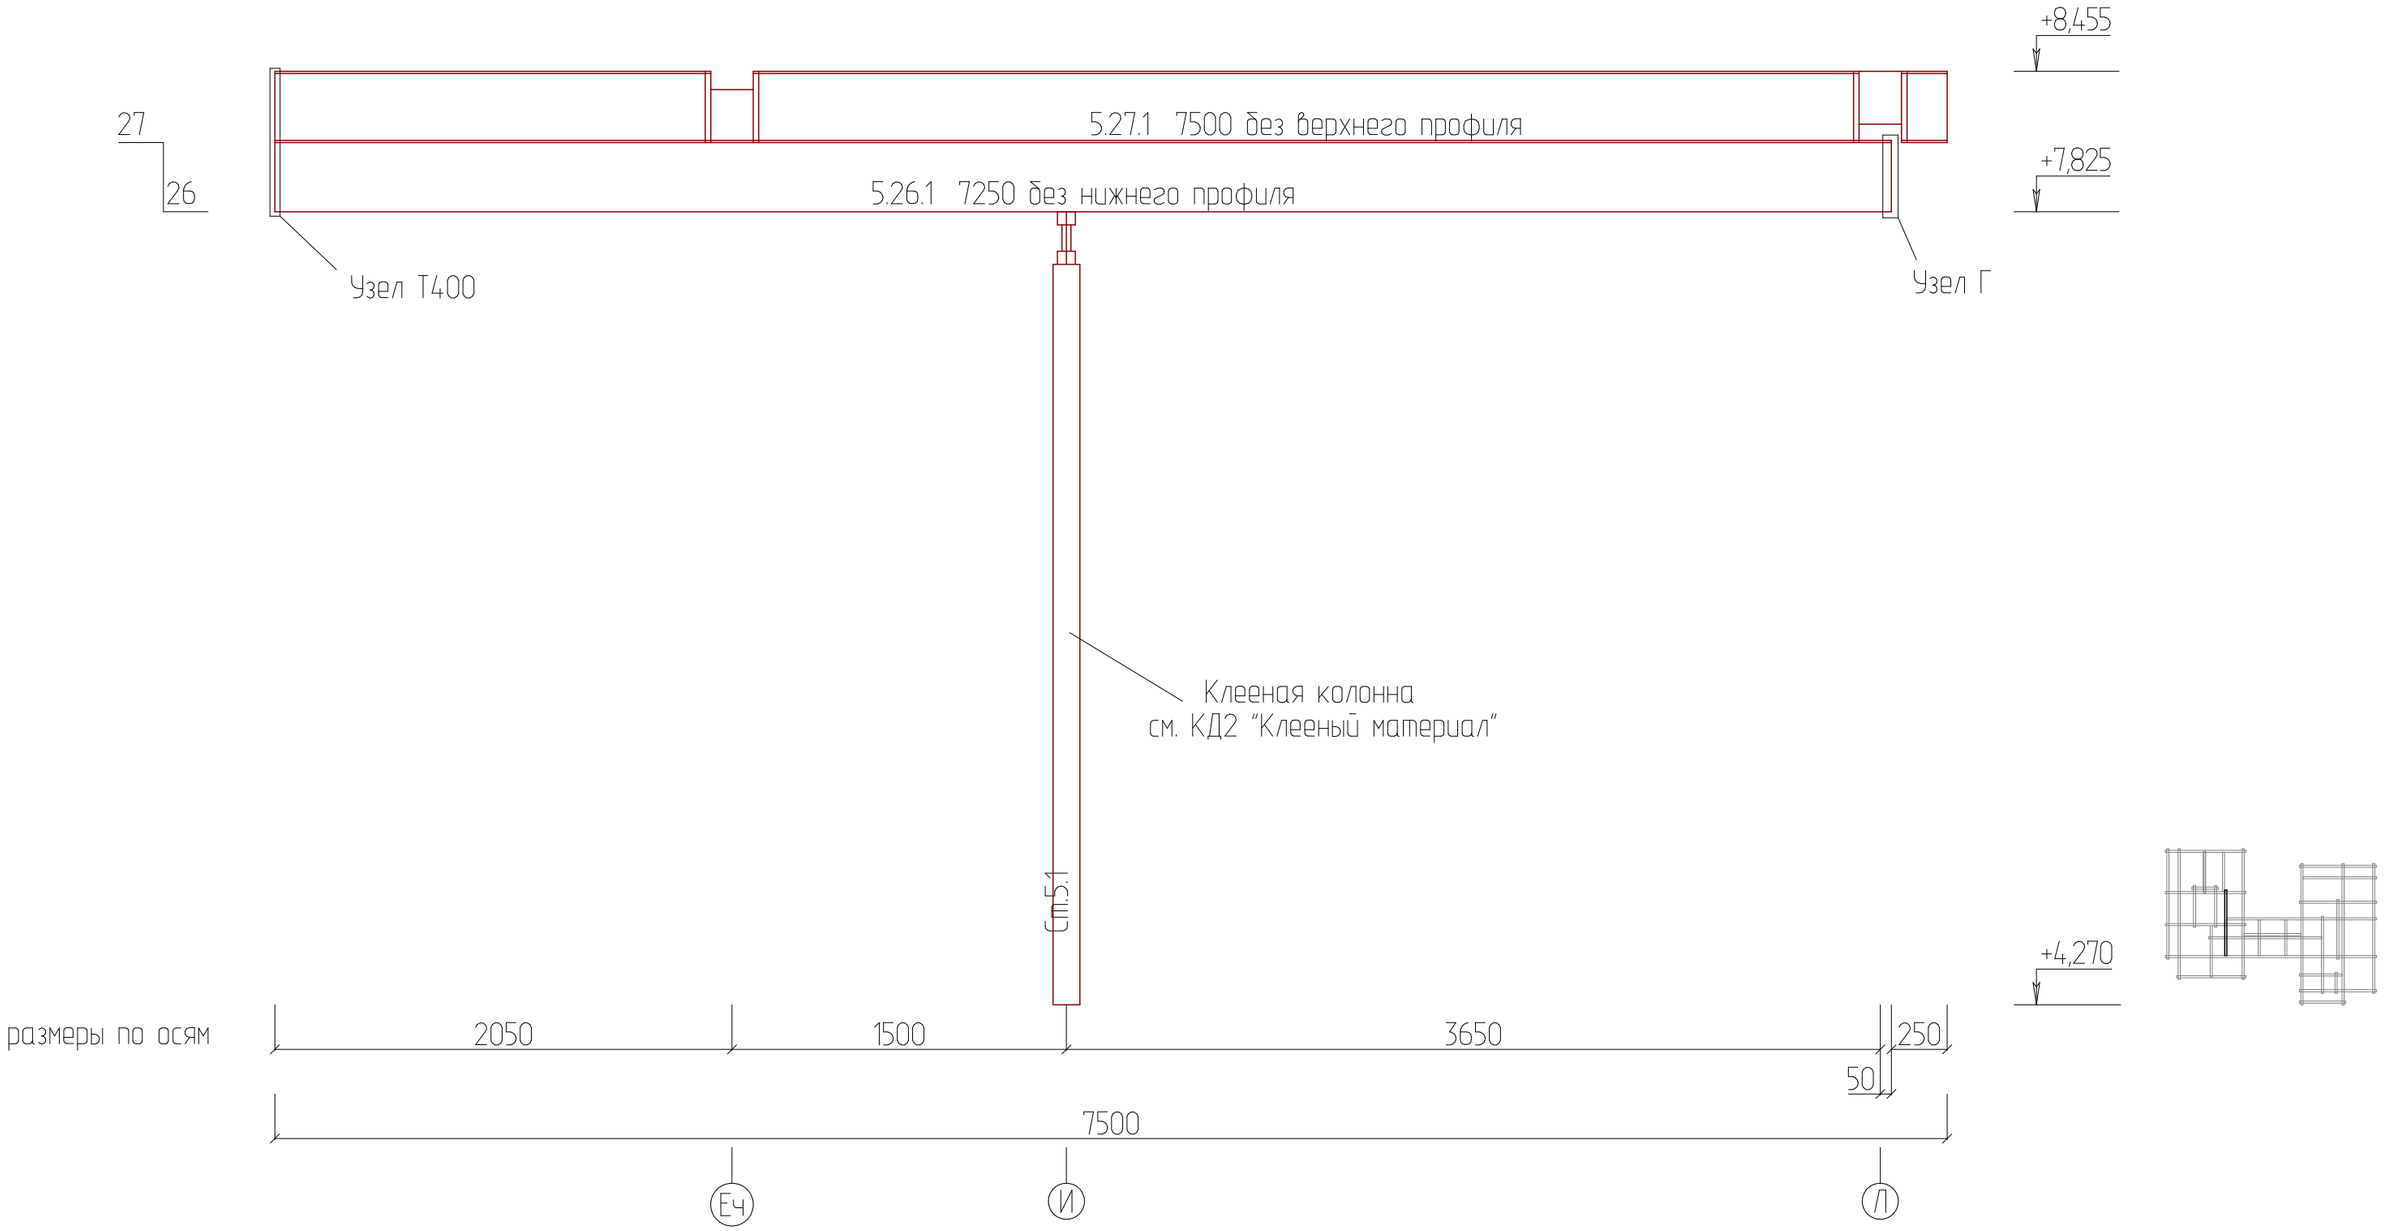


						- АС		
Изм.	Кол. уч.	Лист	№ док.	Подпись	Дата			
Разработал		Москалюк А.				Берта Ромарио	Стадия	Лист	Листов
Проверил		Баннов Е.					Р	14	
Конструктор									
ГИП		Баннов Е.				Развертка по стене (оси) 5	ООО "Строй Хауз"		
Н.контроль									

Развертка по стене (оси) 7

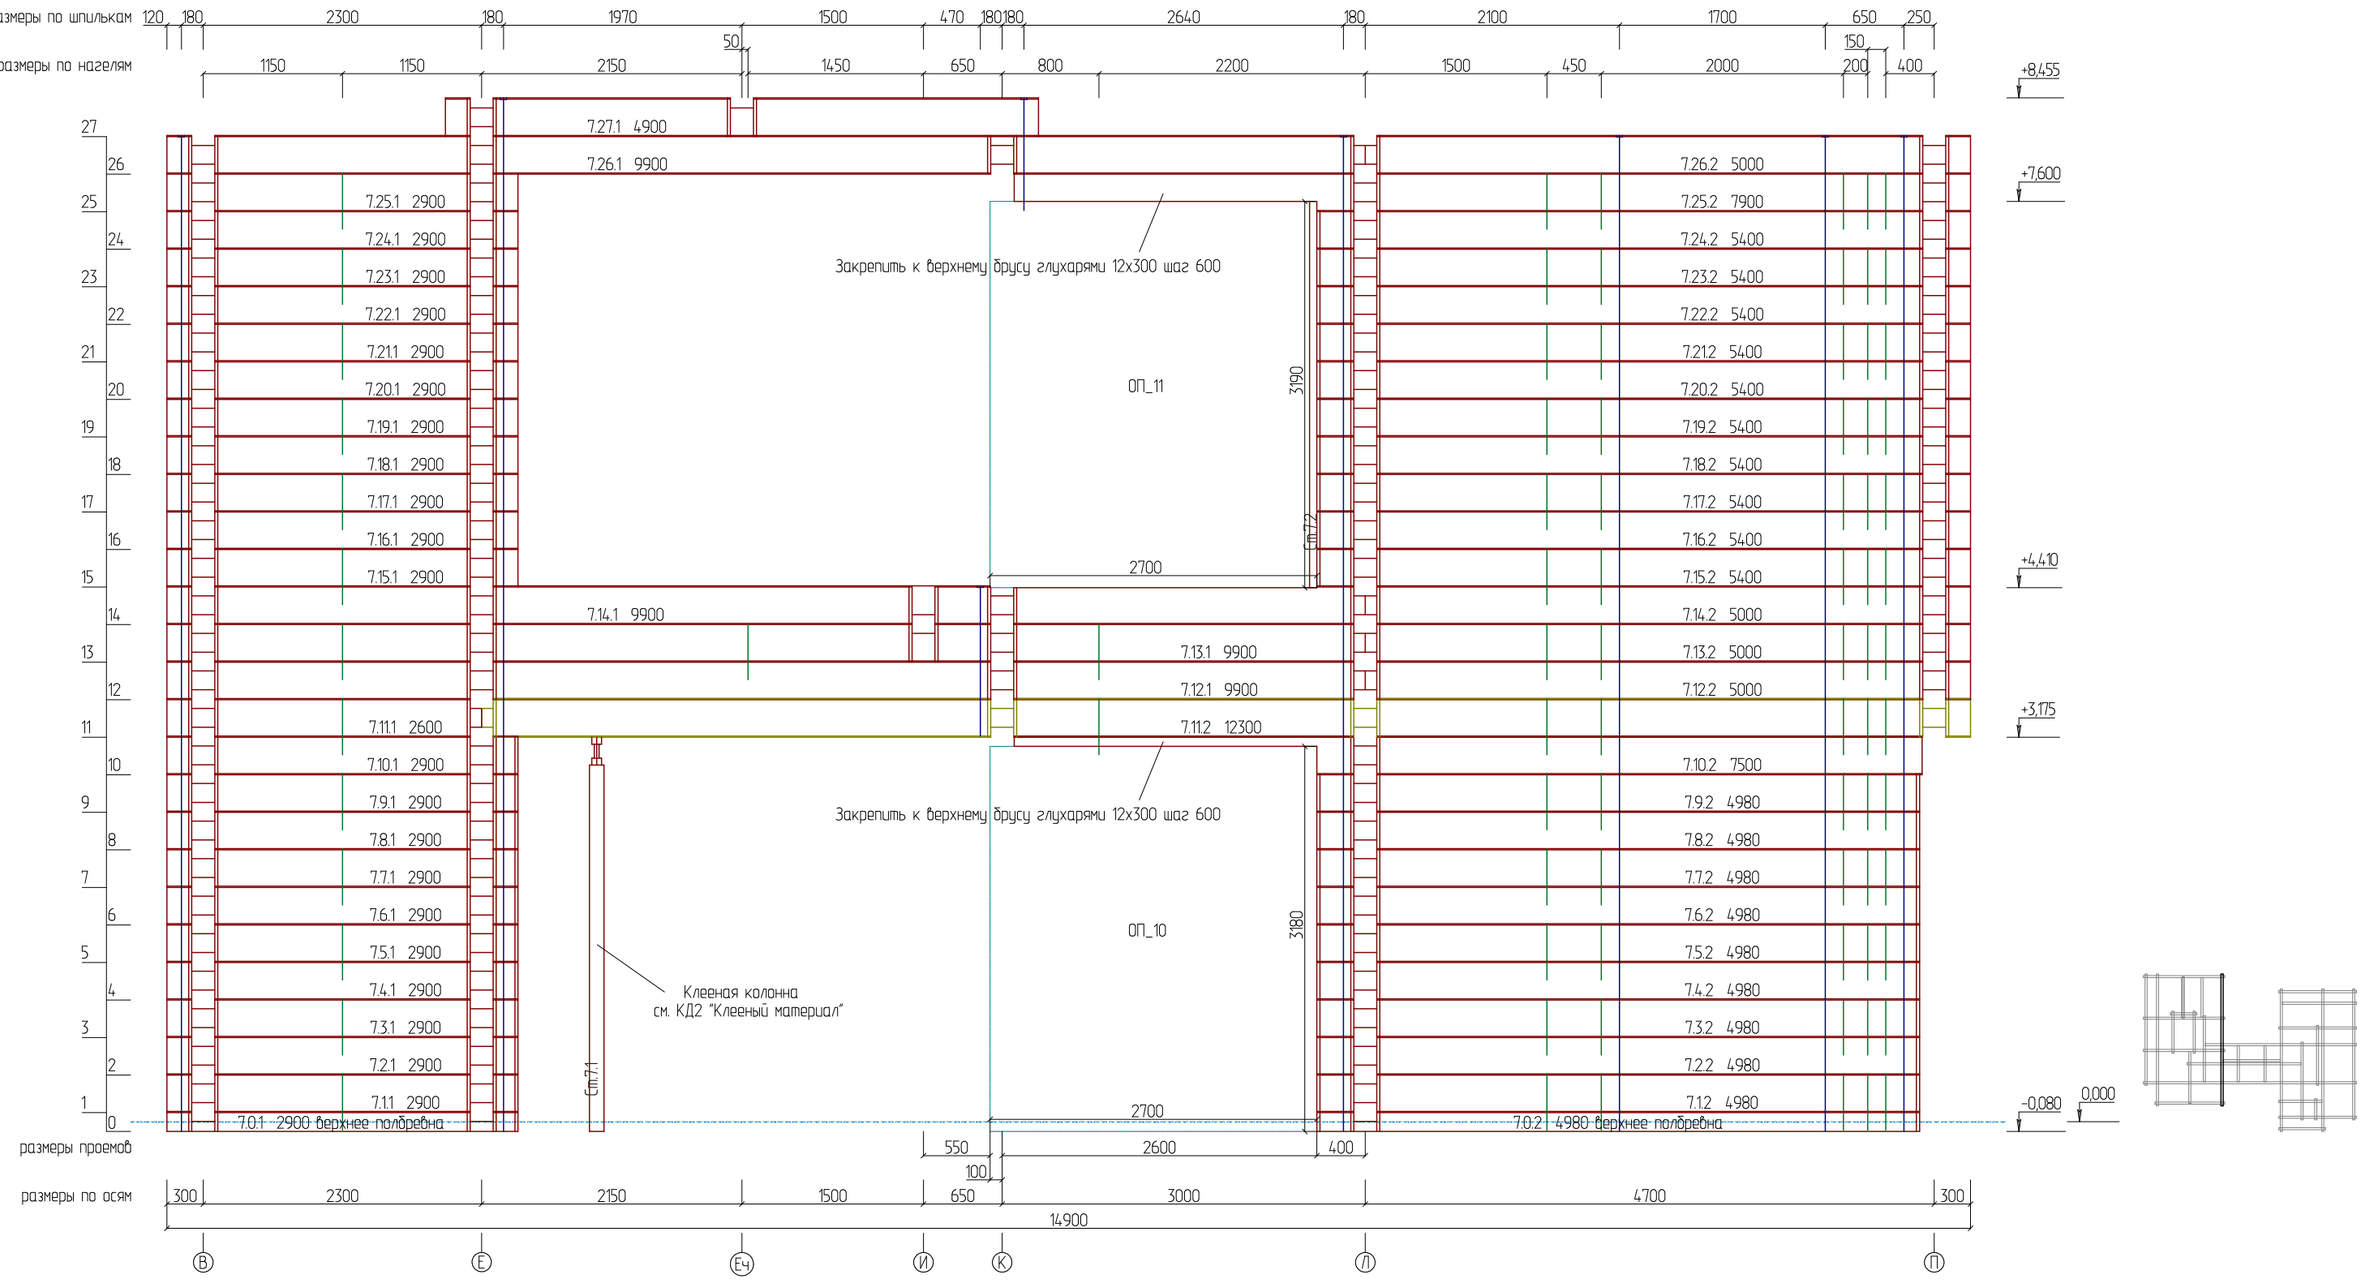

						- АС		
Изм.	Кол. уч.	Лист	№ док.	Подпись	Дата			
Разработал		Москалюк А.				Берта Ромарио	Стадия	Лист	Листов
Проверил		Баннов Е.					Р	15	
Конструктор									
ГИП		Баннов Е.				Развертка по стене (оси) 7	ООО "Строй Хауз"		
Н.контроль									

Развертка по стене (оси) 9

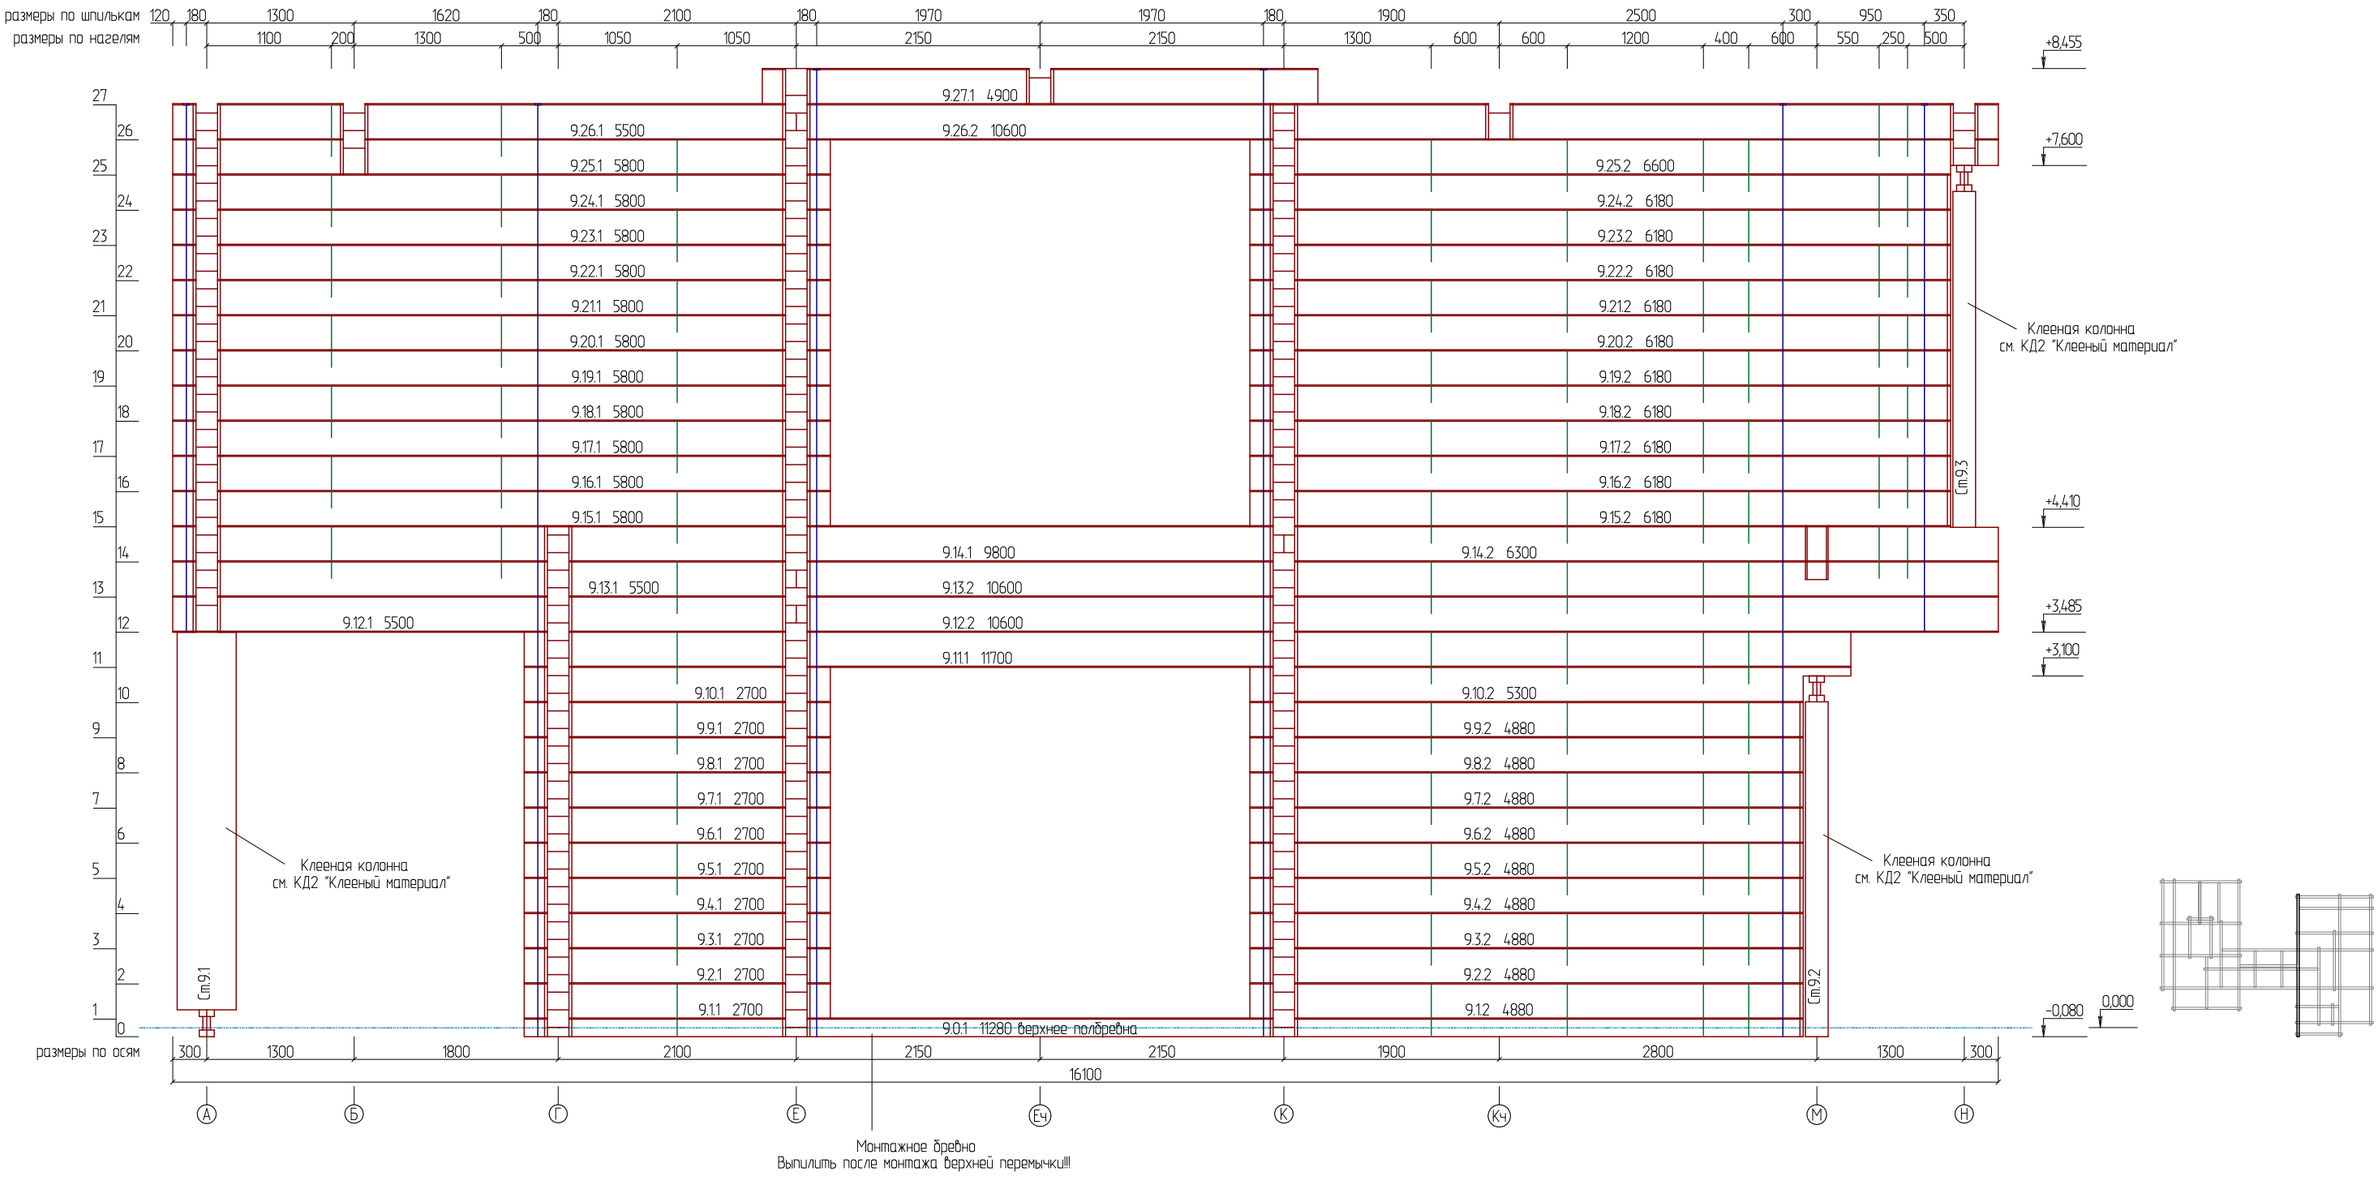


						- АС
Изм.	Кол. уч.	Лист	№ док.	Подпись	Дата	
Разработал		Москалюк А.				Берта Ромарио
Проверил		Баннов Е.				
Конструктор						
ГИП		Баннов Е.				Развертка по стене (оси) 9
Н.контроль						


Стадия	Лист	Листов
Р	16	

ООО "Строй Хауз"

Развертка по стене (оси) 10

Стянуть между собой полнорезьбовыми шурупами 8х400 по узлу Б

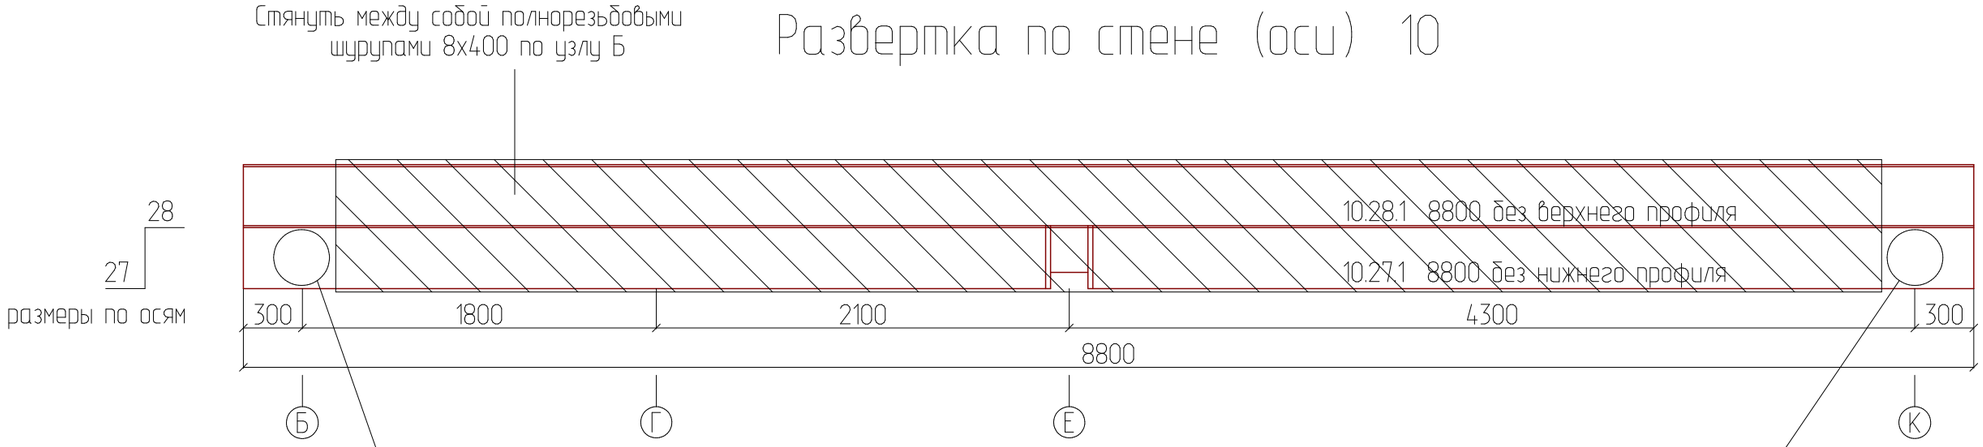

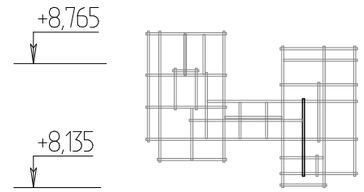


Закрепить к балке по оси Б на полнорезьбовые шурупы 8х240 под углом 45 градусов с 2-х сторон, всего 4шт.

Закрепить к балке по оси К на полнорезьбовые шурупы 8х240 под углом 45 градусов с 2-х сторон, всего 4шт.

						- АС			
Изм.	Кол. уч.	Лист	№ док.	Подпись	Дата				
Разработал		Москалюк А.				Берта Ромарио	Стадия	Лист	Листов
Проверил		Баннов Е.					Р	17	
Конструктор									
ГИП		Баннов Е.				Развертка по стене (оси) 10	ООО "Строй Хауз"		
Н.контроль									

Развертка по стене (оси) 11

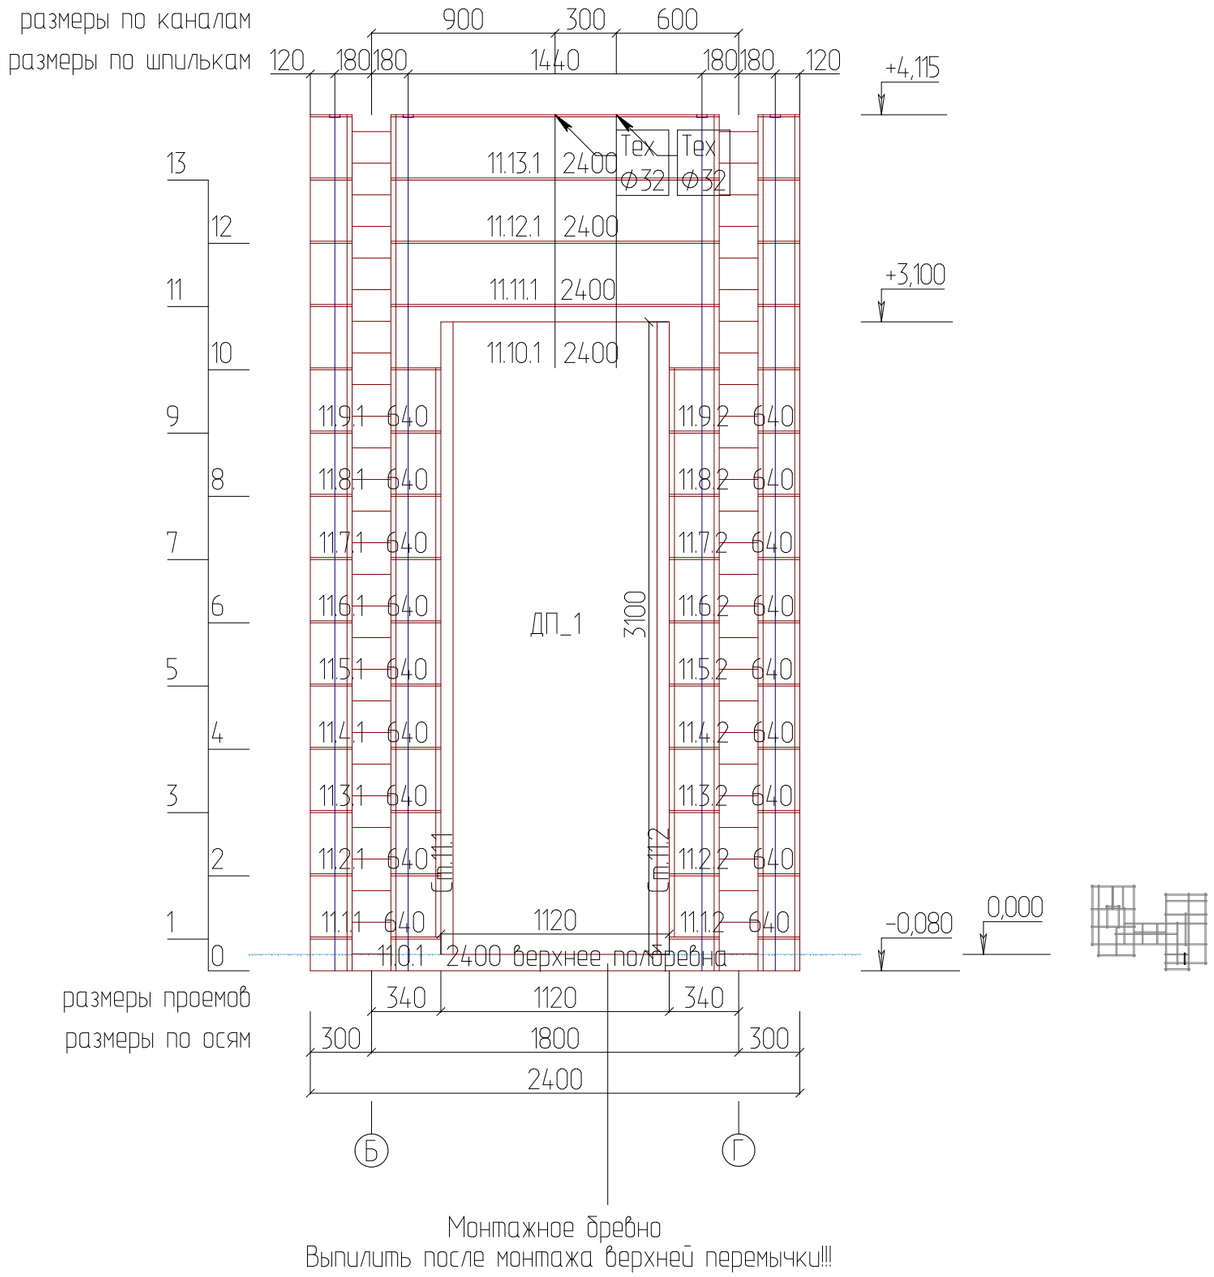

						- АС
Изм.	Кол. уч.	Лист	№ док.	Подпись	Дата	
Разработал		Москалюк А.				Берта Ромарио
Проверил		Баннов Е.				
Конструктор						
ГИП		Баннов Е.				Развертка по стене (оси) 11
Н.контроль						

Стадия	Лист	Листов
Р	18	

ООО "Строй Хауз"

Развертка по стене (оси) 11ч

Стянуть между собой полнорезьбовыми шурупами 8х400 по узлу Б

Узлы крепления см. КД2 "Клееный материал"

30
29

11ч.30.1 6800 без верхнего профиля

11ч.29.1 6800 без нижнего профиля

См.11ч.1

См.11ч.2


Клееная колонна
см. КД2 "Клееный материал"

+9,385

+8,755

+8,300

+8,145

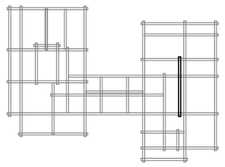

размеры по осям


300	4300	1900	300

6800

Е К Кч

Изм.	Кол. уч.	Лист	№ док.	Подпись	Дата	- АС			
Разработал		Москалюк А.				Берта Ромарио	Стадия	Лист	Листов
Проверил		Баннов Е.					Р	19	
Конструктор									
ГИП		Баннов Е.				Развертка по стене (оси) 11ч	ООО "Строй Хауз"		
Н.контроль									

Развертка по стене (оси) 12

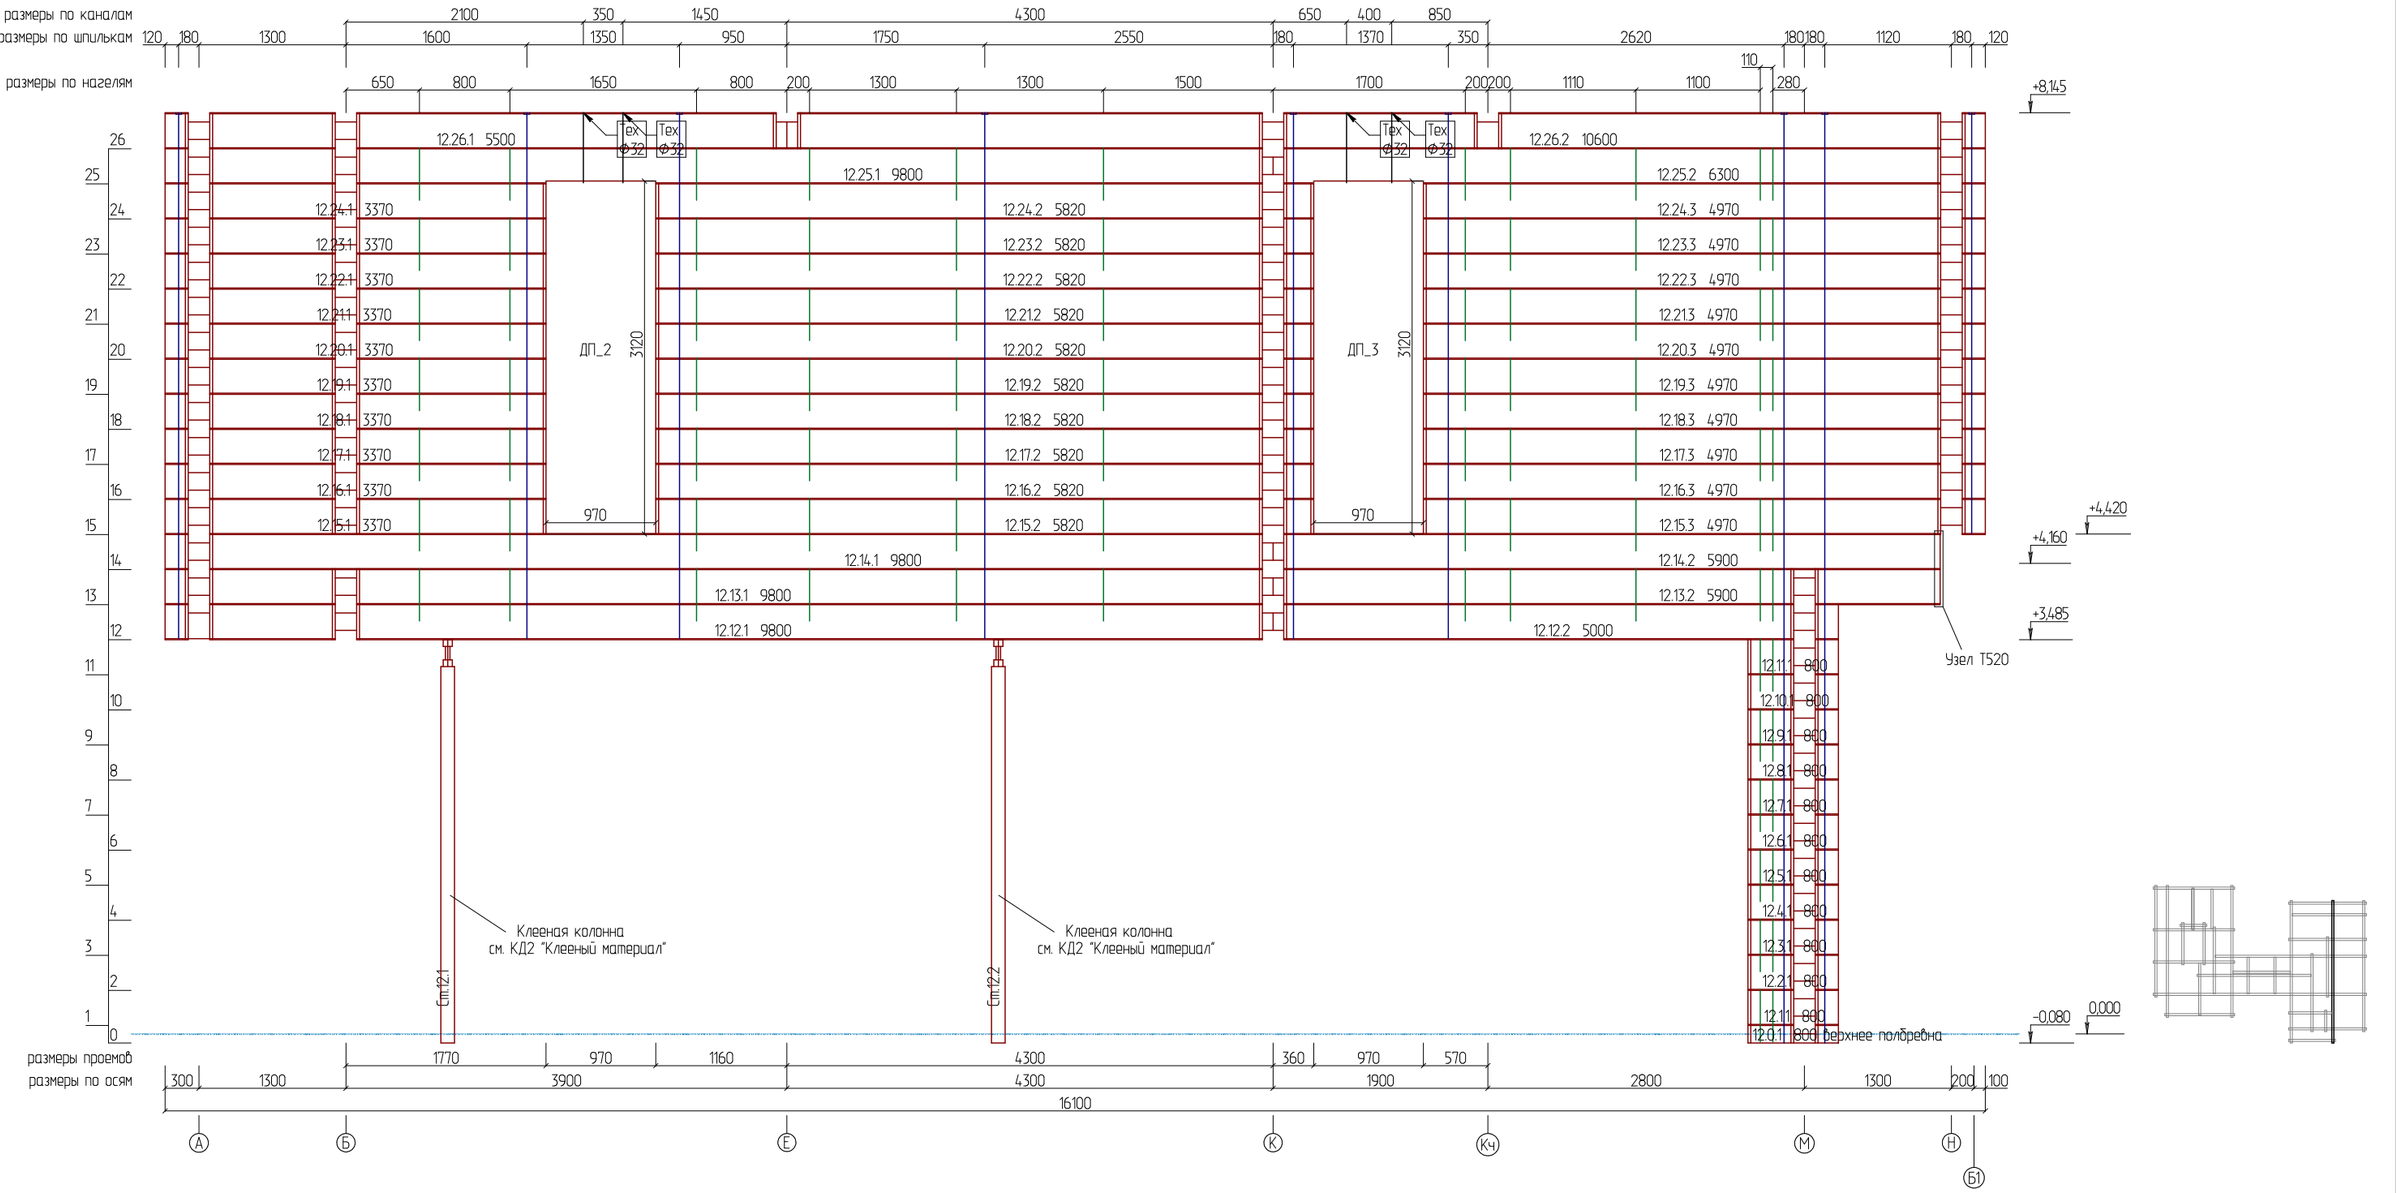


						- АС
Изм.	Кол. уч.	Лист	№ док.	Подпись	Дата	
Разработал		Москалюк А.				Берта Ромарио
Проверил		Баннов Е.				
Конструктор						
ГИП		Баннов Е.				
Н.контроль						Развертка по стене (оси) 12

Стадия	Лист	Листов
Р	20	

ООО "Строй Хауз"

Развертка по стене (оси) 13

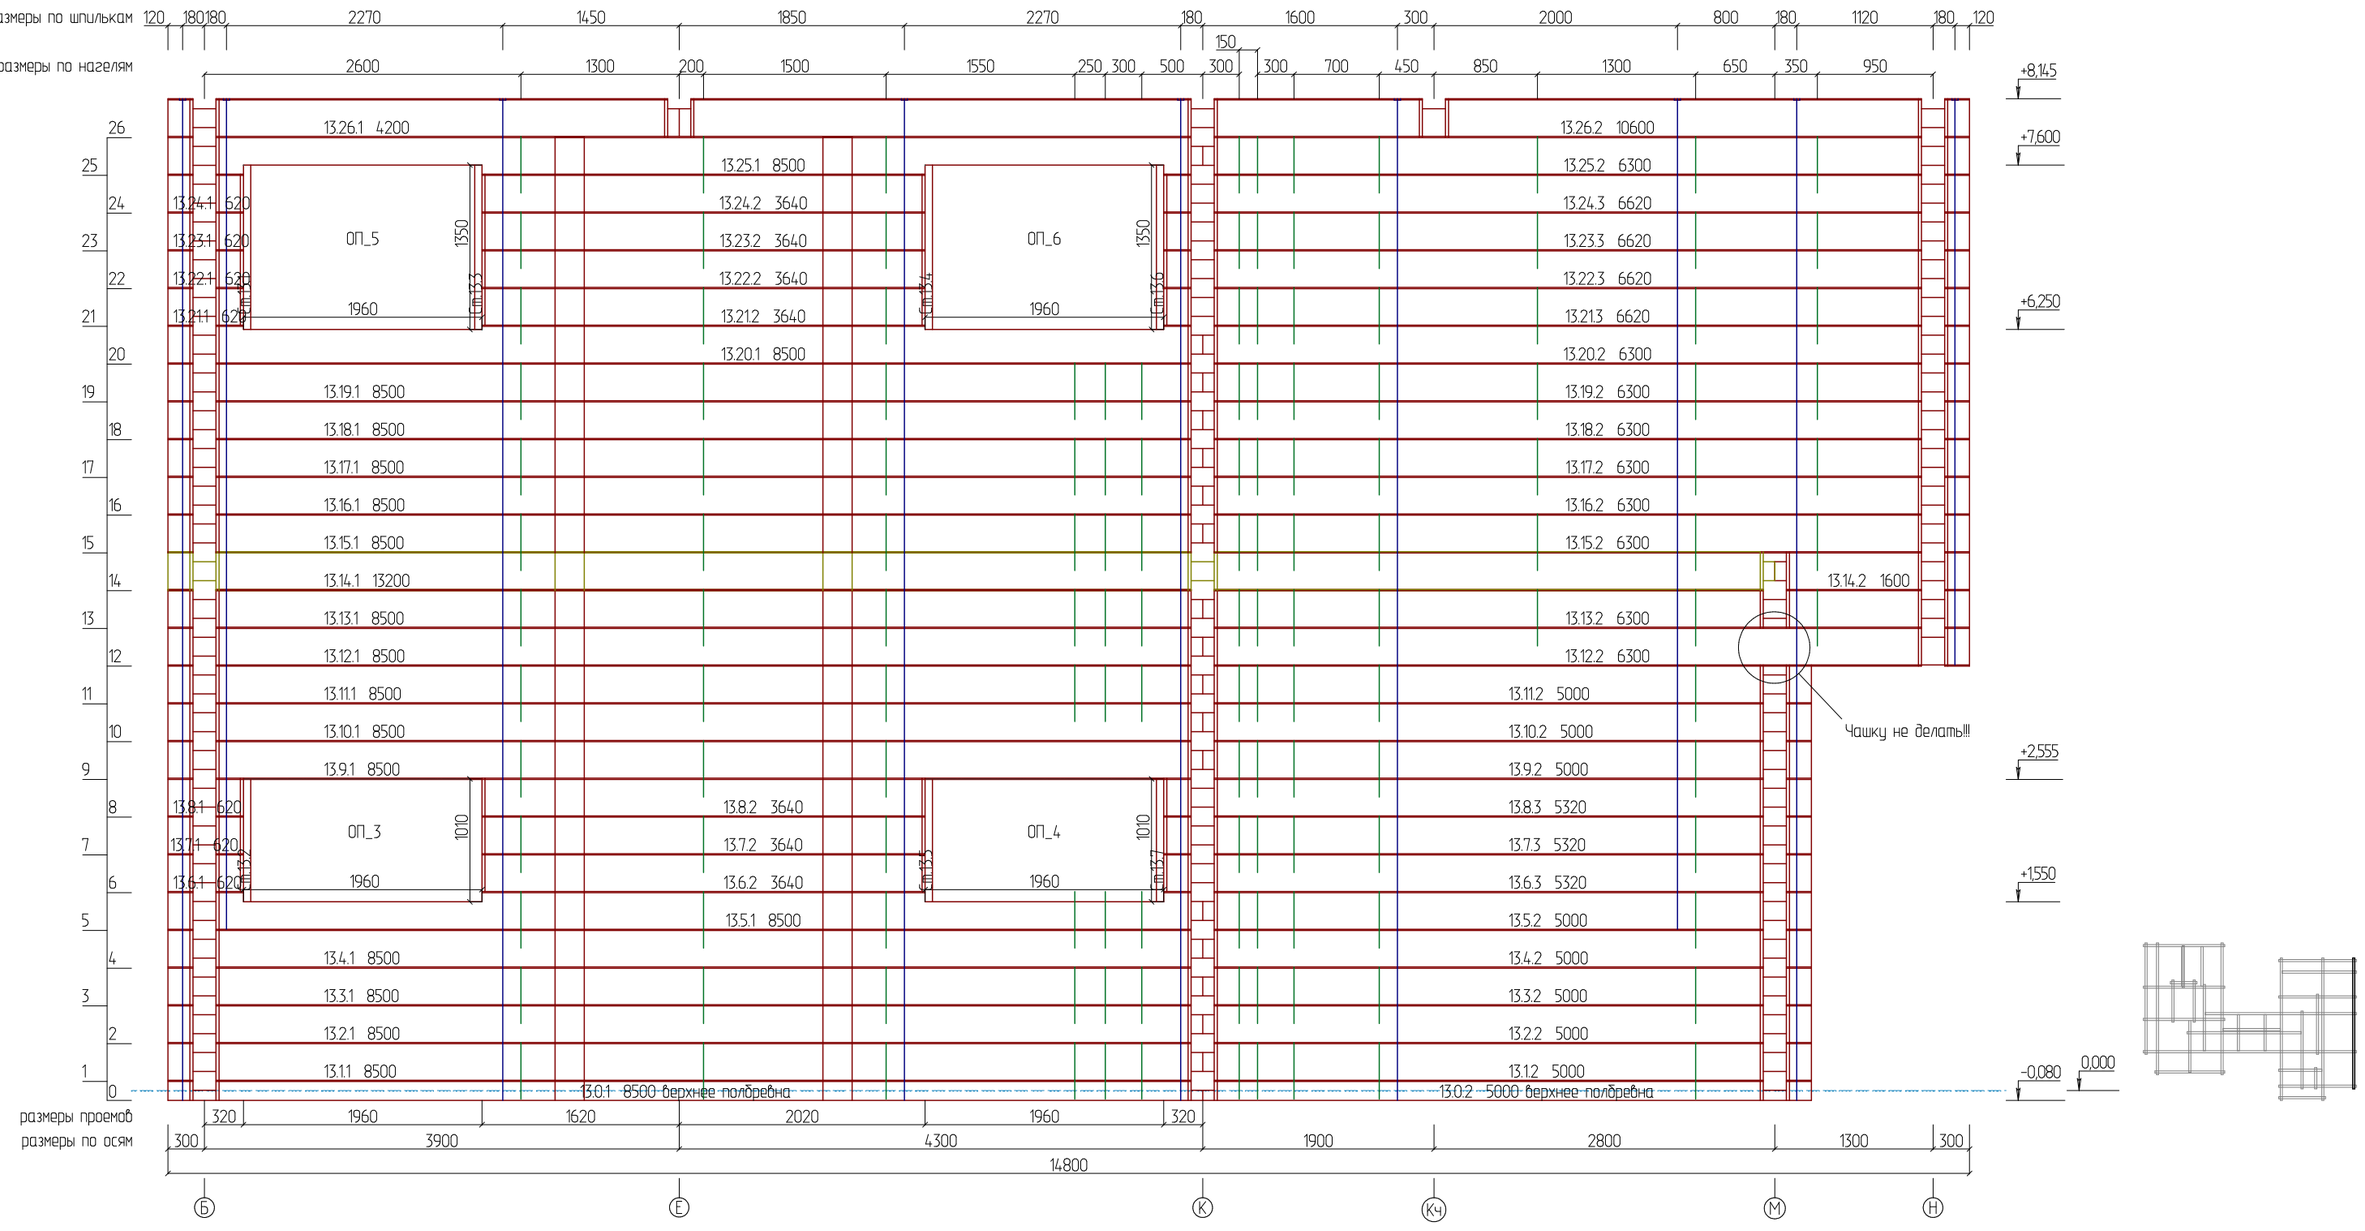


						- АС
Изм.	Кол. уч.	Лист	№ док.	Подпись	Дата	
Разработал		Москалюк А.				Берта Ромарио
Проверил		Баннов Е.				
Конструктор						
ГИП		Баннов Е.				Развертка по стене (оси) 13
Н.контроль						

Стадия	Лист	Листов
Р	21	

ООО "Строй Хауз"

Развертка по стене (оси) А

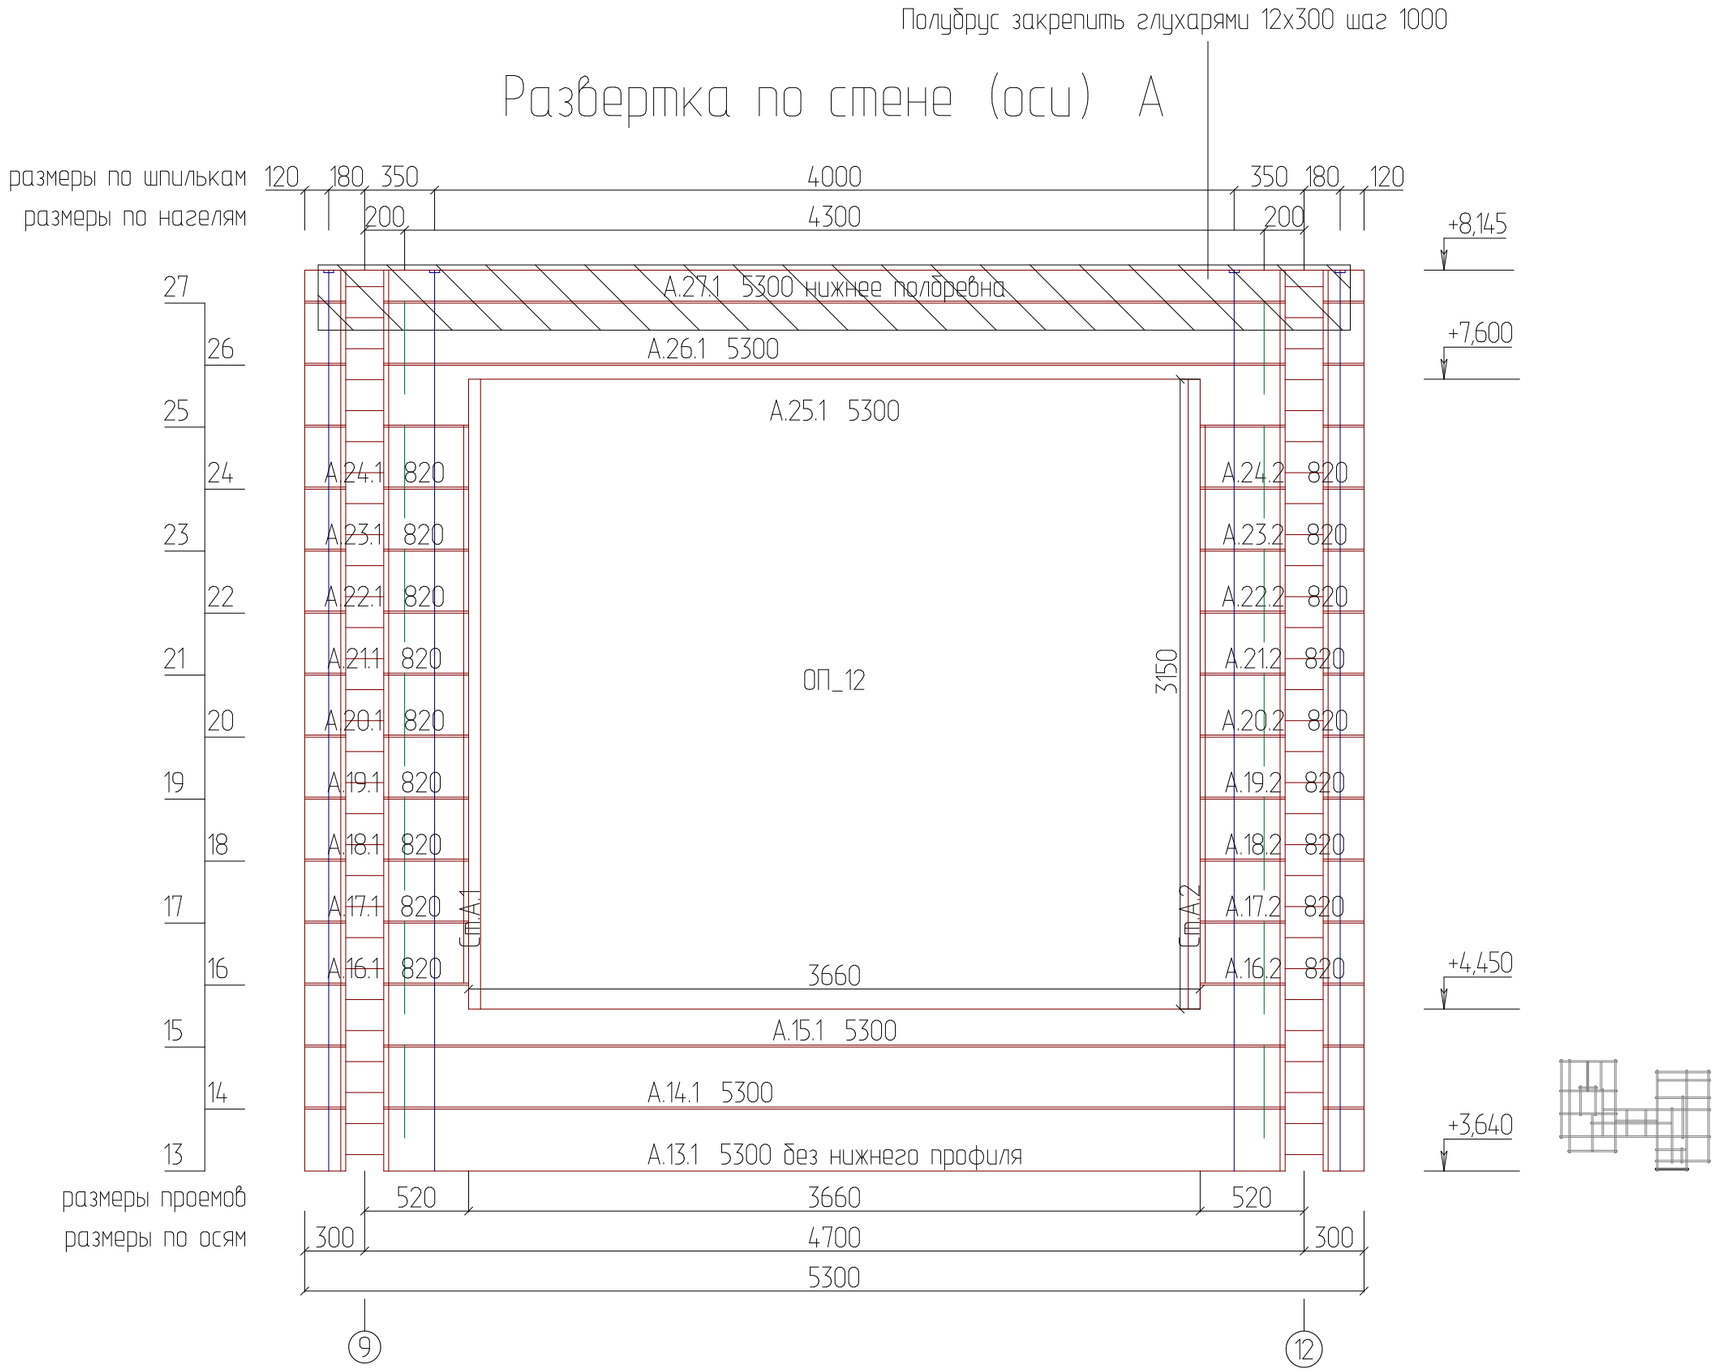


						- АС
Изм.	Кол. уч.	Лист	№ док.	Подпись	Дата	
Разработал		Москалюк А.				Берта Ромарио
Проверил		Баннов Е.				
Конструктор						
ГИП		Баннов Е.				
Н.контроль						Развертка по стене (оси) А

Стадия	Лист	Листов
Р	22	


ООО "Строй Хауз"

Развертка по стене (оси) Б

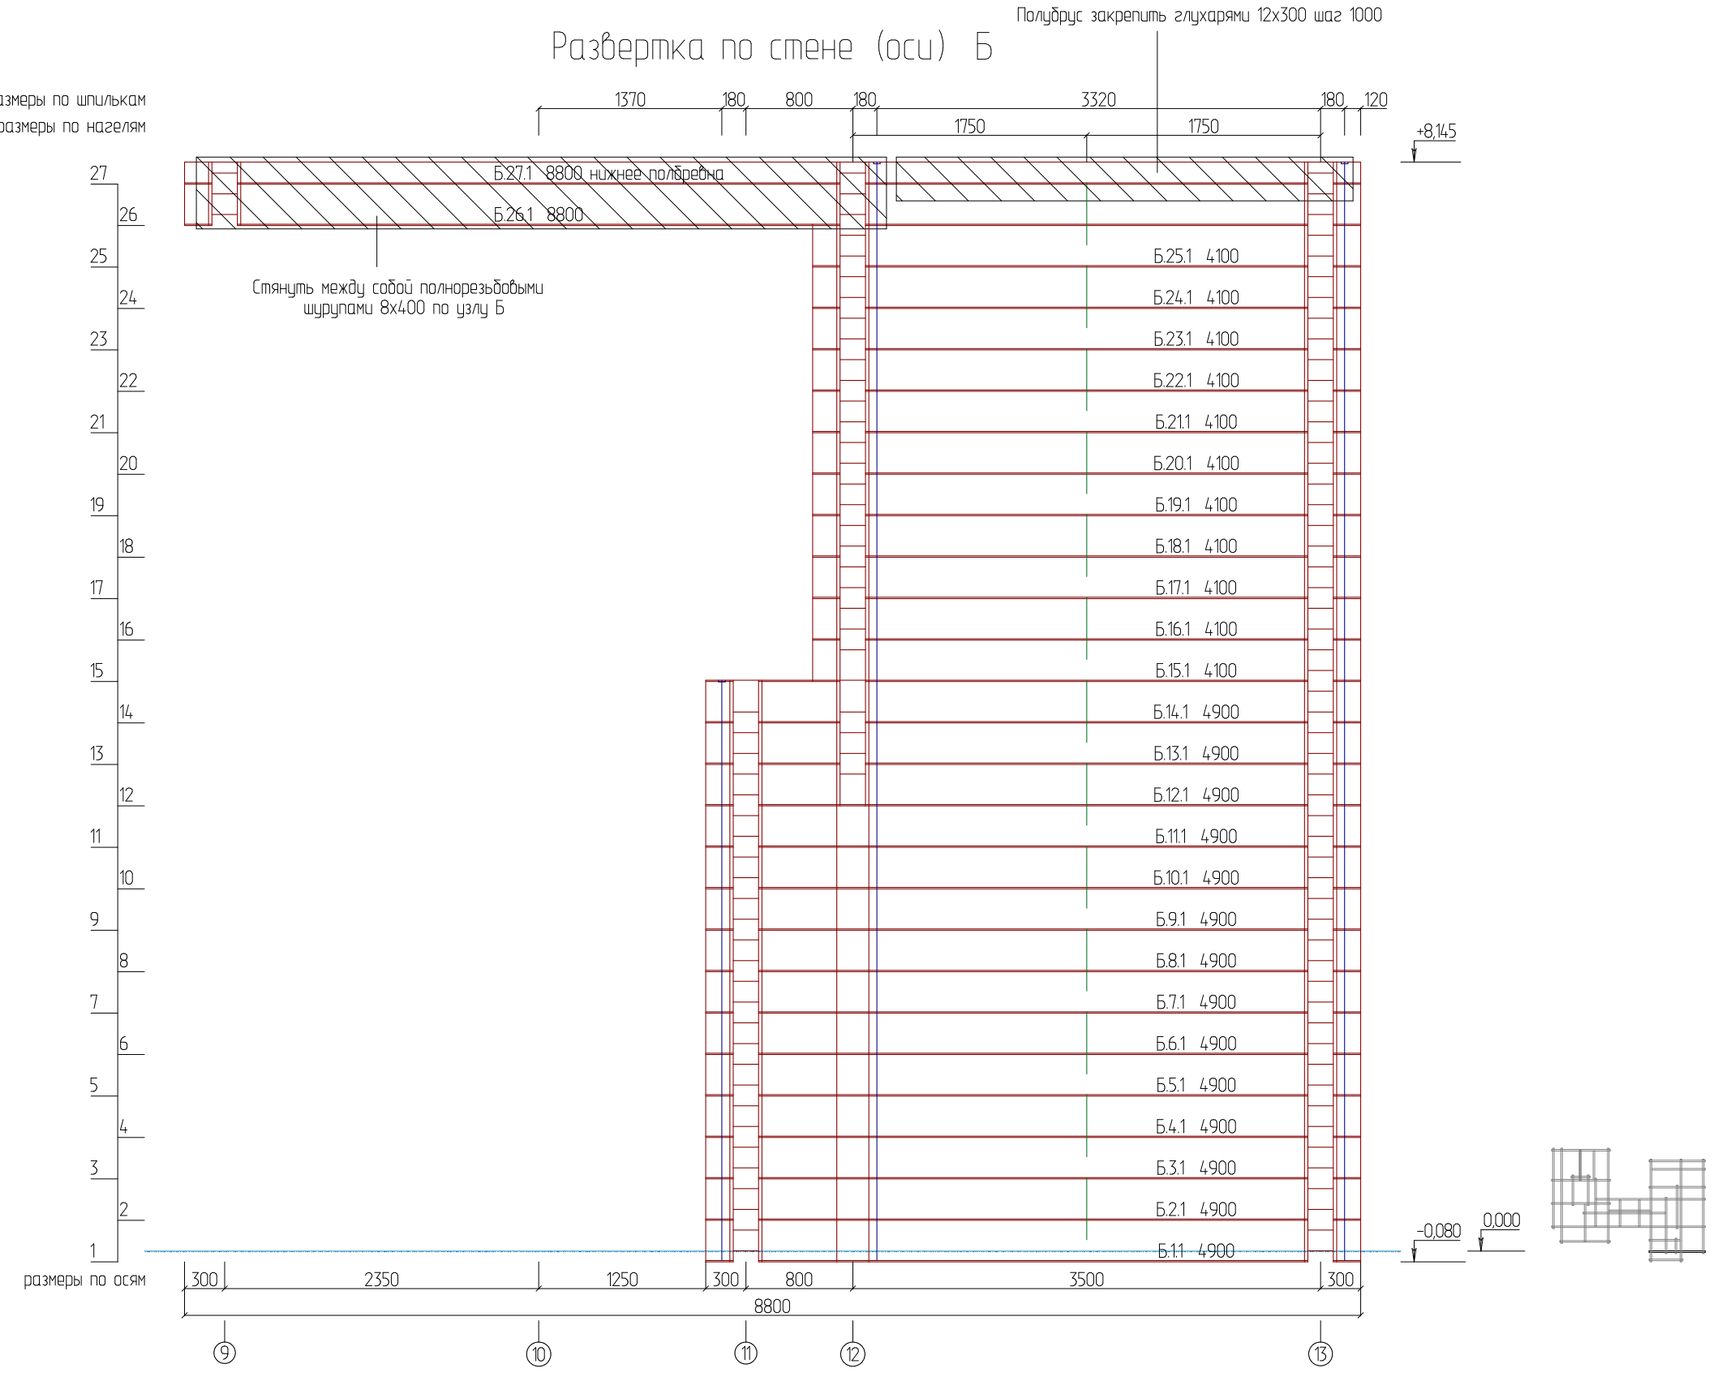

						- АС		
Изм.	Кол. уч.	Лист	№ док.	Подпись	Дата			
Разработал		Москалюк А.				Берта Ромарио	Стадия	Лист	Листов
Проверил		Баннов Е.					Р	23	
Конструктор									
ГИП		Баннов Е.				Развертка по стене (оси) Б	ООО "Строй Хауз"		
Н.контроль									

Развертка по стене (оси) В

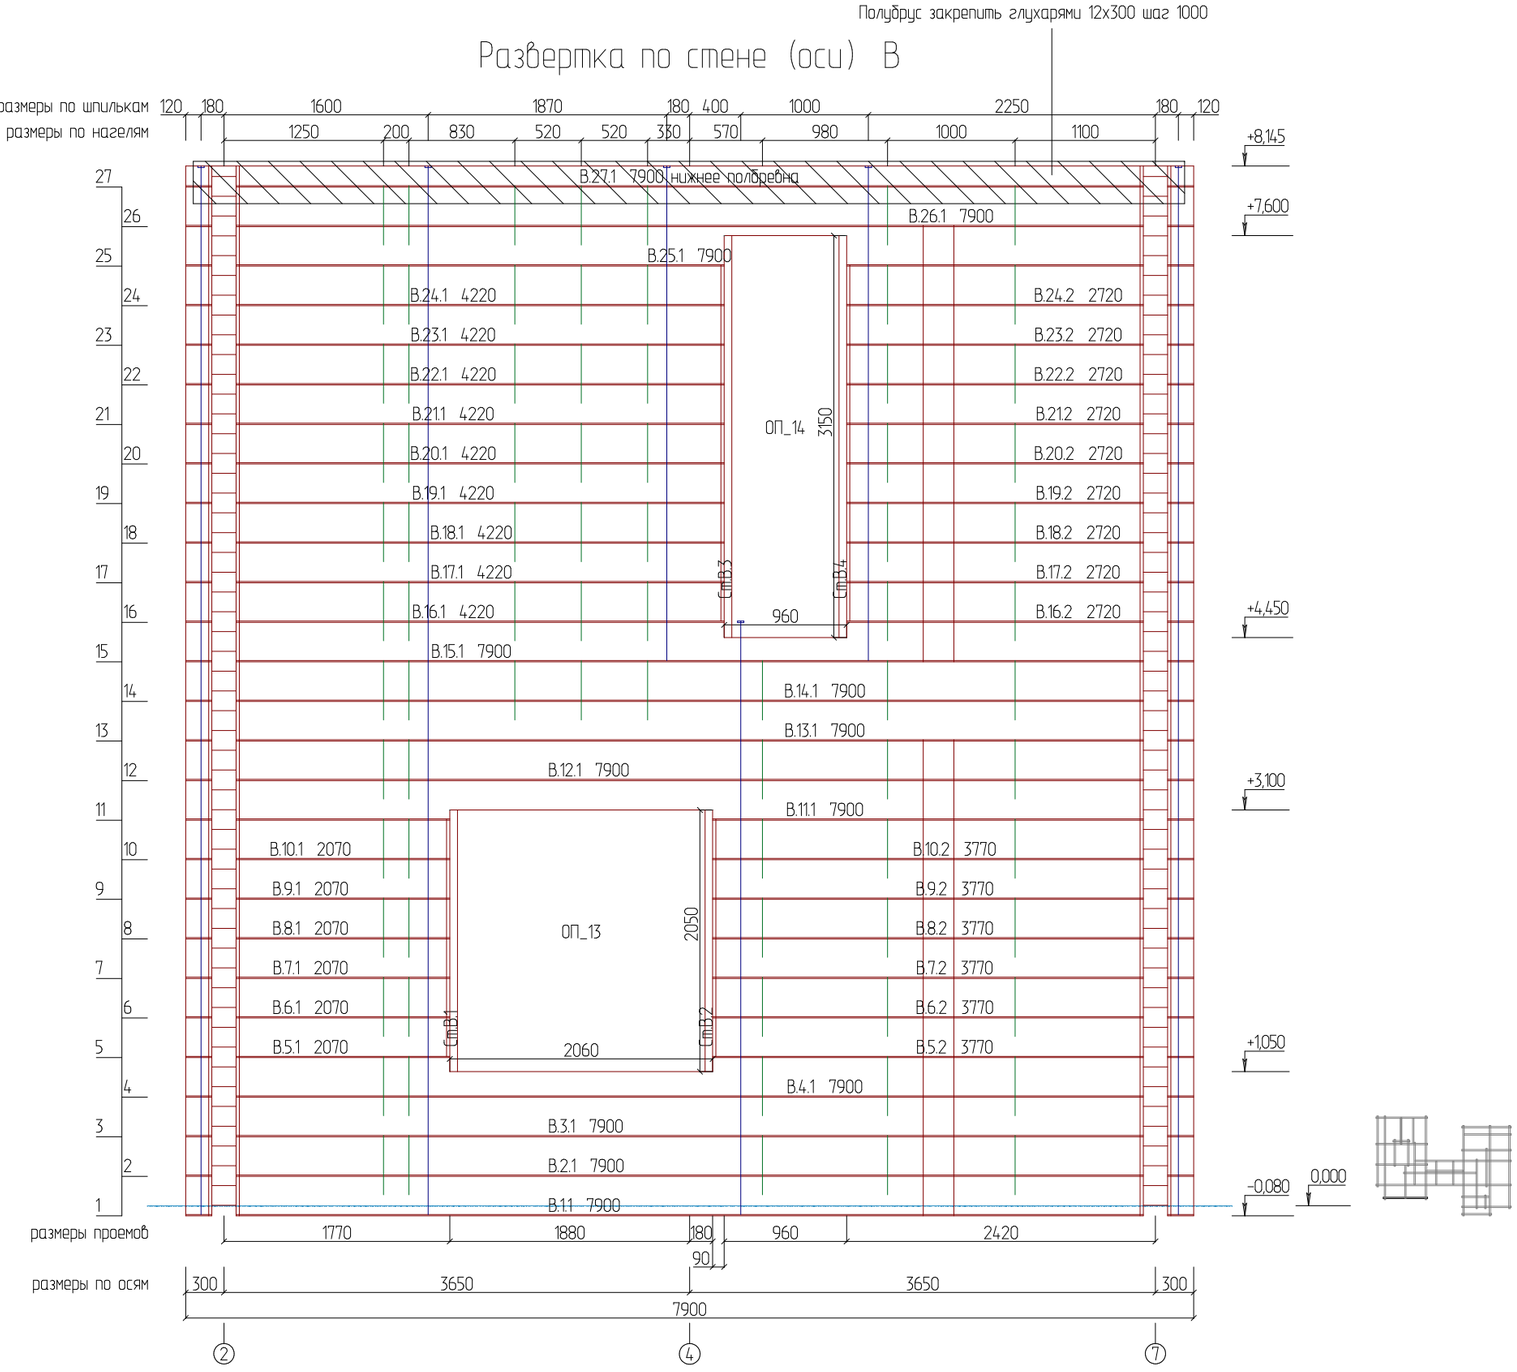


						- АС
Изм.	Кол. уч.	Лист	№ док.	Подпись	Дата	

Разработал	Москалюк А.			Берта Ромарио	Стадия: Р; Лист: 24; Листов:
Проверил	Баннов Е.				
Конструктор					
ГИП	Баннов Е.			Развертка по стене (оси) В	ООО "Строй Хауз"
Н.контроль					

Полубрус закрепить глухарями 12х300 шаг 1000

Развертка по стене (оси) Г

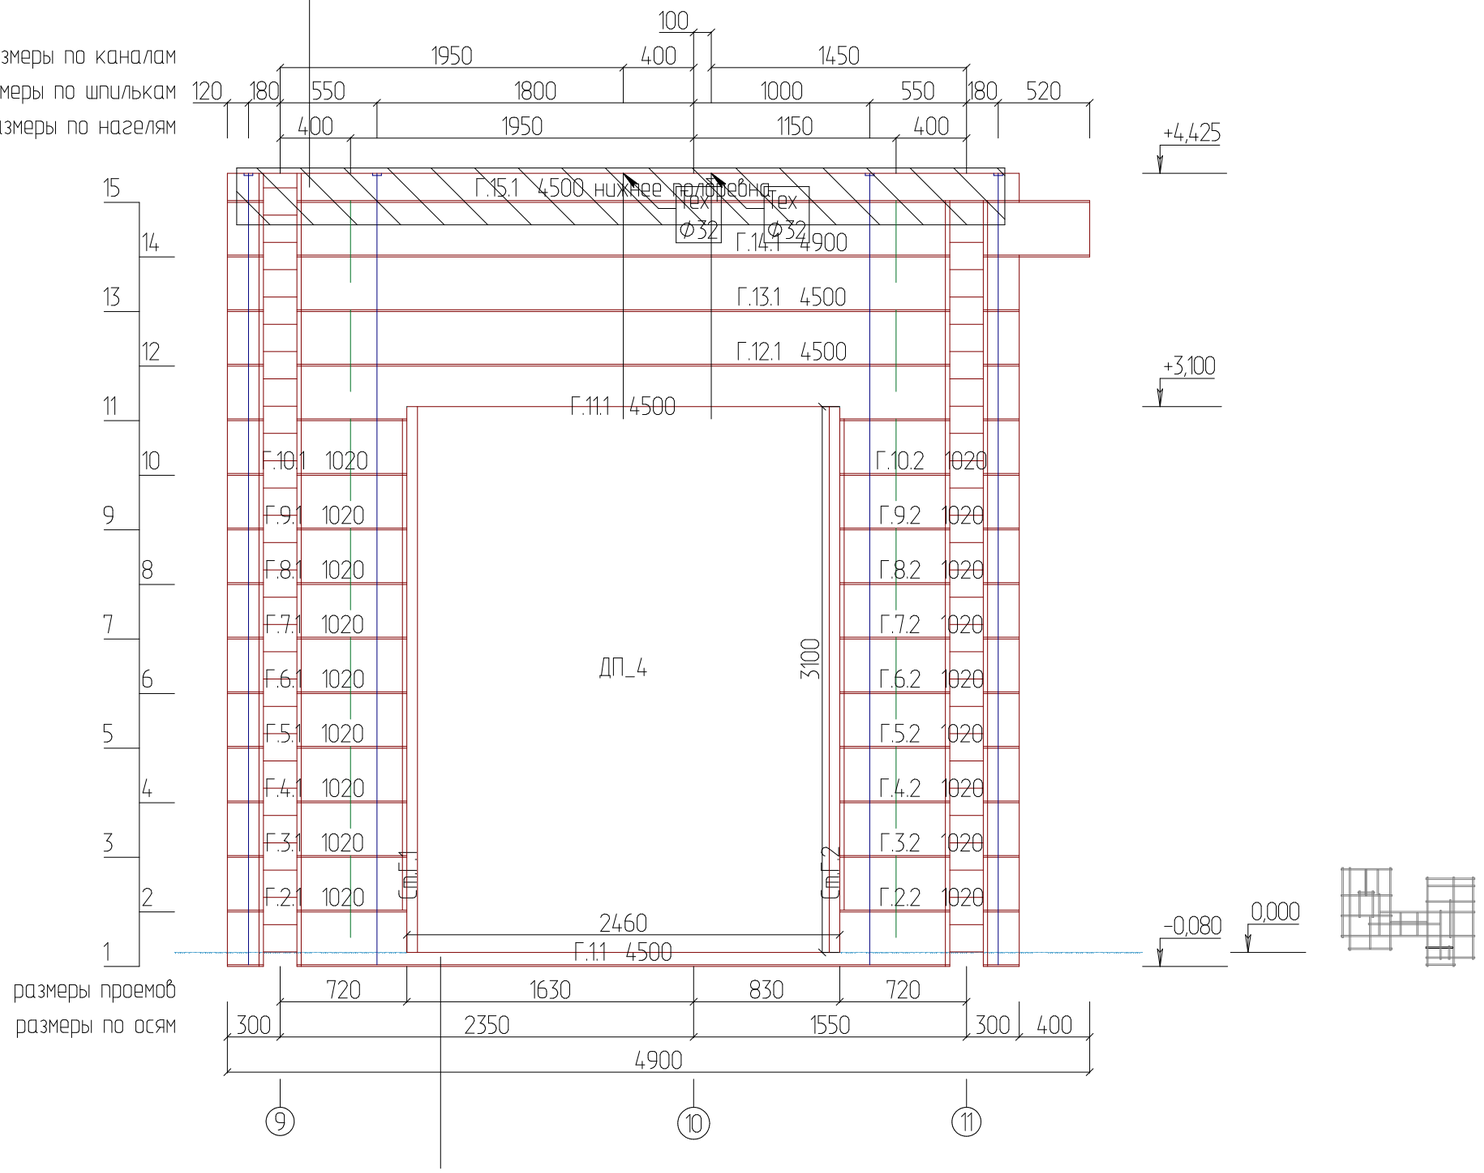


Монтажное бревно
Выпилить после монтажа верхней перемычки!!!

						- АС
Изм.	Кол. уч.	Лист	№ док.	Подпись	Дата	
Разработал		Москалюк А.				Берта Ромарио
Проверил		Баннов Е.				
Конструктор						
ГИП		Баннов Е.				Развертка по стене (оси) Г
Н.контроль						

Стадия	Лист	Листов
Р	25	

ООО "Строй Хауз"

Развертка по стене (оси) Е

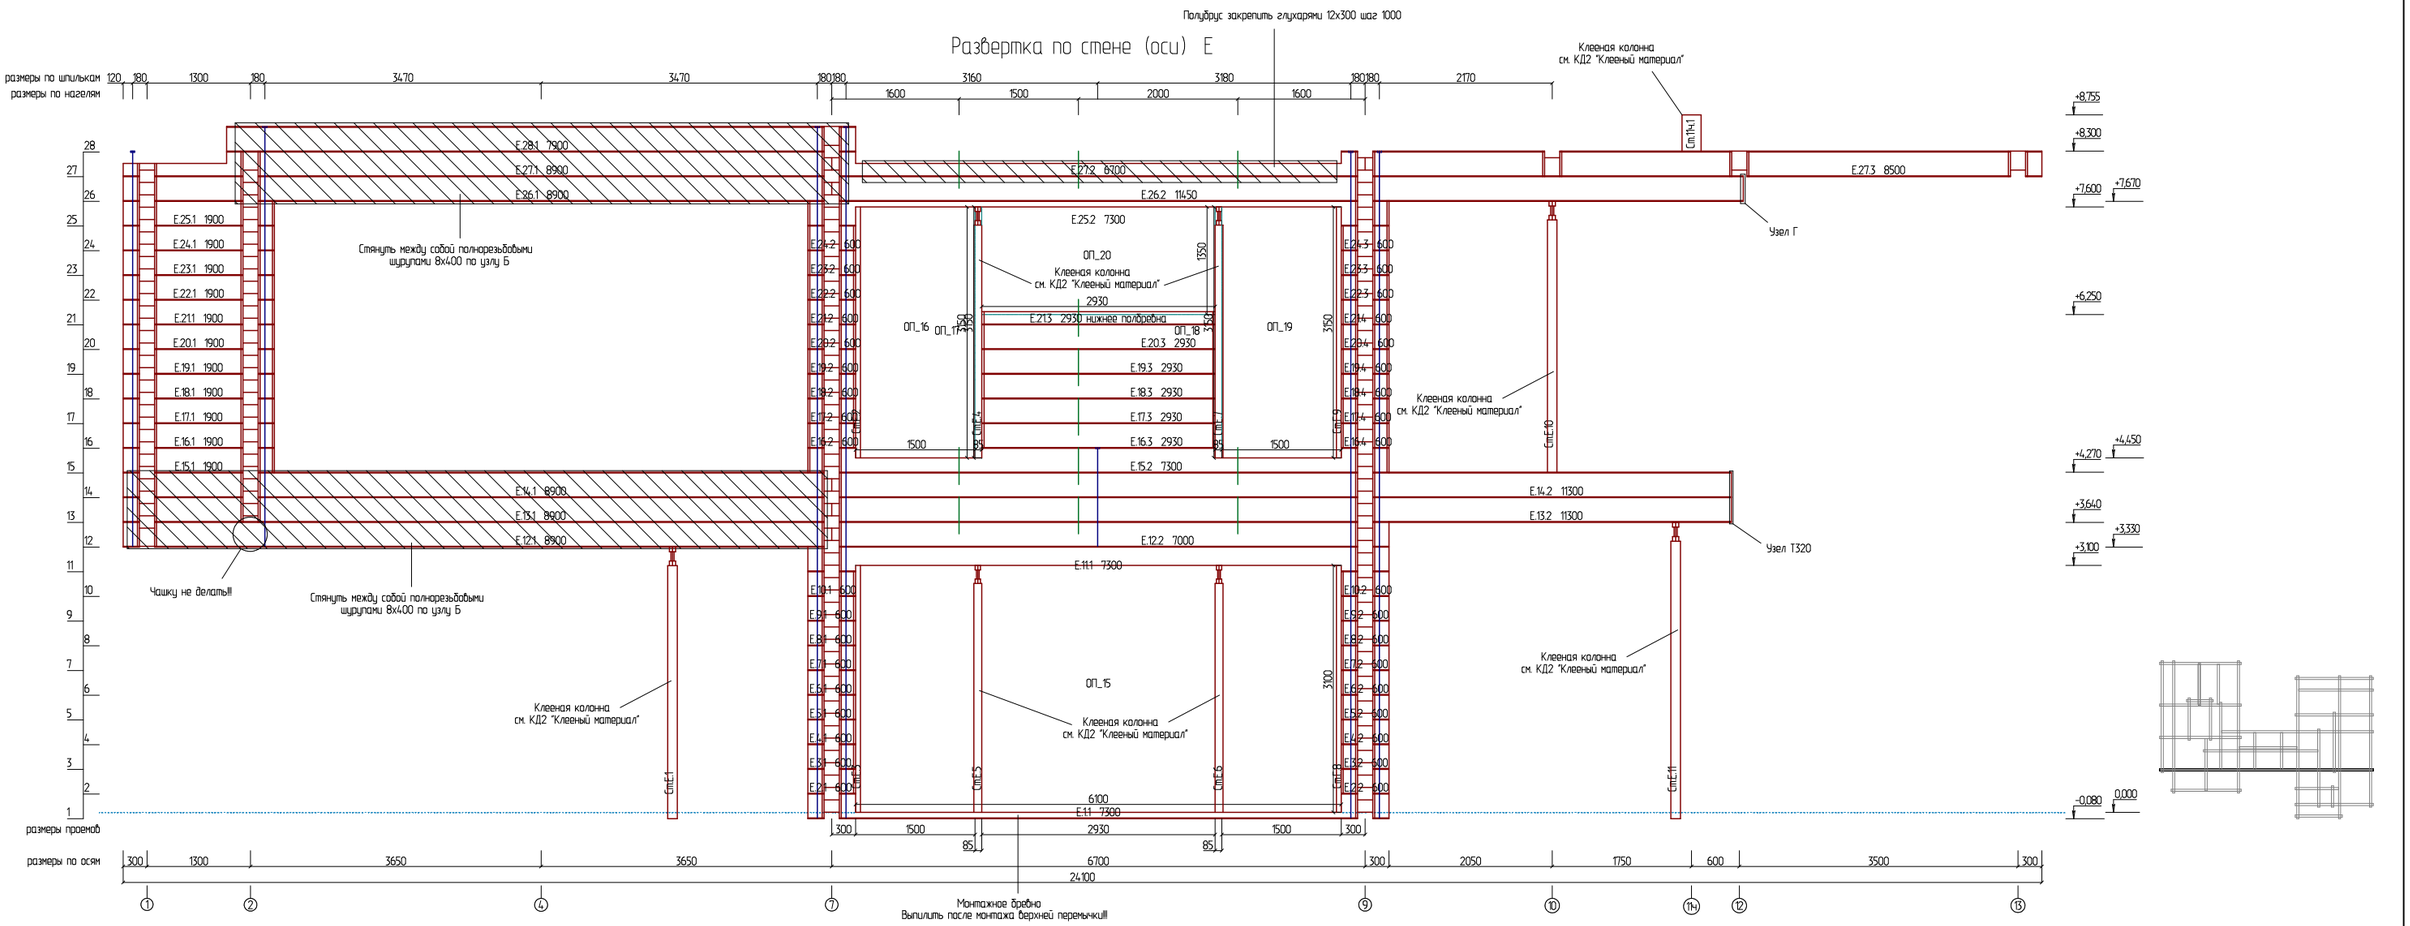


						- АС
Изм.	Кол. уч.	Лист	№ док.	Подпись	Дата	
Разработал		Москалюк А.				Берта Ромарио
Проверил		Баннов Е.				
Конструктор						
ГИП		Баннов Е.				
Н.контроль						Развертка по стене (оси) Е

Стадия	Лист	Листов
Р	26	

ООО "Строй Хауз"

Развертка по стене (оси) Еч

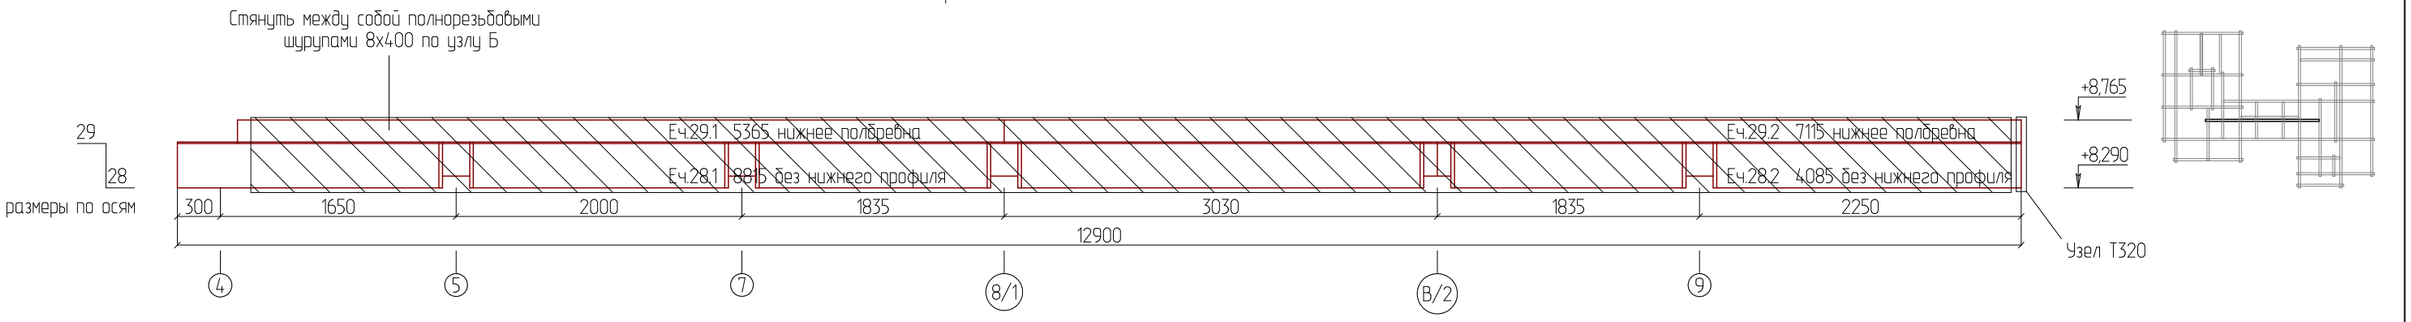


						- АС
Изм.	Кол. уч.	Лист	№ док.	Подпись	Дата	
Разработал		Москалюк А.				Берта Ромарио
Проверил		Баннов Е.				
Конструктор						
ГИП		Баннов Е.				Развертка по стене (оси) Еч
Н.контроль						

Стадия	Лист	Листов
Р	27	

ООО "Строй Хауз"

Развертка по стене (оси) Ж

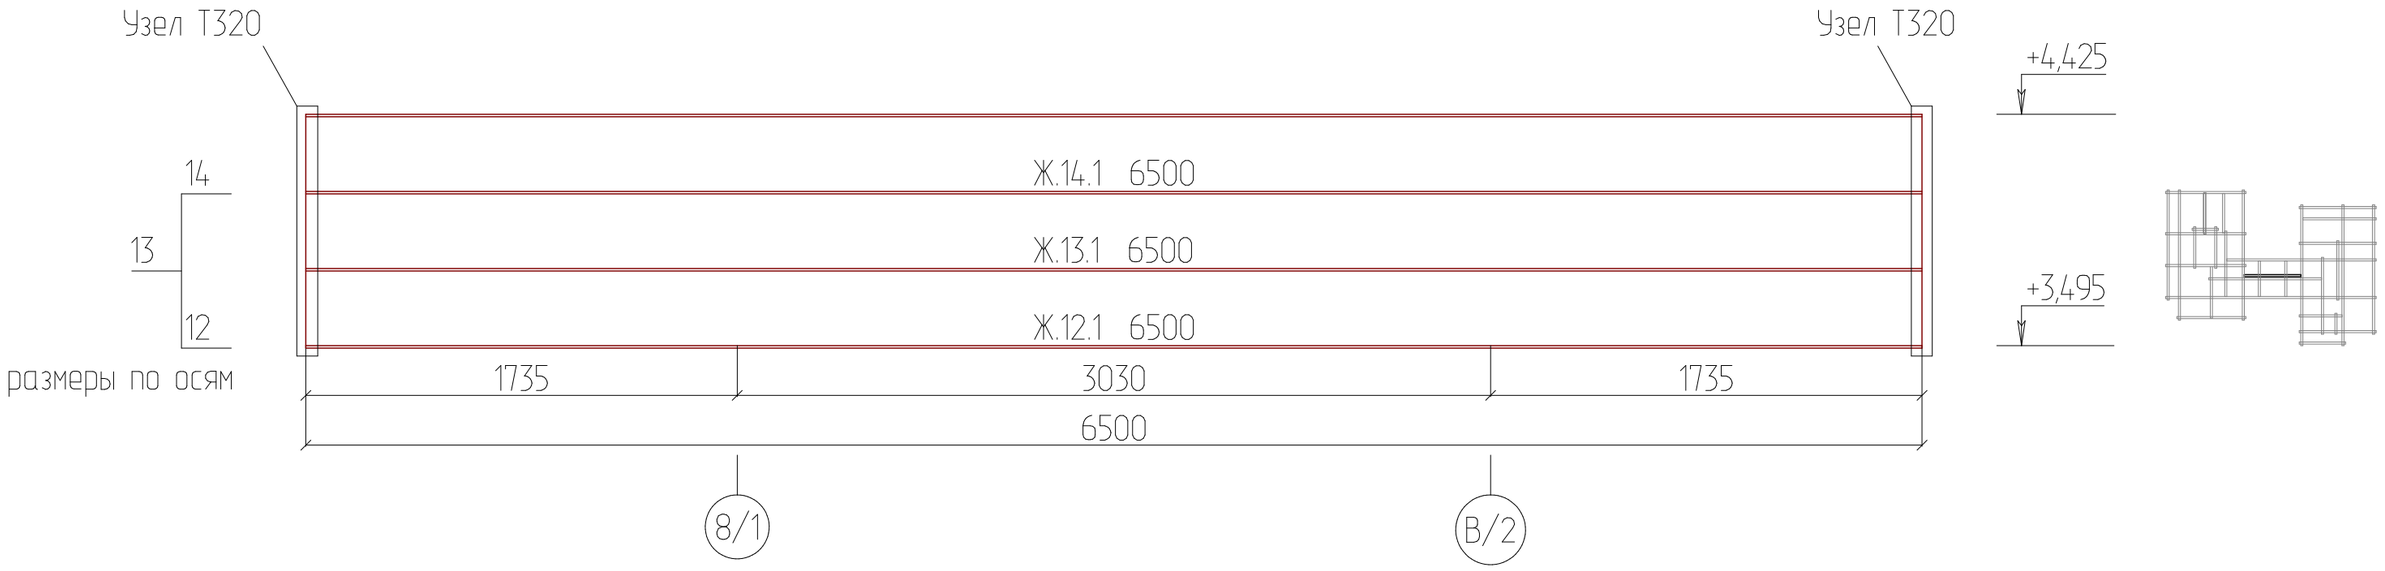


						- АС
Изм.	Кол. уч.	Лист	№ док.	Подпись	Дата	
Разработал		Москалюк А.				Берта Ромарио
Проверил		Баннов Е.				
Конструктор						
ГИП		Баннов Е.				Развертка по стене (оси) Ж
Н.контроль						

Стадия	Лист	Листов
Р	28	

ООО "Строй Хауз"

Развертка по стене (оси) И

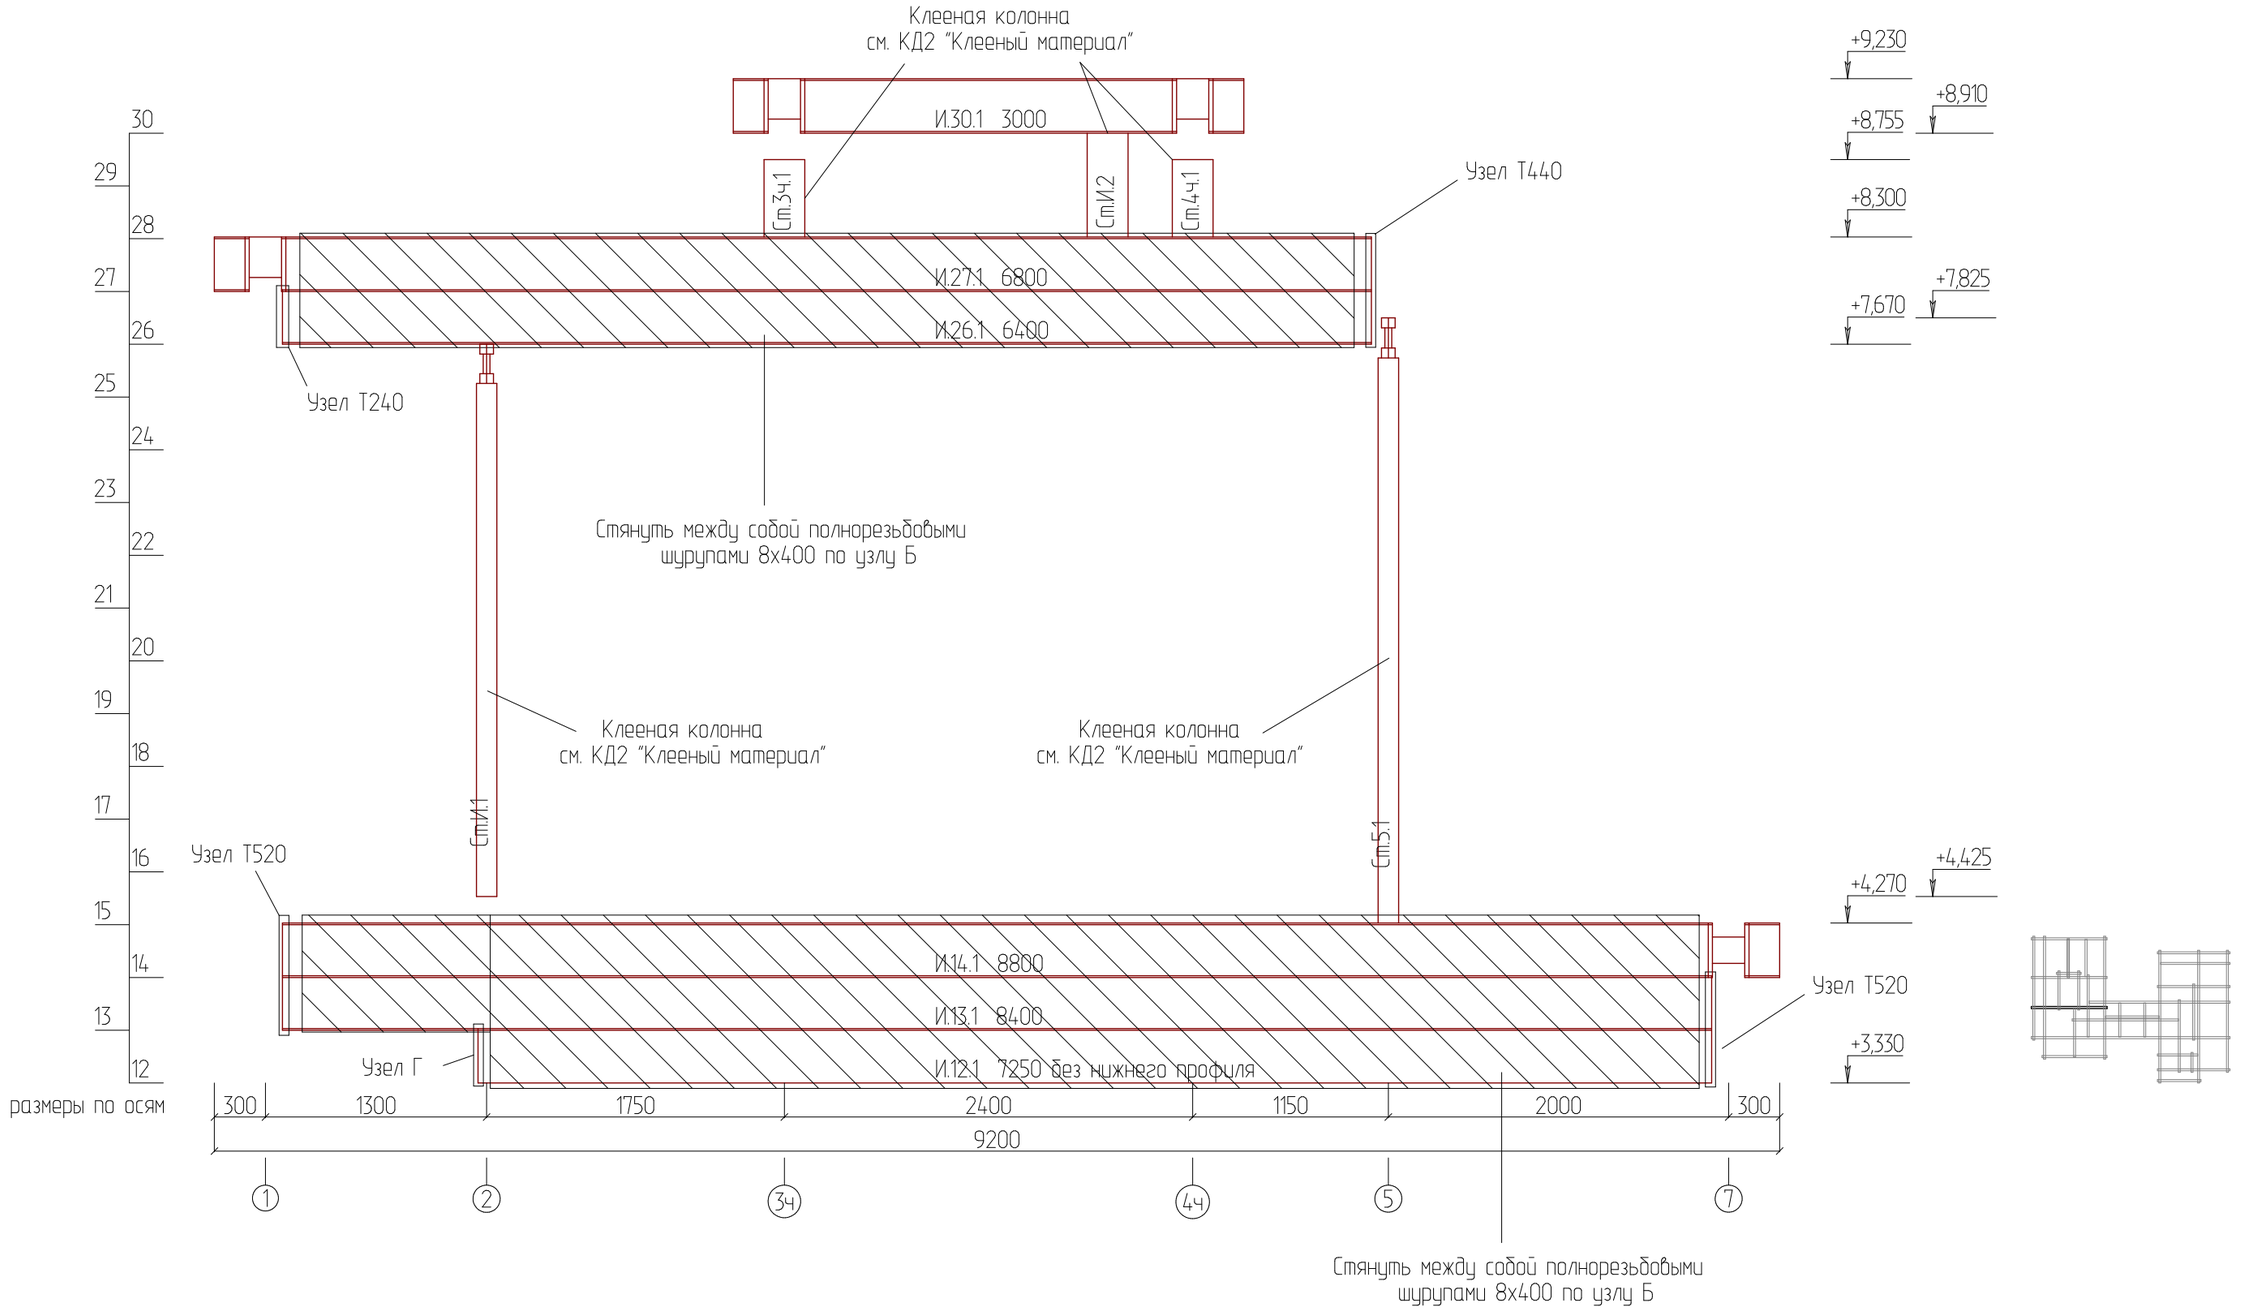


						- АС
Изм.	Кол. уч.	Лист	№ док.	Подпись	Дата	
Разработал		Москалюк А.				Берта Ромарио
Проверил		Баннов Е.				
Конструктор						
ГИП		Баннов Е.				Развертка по стене (оси) И
Н.контроль						

Стадия	Лист	Листов
Р	29	

ООО "Строй Хауз"

Развертка по стене (оси) К

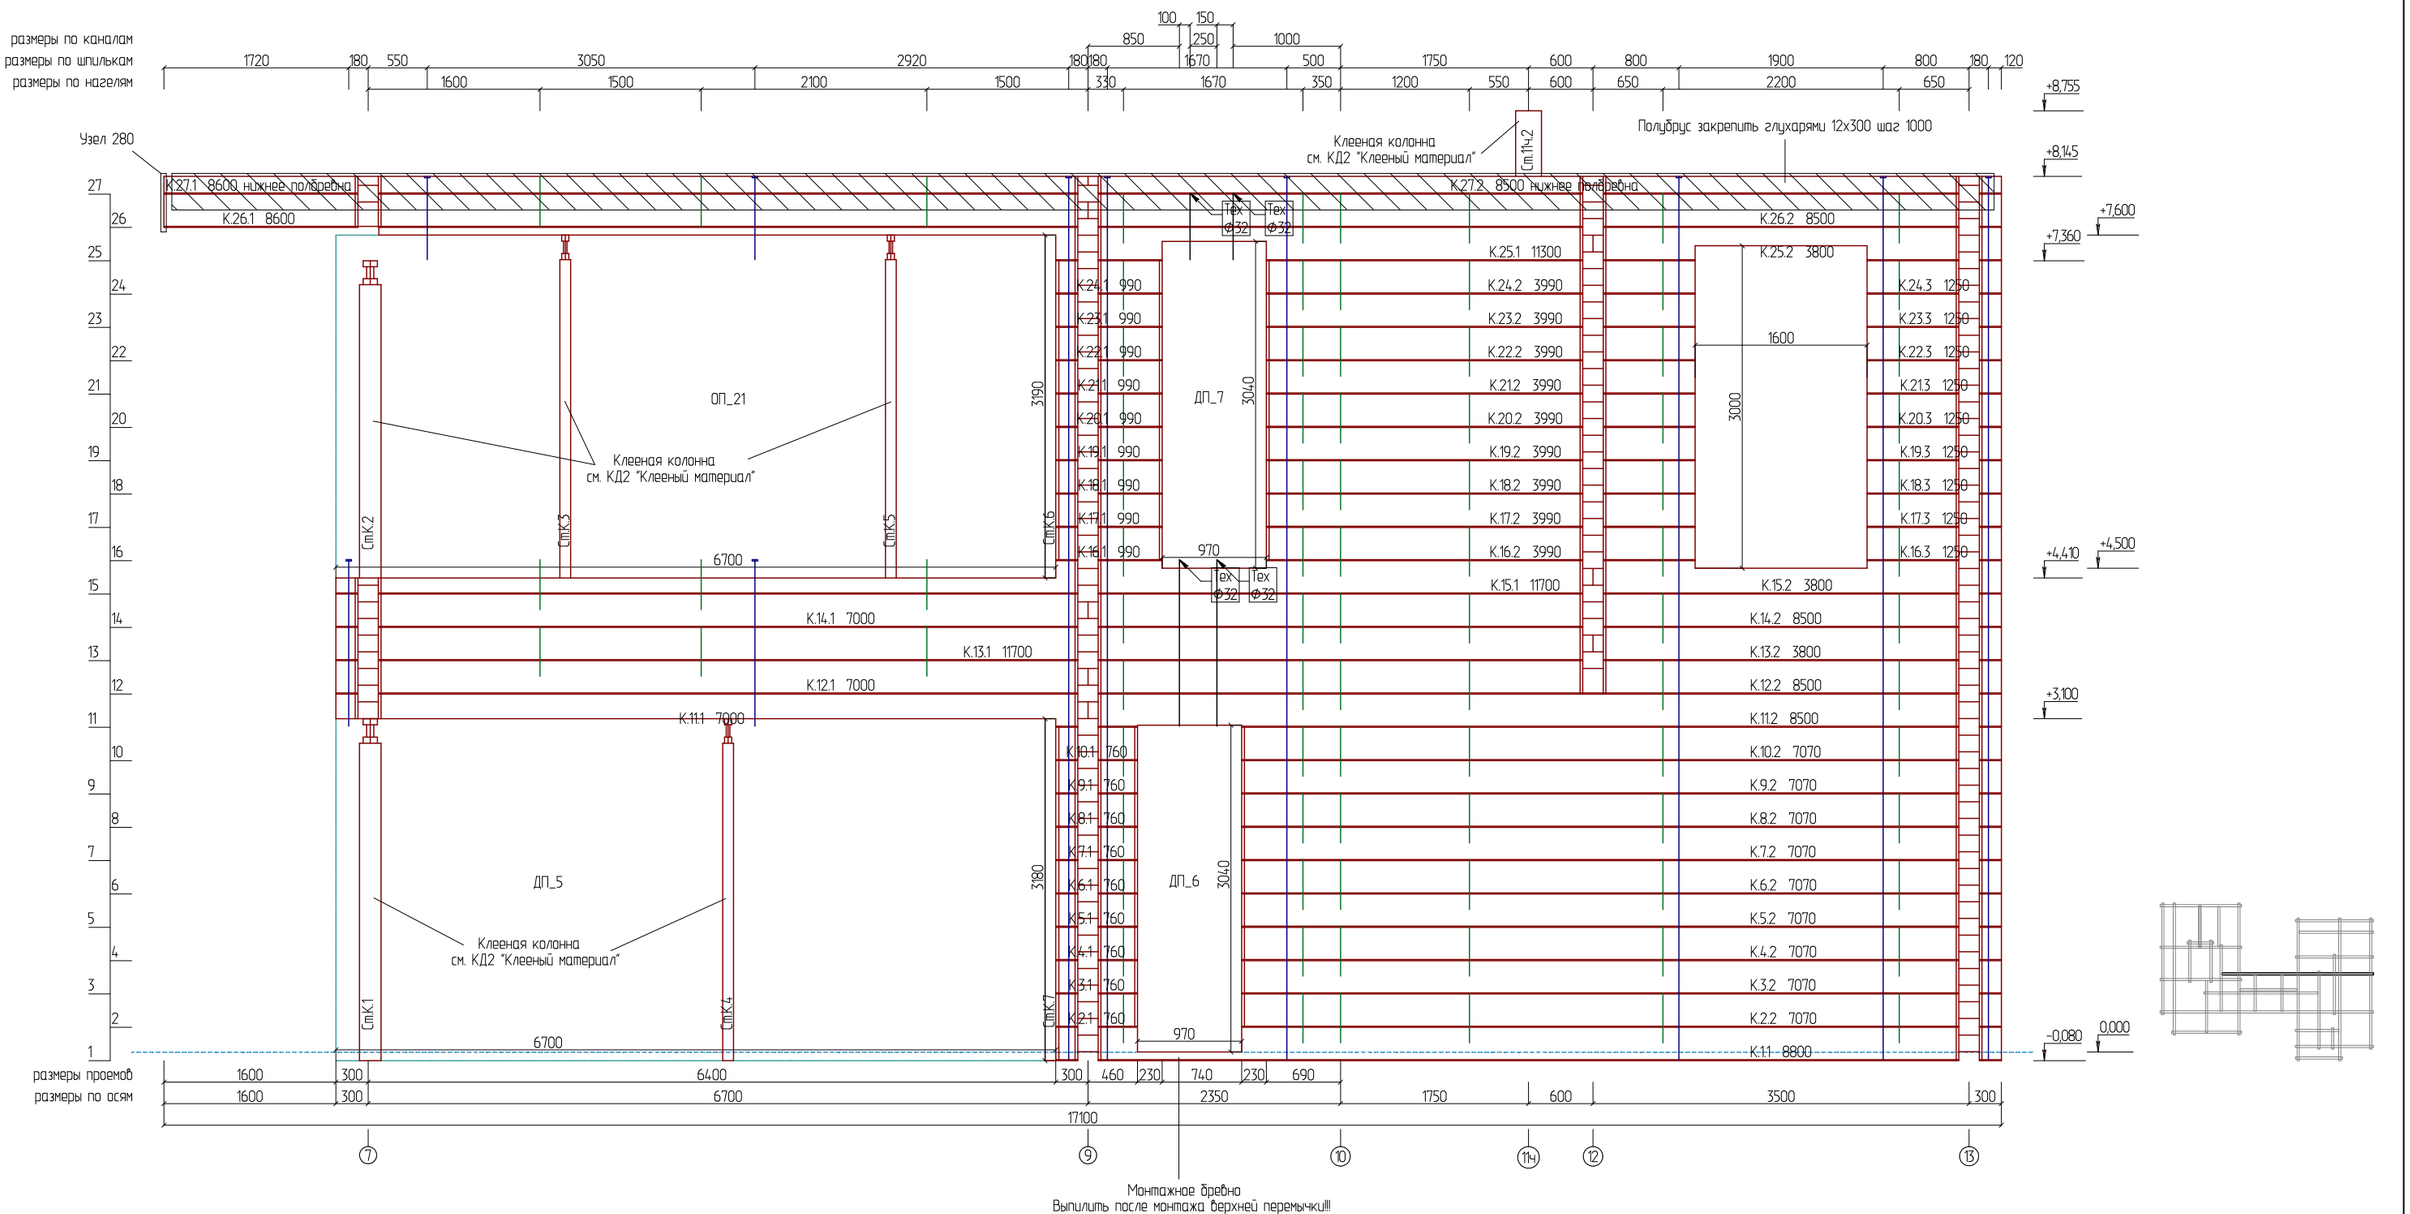


						- АС
Изм.	Кол. уч.	Лист	№ док.	Подпись	Дата	
Разработал		Москалюк А.				Берта Ромарио
Проверил		Баннов Е.				
Конструктор						
ГИП		Баннов Е.				Развертка по стене (оси) К
Н.контроль						


Стадия	Лист	Листов
Р	30	

ООО "Строй Хауз"

Развертка по стене (оси) Кч

Стянуть между собой полнорезьбовыми шурупами 8х400 по узлу Б

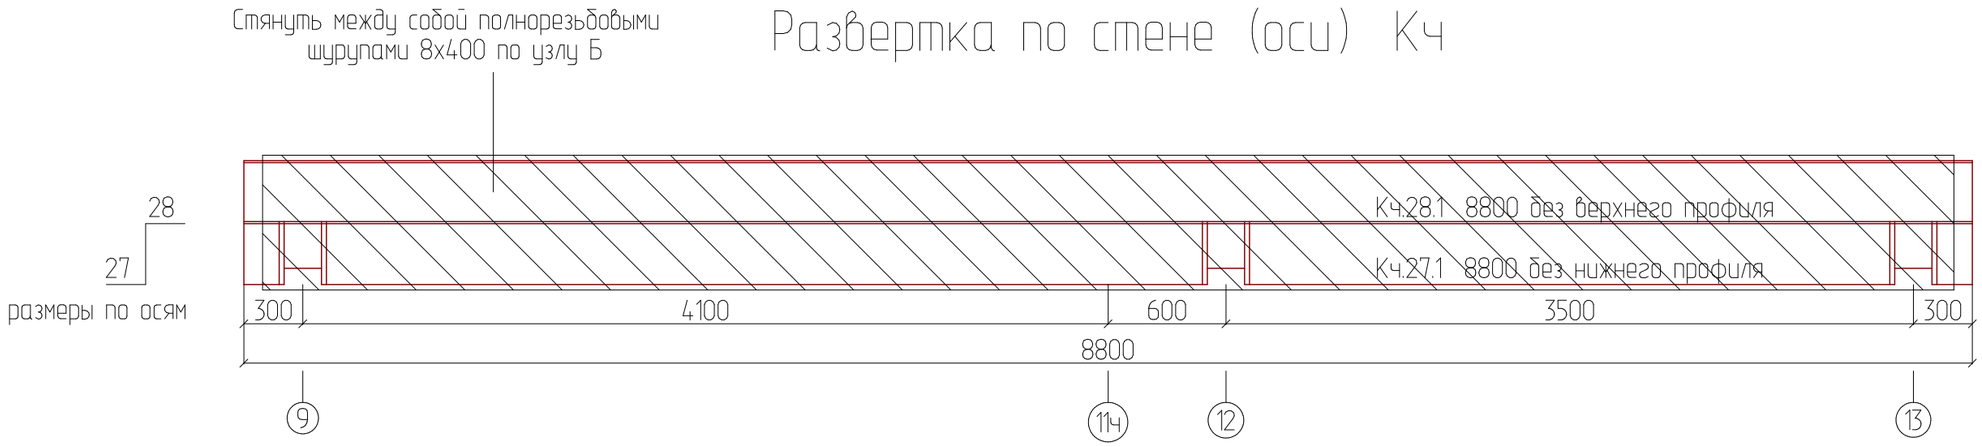

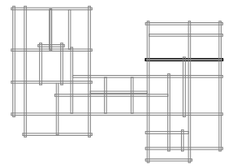


						- АС
Изм.	Кол. уч.	Лист	№ док.	Подпись	Дата	
Разработал		Москалюк А.				Берта Ромарио
Проверил		Баннов Е.				
Конструктор						
ГИП		Баннов Е.				Развертка по стене (оси) Кч
Н.контроль						

Стадия	Лист	Листов
Р	31	

ООО "Строй Хауз"

Развертка по стене (оси) Л

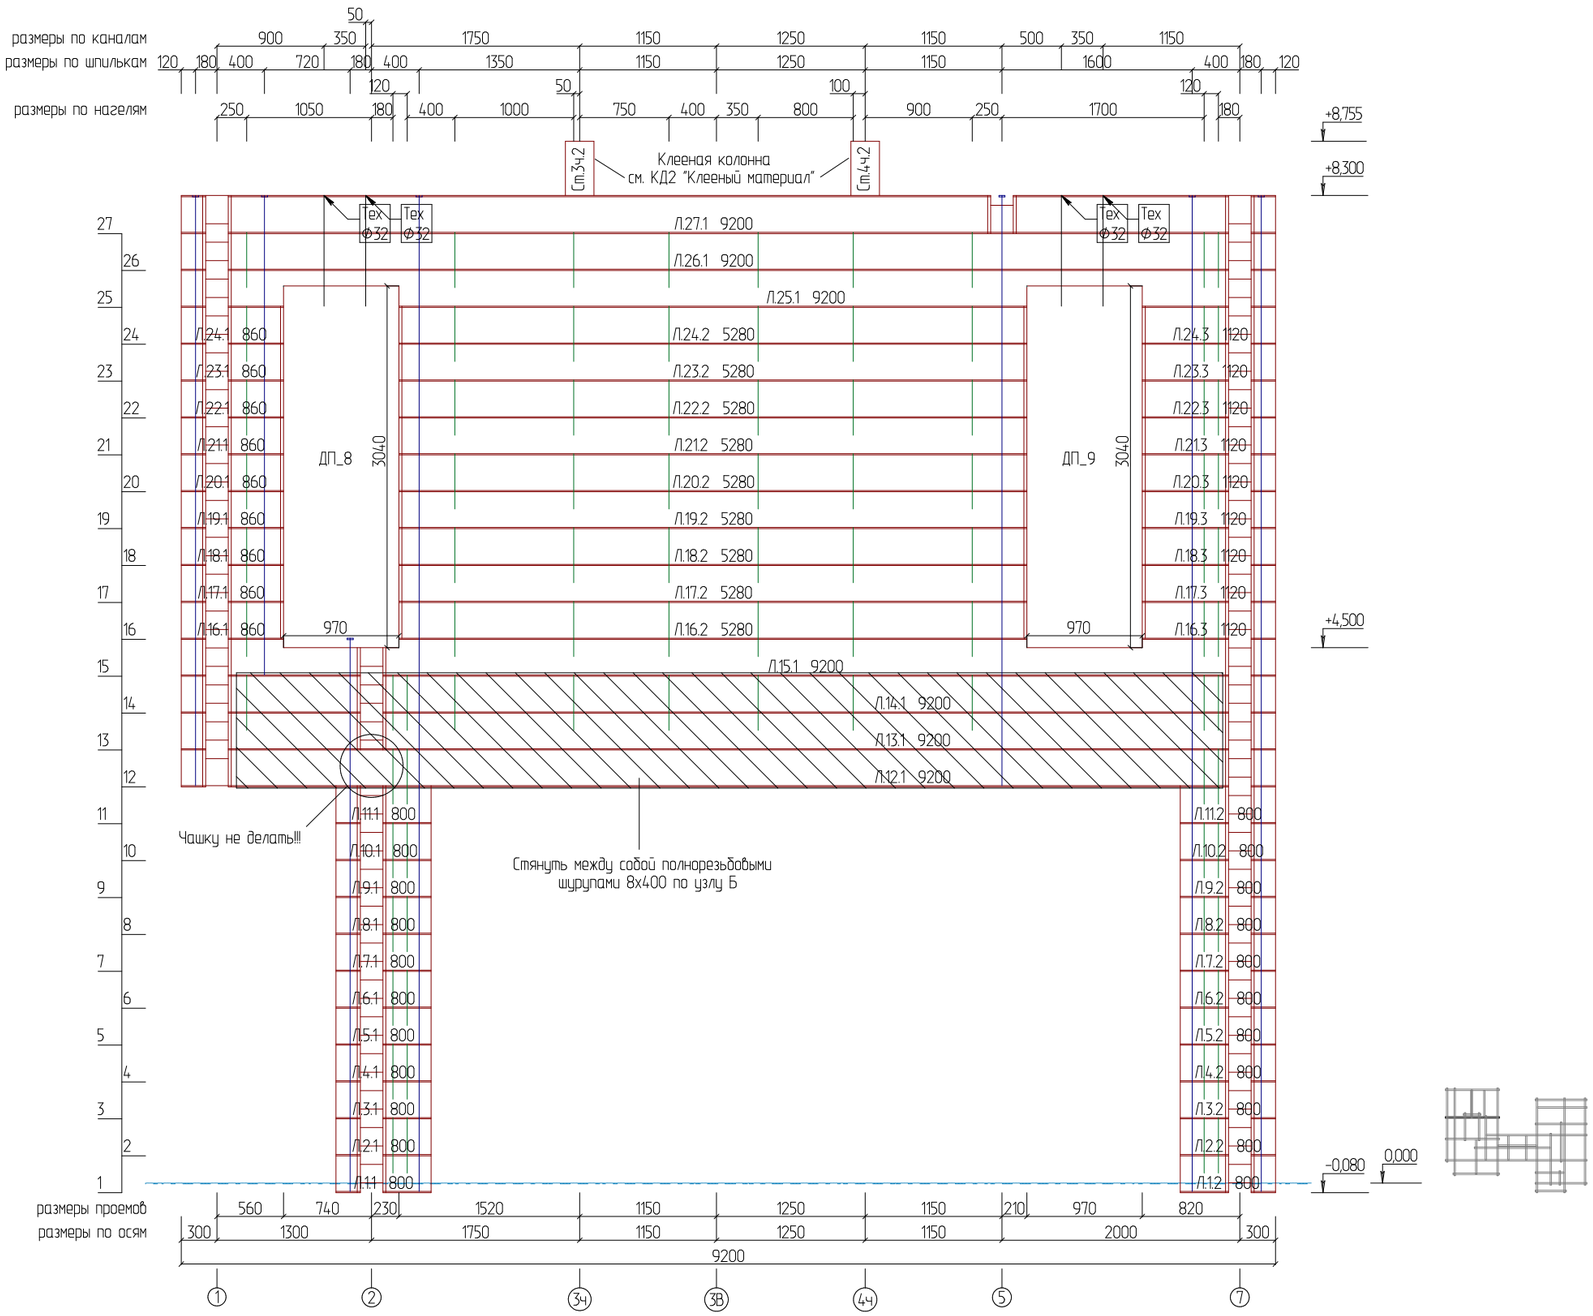


						- АС
Изм.	Кол. уч.	Лист	№ док.	Подпись	Дата	
Разработал		Москалюк А.				Берта Ромарио
Проверил		Баннов Е.				
Конструктор						
ГИП		Баннов Е.				Развертка по стене (оси) Л
Н.контроль						

Стадия	Лист	Листов
Р	32	

ООО "Строй Хауз"

Развертка по стене (оси) Лч

Полубрус закрепить глухарями 12х300 шаг 1000

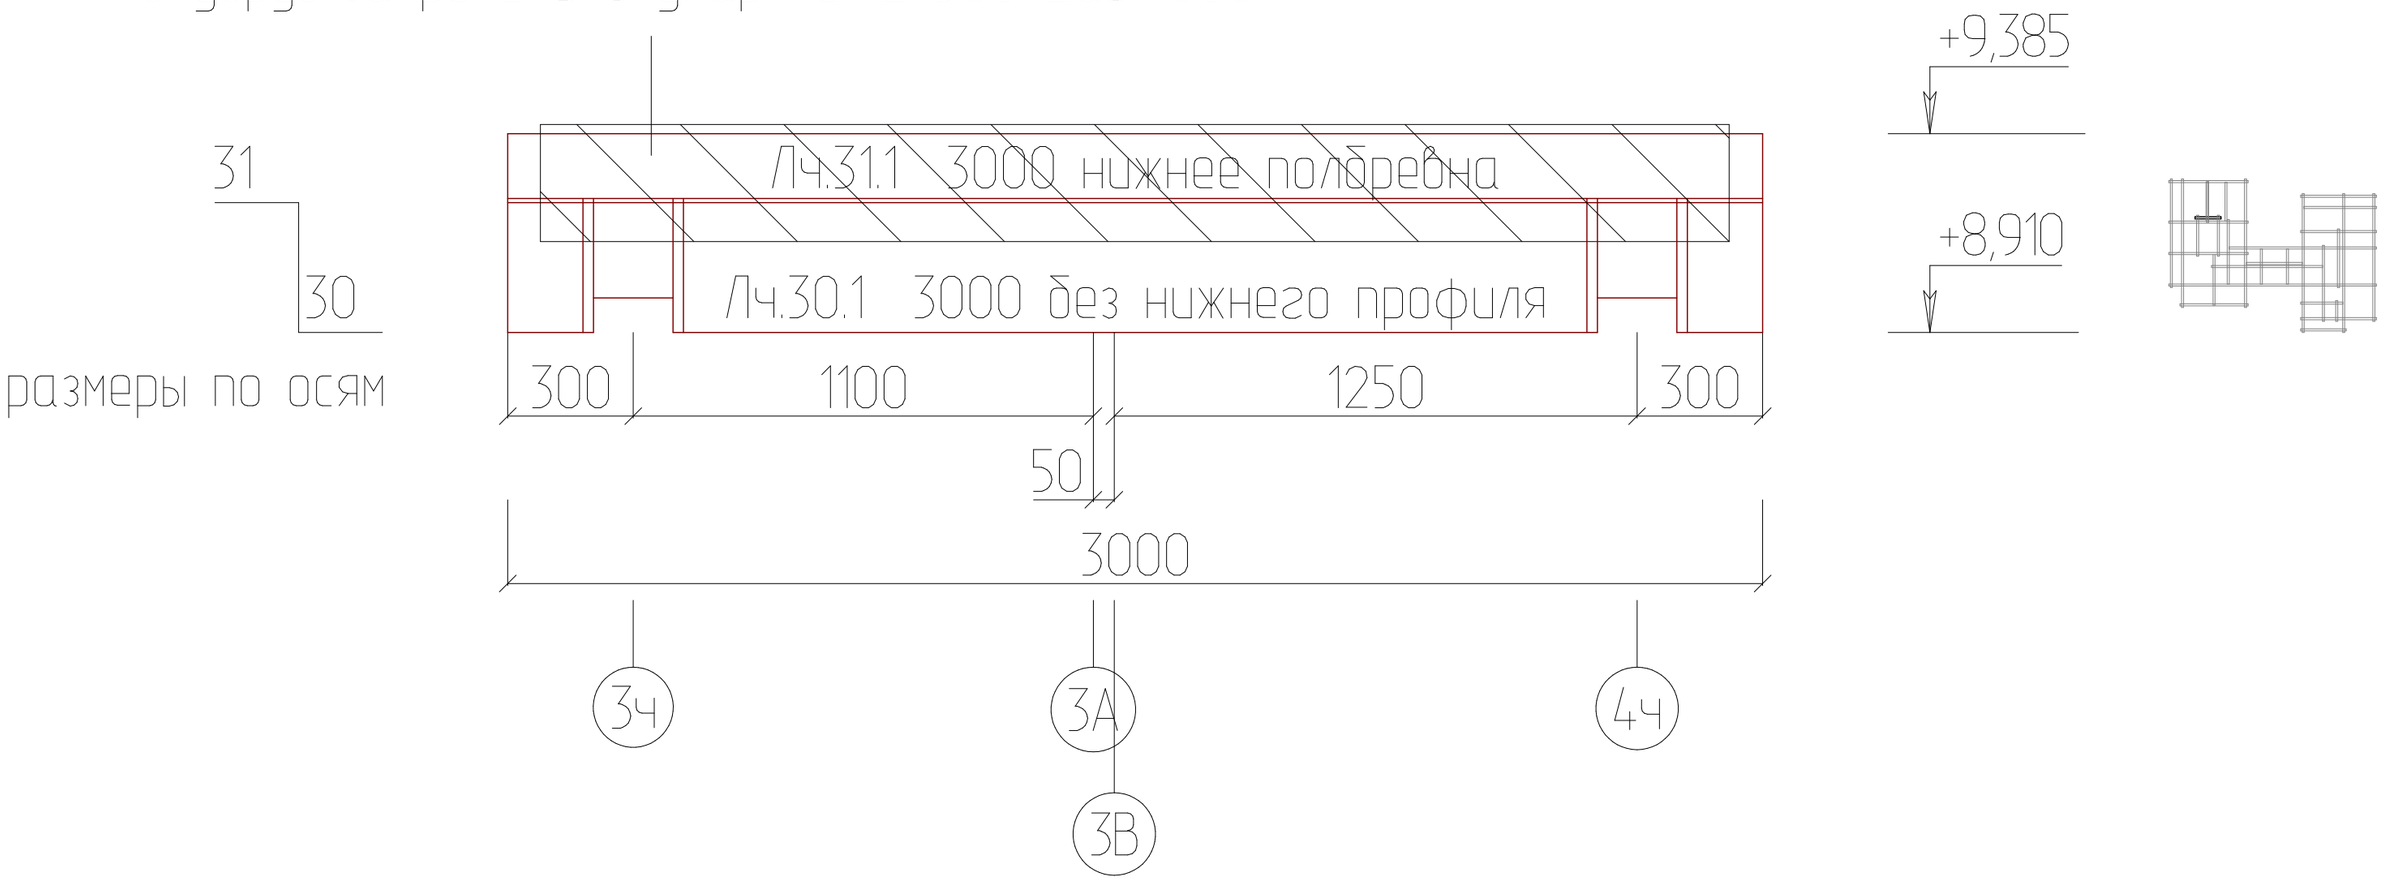


						- АС
Изм.	Кол. уч.	Лист	№ док.	Подпись	Дата	
Разработал		Москалюк А.				Берта Ромарио
Проверил		Баннов Е.				
Конструктор						
ГИП		Баннов Е.				Развертка по стене (оси) Лч
Н.контроль						

Стадия	Лист	Листов
Р	33	

ООО "Строй Хауз"

Развертка по стене (оси) М

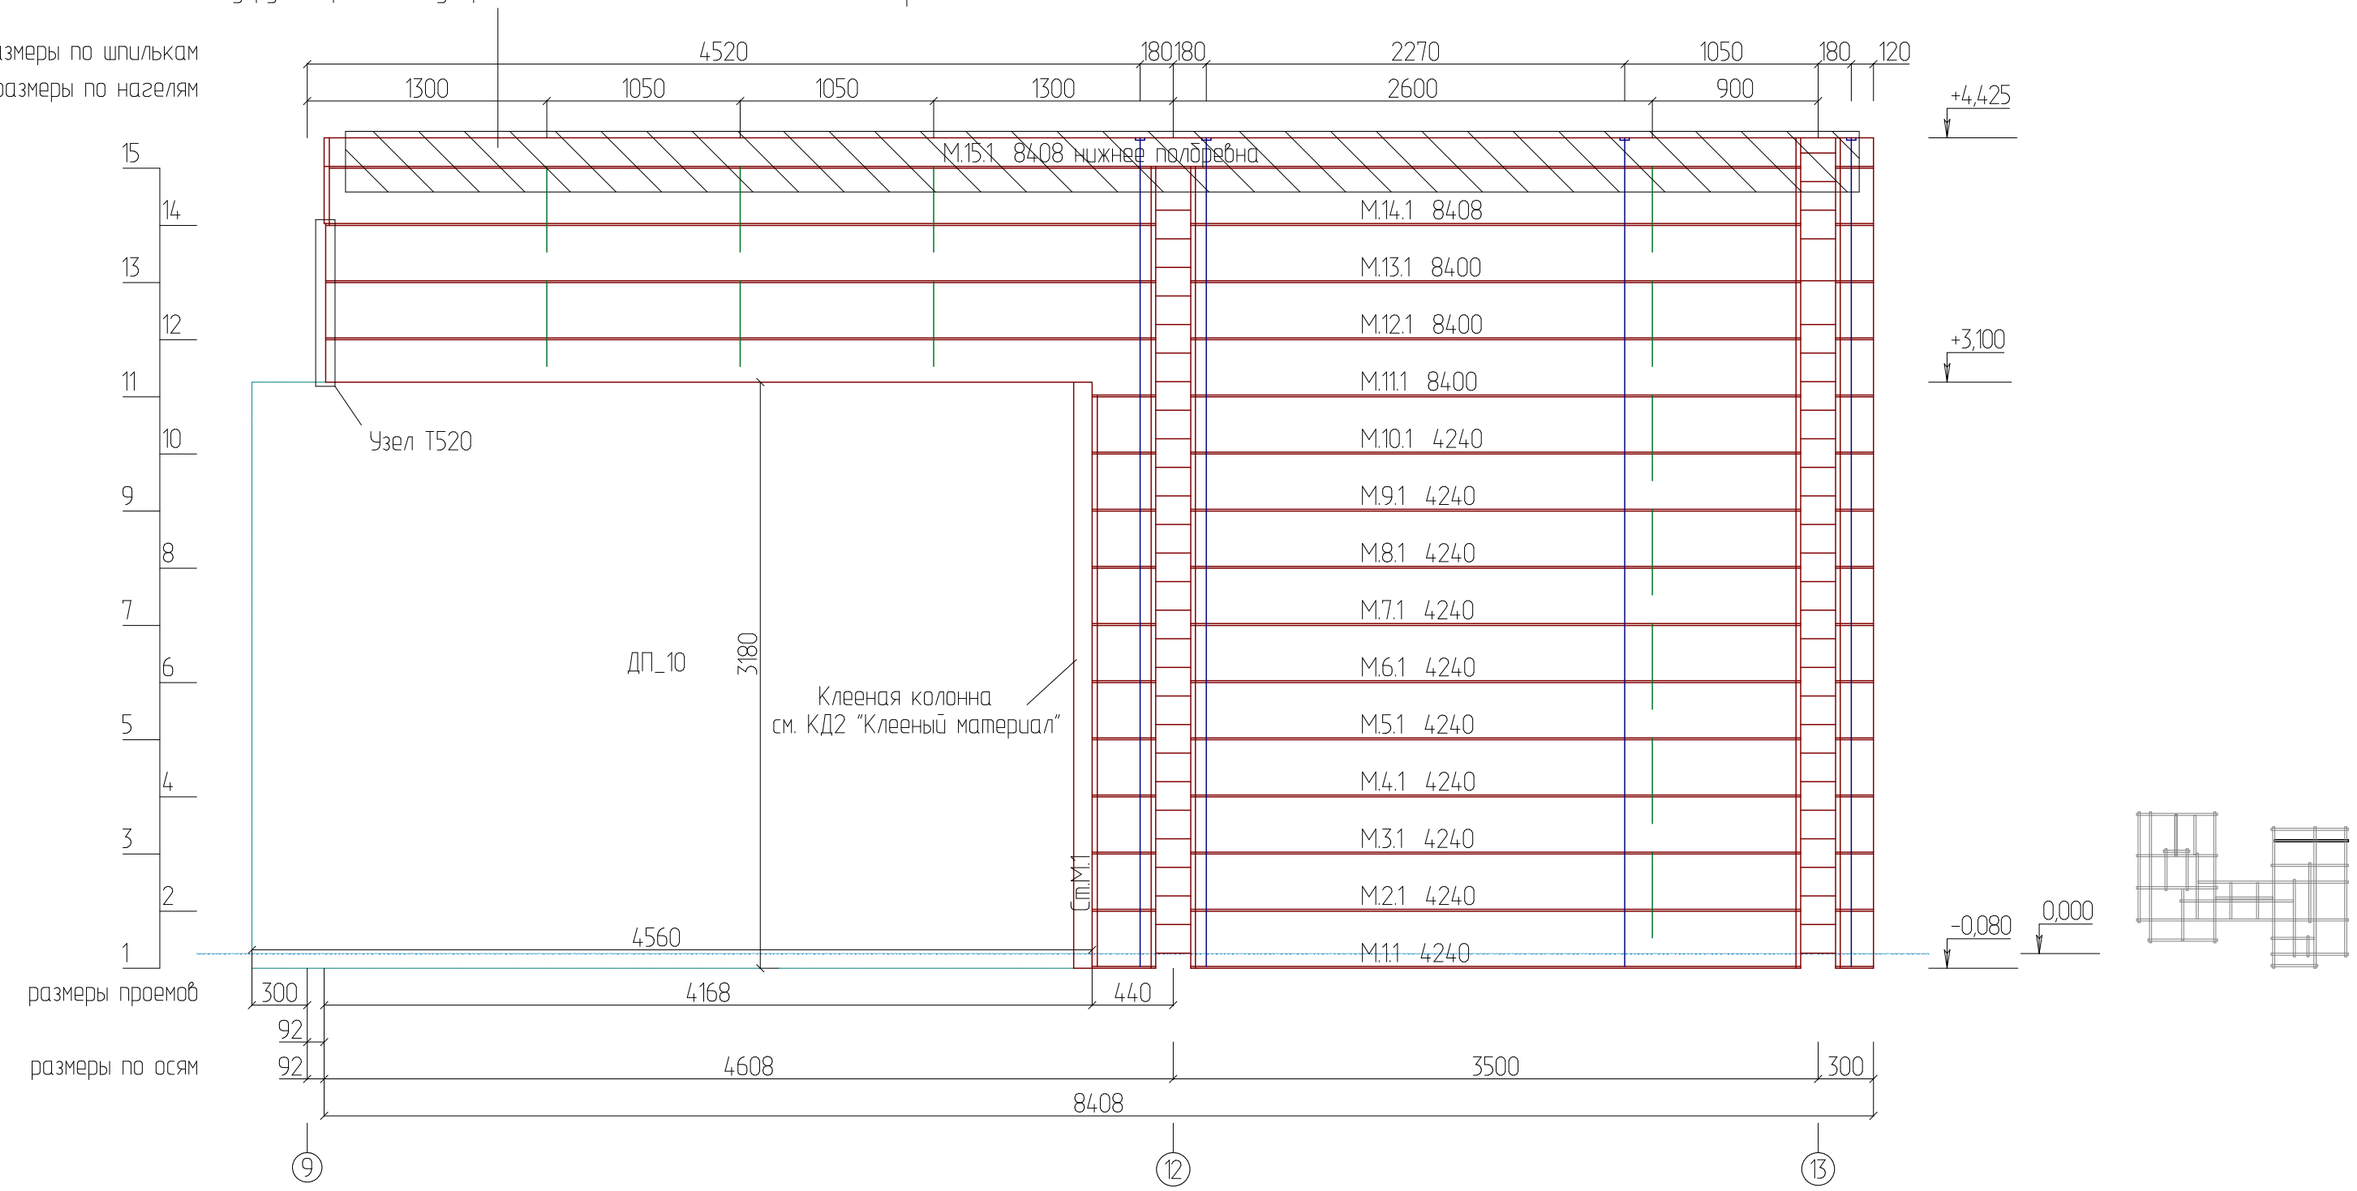


						- АС
Изм.	Кол. уч.	Лист	№ док.	Подпись	Дата	
Разработал		Москалюк А.				Берта Ромарио
Проверил		Баннов Е.				
Конструктор						
ГИП		Баннов Е.				
Н.контроль						Развертка по стене (оси) М

Стадия	Лист	Листов
Р	34	

ООО "Строй Хауз"


Развертка по стене (оси) Н

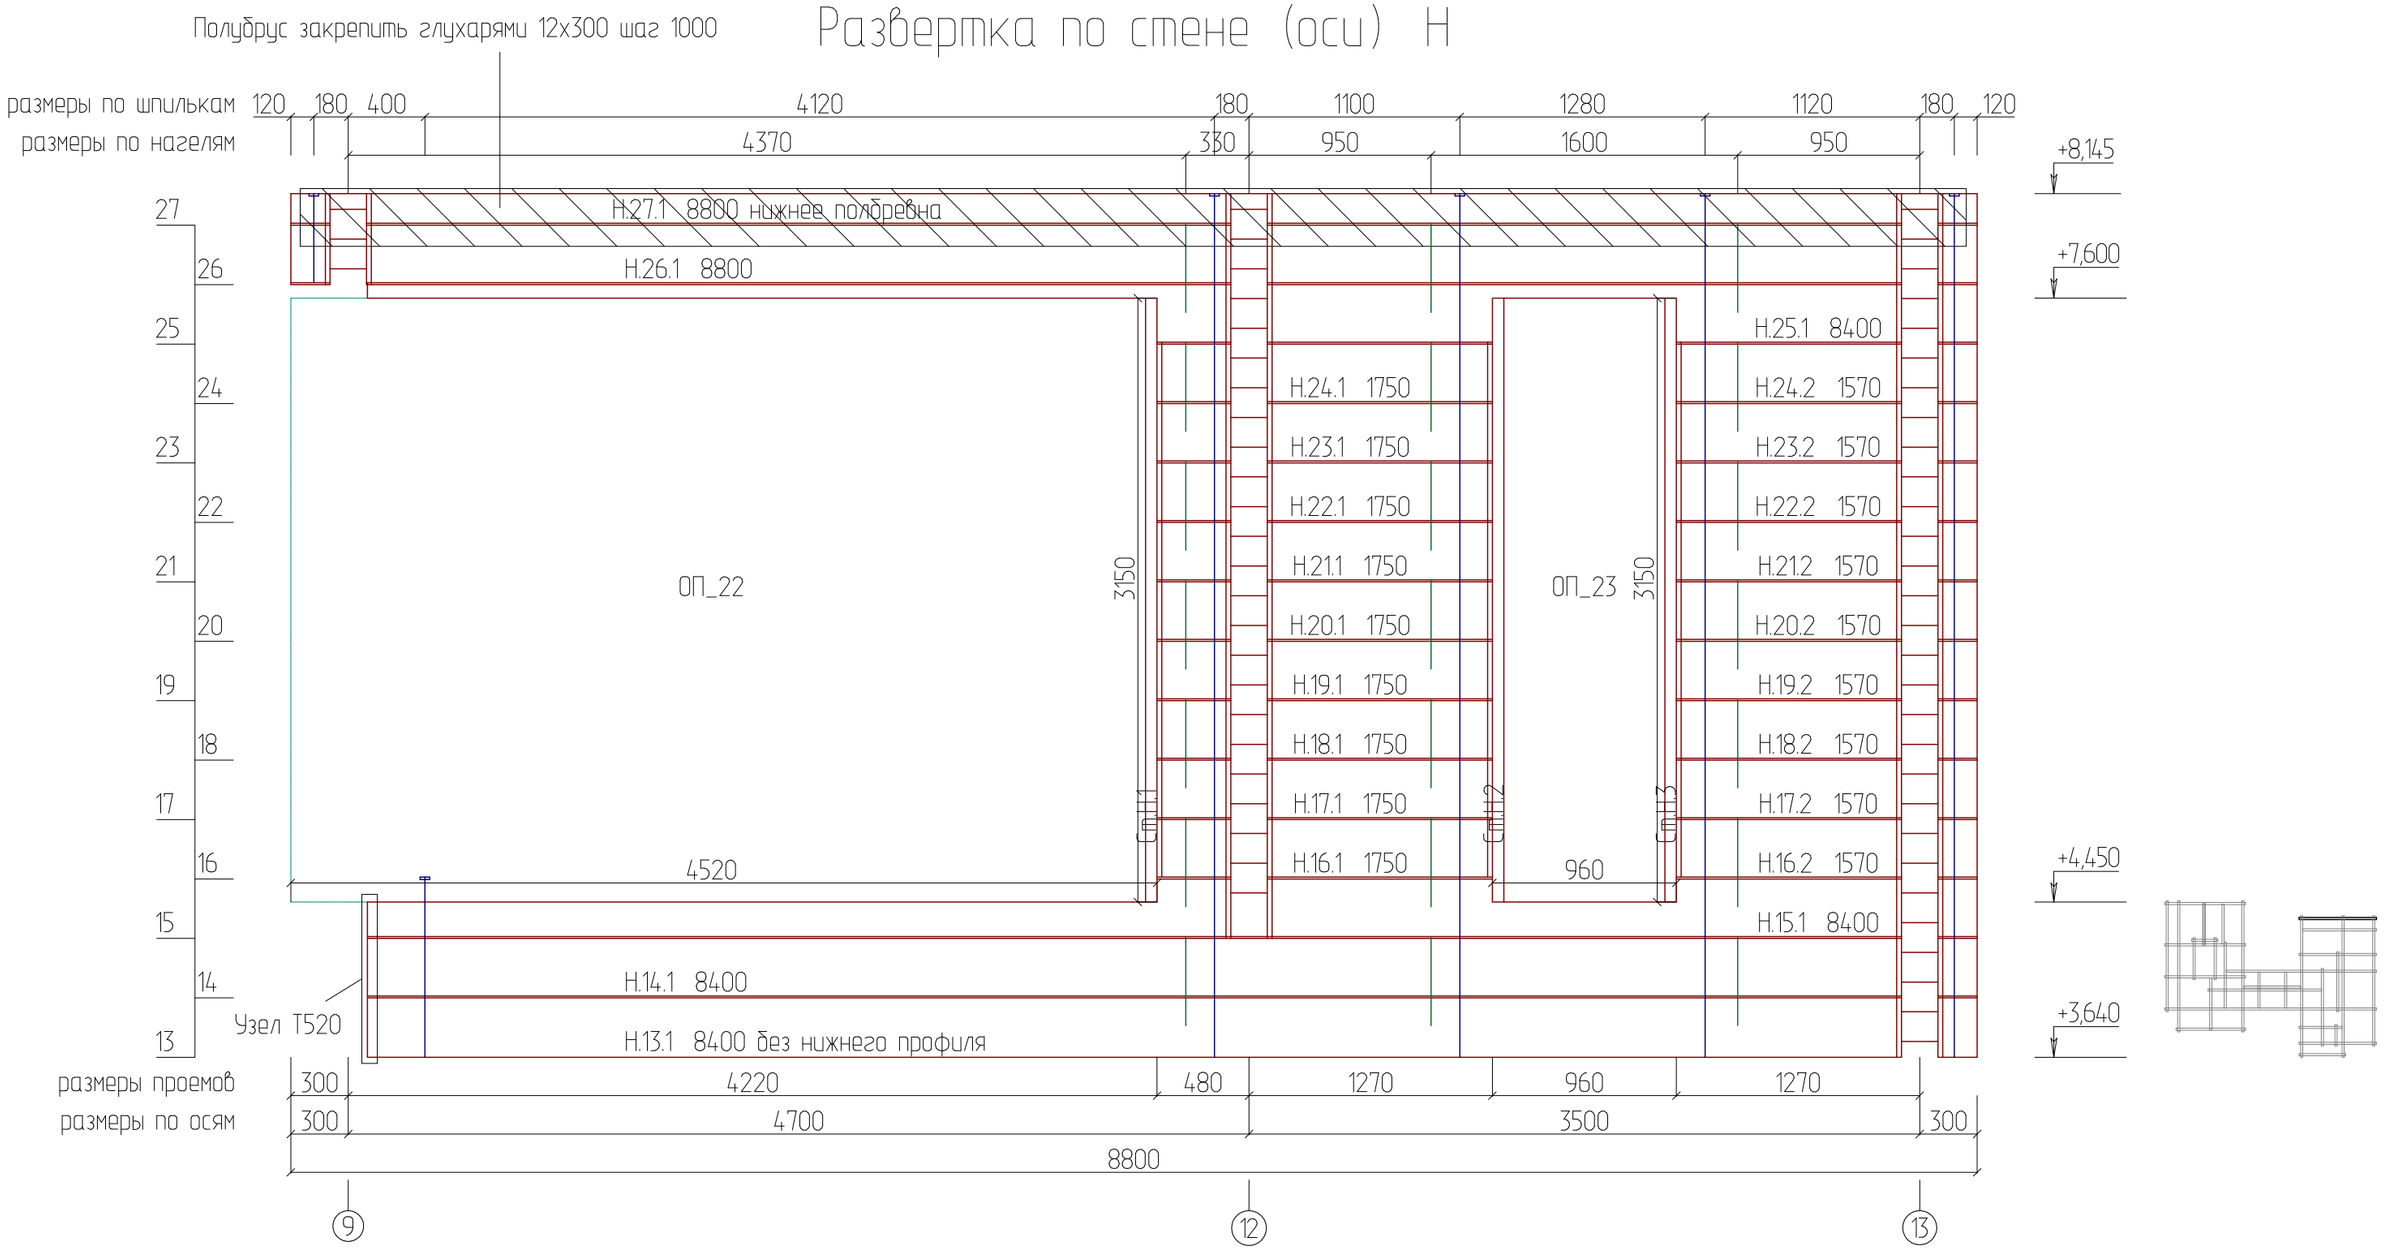

						- АС
Изм.	Кол. уч.	Лист	№ док.	Подпись	Дата	

Разработал	Москалюк А.			Берта Ромарио	Стадия: Р; Лист: 35; Листов:
Проверил	Баннов Е.				
Конструктор					
ГИП	Баннов Е.			Развертка по стене (оси) Н	ООО "Строй Хауз"
Н.контроль					

Развертка по стене (оси) П

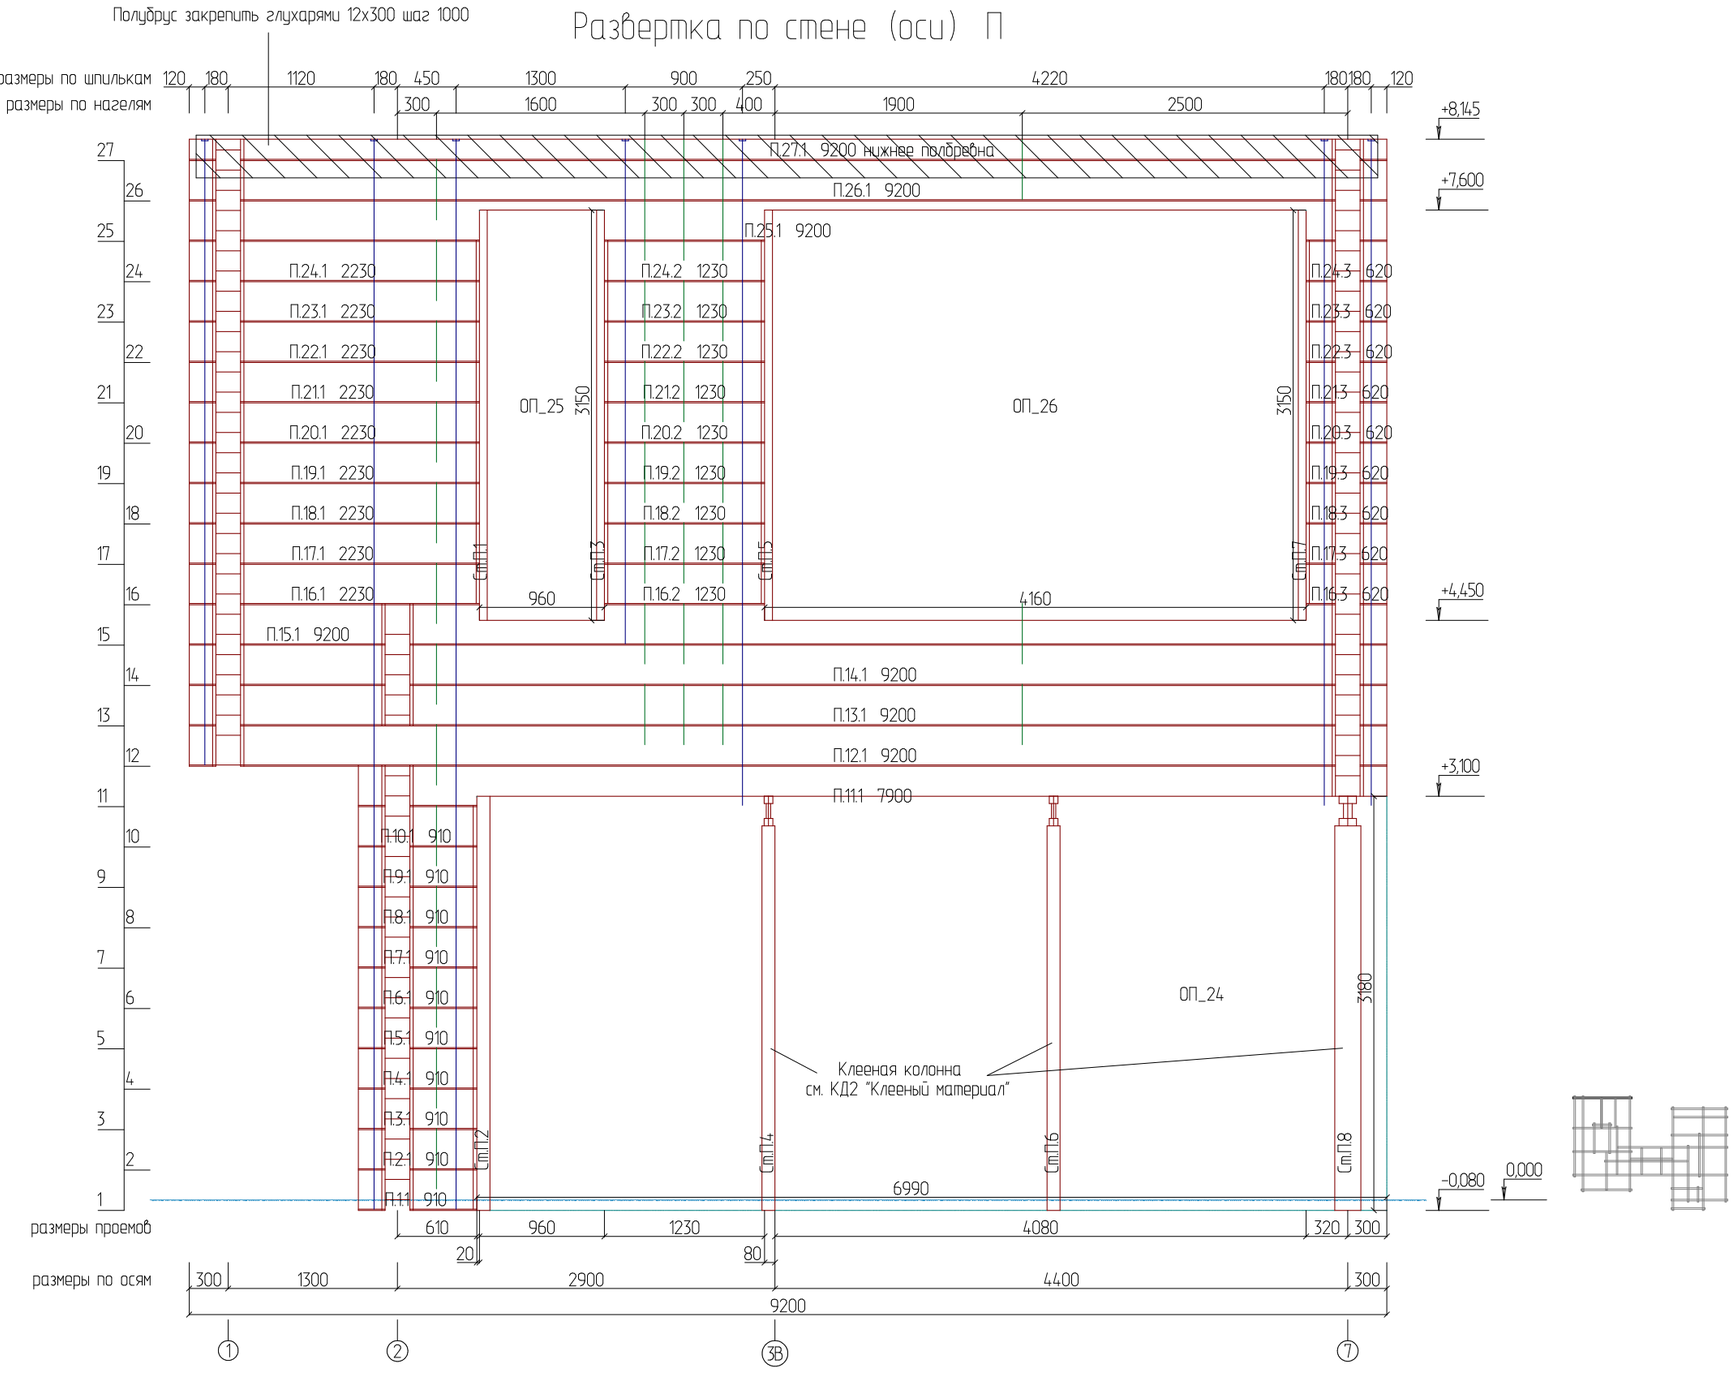

						- АС
Изм.	Кол. уч.	Лист	№ док.	Подпись	Дата	
Разработал		Москалюк А.				Берта Ромарио
Проверил		Баннов Е.				
Конструктор						
ГИП		Баннов Е.				
Н.контроль						Развертка по стене (оси) П

Стадия	Лист	Листов
Р	36	

ООО "Строй Хауз"

Спецификация материалов КД1.Разбрусовка

Поз.	Обозначение	Наименование	Кол.	Ед.изм.	Приме-чание
1		Брус клееный 320х240	228.53	м3	
2		Нагель ø32	636	м\пог	
3		Глахарь 12х300	124	шт	
4		Шайба М12	124	шт	
5		Шуруп полнорезьбовой 8х400	300	шт	
6		Т-образный кронштейн 240мм алюминий	2	шт	
7		Т-образный кронштейн 280мм алюминий	1	шт	
8		Т-образный кронштейн 320мм алюминий	8	шт	
9		Т-образный кронштейн 400мм алюминий	3	шт	
10		Т-образный кронштейн 520мм алюминий	4	шт	
11		Гвоздь ершеный 4,2х90	5	кг	
12		Штифт гладкий STA 12X130 мм потайной	170	шт	
13		Аватерм	104	м2	
14		Уплотнитель ПСУЛ	#TYPE	м\пог	
15		Скоба 120 мм	108	шт	
16		Гайка М12	#TYPE	шт	
17		Шайба М12	#TYPE	шт	
18		Шпилька М12	743	м\пог	
19		Соеденительная муфта М12	646	шт	
20		Состав для обработки торцов бруса	49	л	

						291-КД1	
						Московская область, Истринский район	
Изм.	Кол. уч.	Лист	№ док.	Подп.	Дата		
Констр.		Москалюк А.			29.09.26	Разбрусовка	Стадия: Р; Лист: ; Листов:
Провер.		Баннов Е.			29.09.26		
ГИП		Баннов Е.			29.09.26	Спецификация	ООО "Строй Хауз"

Формат А3