ООО "Строй Хауз"

Московская обл., Истринский р-н, д. Веледниково, ул. Живописная, д. 25

Берта Ромарио

по адресу: Московская область, Истринский район

Индивидуальный жилой дом

РАБОЧАЯ ДОКУМЕНТАЦИЯ

Раздел КД2.Клееный материал

(Конструкции деревянные)

291-КД2

Конструктор	Москалюк А.
Проверил	Баннов Е.
ГИП	Баннов Е.



г. Москва 2026г.

Согласовано

Взам. инв. №

Подп. и дата

Инв. № подл.

Формат А4

Ведомость рабочих чертежей основного комплекта

Лист	Наименование	Примечание
1	Ведомость рабочих чертежей	А3
2	Спецификация	А3
3	План клееных конструкций первого этажа	А3
4	План клееных конструкций второго этажа	А3
5	План диагональных стропил	А3
6	Узлы Ст1, Ст2	А3
7	Узлы Ст3..Ст5	А3
8	Узлы Ст6..Ст8	А3
9	Узлы Ст9, Ст10	А3
10	Узлы Ст11, Ст12	А3
11	Узлы Ст13..Ст15	А3
12	Узел А	А3
13	Узлы Ен1..Ен3	А3
14	Узел Ен4	А3
15	Спецификация	А3

Ведомость ссылочных и прилагаемых документов

Обозначение	Наименование	Примечание
СП 64. 13330.2017	"Деревянные конструкции"	
СП 20.13330.2016	"Нагрузки и воздействия"	
СП 70.13330.2012	"Несущие и ограждающие конструкции"	
ГОСТ 20022.6-93	"Защита древесины"	

ОБЩИЕ ДАННЫЕ

1. Данный комплект чертежей выполнен на основании архитектурно-планировочных решений;
2. Строительная площадка расположена в I ветровом и III снеговом районах с нормативной глубиной сезонного промерзания:
- глина или суглинок 1,03м;
- супесь, пески пылеватые или мелкие – 1,25м;
- песок средней крупности, крупный или гравелистый – 1,34м;
3. За относительную отметку 0,000 принят уровень чистого пола 1 этажа;
4. Посадку сооружения смотри чертежи генплана;
5. Отклонения в размерах конструкций не должны превышать предельных значений, приведенных в табл.4.11 СП 70.13330.2012 "Несущие и ограждающие конструкции ";
6. Все деревянные конструкции кроме клееных защитить антисептиком "Зотекс". Средство наносить в 2-3 приёма с интервалом 20-30 минут, и суммарным расходом не менее 0,3л/м2. Средством "Зотекс" обрабатывать древесину, очищенную от грязи, коры и других покрытий кистью, валиком, распылением, вымачиванием или другими способами по ГОСТ 20022.6-93. Обработку проводить при положительной температуре. Не обрабатывать мёрзлую древесину;
7. Все стыки пароизоляции проклеить скотчем Finka Inside Tape. К стенам крепить скобой степлера, сплошным швом и проклеить скотчем Finka Inside Tape;
8. Все соединения в зоне утепления уплотнить с помощью Аватерм;
9. Чертежи рассматривать и применять в соответствии с приложением к договору;
10. Торцы всех балок и колонн предварительно обработать клеем ПВА.

Ведомость основных комплектов рабочих чертежей

Обозначение	Наименование	Примечание
АР	Архитектурно-планировочное решение	
КЖ0	Фундамент	
КД1	Разбрусовка	
КД2	Клееный материал	
КД3	Подвенечный оклад	
КД4	Межэтажные перекрытия	
КД5	Кровля	
КД6	Каркасные перегородки	

Согласовано

Взам. инв. №

Подп. и дата

Инв. № подл.

Изм.	Кол. уч.	Лист	№ док.	Подп.	Дата
Констр.		Москалюк А.			29.09.26
Провер.		Баннов Е.			29.09.26
ГИП		Баннов Е.			29.09.26

291-КД2

Московская область, Истринский район

Клееный материал

Стадия	Лист	Листов
Р	1	15

Ведомость рабочих чертежей

ООО "Строй Хауз"

Формат А3

Спецификация клееных элементов (колонны)


Поз.	Маркировка	Наименование	Габариты, мм					Кол-во	Объем, м³	Примечание
1	К1	Колонна клееная	140	x	140	x	3800	1	0,07	Каркас, 1-й этаж, ось 11
2	К2	Колонна клееная	140	x	140	x	3700	2	0,15	Каркас, 2-й этаж, оси 3 и 4
3	К3	Колонна клееная	140	x	140	x	3400	1	0,07	Каркас, 2-й этаж, ось Е
4	К4	Колонна клееная	140	x	140	x	3400	1	0,07	Каркас, 1-й этаж, ось 6
5	К5	Колонна клееная	140	x	140	x	3250	1	0,06	Каркас, 1-й этаж, ось 7
6	К6	Колонна клееная	140	x	140	x	3700	1	0,07	Каркас, 1-й этаж, ось 11
7	К7	Колонна клееная	140	x	140	x	3550	2	0,14	Каркас, 1-й этаж, ось 12
8	К8	Колонна клееная	200	x	520	x	3800	1	0,4	Крыльцо
9	К9	Колонна клееная	120	x	240	x	3800	1	0,11	Пристенная колонна, ось Г
10	К10	Колонна клееная	120	x	240	x	3550	1	0,1	Пристенная колонна, ось Б
11	К11	Колонна клееная	120	x	240	x	8000	2	0,46	Пристенная колонна, ось 13
12	К12	Колонна клееная	120	x	240	x	3400	3	0,29	Пристенная колонна, ось 2
13	К13	Колонна клееная	120	x	240	x	3700	1	0,11	Пристенная колонна, ось 2
14	К14	Колонна клееная	120	x	240	x	3900	1	0,11	Пристенная колонна, ось В
15	К15	Колонна клееная	140	x	140	x	3250	1	0,06	Каркас, 2-й этаж, ось И
16	К16	Колонна клееная	140	x	140	x	3550	1	0,07	Каркас, 2-й этаж, ось 5
17	К17	Колонна клееная	140	x	140	x	3400	1	0,07	Каркас, 2-й этаж, ось Е
18	К18	Колонна клееная	200	x	200	x	500	5	0,1	Чердак
19	К19	Колонна клееная	200	x	200	x	650	2	0,05	Чердак
20	Кн1	Колонна клееная	240	x	240	x	3200	2	0,37	Окна, 1-й этаж, оси М и П
21	Кн2	Колонна клееная	200	x	520	x	3200	1	0,33	Окна, 1-й этаж, ось К
22	Кн3	Колонна клееная	100	x	240	x	3200	10	0,77	Окна, 1-й этаж, оси Е, К, М, П и 7
23	Кн4	Колонна клееная	100	x	240	x	3150	4	0,3	Окна, 2-й этаж, оси Е и К
24	Кн5	Колонна клееная	240	x	240	x	3150	1	0,18	Окна, 2-й этаж, ось Н
25	Кн6	Колонна клееная	200	x	520	x	3150	1	0,33	Окна, 2-й этаж, ось К
26	Кн7	Колонна клееная	200	x	200	x	3150	1	0,13	Окна, 2-й этаж, ось 1
27	Кн8	Колонна клееная	200	x	200	x	1350	1	0,05	Окна, 2-й этаж, ось 1
ИТОГО								50	5,02	

Спецификация клееных элементов (балки)

Поз.	Наименование	Габариты, мм					Кол-во	Объем, м³	Примечание
Бк1	Балка клееная	160	x	520	x	7100	1	0,59	Снаружи стены В
Бк2	Балка клееная	160	x	520	x	8000	1	0,67	Снаружи стены Н
Бд1	Балка клееная	200	x	280	x	8300	3	1,39	Диагональное стропило
Бд2	Балка клееная	200	x	280	x	8010	3	1,35	Диагональное стропило
Бд3	Балка клееная	200	x	240	x	7360	3	1,06	Диагональное стропило
Бд4	Балка клееная	200	x	200	x	5180	4	0,83	Диагональное стропило
Бд5	Балка клееная	200	x	200	x	5470	3	0,66	Диагональное стропило
Бд6	Балка клееная	200	x	200	x	2740	1	0,11	Диагональное стропило
Бд7	Балка клееная	200	x	280	x	1150	1	0,06	Диагональное стропило
ИТОГО							20	6,72	

Изм.	Кол. уч.	Лист	№ док.	Подп.	Дата	291-КД2			
						Московская область, Истринский район			
Констр.		Москалюк А.			29.09.26	Клееный материал	Стадия	Лист	Листов
Провер.		Баннов Е.			29.09.26		Р	2	
ГИП		Баннов Е.			29.09.26	Спецификация	ООО "Строй Хауз"		

Формат А3

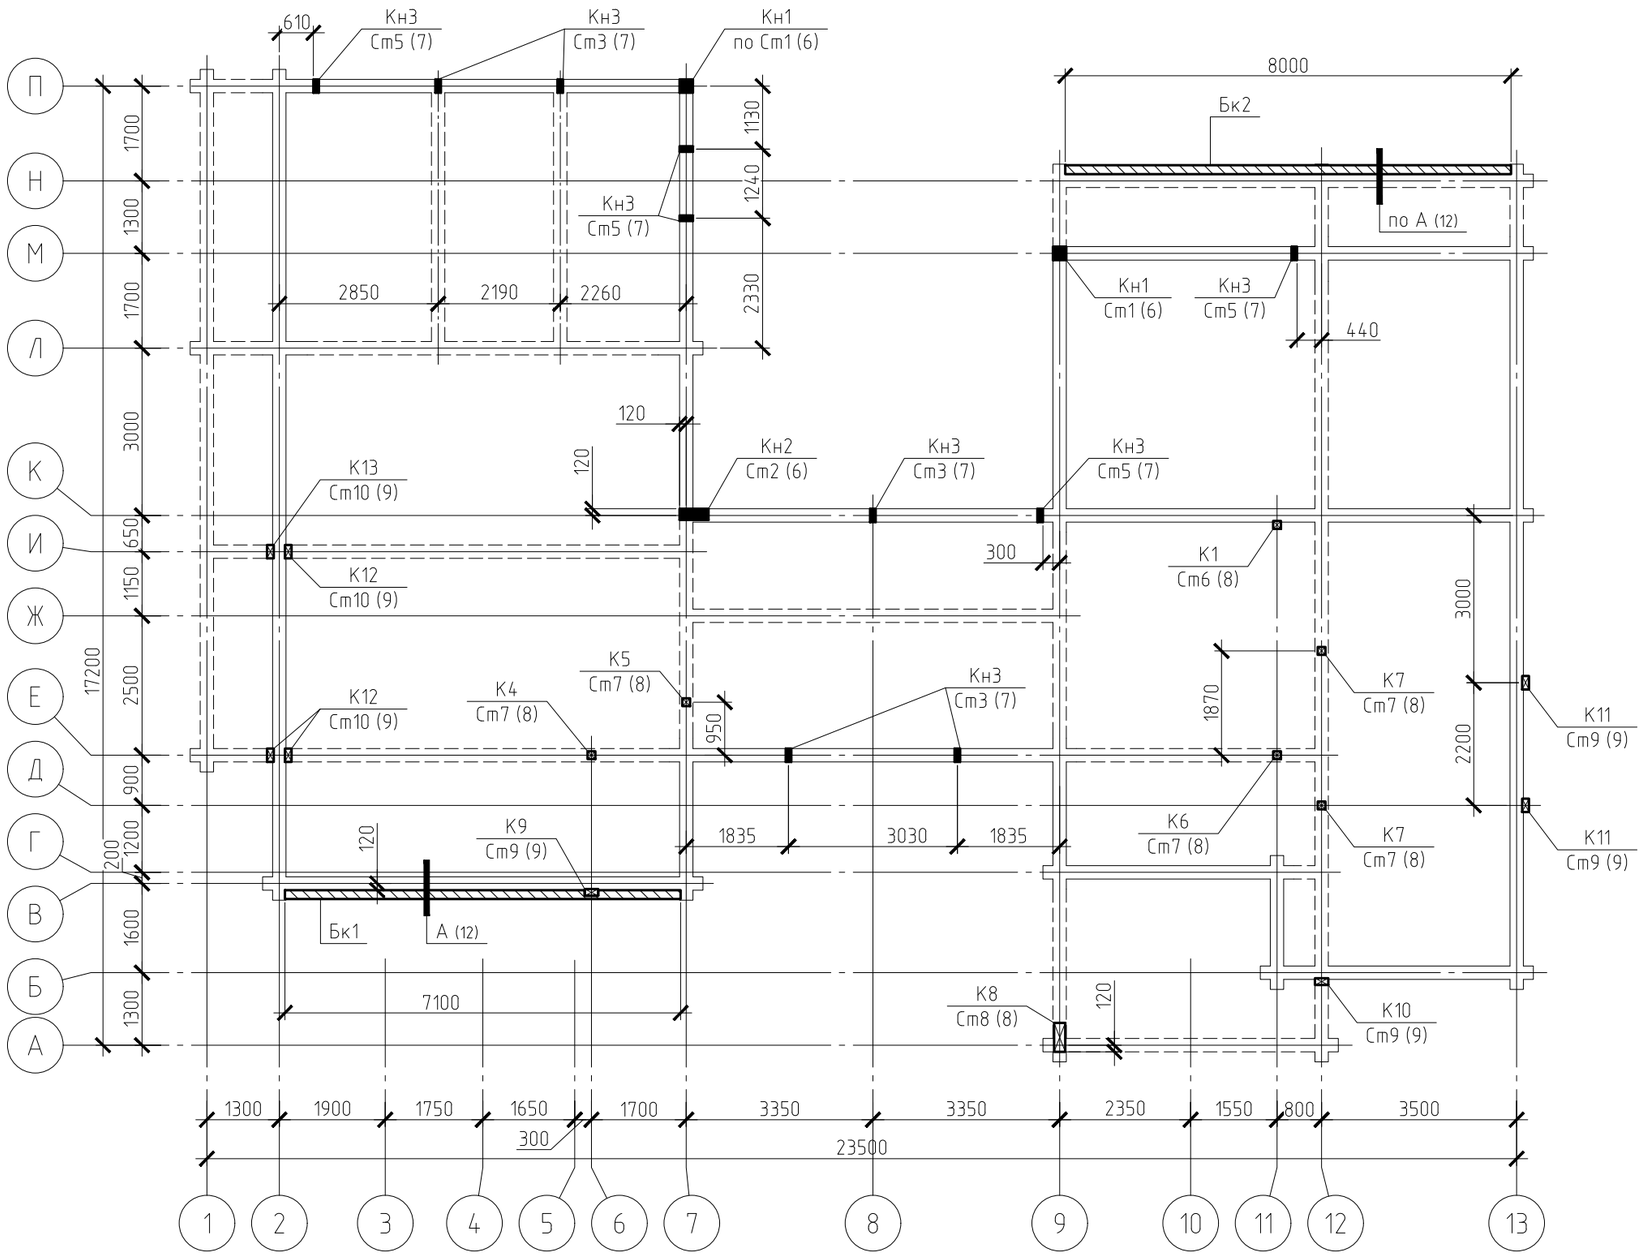

Спецификацию клееных элементов см.л.2

– стеновой брус – брусовые балки


– клееная балка

– клееная колонна

– оконная клееная колонна (размеры и привязки уточнять при монтаже окон/дверей)

						291-КД2		
						Московская область, Истринский район		
Изм.	Кол. уч.	Лист	№ док.	Подп.	Дата			
Констр.		Москалюк А.			29.09.26	Клееный материал	Стадия	Лист	Листов
Провер.		Баннов Е.			29.09.26		Р	3	
ГИП		Баннов Е.			29.09.26	План клееных конструкций первого этажа	ООО "Строй Хауз"		

Формат А3

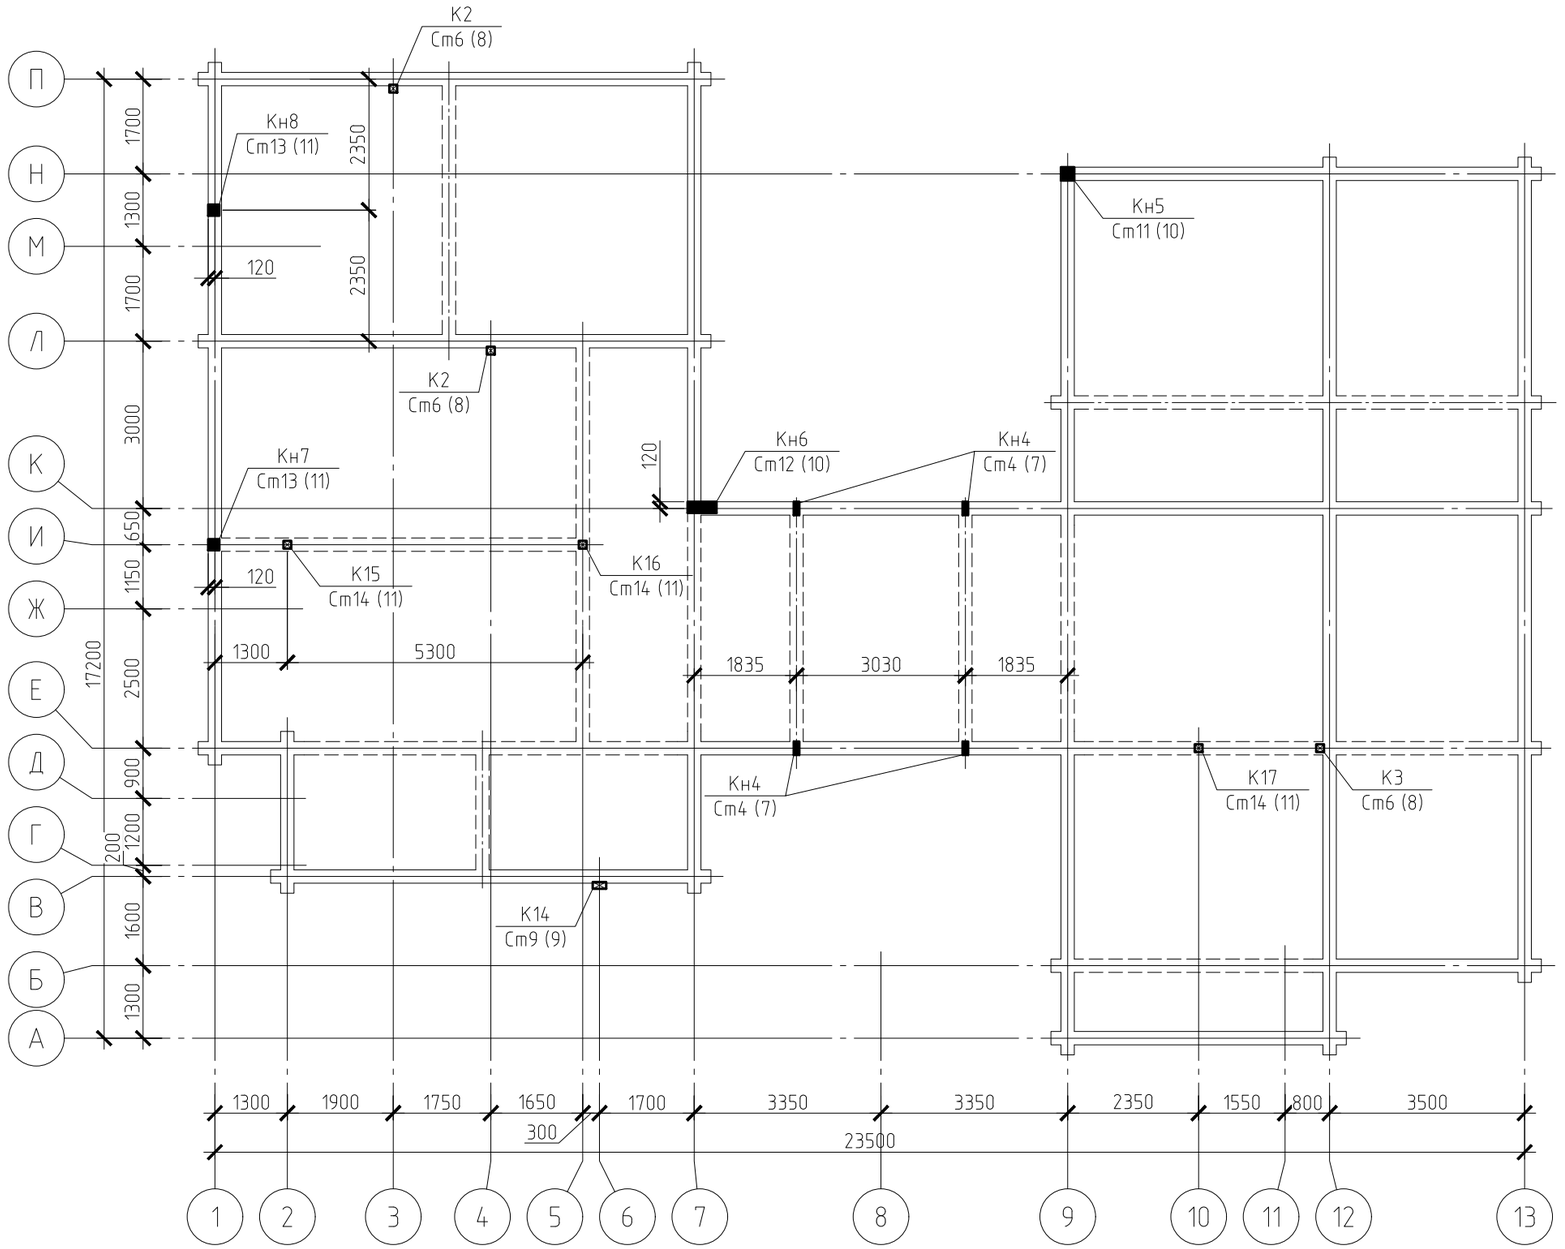

Спецификацию клееных элементов см.л.2

▭ – стеновой брус ▭▭▭ – брусовые балки


▨ – клееная балка

⊠ – клееная колонна

■ – оконная клееная колонна (размеры и привязки уточнять при монтаже окон/дверей)

						291-КД2		
						Московская область, Истринский район		
Изм.	Кол. уч.	Лист	№ док.	Подп.	Дата			
Констр.		Москалюк А.			29.09.26	Клееный материал	Стадия	Лист	Листов
Провер.		Баннов Е.			29.09.26		Р	4	
ГИП		Баннов Е.			29.09.26	План клееных конструкций второго этажа	ООО "Строй Хауз"		

Формат А3

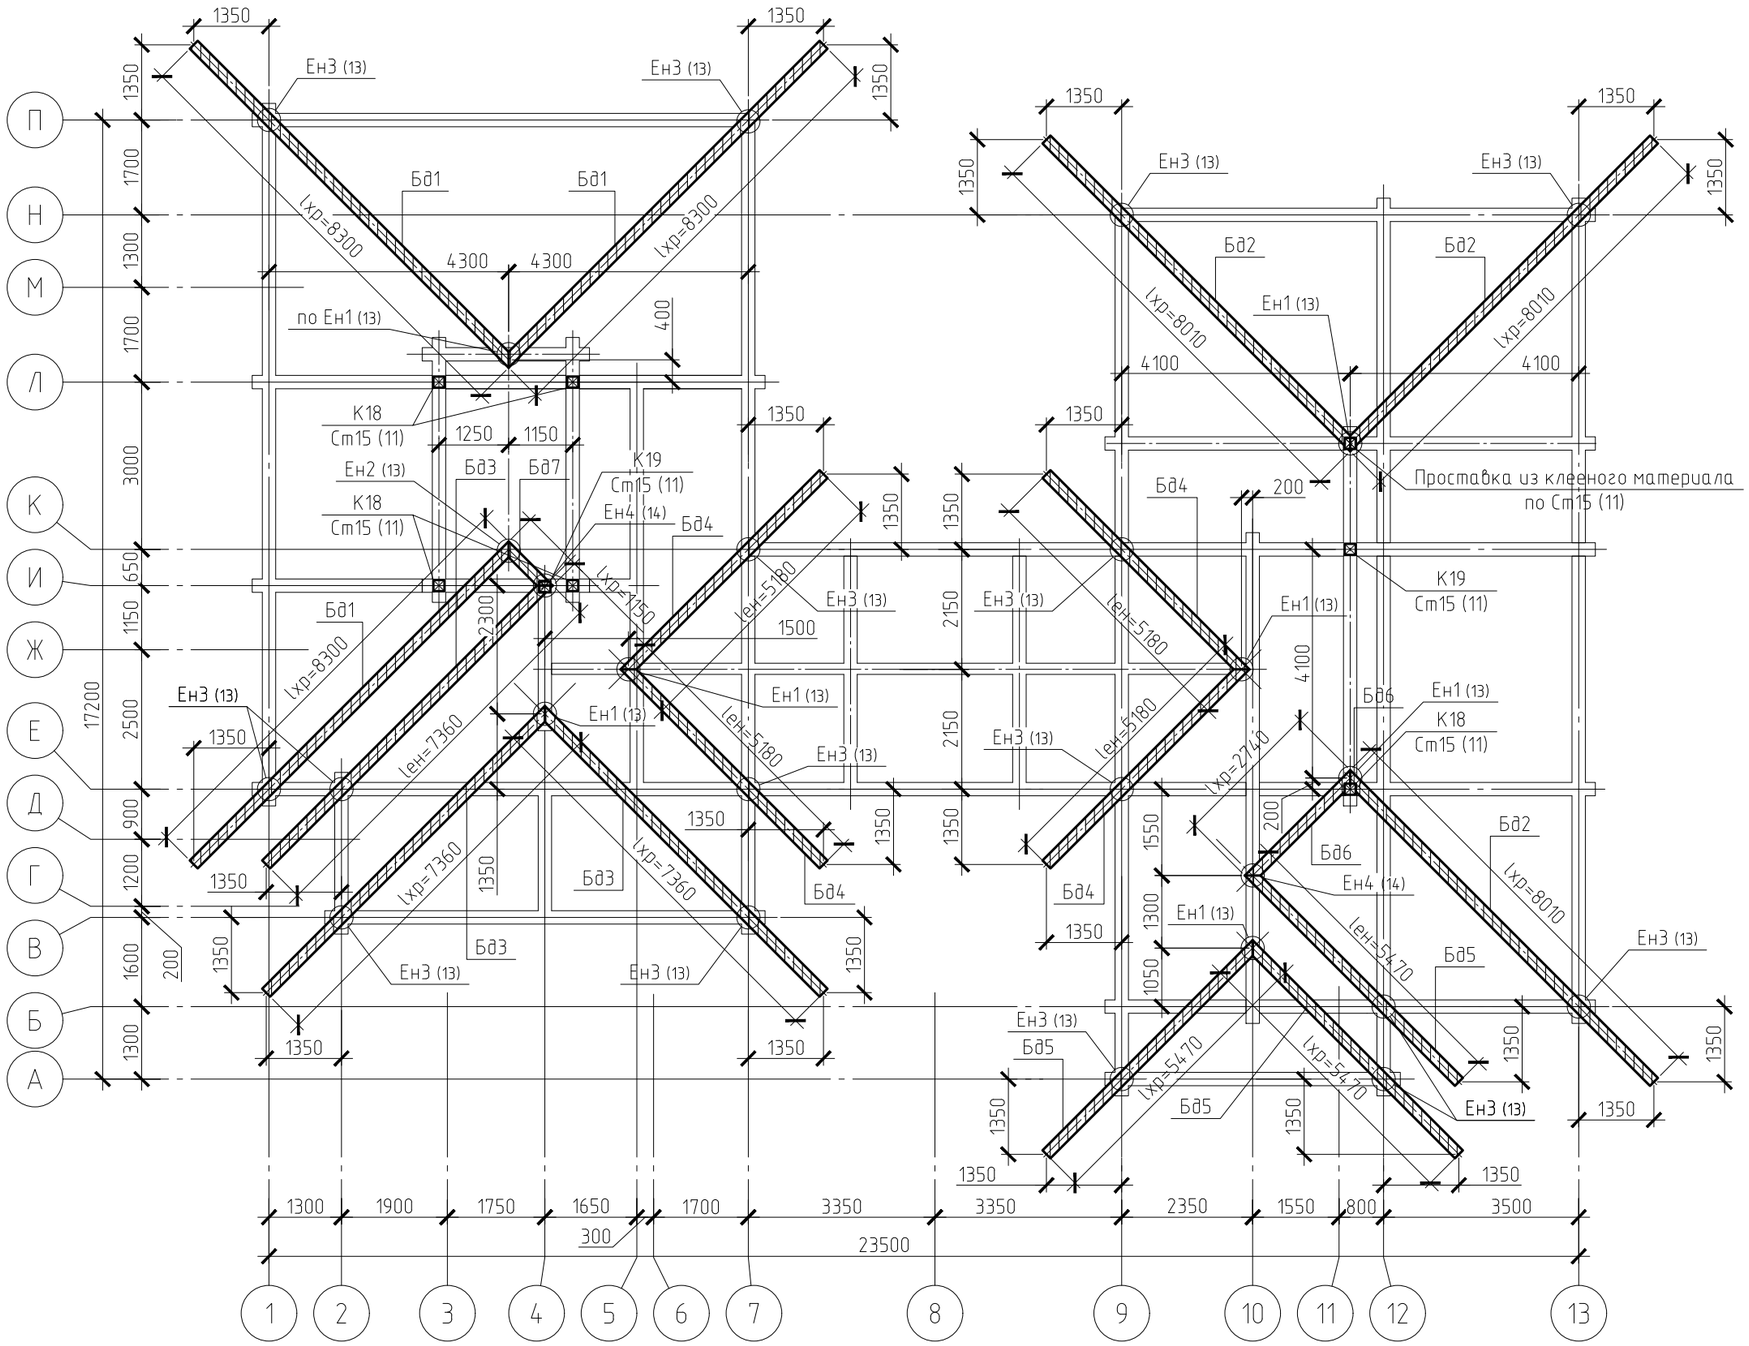

Спецификацию клееных элементов см.л.2

– стеновой брус – брусовые балки

– клееная балка

– клееная колонна

– оконная клееная колонна (размеры и привязки уточнять при монтаже окон/дверей)

Изм.	Кол. уч.	Лист	№ док.	Подп.	Дата
Констр.		Москалюк А.			29.09.26
Провер.		Баннов Е.			29.09.26
ГИП		Баннов Е.			29.09.26

291-КД2

Московская область, Истринский район


Клееный материал


Стадия	Лист	Листов
Р	5	


План диагональных стропил

ООО "Строй Хауз"

Формат А3

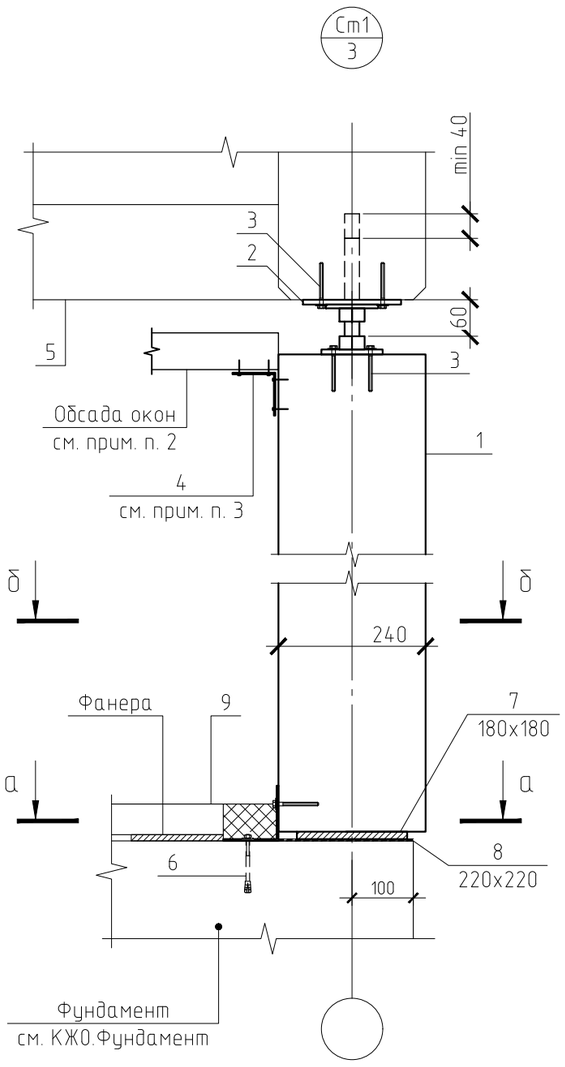


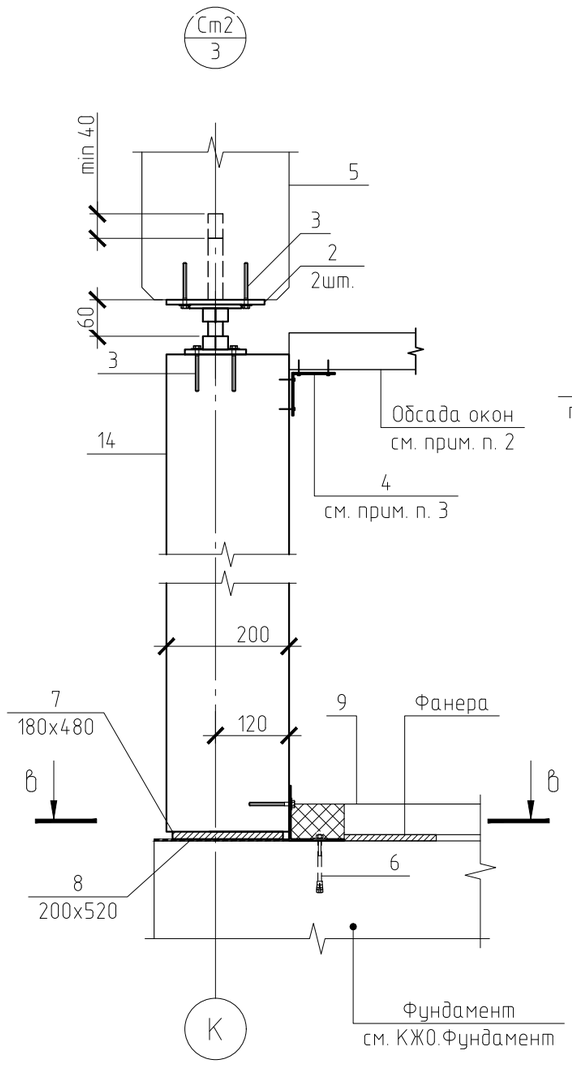

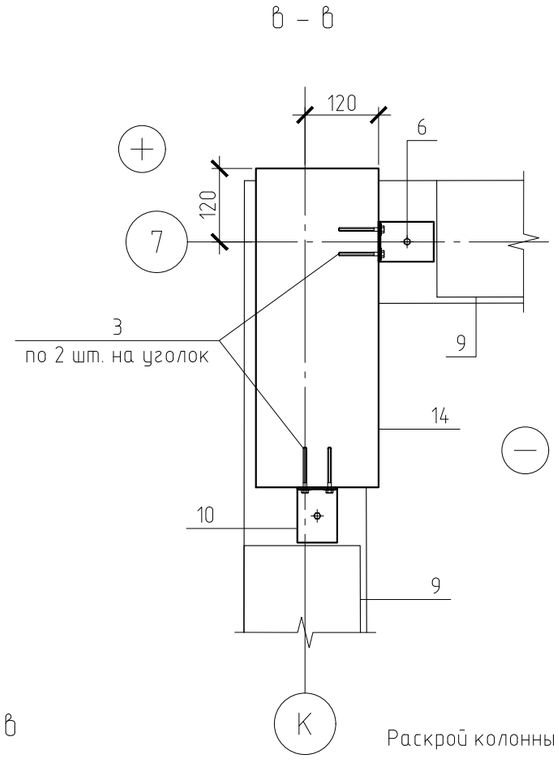


Поз.	Наименование
1	Колонна клееная 240x240
2	Регулировочная стойка Рс-24
3	Глухарь М6х80, шайба М6 усиленная, 4шт.
4	Уголок КР 4
5	Брусовая стена/балка
6	Анкер М6х100, шайба М6 усиленная
7	Фанера ламинированая 12мм, торцы обмазать мастикой
8	Техноэласт ЭПП
9	Подвенечный оклад
10	Уголок КР 1
11	ПСУЛ
12	Шип, фанера 24мм / паз в брусе, крепить с/н 6х80 шаг 400
13	Avaterm
14	Колонна клееная 200x520


Раскрой колонны для устр-ва пазов под ПСУЛ

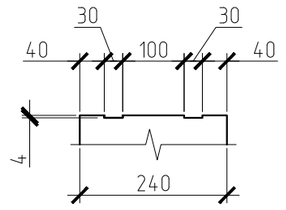


Шип "Ласточкин хвост (ЛХ)"

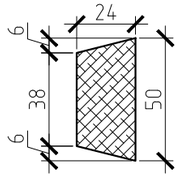

а – а

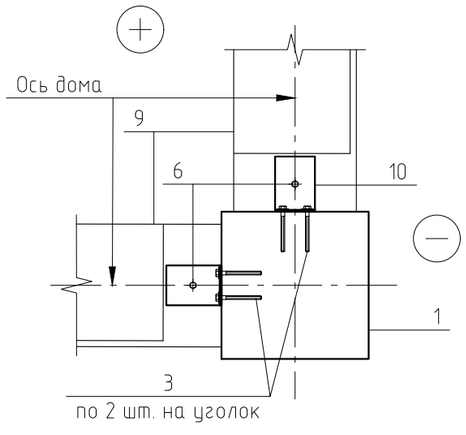

б – б

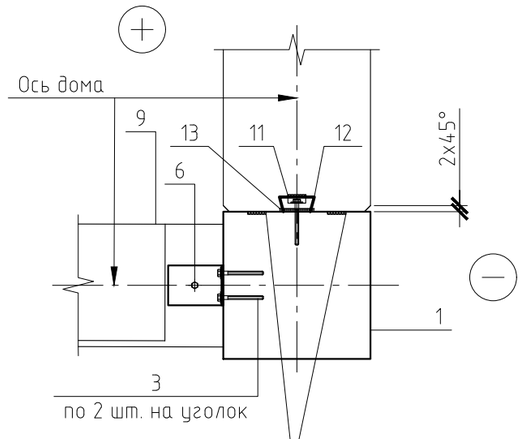


Примечание:
1. Зазор между подвенечным окладом и колонной заполнить монтажной пеной (на основе пенополиуретана). После отверждения пены выступающие наплывы срезать. Не допускается заполнять зазоры до сборки коробки сооружения. Монтажная пена должна соответствовать по температуре применения в летнее или зимнее время;
2. Усадочный зазор заполнить минераловатной теплоизоляцией, закрыть откосом и наличником;
3. Уголки КР 4 крепить саморезами 4х50 по 4шт.;
4. Бетонную площадку под опору колонны предварительно отшлифовать;
5. По окончанию всех работ с монтажной пеной покрыть ее с наружной стороны акрилатным герметиком СТИЗ А, а с внутренней акрилатным герметиком СТИЗ Б.


						291-КД2		
						Московская область, Истринский район		
Изм.	Кол. уч.	Лист	№ док.	Подп.	Дата			
Констр.		Москалюк А.			29.09.26	Клееный материал	Стадия	Лист	Листов
Провер.		Баннов Е.			29.09.26		Р	6	
ГИП		Баннов Е.			29.09.26	Узлы См1, См2	ООО "Строй Хауз"		

Формат А3


Поз.	Наименование
1	Колонна клееная 100х240
2	Глухарь М6х80, шайба М6 усиленная, 4шт.
3	Регулировочная стойка Рс-24
4	Уголок КР 4
5	Фанера ламинированая 12мм
6	Анкер М6х100 с усил. шайбой
7	Техноэласт ЭПП
8	Авaтерм
9	Уголок КР 1
10	Деревянный нагель ⌀20, 2шт.
11	Брусовая стена/балка
12	Шип, фанера 24мм / паз в брусе, крепить с/н 6х80 шаг 400
13	ПСУЛ

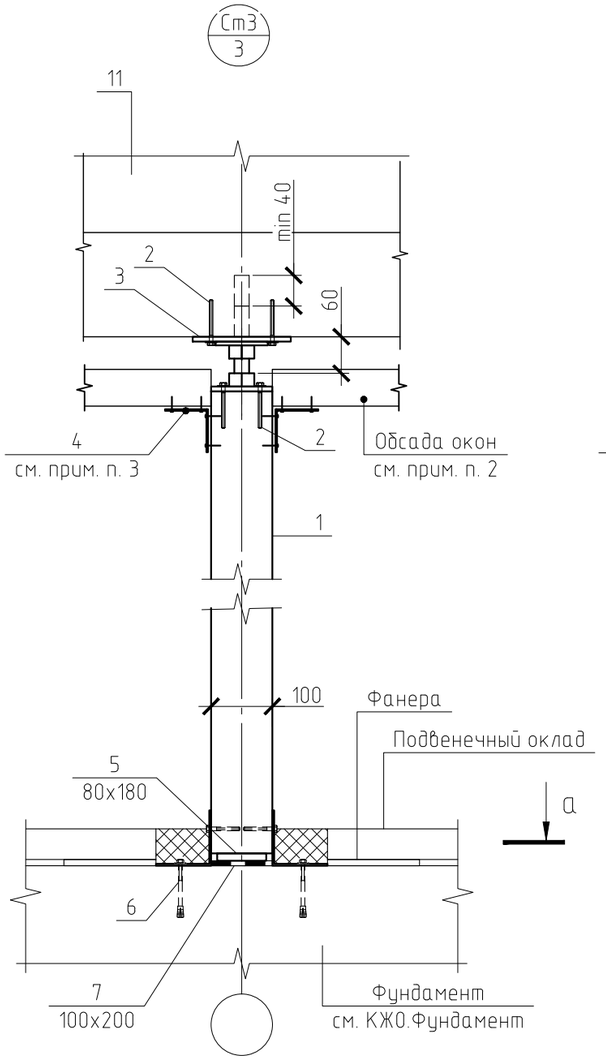


а – а

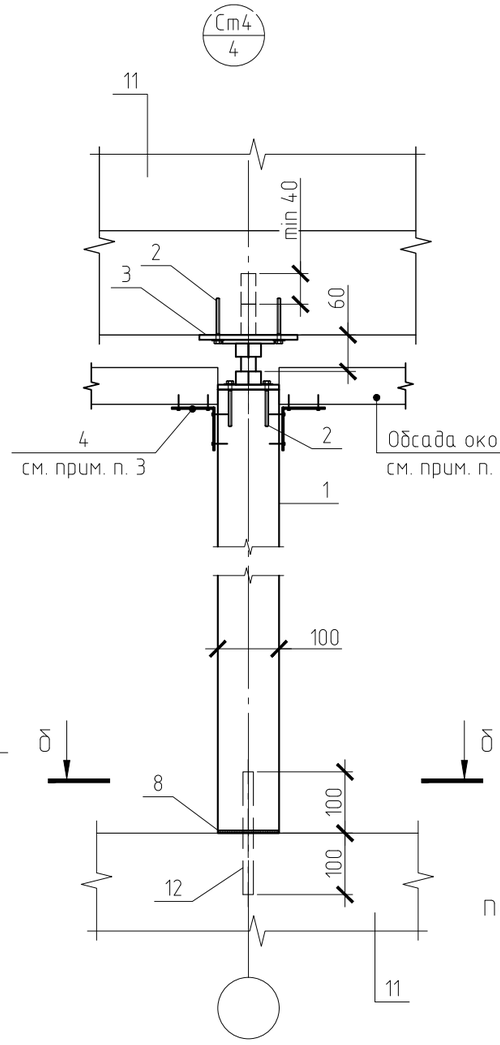



б – б

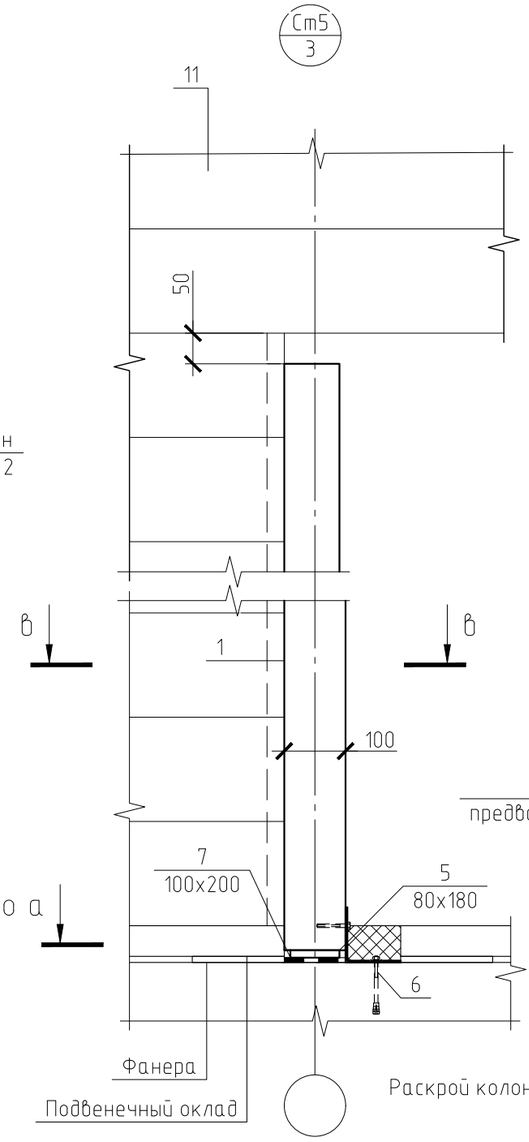


в – в (развернуто)

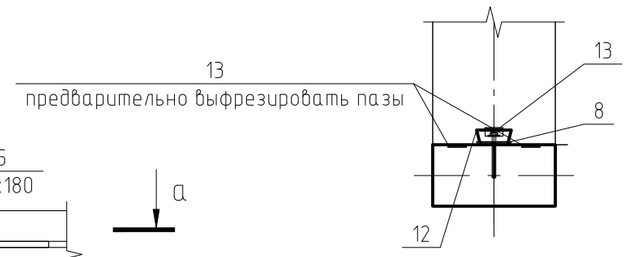

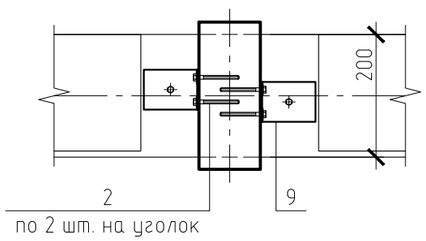


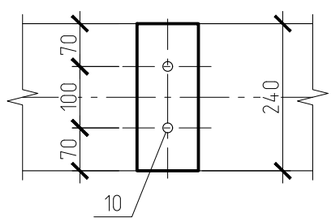

Раскрой колонны для устр-ва пазов под ПСУЛ

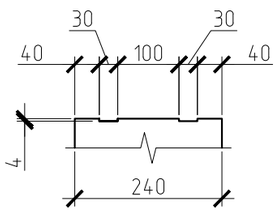

Шип "Ласточкин хвост (ЛХ)"

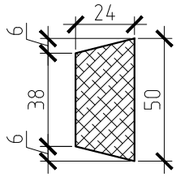

Примечание:
1. Зазор между подвенечным окладом и колонной заполнить монтажной пеной (на основе пенополиуретана). После отверждения пены выступающие наплывы срезать. Не допускается заполнять зазоры до сборки коробки сооружения. Монтажная пена должна соответствовать по температуре применения в летнее или зимнее время;
2. Усадочный зазор заполнить минераловатной теплоизоляцией, закрыть откосом и наличником;
3. Уголки КР 4 крепить саморезами 4х50 по 4шт.;
4. Бетонную площадку под опору колонны предварительно отшлифовать;
5. По окончанию всех работ с монтажной пеной покрыть ее с наружной стороны акрилатным герметиком СТИЗ А, а с внутренней акрилатным герметиком СТИЗ Б.

Изм.	Кол. уч.	Лист	№ док.	Подп.	Дата
Констр.		Москалюк А.			29.09.26
Провер.		Баннов Е.			29.09.26
ГИП		Баннов Е.			29.09.26

291-КД2

Московская область, Истринский район

Клееный материал


Стадия	Лист	Листов
Р	7	

Узлы Ст3..Ст5


ООО "Строй Хауз"

Формат А3


Ст6
3,4

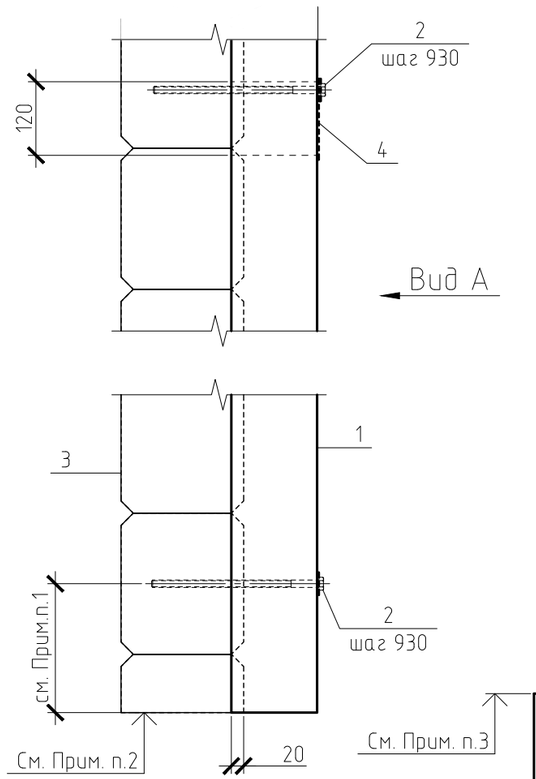


Вид А

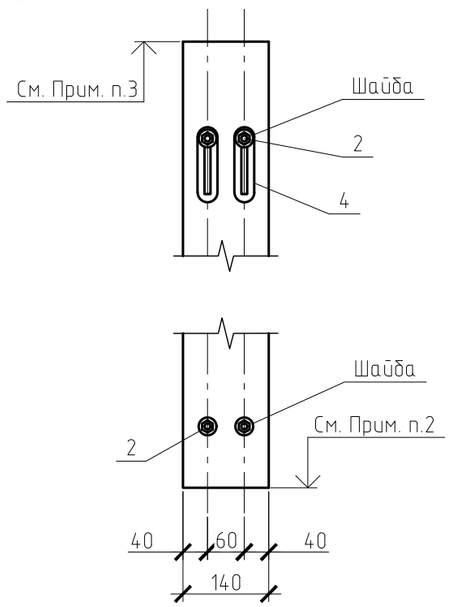

Ст7
3

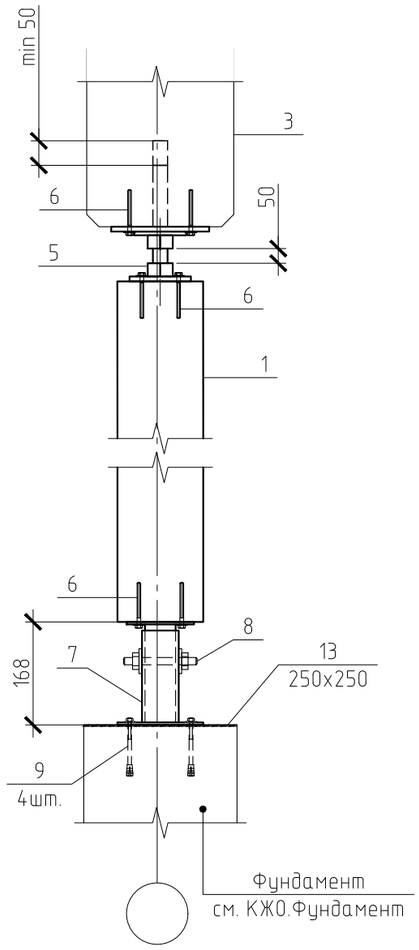

Ст8
3

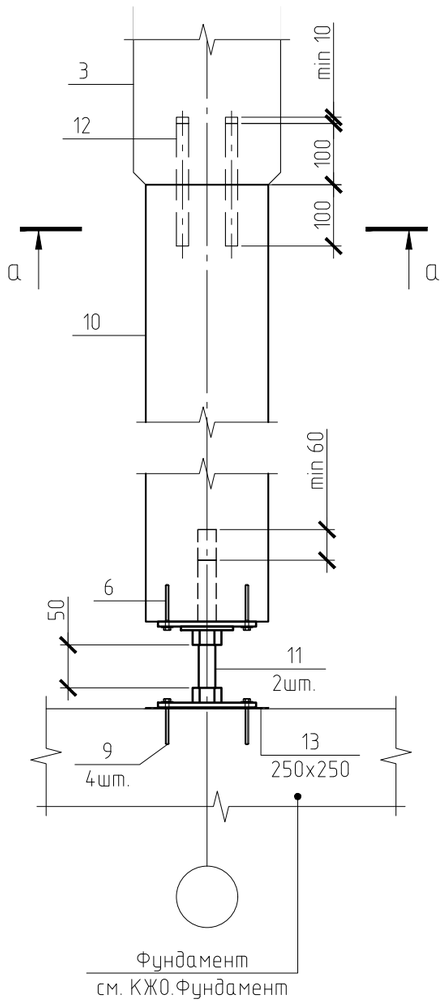

Поз.	Наименование
1	Колонна клееная 140х140
2	Глухарь М12х280 с шайбой М12 усиленная
3	Брусовая стена/балка
4	Стальная метал. пластина 38х100
5	Регулировочная стойка Рс-24
6	Глухарь М6х80, шайба М6 усиленная, 4шт.
7	Комплект опор PSP 110/140
8	Шпилька М12 L=150мм, с гайкой и шайбой
9	Анкер М6х100 с усил. шайбой
10	Колонна клееная 200х520
11	Регулировочная стойка Рс-27
12	Деревянный нагель ⌀20, 4шт.
13	Техноэласт ЭПП


а – а


Примечание:
1. Самые нижние глухари располагать по центру ближайшего венца брусовой стены, к которой крепится клееная колонна;
2. Уровень низа клеенных колонн первого этажа должен совпадать с уровнем низа брусовых стен, а второго этажа на 20мм ниже уровня пола второго этажа;
3. Уровень верха клееных колонн должен быть ниже на 50мм вышележащей балки или финишной отделки потолка.


						291-КД2	
						Московская область, Истринский район	
Изм.	Кол. уч.	Лист	№ док.	Подп.	Дата		
Констр.		Москалюк А.			29.09.26	Клееный материал	Стадия: Р; Лист: 8; Листов:
Провер.		Баннов Е.			29.09.26		
ГИП		Баннов Е.			29.09.26	Узлы Ст6..Ст8	ООО "Строй Хауз"

Формат А3

Поз.	Наименование
1	Колонна клееная 120х240
2	Брусовая стена/балка
3	Глухарь М12х240 с шайбой М12 усиленная
4	Стальная метал. пластина 38х100
5	Паз 30х40 на всю длину колонны

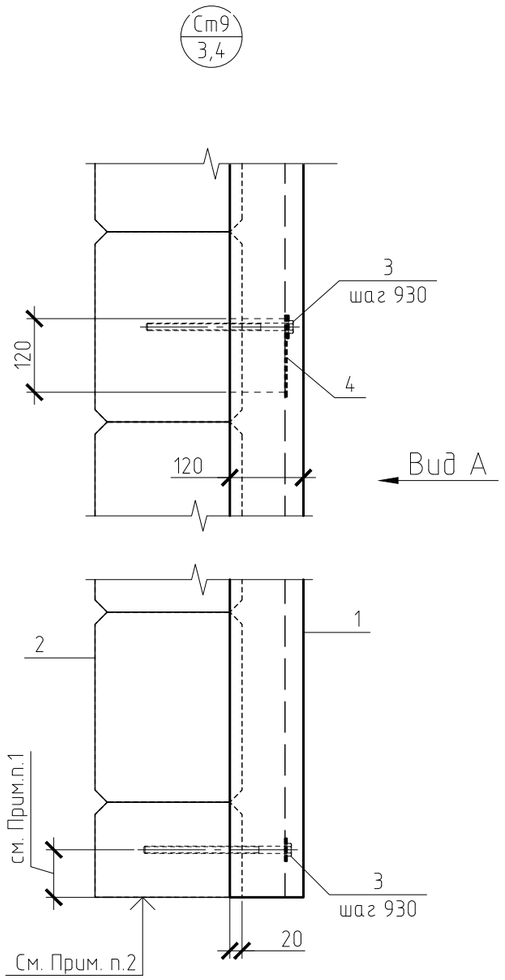

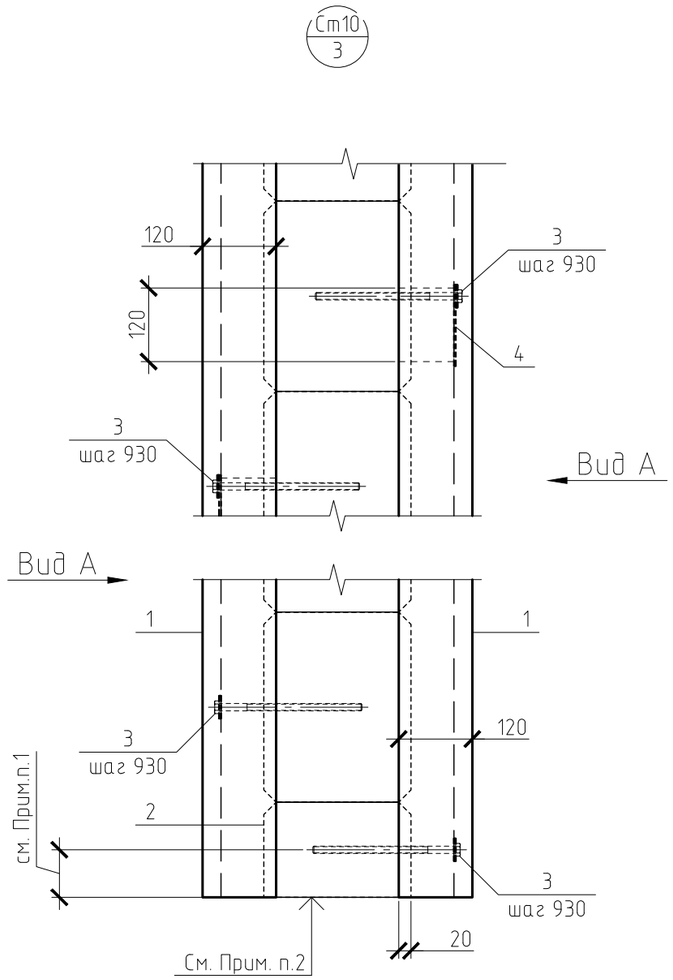


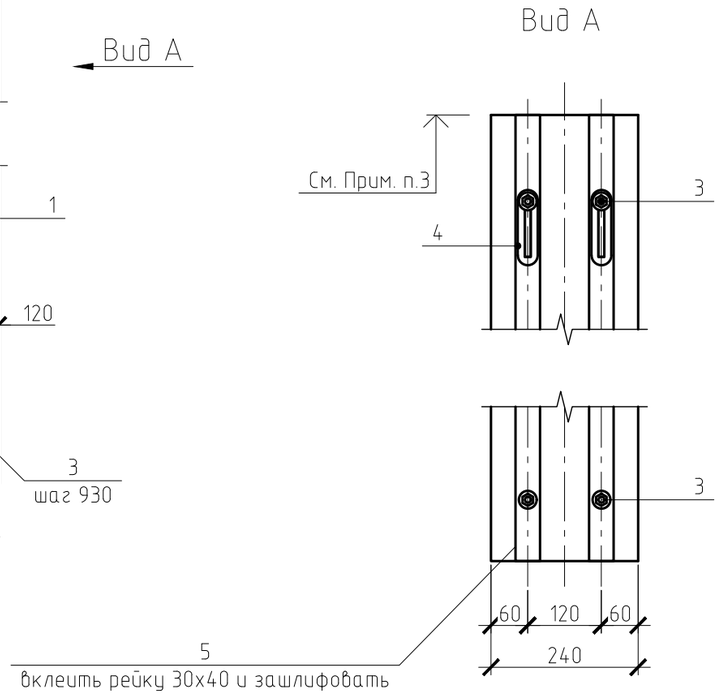


Примечание:
1. Самые нижние глухари располагать по центру ближайшего венца брусовой стены, к которой крепится клееная колонна;
2. Уровень низа клеенных колонн первого этажа должен совпадать с уровнем низа брусовых стен, а второго этажа на 20мм ниже уровня пола второго этажа;
3. Уровень верха клееных колонн должен быть ниже на 50мм (на 100мм если колонна больше 5м) вышележащей балки или финишной отделки потолка.

Изм.	Кол. уч.	Лист	№ док.	Подп.	Дата	291-КД2			
						Московская область, Истринский район			
Констр.		Москалюк А.			29.09.26	Клееный материал	Стадия	Лист	Листов
Провер.		Баннов Е.			29.09.26		Р	9	
ГИП		Баннов Е.			29.09.26	Узлы Ст9, Ст10	ООО "Строй Хауз"		


Формат А3

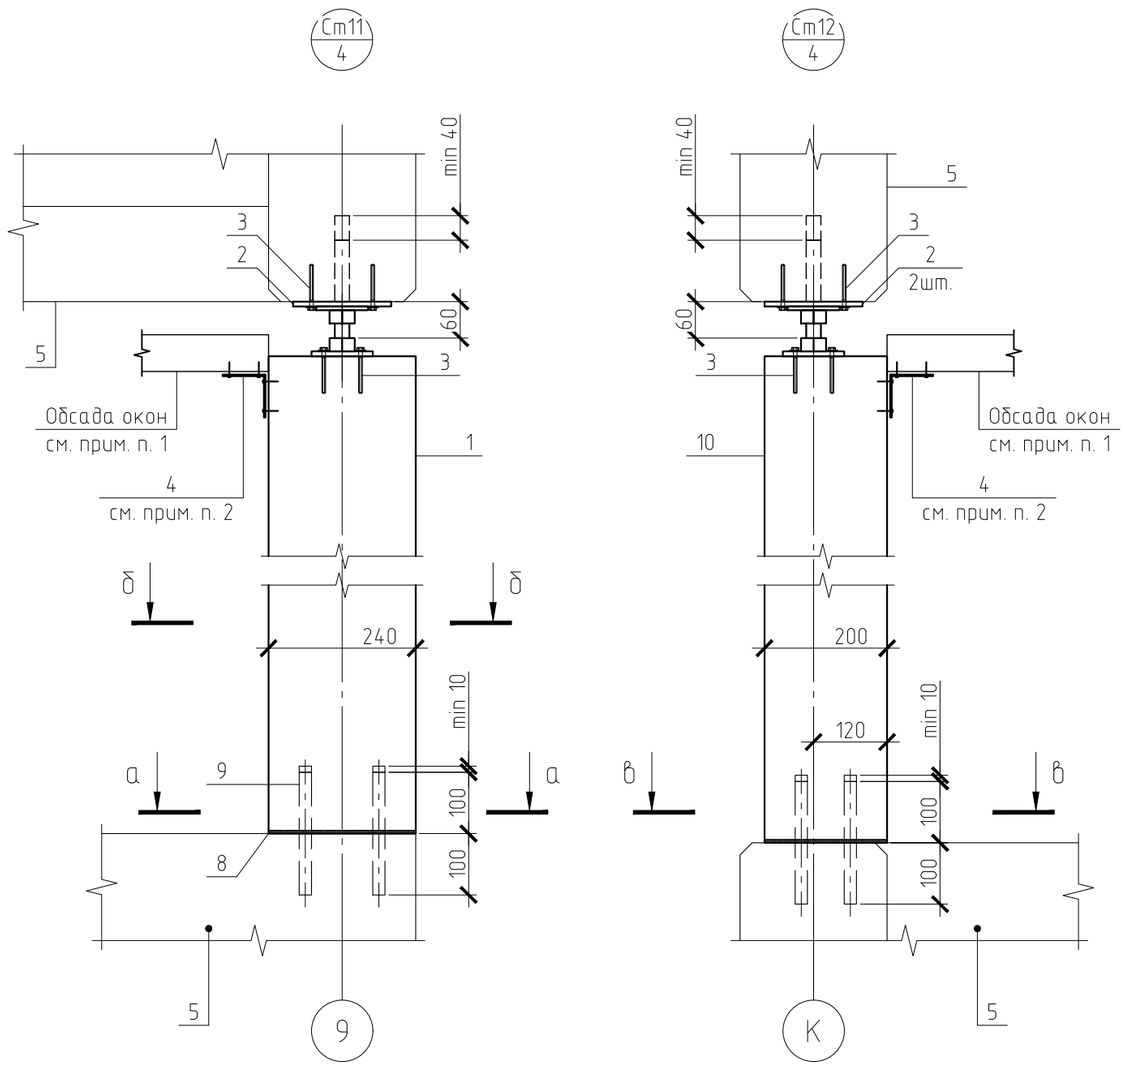

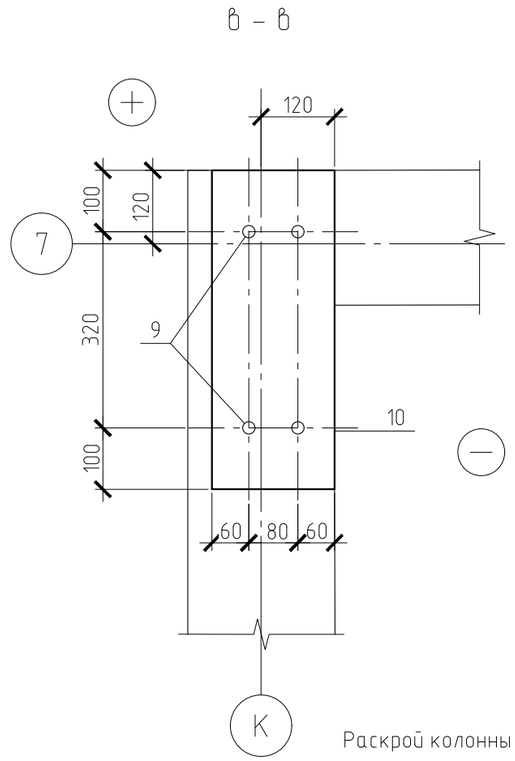


Поз.	Наименование
1	Колонна клееная 240х240
2	Регулировочная стойка Рс-24
3	Глухарь М6х80, шайба М6 усиленная, 4шт.
4	Уголок КР 4
5	Брусовая стена/балка
6	ПСУЛ
7	Шип, фанера 24мм / паз в брусе, крепить с/н 6х80 шаг 400
8	Avaterm
9	Деревянный нагель ⌀20, 2шт.
10	Колонна клееная 200х520


Раскрой колонны для устр-ва пазов под ПСУЛ

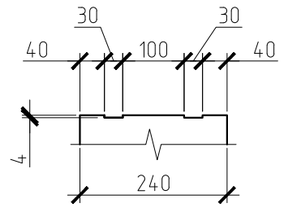


Шип "Ласточкин хвост (ЛХ)"

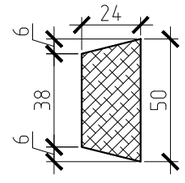

а – а

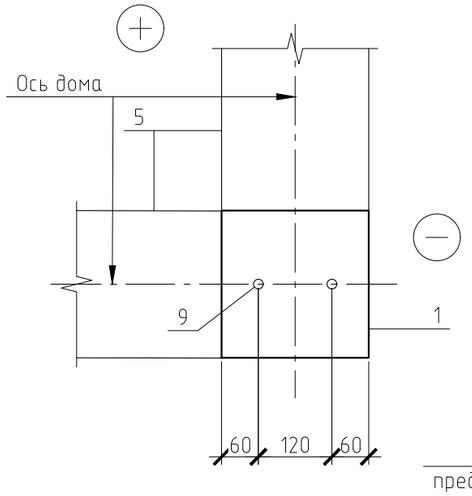

б – б

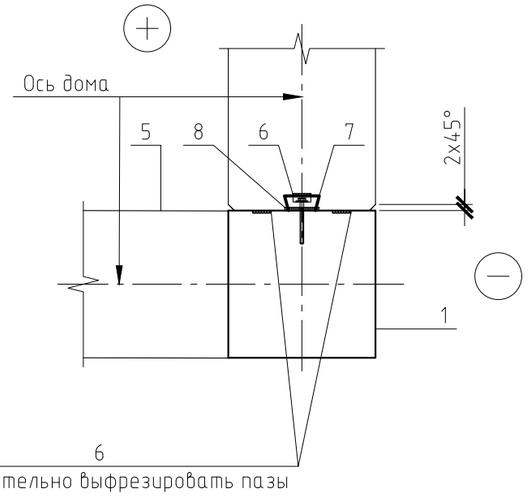



Примечание:
1. Усадочный зазор заполнить минераловатной теплоизоляцией, закрыть откосом и наличником;
2. Уголки КР 4 крепить саморезами 4х50 по 4шт.


Изм.	Кол. уч.	Лист	№ док.	Подп.	Дата	291-КД2			
						Московская область, Истринский район			
Констр.		Москалюк А.			29.09.26	Клееный материал	Стадия	Лист	Листов
Провер.		Баннов Е.			29.09.26		Р	10	
ГИП		Баннов Е.			29.09.26	Узлы Ст11, Ст12	ООО "Строй Хауз"		


Формат А3


Поз.	Наименование
1	Колонна клееная 200х200
2	Регулировочная стойка Рс-24
3	Глухарь М6х80, шайба М6 усиленная, 4шт.
4	Уголок КР 4
5	Брусовая стена/балка
6	Аватерм
7	Деревянный нагель ⌀20, 2шт.
8	Колонна клееная 140х140

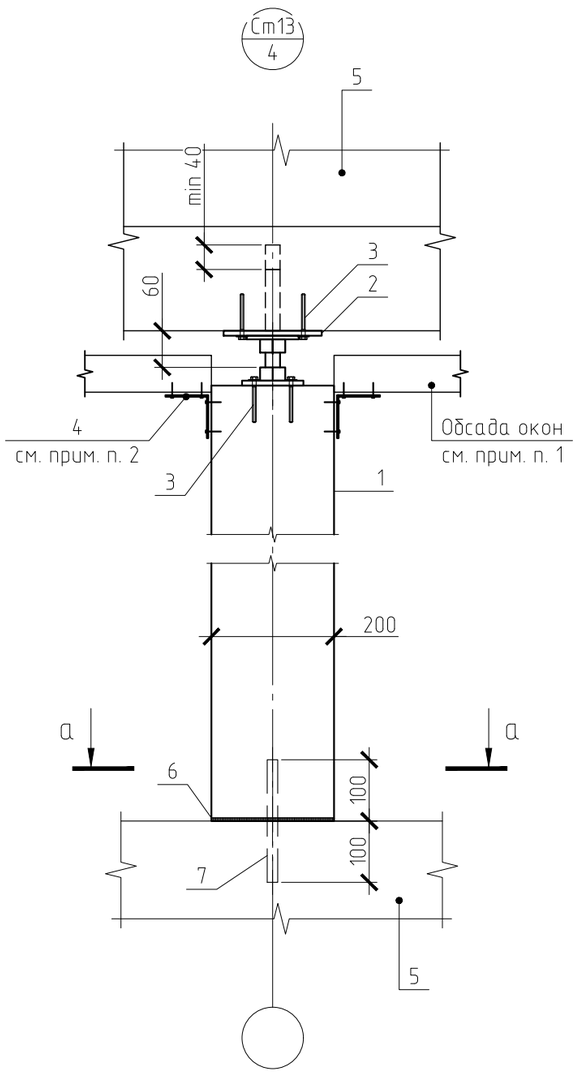

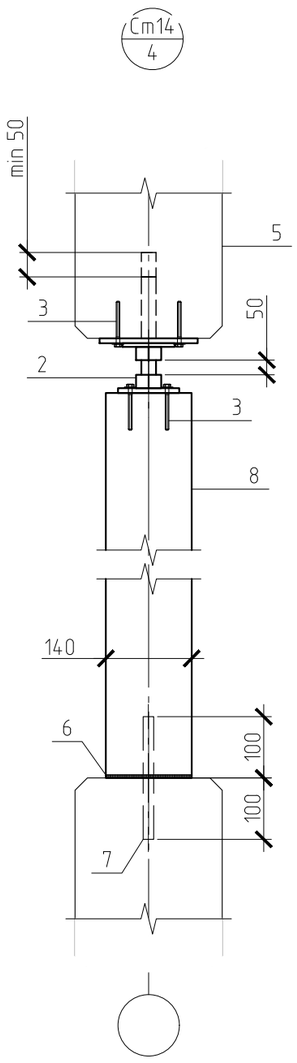

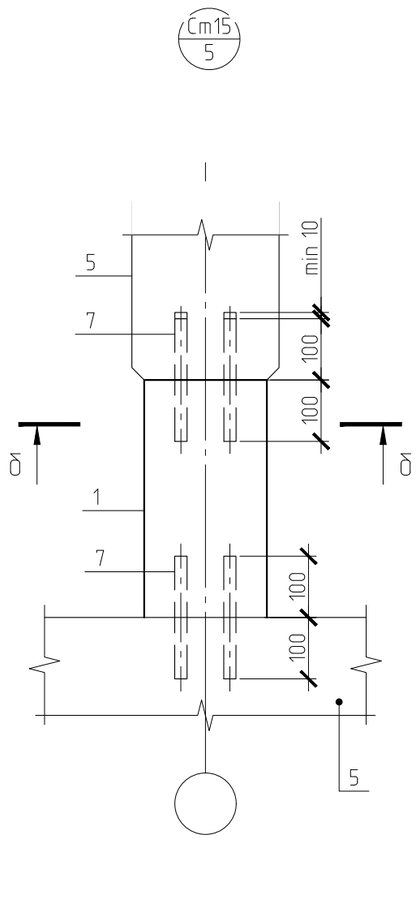

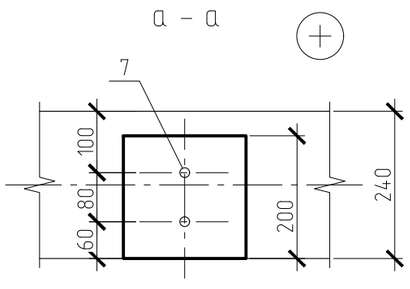

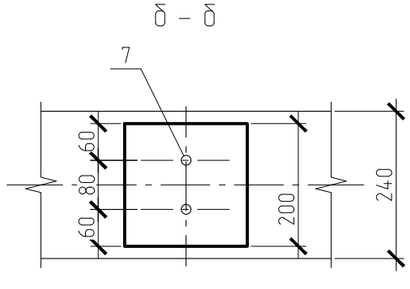


Примечание:
1. Усадочный зазор заполнить минераловатной теплоизоляцией, закрыть откосом и наличником;
2. Уголки КР 4 крепить саморезами 4х50 по 4шт.

Изм.	Кол. уч.	Лист	№ док.	Подп.	Дата	291-КД2			
						Московская область, Истринский район			
Констр.		Москалюк А.			29.09.26	Клееный материал	Стадия	Лист	Листов
Провер.		Баннов Е.			29.09.26		Р	11	
ГИП		Баннов Е.			29.09.26	Узлы См13..См15	ООО "Строй Хауз"		

Формат А3

Поз.	Наименование
1	Клееная балка
2	Брусовая стена
3	Полнорезьбовой шуруп 8х280

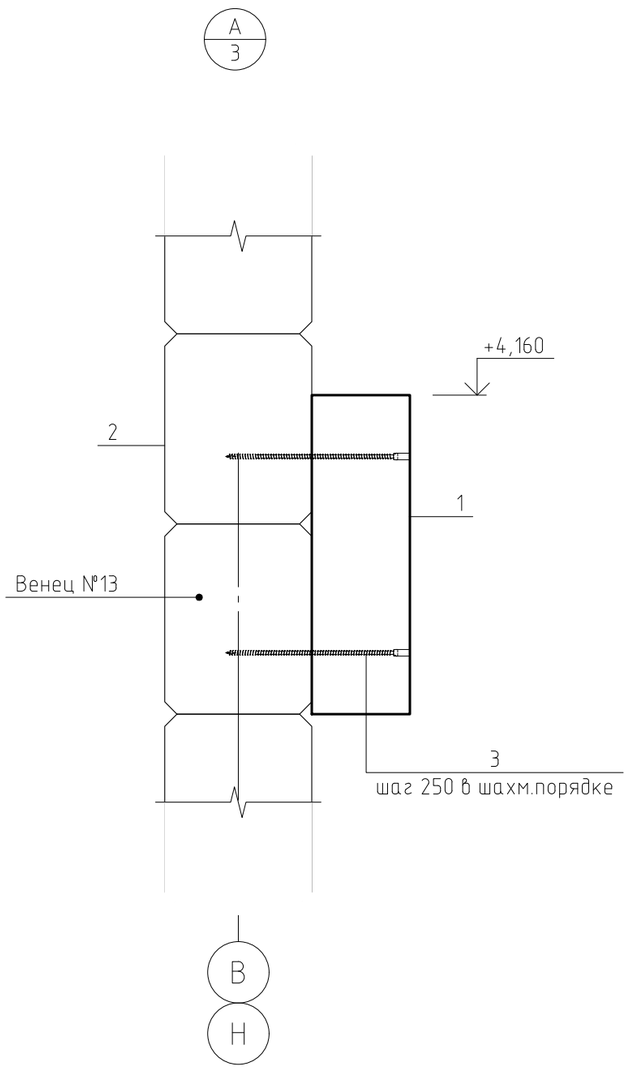


Примечание:
1. Отверстия под саморезы заделать чопиками.


Изм.	Кол. уч.	Лист	№ док.	Подп.	Дата	291-КД2			
						Московская область, Истринский район			
Констр.		Москалюк А.			29.09.26	Клееный материал	Стадия	Лист	Листов
Провер.		Баннов Е.			29.09.26		Р	12	
ГИП		Баннов Е.			29.09.26	Узел А	ООО "Строй Хауз"		

Формат А3


Ен1
5

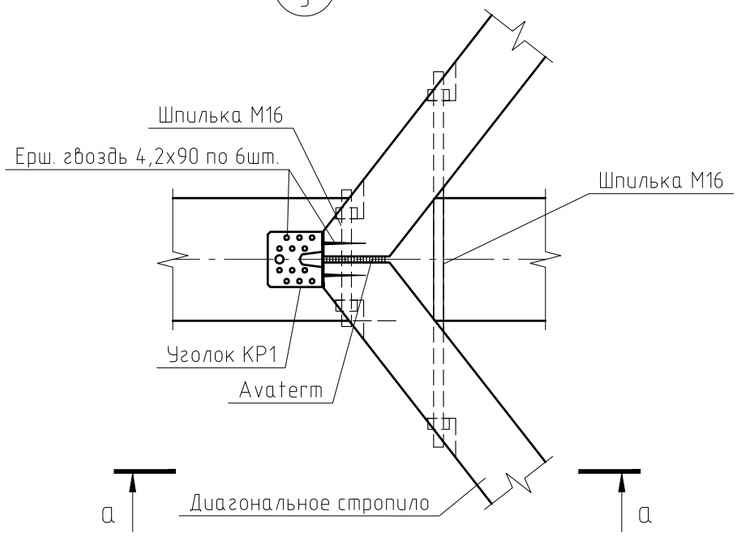


Ен2
5

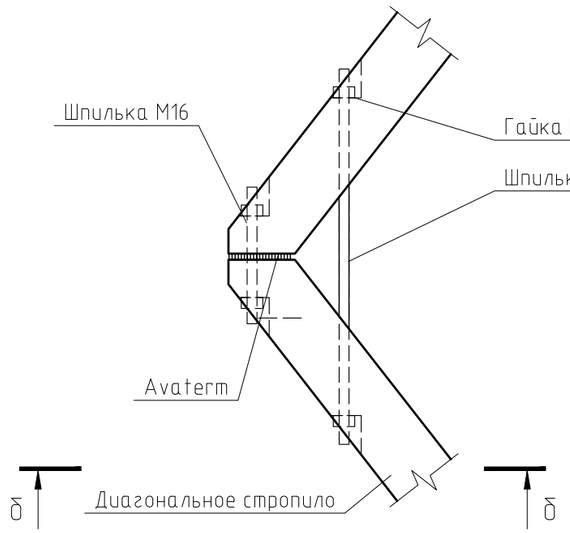


Ен3
5

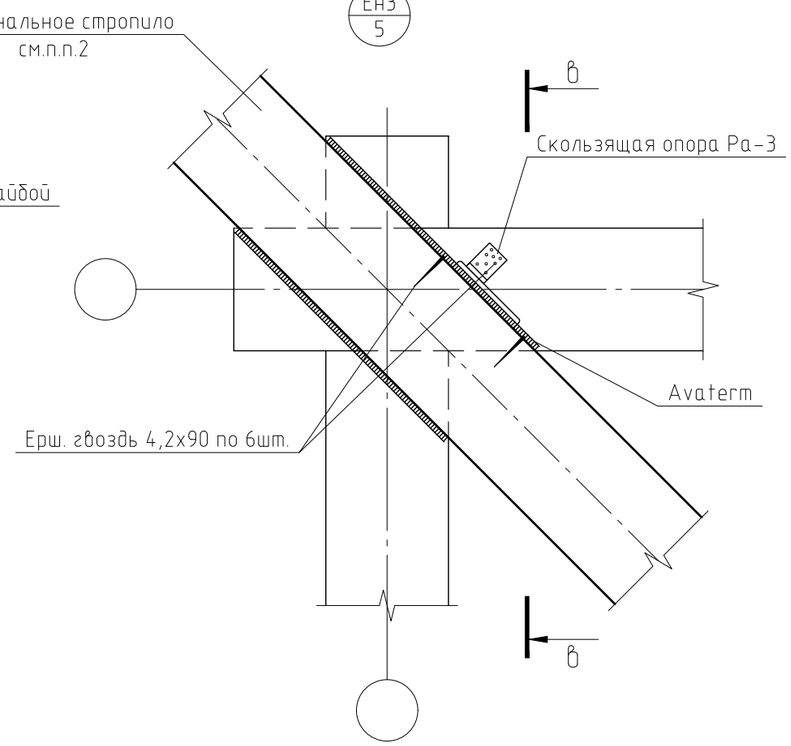


а – а

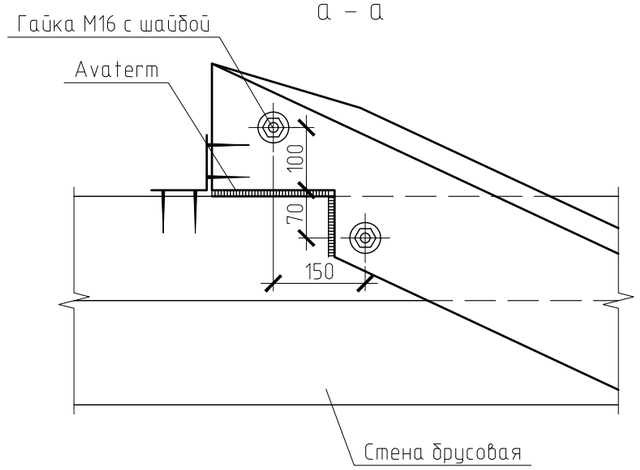

б – б

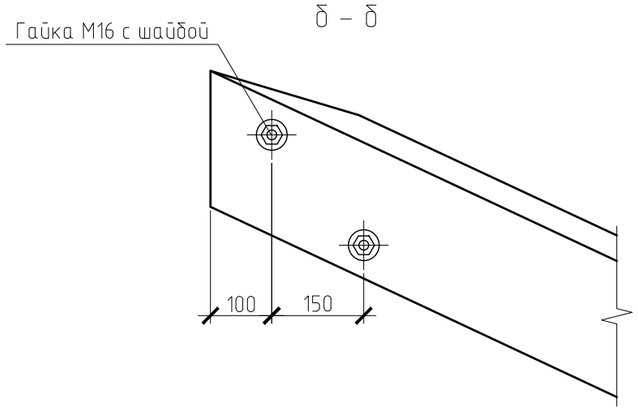

в – в

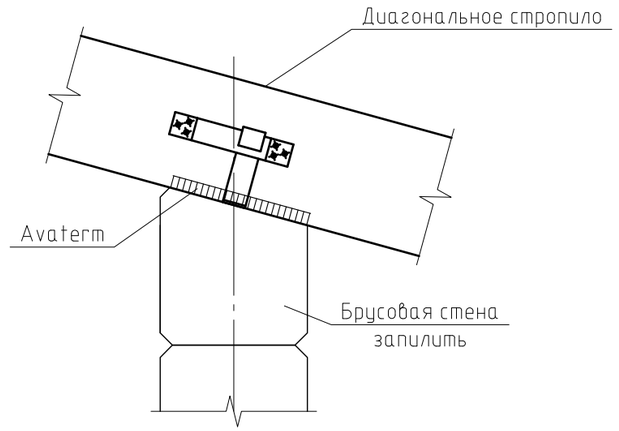


Примечание:
1. Точную привязку диагональных стропил смотреть на плане. Положение может отличаться от указанного в узле (например, ось стропила может проходить через центр переруба);
2. В местах выхода диагональных стропил на улицу необходимо их запилить до высоты 200мм;
3. Максимальная подрезка стропил не более четверти их высоты. При необходимости дальше уже выпиливать опорную стену/балку.


						291-КД2		
						Московская область, Истринский район		
Изм.	Кол. уч.	Лист	№ док.	Подп.	Дата			
Констр.		Москалюк А.			29.09.26	Клееный материал	Стадия	Лист	Листов
Провер.		Баннов Е.			29.09.26		Р	13	
ГИП		Баннов Е.			29.09.26	Узлы Ен1..Ен3	ООО "Строй Хауз"		

Формат А3

Ен4
5

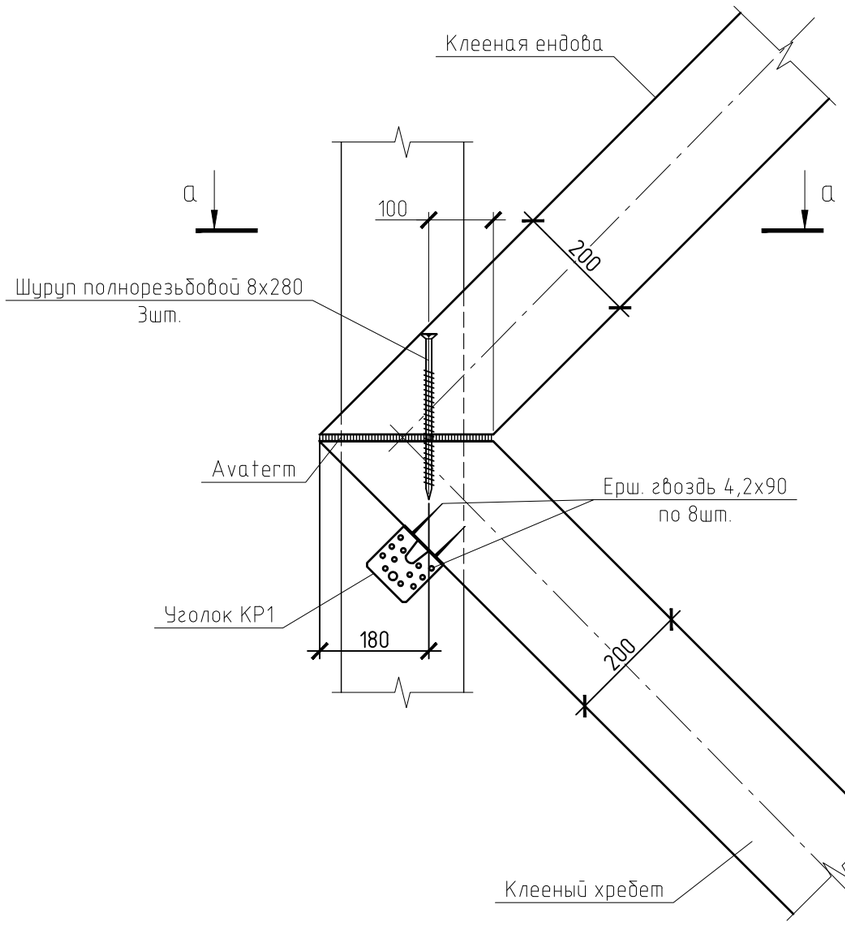

а – а

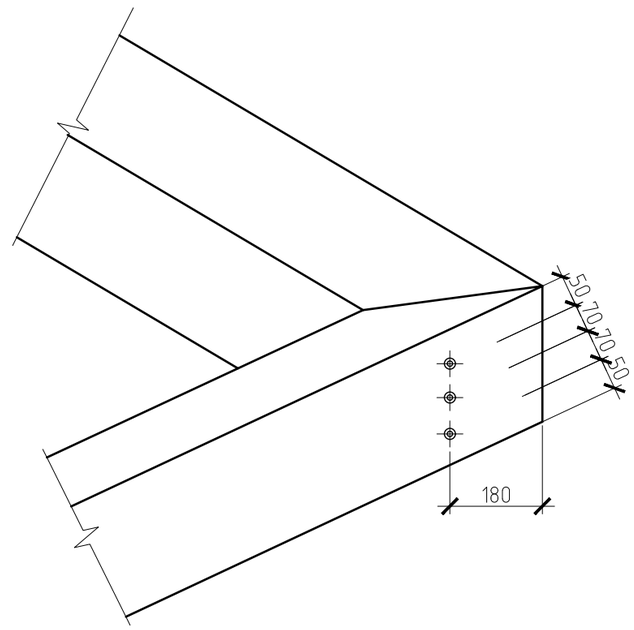

Примечание:
1. Точную привязку диагональных стропил смотреть на плане. Положение может отличаться от указанного в узле (например, ось стропила может проходить через центр переруба);
2. В местах выхода диагональных стропил на улицу необходимо их запилить до высоты 200мм;
3. Максимальная подрезка стропил не более четверти их высоты. При необходимости дальше уже выпиливать опорную стену/балку.

						291-КД2		
						Московская область, Истринский район		
Изм.	Кол. уч.	Лист	№ док.	Подп.	Дата			
Констр.		Москалюк А.			29.09.26	Клееный материал	Стадия	Лист	Листов
Провер.		Баннов Е.			29.09.26		Р	14	
ГИП		Баннов Е.			29.09.26	Узел Ен4	ООО "Строй Хауз"		

Формат А3

Спецификация материалов КД2.Клееного материала

Поз.	Обозначение	Наименование	Кол.	Ед.изм.	Приме-чание
1		Регулировочная стойка Рс 27	2	шт	
2		Анкер 6х100	49	шт	
3		Глухарь 6х80	278	шт	
4		Шайба усиленная М6	327	шт	
5		Нагель ø20	14	п.м.	
6		Регулировочная стойка РС 24	26	шт	
7		Уголок КР1	30	шт	
8		Фанера ламинированная 12мм	0.3	м2	
9		Техноэласт ЭПП	0.72	м2	
10		Уплотнитель ПСУЛ	74	п.м.	
11		Авaтерм	12	м2	
12		Шуруп самонарезающий 6х80	70	шт	
13		Глухарь 12х280	44	шт	
14		Глухарь 12х240	120	шт	
15		Шайба усиленная М12	164	шт	
16		Овальная металлическая пластина	128	шт	
17		Остнование столба PSP 110	5	шт	
18		Остнование столба PSP 140	5	шт	
19		Брусок строганый 30х40	0.12	м3	
20		Анисептик Зотекс	10	л	
21		Шуруп полнорезьбовой 8х280	78	шт	
22		Скользящая опора Ра3	16	шт	
23		Гвоздь ершеный 4,2х90	3	кг	
24		Шпилька М16	14	п.м.	
25		Гайка М16	40	шт	
26		Шайба М16	40	шт	

Изм.	Кол. уч.	Лист	№ док.	Подп.	Дата	291-КД2			
						Московская область, Истринский район			
Констр.		Москалюк А.			29.09.26	Клееный материал	Стадия	Лист	Листов
Провер.		Баннов Е.			29.09.26		Р	15	
ГИП		Баннов Е.			29.09.26	Спецификация	ООО "Строй Хауз"		

Формат А3