ООО "Строй Хауз"

Московская обл., Истринский р-н, д. Веледниково, ул. Живописная, д. 25

Берта Ромарио

по адресу: Московская область, Истринский район

Индивидуальный жилой дом

Рабочая документация

Раздел КДЗ. Подвенечный оклад

(Конструкции деревянные)

291 – КДЗ

Разработал		Брусникин Д.М.
Проверил		Москалюк А.Е.
ГИП		Баннов Е.А.

2026

Согласовано

Взам. инв. №

Подп. и дата

Инв. № подл.

Ведомость ссылочных и прилагаемых документов

Обозначение	Наименование	Примечание
СП 20.13330.2016	"Нагрузки и воздействия"	
СП 64.13330.2017	"Деревянные конструкции"	
СП 70.13330.2012	"Несущие и ограждающие конструкции"	
ГОСТ 20022.6-93	"Защита древесины"	
ГОСТ 34028-2016	"Прокат арматурный для железобетонных уонструкций"	
ТУ 5362-001-52036415-2001	"Детали и изделия деревянные для зданий из строганного бруса"	

Ведомость основных комплектов рабочих чертежей

Обозначение	Наименование	Примечание
АР	"Архитектурно-планировочные решения"	
КЖ0	Фунщдамент	
КД1	Разбрусовка	
КД2	Клеенный материал	
КД3	Подвенечный оклад	
КД4	Межэтажное перекрытие	
КД5	Кровля	
КД6	Каркасныке перегородки	

Общие данные.

1. Данный комплект чертежей выполнен на основании архитектурно-планировочных решений.
2. Строительная площадка расположена в I ветровом и III снеговом районах с нормативной глубиной сезонного промерзания:
- глина и суглинок 1,03м;
- супесь, пески вылеватые или мелкие - 1,25м;
- песок средней крупности, крупный или гравилистый - 1,34м.
3. За относительную отметку 0,000 принят уровень чистого пола 1 этажа.
4. Посадку сооружения смотри чертежи генплана.
5. Отклонения в размерах конструкций не должны превышать предельных значений, приведенных в табл. 4.11 СП 70.13330.2012 "Несущие и ограждающие конструкции ".
6. Все деревянные конструкции, кроме клееных, защитить антисептиком "Зотекс". Средство наносить в 2-3 приёма с интервалом 20-30 минут, и суммарным расходом не менее 0,3л/м2. Средством "Зотекс" обрабатывать древесину, очищенную от грязи, коры и других покрытий кистью, валиком, распылением, вымачиванием или другими способами по ГОСТ 20022.6-93. Обработку проводить при положительной температуре. Не обрабатывать мёрзлую древесину.

Ведомость рабочих чертежей основного комплекта

Лист	Наименование	Примечание
1	Общие данные	А3
2	Общий вид	А3
3	План подвенечного оклада	А3
4	Диагонали подвенечного оклада	А3
5	Узлы устройства стыковки подвенечного оклада	А3
6	Узел П1 - Узел П2	А3
7	Ведомость материалов	А3

Согласовано

Взам. инв. №

Подп. и дата

Инв. № подл.

Изм.	Кол.уч.	Лист	№док.	Подп.	Дата
Разработал		Брусникин Д.М.			30.09.26
Проверил		Москалюк А.Е.			30.09.26
ГИП		Баннов Е.А.			30.09.26


291 - КД3

по адресу: Московская область, Истринский район

Подвенечный оклад	Стадия	Лист	Листов
	Р	1	
Общие данные	ООО "Строй Хауз"		

Формат А3 297 x 420

Общий вид

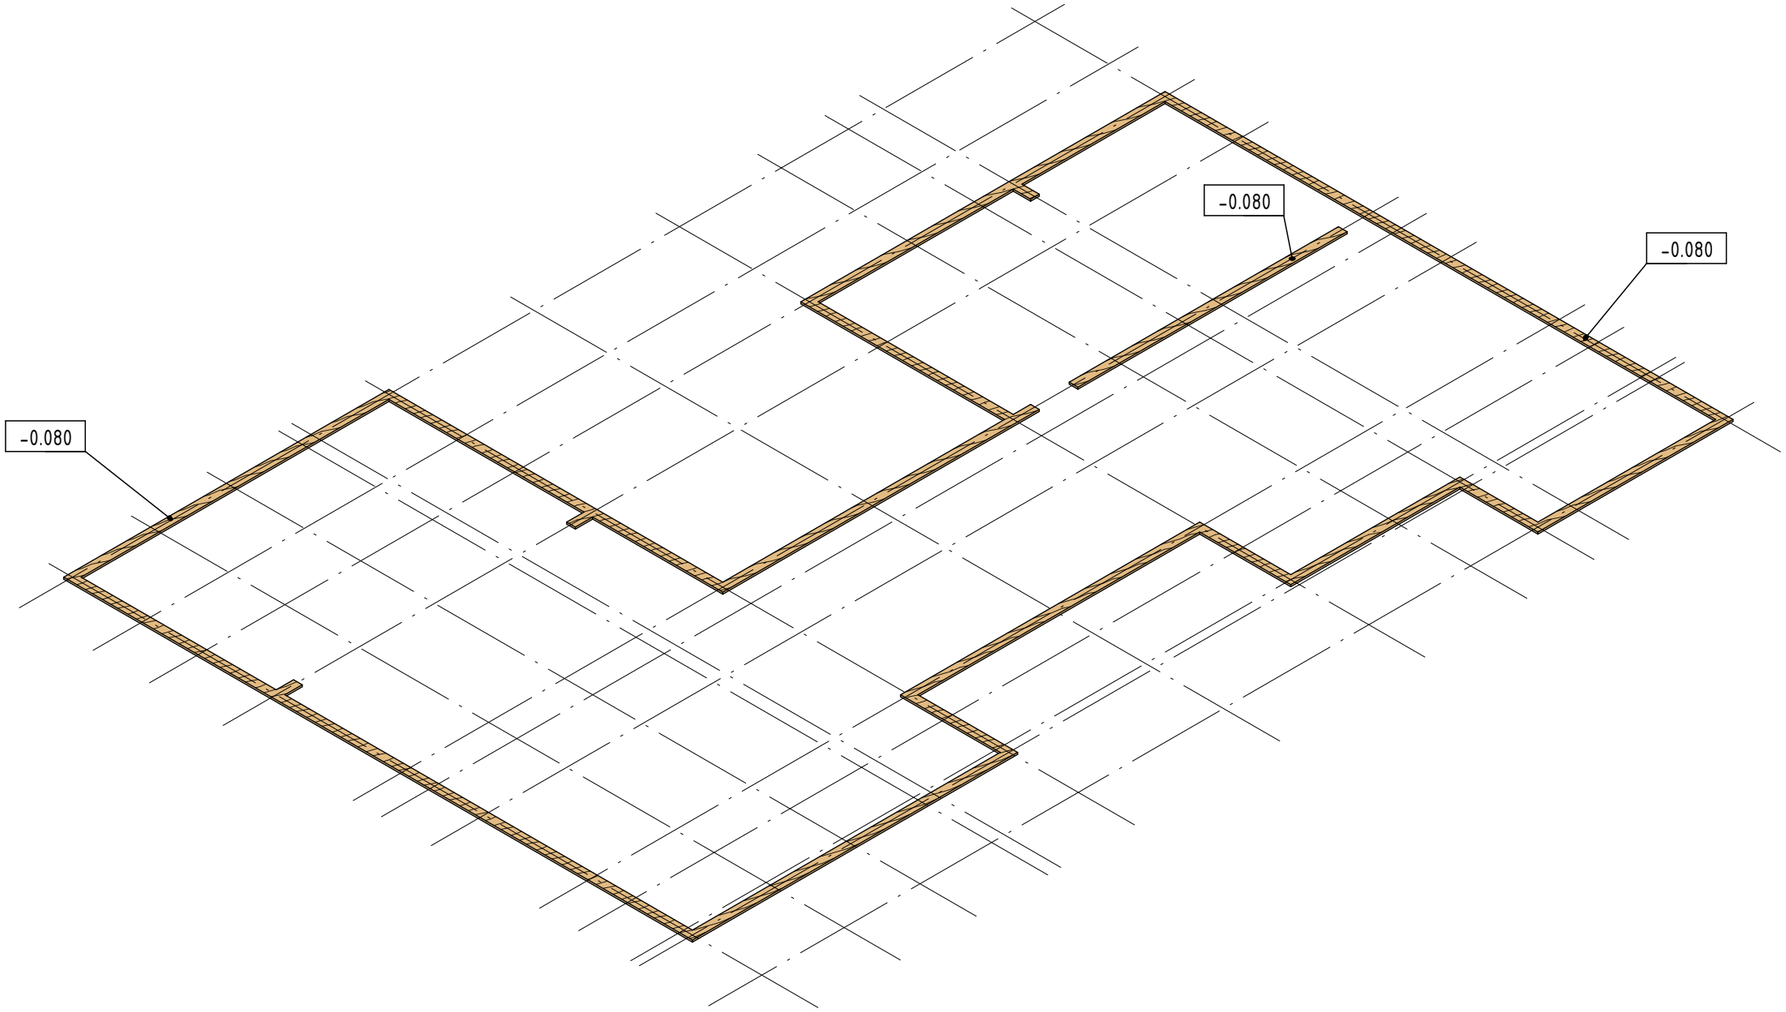

Согласовано

Взам. инв. №

Подп. и дата

Инв. № подл.

Изм.	Кол.уч.	Лист	№док.	Подп.	Дата
Разработал		Брусникин Д.М.			30.09.26
Проверил		Москалюк А.Е.			30.09.26
ГИП		Баннов Е.А.			30.09.26


291 - КДЗ

по адресу: Московская область, Истринский район

Подвенечный оклад	Стадия	Лист	Листов
	Р	2	
Общий вид	ООО "Строй Хауз"		

Формат А3 297 x 420

План подвенечного оклада

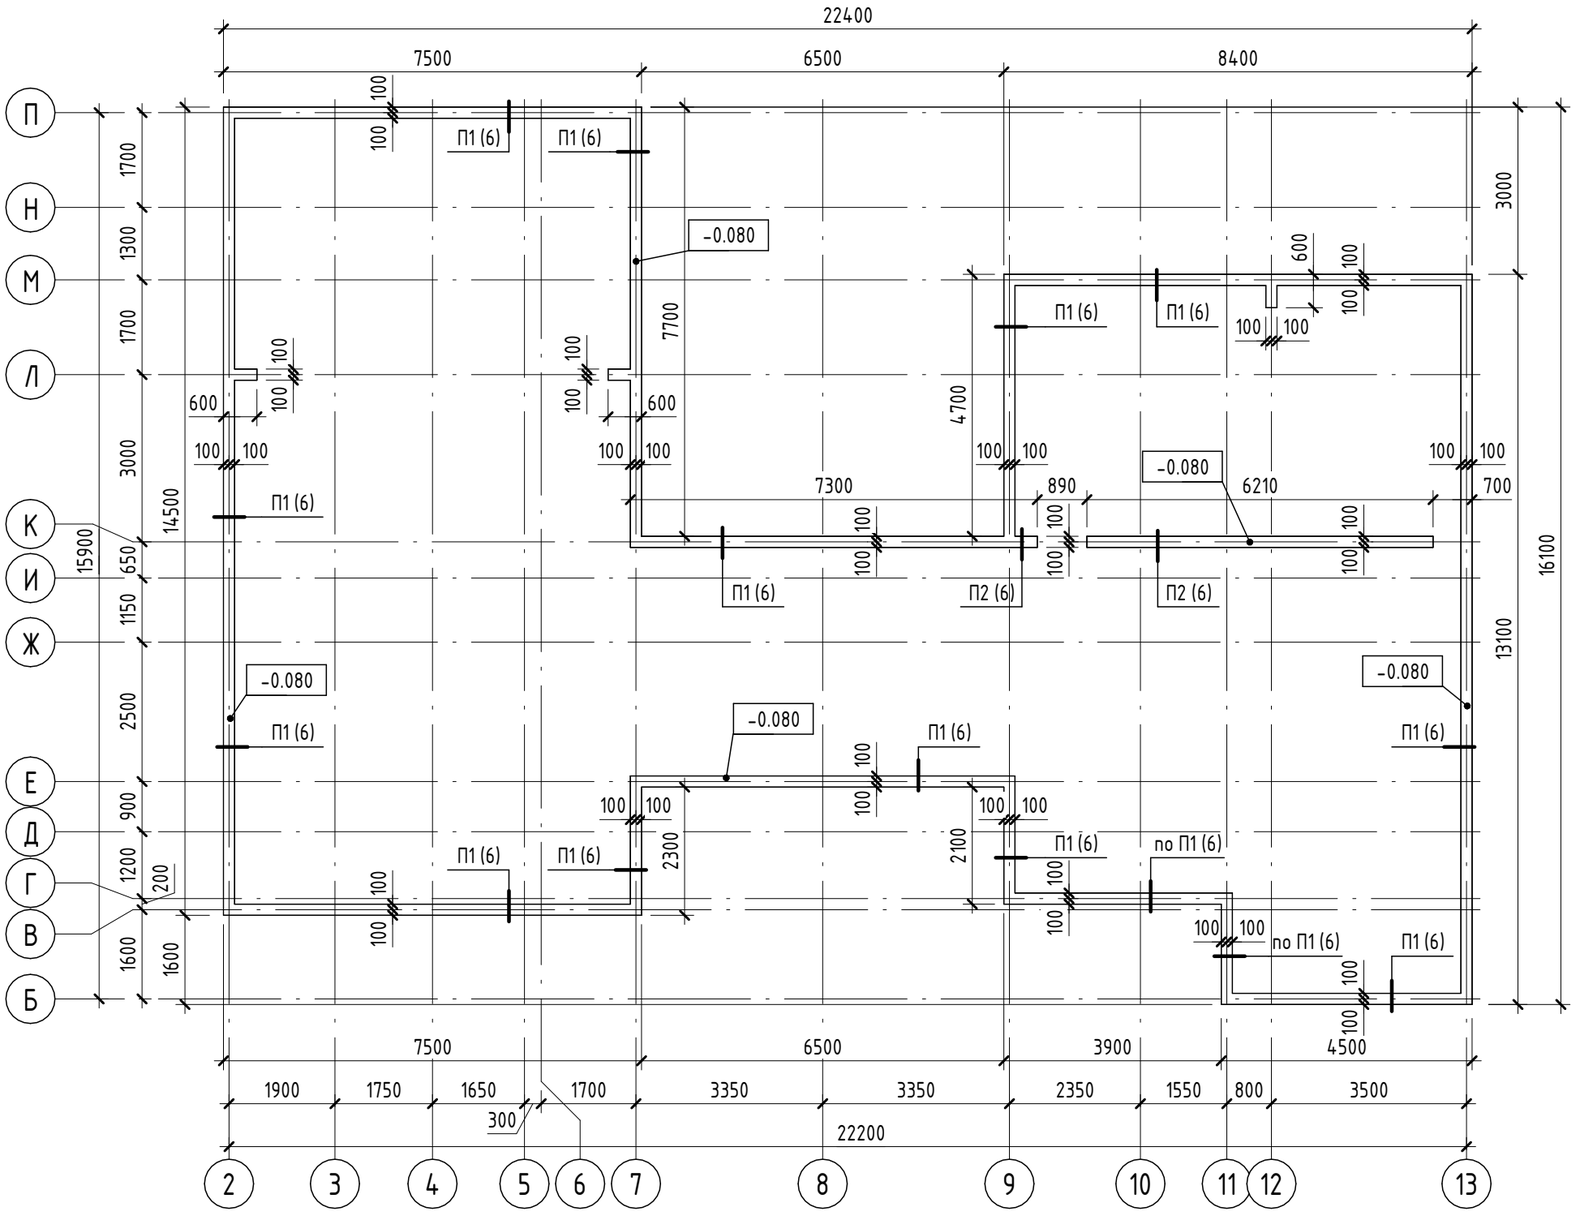

Примечание:
1. Ведомость материалов см. на л. 7;
2. Узлы крепления подвенечного оклада см. на л. 5;
3. В местах расположения клеёных колонн, доску выпилить, колонну монтировать к фундаменту.

Условные обозначения:

- подвенечный оклад, строганая доска 41х200.

Изм.	Кол.уч.	Лист	№док.	Подп.	Дата
Разработал		Брусникин Д.М.			30.09.26
Проверил		Москалюк А.Е.			30.09.26
ГИП		Баннов Е.А.			30.09.26

291 – КДЗ

по адресу: Московская область, Истринский район

Подвенечный оклад	Стадия	Лист	Листов
	Р	3	

План подвенечного оклада

ООО "Строй Хауз"

Согласовано


Взам. инв. №

Подп. и дата

Инв. № подл.

Формат А3 297 х 420

Диагонали подвенечного оклада

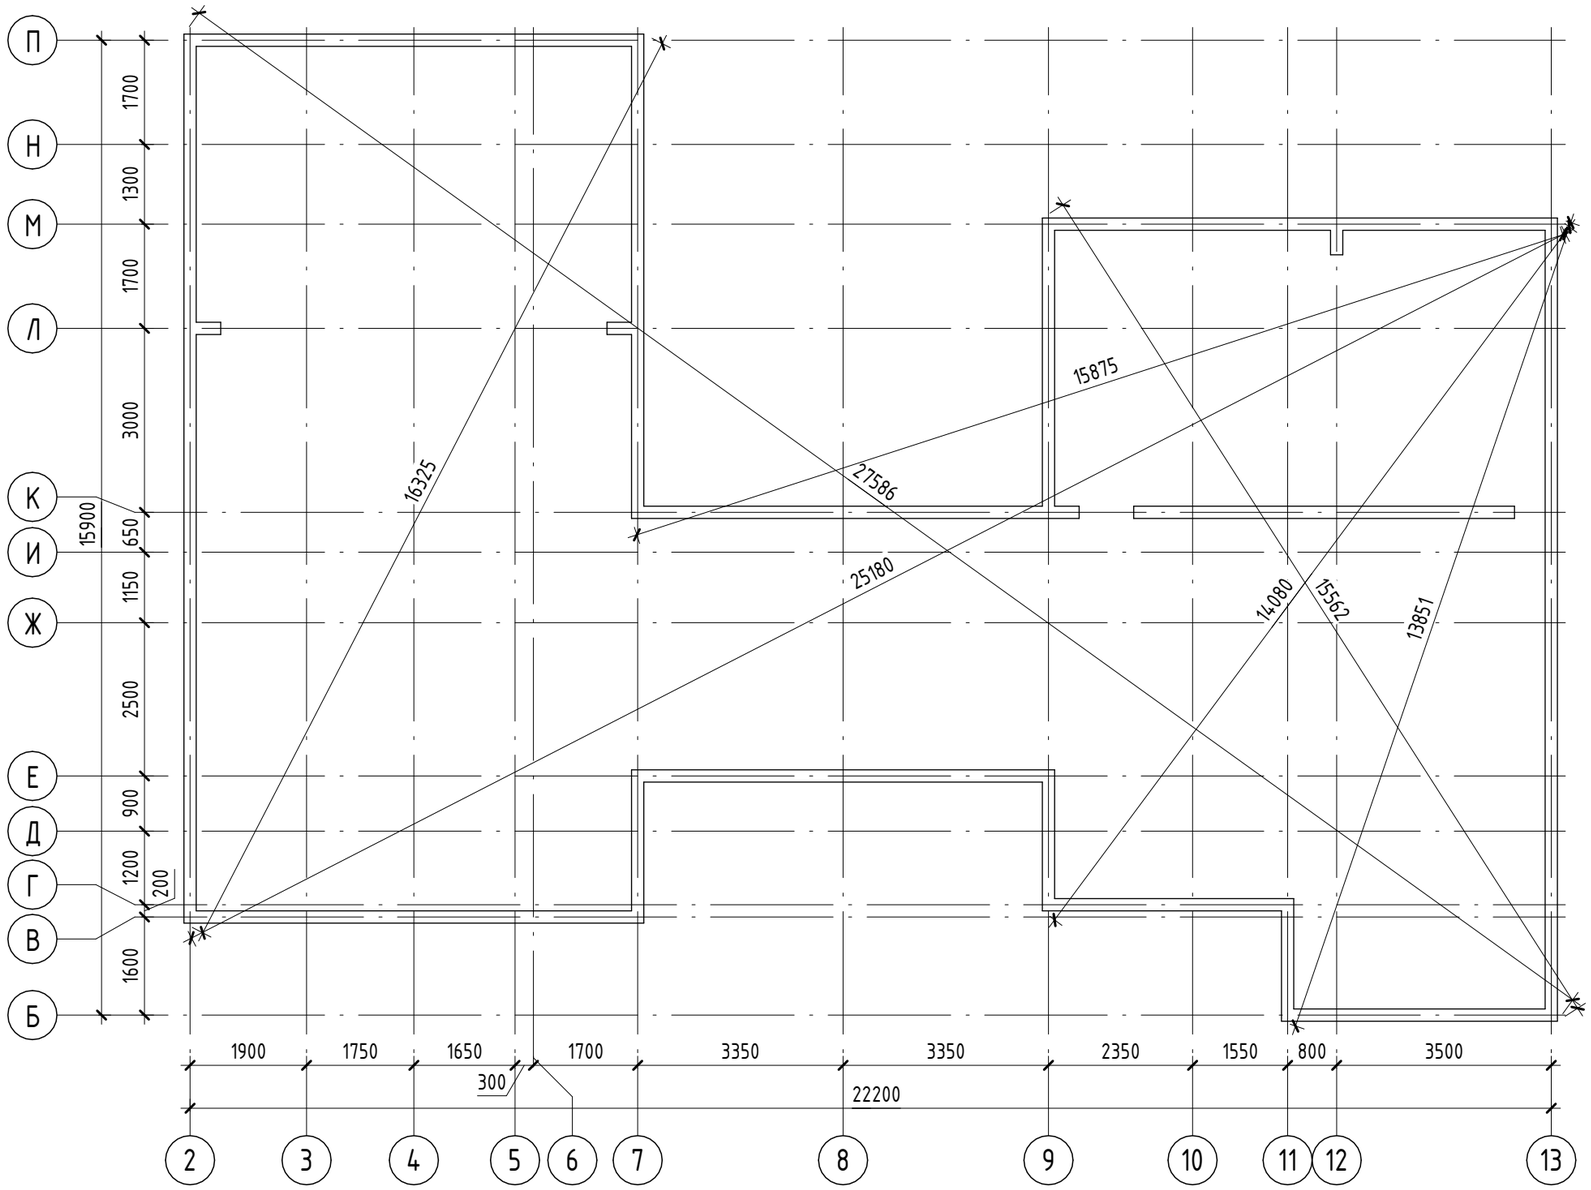

Примечание:
1. Ведомость материалов см. на л. 7;
2. Узлы крепления подвенечного оклада см. на л. 5;
3. В местах расположения клеёных колонн, доску выпилить, колонну монтировать к фундаменту.

Условные обозначения:

– подвенечный оклад, строганая доска 41х200.

Изм.	Кол.уч.	Лист	№док.	Подп.	Дата	291 – КДЗ			
						по адресу: Московская область, Истринский район			
Разработал		Брусникин Д.М.			30.09.26	Подвенечный оклад	Стадия	Лист	Листов
							Р	4	
Проверил		Москалюк А.Е.			30.09.26				
ГИП		Баннов Е.А.			30.09.26	Диагонали подвенечного оклада	ООО "Строй Хауз"		

Согласовано


Взам. инв. №

Подп. и дата


Инв. № подл.

Формат А3 297 х 420


Устройство Г-образного пересечения подвенечного оклада

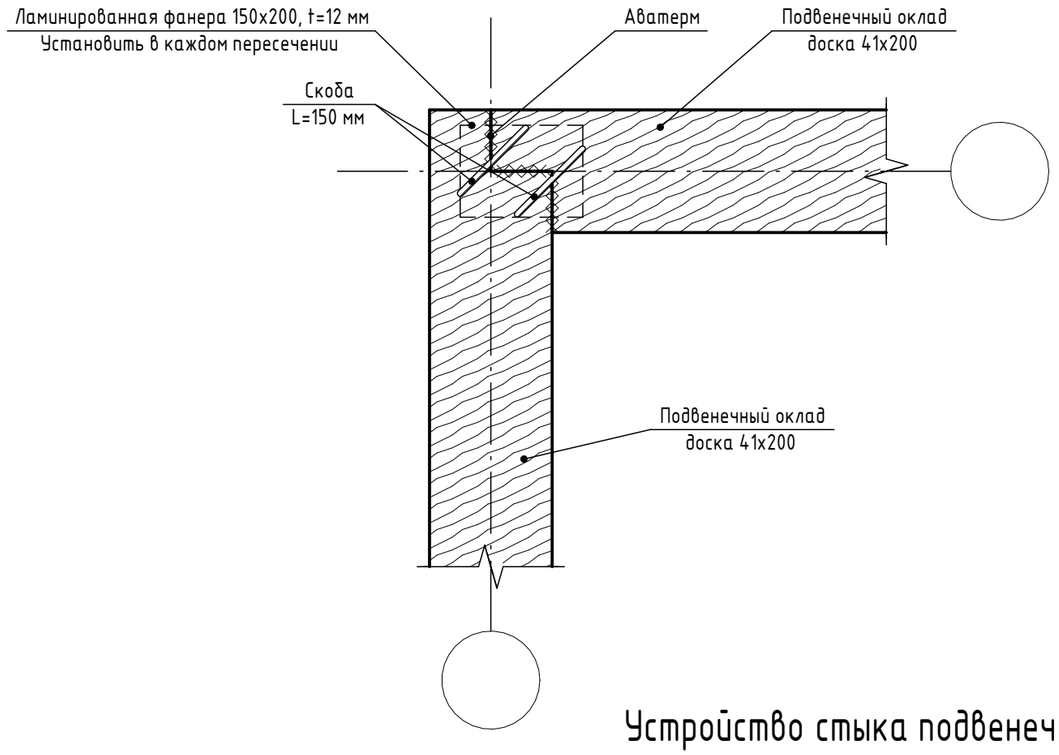

Устройство Т-образного пересечения подвенечного оклада

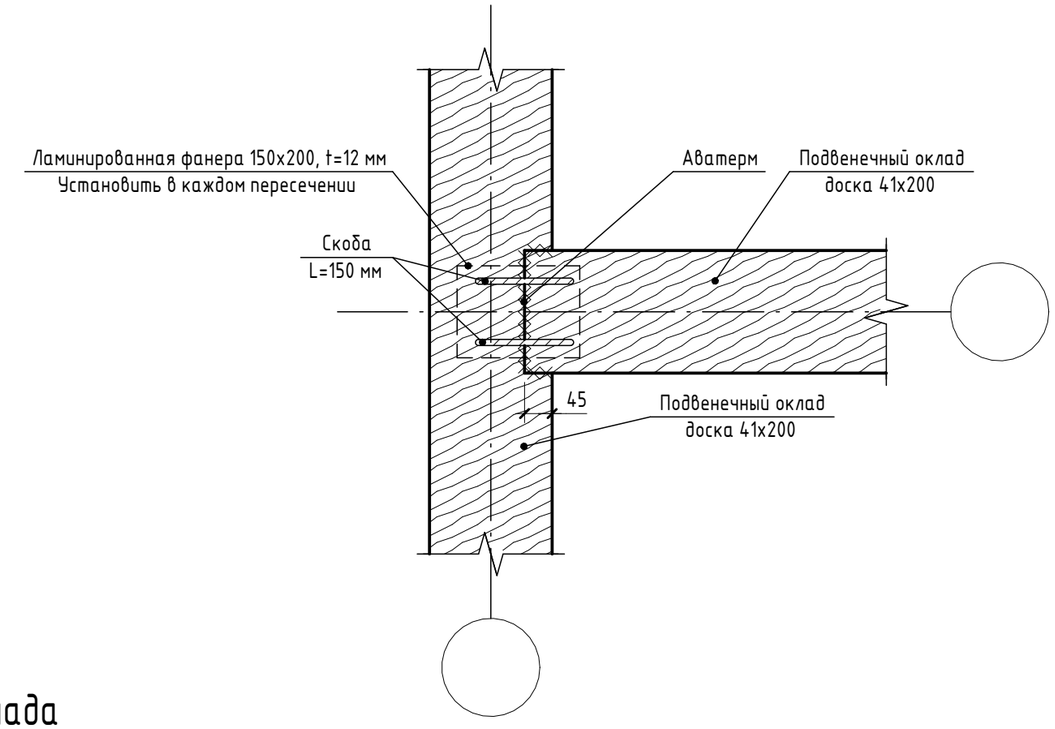

Устройство стыка подвенечного оклада

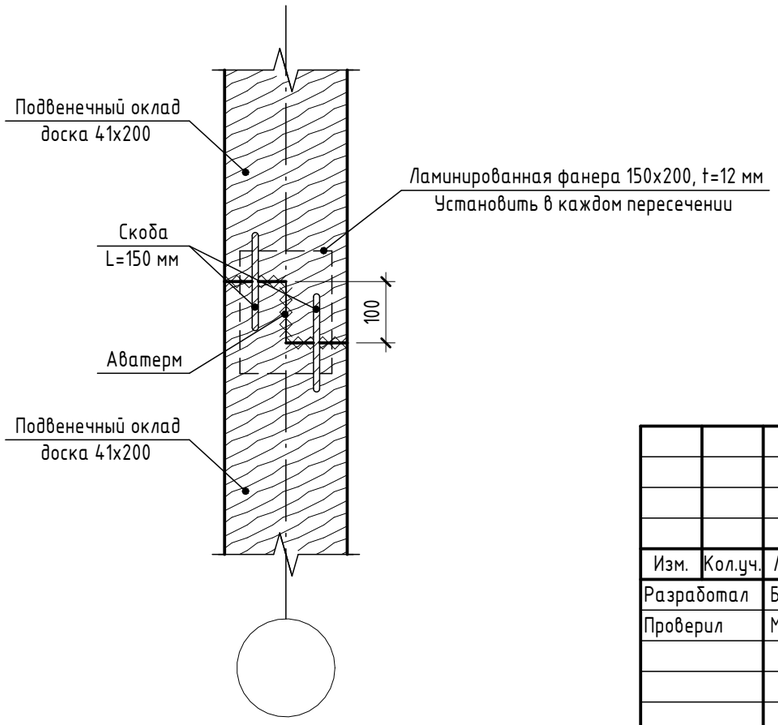

Изм.	Кол.уч.	Лист	№док.	Подп.	Дата
Разработал		Брусникин Д.М.			30.09.26
Проверил		Москалюк А.Е.			30.09.26
ГИП		Баннов Е.А.			30.09.26

291 – КДЗ

по адресу: Московская область, Истринский район

Подвенечный оклад	Стадия	Лист	Листов
	Р	5	
Узлы устройства стыковки подвенечного оклада	ООО "Строй Хауз"		

Согласовано

Взам. инв. №


Подп. и дата

Инв. № подл.

Формат А3 297 х 420


П1
З

(Устройство подвенечного оклада по внешней подвенечной ленте)

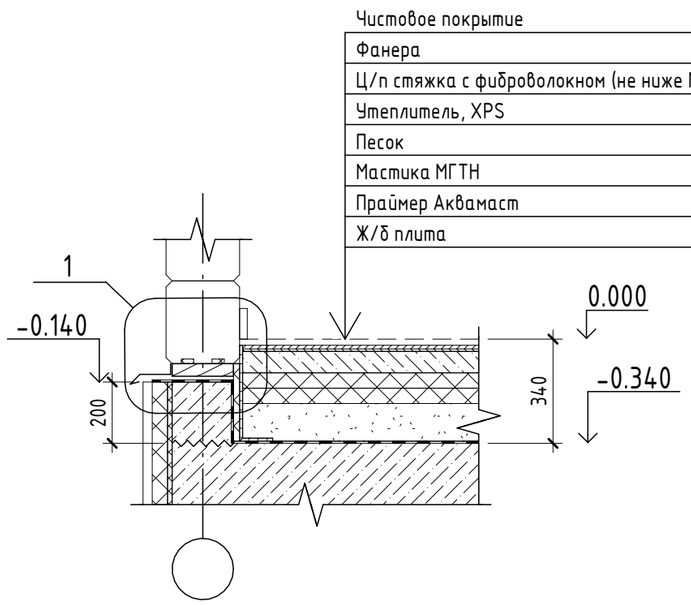


П2
З


(Устройство подвенечного оклада по внутренней подвенечной ленте)

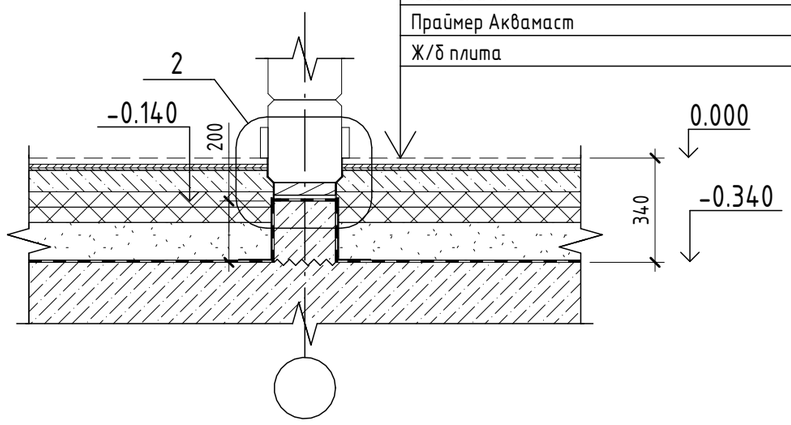

Фрагмент 1

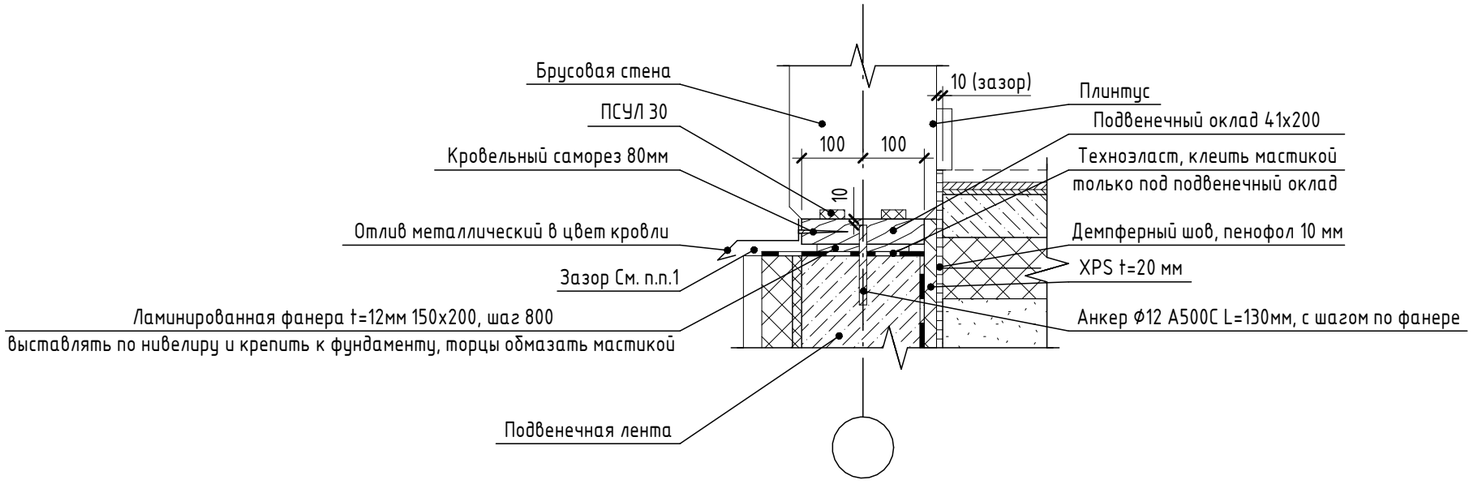

Фрагмент 2

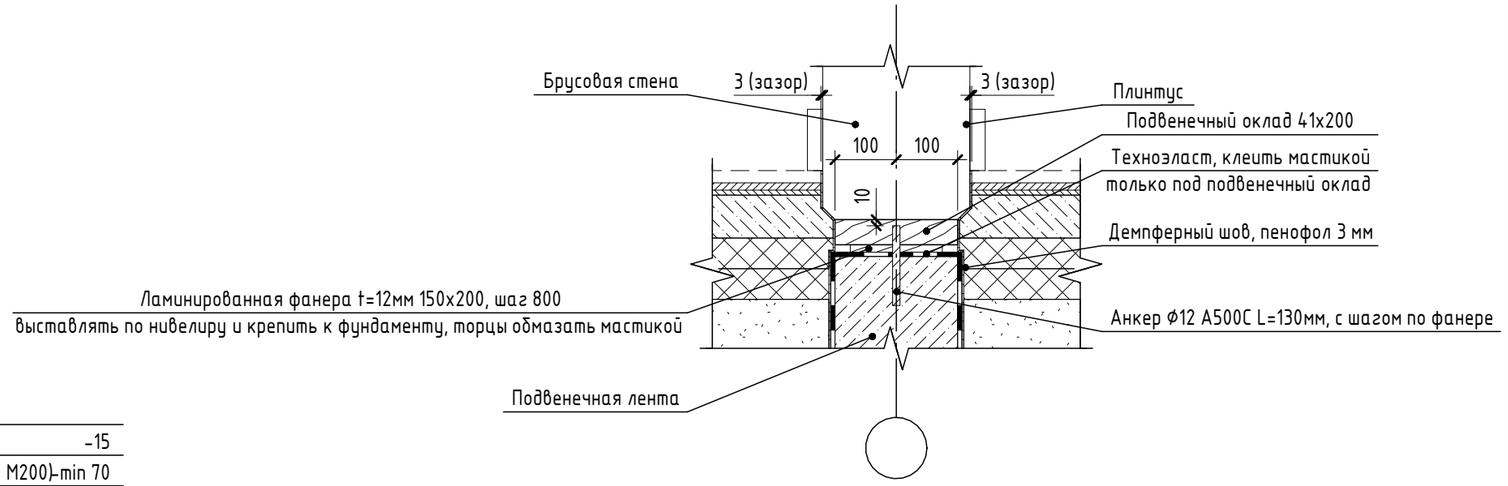

Примечание:

1. Зазор между подвенечным окладом и фундаментом (по теплому контуру здания) заполнить монтажной пеной (на основе пенополиуритана) путем нагнетания пены, нагнетать следует по всей плоскости зазора без воздушных пустот и мешков. После окончательного отвердения пены, выступающие наплывы срезать. Не допускается запенивать зазоры до сборки коробки сооружения. Монтажная пена должна соответствовать по температуре применения в летнее или зимнее время;
2. По окончанию всех работ с монтажной пеной покрыть ее с наружной стороны акрилатным герметиком СТИЗ А, а с внутренней-акрилатным герметиком СТИЗ Б.

Изм.	Кол.уч.	Лист	№док.	Подп.	Дата
Разработал		Брусникин Д.М.			30.09.26
Проверил		Москалюк А.Е.			30.09.26
ГИП		Баннов Е.А.			30.09.26

291 - КДЗ

по адресу: Московская область, Истринский район

Подвенечный оклад	Стадия	Лист	Листов
	Р	6	
Узел П1 - Узел П2	ООО "Строй Хауз"		

Согласовано

Взам. инв. №

Подп. и дата

Инв. № подл.

Формат А3 297 х 420

Ведомость материалов

Поз.	Обозначение	Наименование	Кол.	Объем	Примечание
1	ТУ 5362-001-52036415-2001	Строганая доска 41х200х5700	19	0.89	шт.
2		Антисептик Зотекс	20		л
3	ГОСТ 34028-2016	Арматура Ф12 А500С	24		п.м.
4		Лента Робибанд "ПСУЛ" 50+ 30/4	205		п.м.
5		Ламинированная фанера 2440х1220х12мм	2		листа
6		Полиуретановая пена	19		шт.
7		Герметик Стиз А	15		кг
8		Герметик Стиз Б	15		кг
9		Гидроизоляция Техноэласт ЭПП	40		м2
10		Мастика МГТН №24	22		кг
11		Утеплитель Avaterm 8мм/20см/20м(4м2)	4		м2
12		Скоба L=150мм	56		шт.

Согласовано

Взам. инв. №

Подп. и дата

Инв. № подл.

Изм.	Кол.уч.	Лист	№док.	Подп.	Дата
Разработал		Брусникин Д.М.			30.09.26
Проверил		Москалюк А.Е.			30.09.26
ГИП		Баннов Е.А.			30.09.26

291 – КДЗ

по адресу: Московская область, Истринский район

Подвенечный оклад

Стадия	Лист	Листов
Р	7	

Ведомость материалов

ООО "Строй Хауз"

Формат А4 297 х 210