ООО "Строй Хауз"

Московская обл., Истринский р-н, д. Веледниково, ул. Живописная, д. 25

Берта Ромарио

по адресу: Московская область, Истринский район

Индивидуальный жилой дом

РАБОЧАЯ ДОКУМЕНТАЦИЯ

Раздел КД5.Кровля

(Конструкции деревянные)

291-КД5

Конструктор	Москалюк А.
Проверил	Баннов Е.
ГИП	Баннов Е.



г. Москва 2026г.

Согласовано

Взам. инв. №

Подп. и дата

Инв. № подл.

Формат А4

Ведомость рабочих чертежей основного комплекта

Лист	Наименование	Примечание
1	Ведомость листов	А4
2	Общие данные	А3
3	План кровли	А3
4	План стропильной системы. Маркировочный план	А3
5	План стропильной системы. Монтажный план	А3
6	Узел С1	А3
7	Узлы С2, С3	А3
8	Узлы С4, С5	А3
9	Узлы С6, Сд	А3
10	Узел Сн	А3
11	Устройство флюгарки	А3
12	План водосточной системы и системы снегозадержания	А3
13	Общие фасады	А3
14	Общие виды	А3
15	Спецификация (Начало)	А4
16	Спецификация (Продолжение)	А4
17	Спецификация (Окончание)	А4

Согласовано

Взам. инв. №

Подп. и дата

Инв. № подл.

Изм.	Кол. уч.	Лист	№ док.	Подп.	Дата
Констр.		Москалюк А.Е.			30.09.26
Провер.		Баннов Е.А.			30.09.26
ГИП		Баннов Е.А.			30.09.26

291-КД5

Московская обл., Истринский р-н

Кровля

Стадия	Лист	Листов
Р	1	17

Ведомость листов

ООО "Строй Хауз"

Формат А4

ОБЩИЕ ДАННЫЕ

1. Данный комплект чертежей выполнен на основании архитектурно-планировочных решений;
2. Строительная площадка расположена в I ветровом и III снеговом районах с нормативной глубиной сезонного промерзания:
- глина или суглинок 1,03м;
- супесь, пески пылеватые или мелкие – 1,25м;
- песок средней крупности, крупный или гравелистый – 1,34м;
3. За относительную отметку 0,000 принят уровень чистого пола 1 этажа;
4. Посадку сооружения смотри чертежи генплана;
5. Отклонения в размерах конструкций не должны превышать предельных значений, приведенных в табл.4.11 СП 70.13330.2012 "Несущие и ограждающие конструкции ";
6. Все деревянные конструкции защитить антисептиком;
7. Все стыки пароизоляции проклеить скотчем Finka Inside Tape. К стенам крепить скобой степлера, сплошным швом и проклеить скотчем Finka Inside Tape;
8. При угле ската кровли менее 22 градуса все нахлесты диффузионной мембраны проклеить самоклеящейся лентой Delta Multi Band M60. Нахлест не менее 100мм;
9. Все соединения в зоне утепления уплотнить с помощью Аватерм;
10. Все деревянные конструкции кроме клееных защитить антисептиком "Зотекс". Средство наносить в 2-3 приёма с интервалом 20-30 минут, и суммарным расходом не менее 0,3л/м2. Средством "Зотекс" обрабатывать древесину, очищенную от грязи, коры и других покрытий кистью, валиком, распылением, вымачиванием или другими способами по ГОСТ 20022.6-93. Обработку проводить при положительной температуре. Не обрабатывать мёрзлую древесину.

Ведомость ссылочных и прилагаемых документов


Обозначение	Наименование	Примечание
СП 64. 13330.2017	"Деревянные конструкции"	
СП 20.13330.2016	"Нагрузки и воздействия"	
СП 70.13330.2012	"Несущие и ограждающие конструкции"	
СП 17.13330.2017	"Кровли"	
ГОСТ 20022.6-93	"Защита древесины"	


Ведомость основных комплектов рабочих чертежей

Обозначение	Наименование	Примечание
АР	"Архитектурно-планировочное решение"	
КЖ0	Фундамент	
КД1	Разбрусовка	
КД2	Клееный материал	
КД3	Подвенечный оклад	
КД4	Межэтажные перекрытия	
КД5	Кровля	
КД6	Каркасные перегородки	

Изм.	Кол. уч.	Лист	№ док.	Подп.	Дата	291-КД5			
						Московская обл., Истринский р-н			
Констр.		Москалюк А.Е.			30.09.26	Кровля	Стадия	Лист	Листов
Провер.		Баннов Е.А.			30.09.26		Р	2	
ГИП		Баннов Е.А.			30.09.26	Общие данные	ООО "Строй Хауз"		

Формат А3

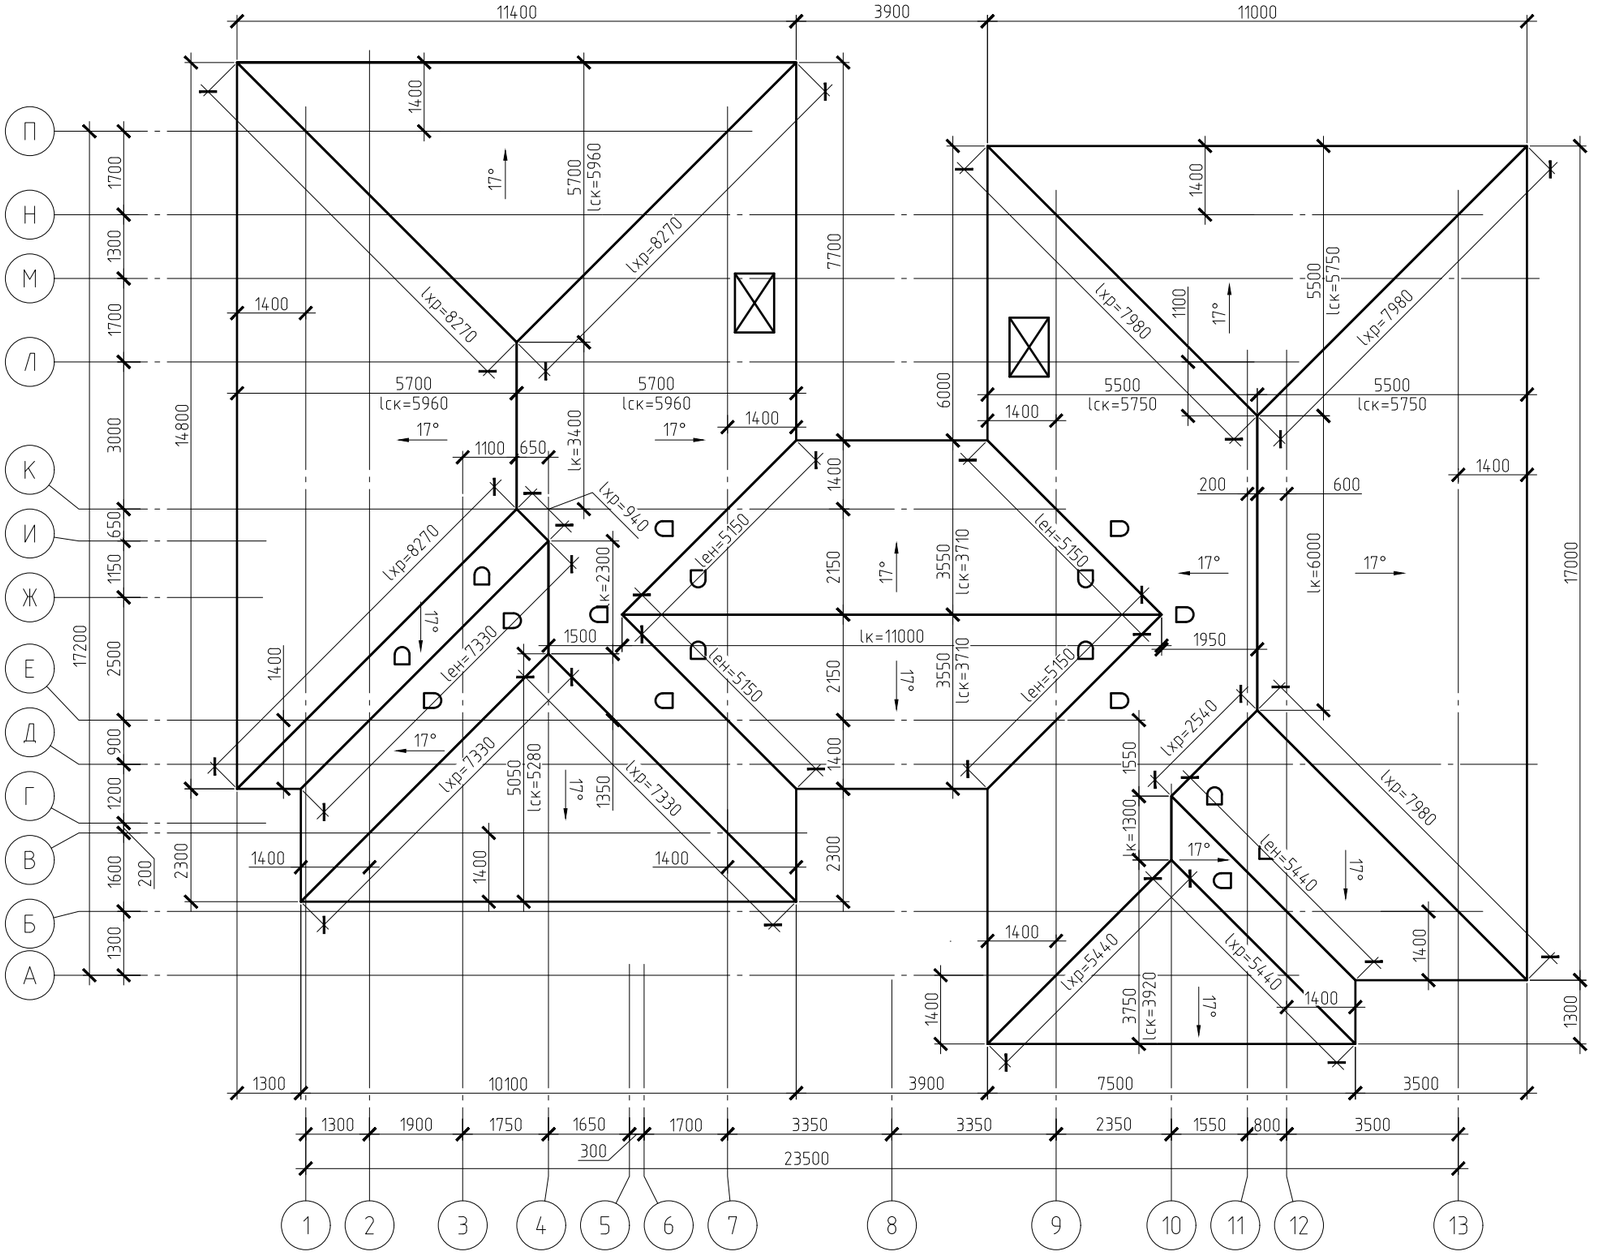

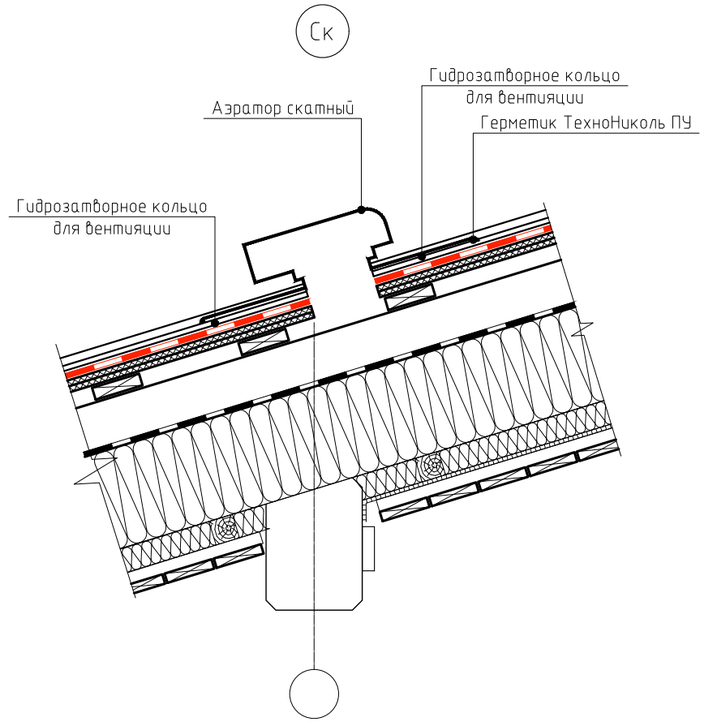

Условные обозначения:


⊠ – дымоход, показан условно

D – кровельный аэратор, см. узел Ск

Примечание:
1. Расположение проходных элементов уточнять по проекту инженерных коммуникаций.

						291-КД5		
						Московская обл., Истринский р-н		
Изм.	Кол. уч.	Лист	№ док.	Подп.	Дата			
Констр.		Москалюк А.Е.			30.09.26	Кровля	Стадия	Лист	Листов
Провер.		Баннов Е.А.			30.09.26		Р	3	
ГИП		Баннов Е.А.			30.09.26	План кровли	ООО "Строй Хауз"		

Формат А3

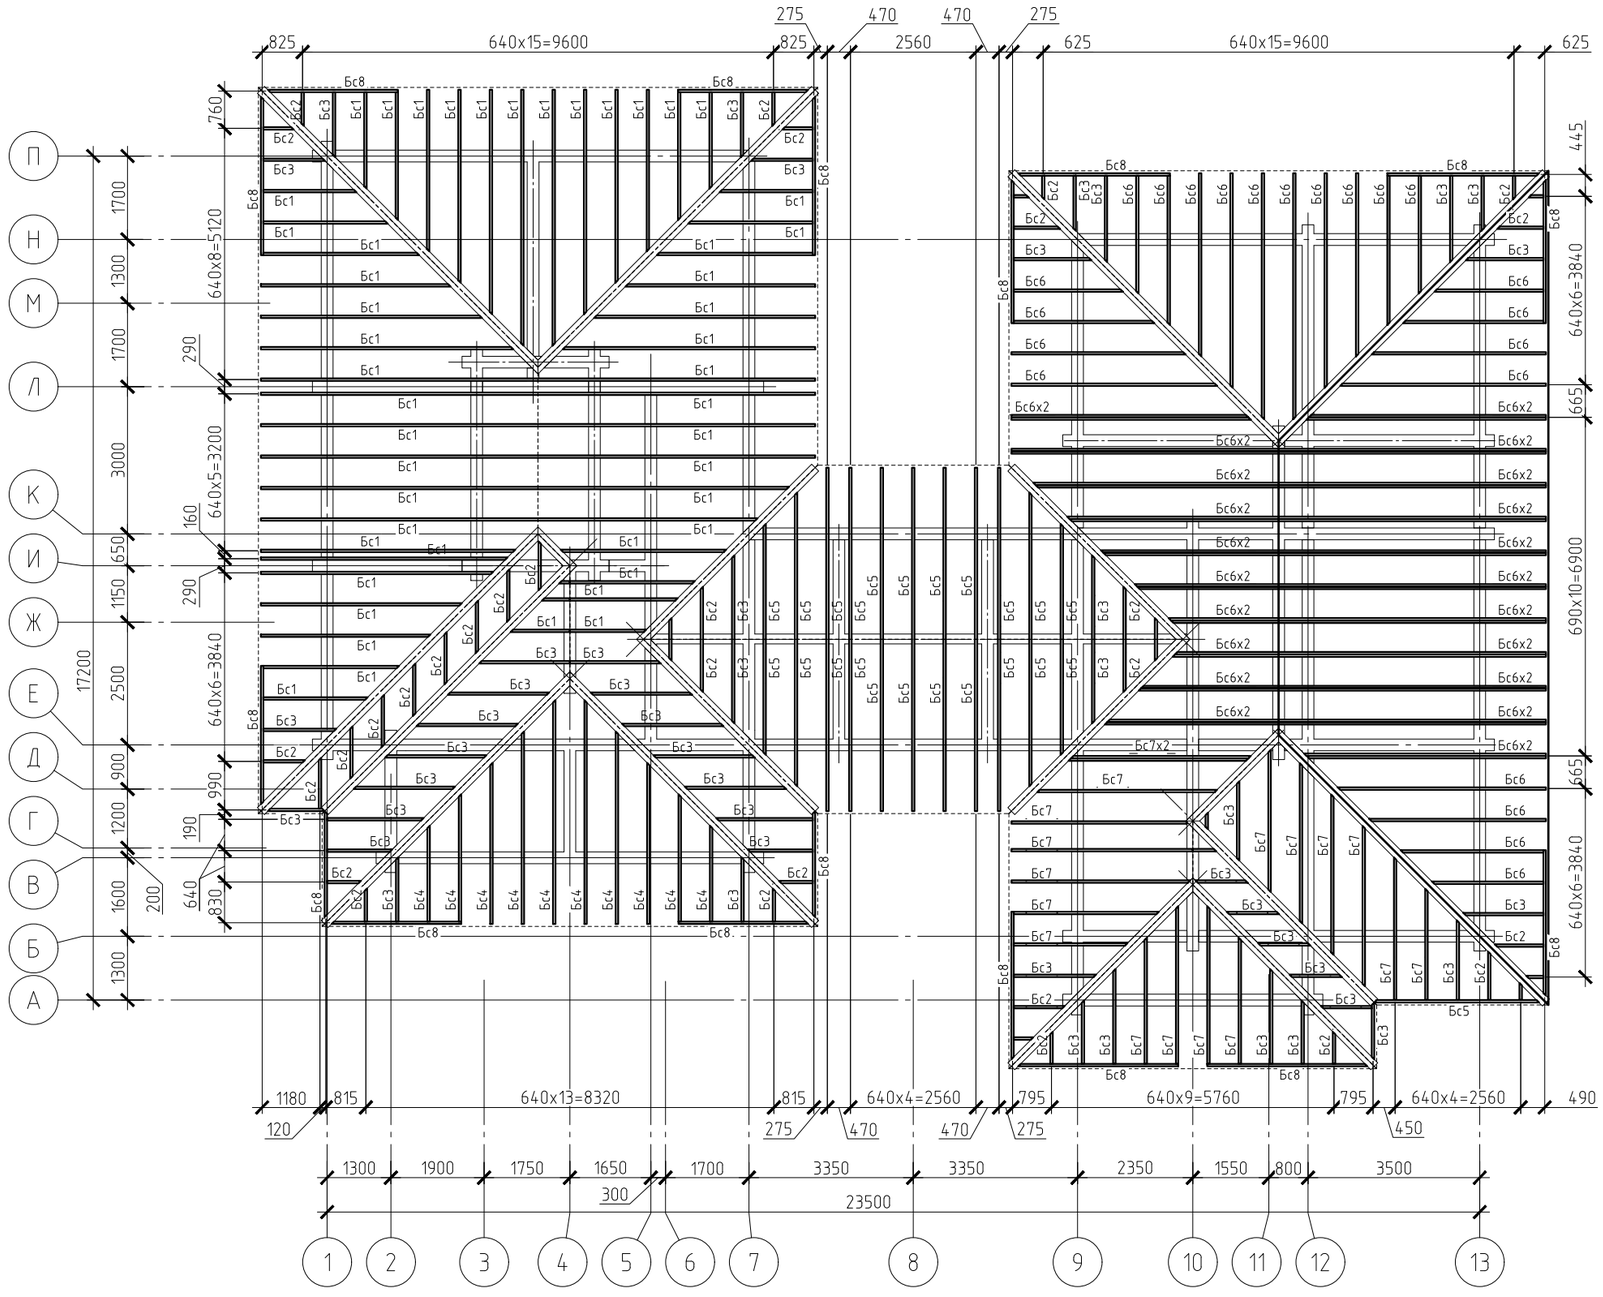

Спецификация элементов

Обозначение	Ширина	Высота	Длина	Кол-во	Примечание
Бс1	50	200	5960	48	Рядовые стропила
Бс2	50	200	1120	30	Рядовые стропила
Бс3	50	200	2060	46	Рядовые стропила
Бс4	50	200	4980	10	Рядовые стропила
Бс5	50	200	3710	22	Рядовые стропила
Бс6	50	200	5750	64	Рядовые стропила
Бс7	50	200	3920	18	Рядовые стропила
Бс8	50	200	3100	17	Рядовые стропила

Условные обозначения:

---------- – контур кровельных скатов

▭ – стропильная доска 50x200(h)

▭ – стропильная доска 2x50x200(h) (наращивать по узлу Сд, см.л.9, min нахлест 600мм)

Примечания:

1. Перемычки, а также стропила к перемычкам крепить на кронштейны WB 11 ерш. гв. 4,2x50 по 6шт.

Изм.	Кол. уч.	Лист	№ док.	Подп.	Дата
Констр.		Москалюк А.Е.			30.09.26
Провер.		Баннов Е.А.			30.09.26
ГИП		Баннов Е.А.			30.09.26

291-КД5

Московская обл., Истринский р-н


Кровля

Стадия	Лист	Листов
Р	4	

План стропильной системы. Маркировочный план

ООО "Строй Хауз"

Формат А3

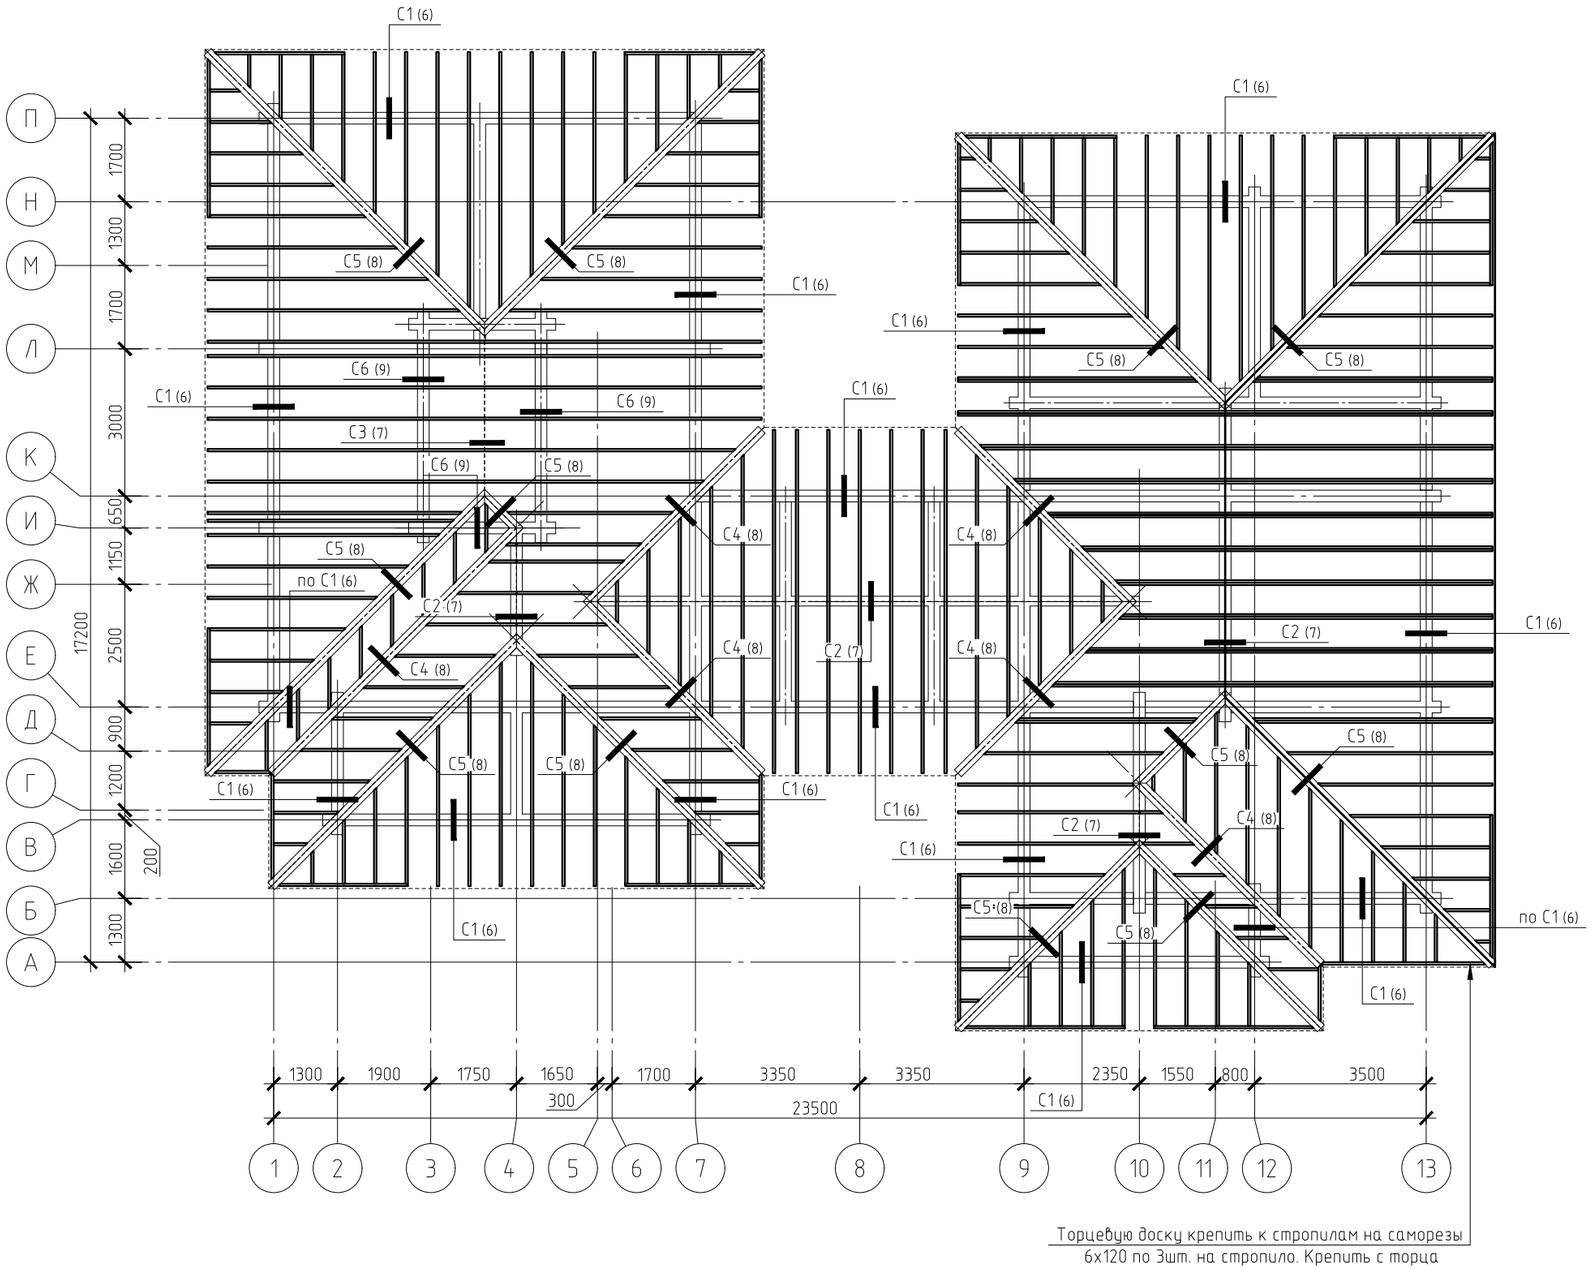

Условные обозначения:

---------- – контур кровельных скатов

– стропильная доска 50х200(h)

– стропильная доска 2х50х200(h) (наращивать по узлу Сд, см.л.9, min нахлест 600мм)

Примечания:

1. Перемычки, а также стропила к перемычкам крепить на кронштейны WB 11 ерш. гв. 4,2х50 по 6шт.

Изм.	Кол. уч.	Лист	№ док.	Подп.	Дата
Констр.		Москалюк А.Е.			30.09.26
Провер.		Баннов Е.А.			30.09.26
ГИП		Баннов Е.А.			30.09.26

291-КД5

Московская обл., Истринский р-н

Кровля

Стадия	Лист	Листов
Р	5	

План стропильной системы.
Монтажный план


ООО "Строй Хауз"

Формат А3

Фальцевое покрытие Кликфальц
Подкладочный ковёр
ОСП δ=12 мм, 2 слоя, см. пр. п. 2
Обрешётка, доска 25х100, шаг 312, см.пр.п.3
Контробрешётка, доска 45х95, шаг по стропилам, см.пр.п.4
Супердиффузионная мембрана Технониколь, см.пр.п.5
Стропило 50х200
Утеплитель 200мм
Обрешётка, брус 45х45, шаг 635, см.пр.п.6
Утеплитель 50мм
Пароизоляция, см.пр.п.8
Обрешётка, доска 18х95, шаг 500, см.пр.п.7

С1 / 5


б – б

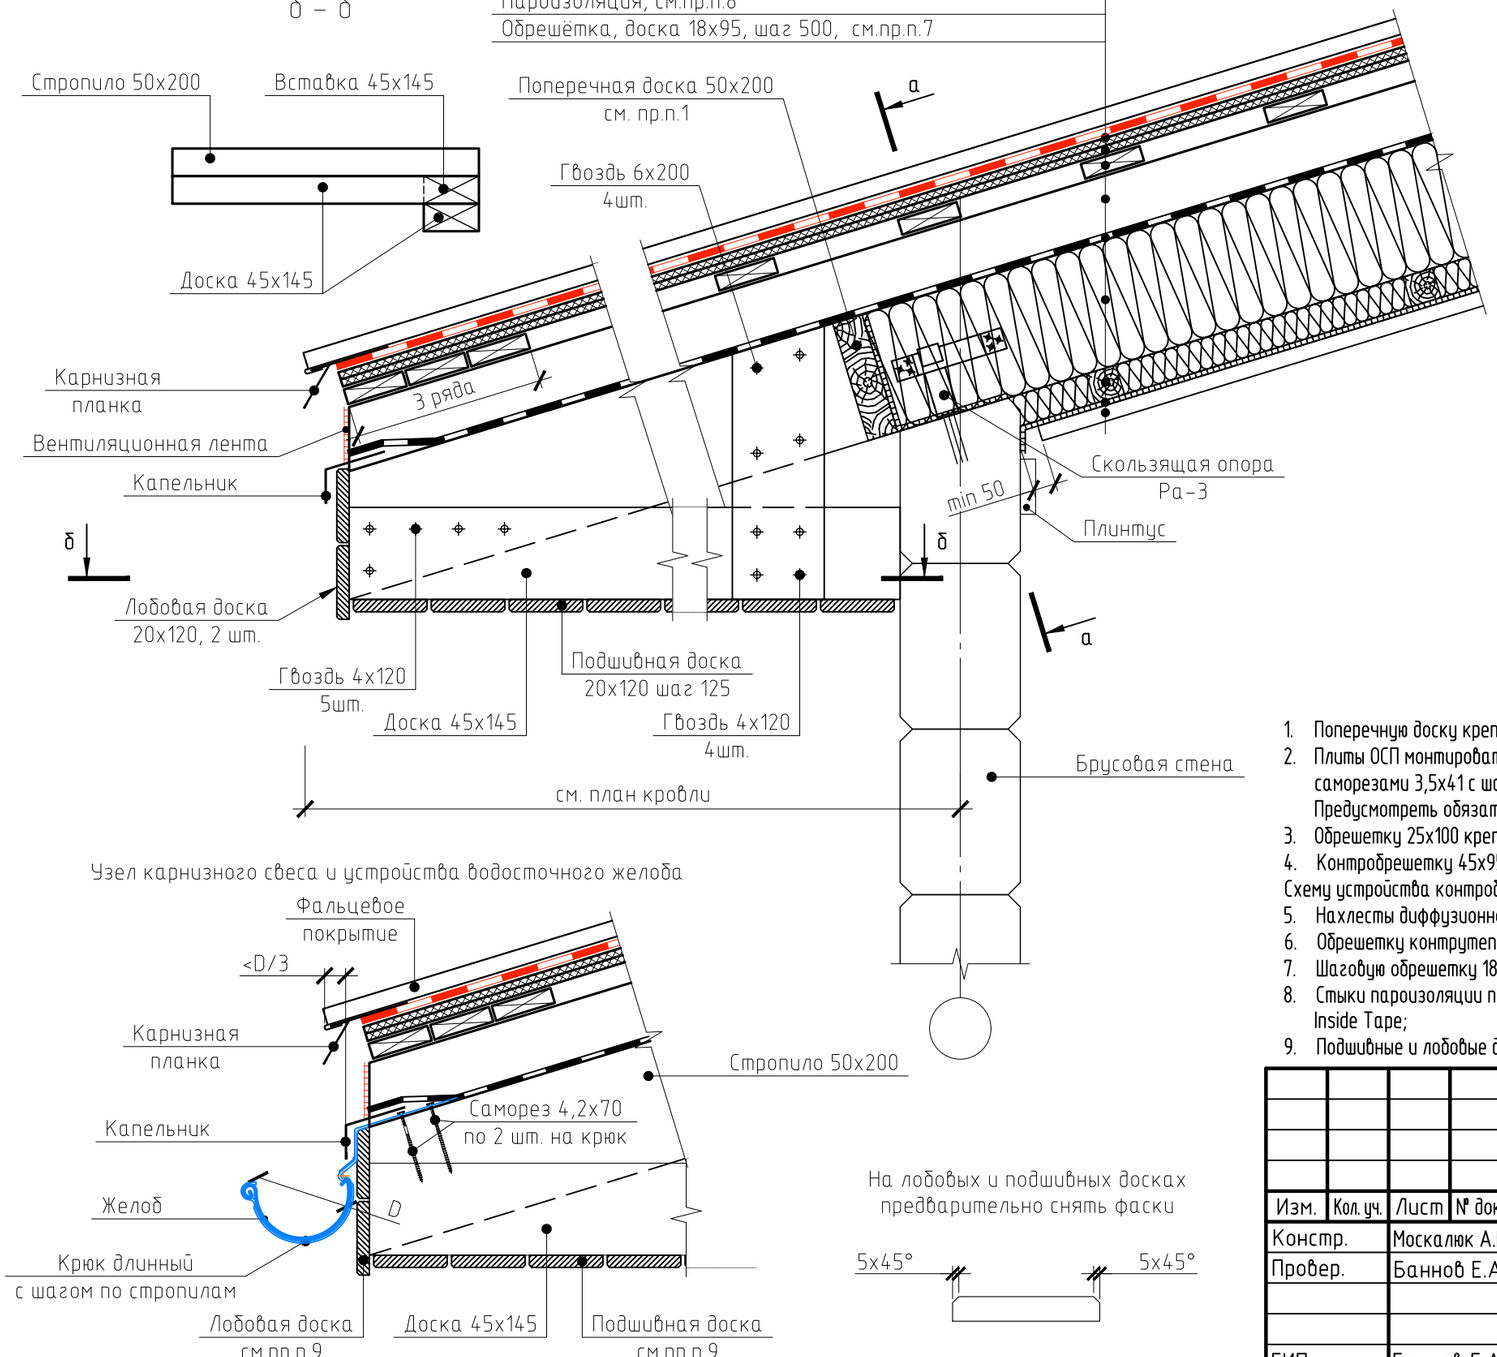

Узел карнизного свеса и устройства водосточного желоба

На лобовых и подшивных досках предварительно снять фаски

а – а

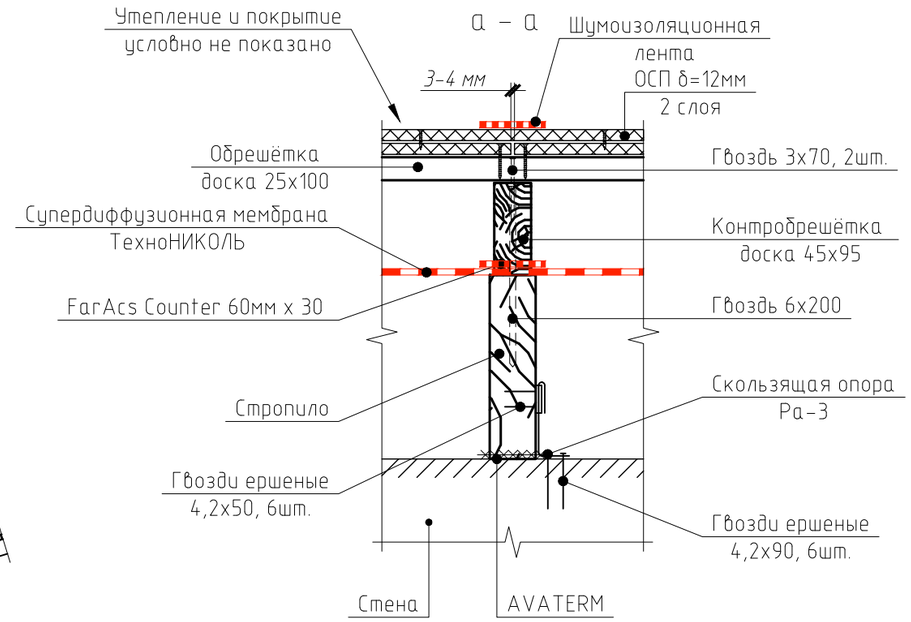

1. Поперечную доску крепить к стропилам гвоздями 4х120, по 2 шт. на сторону под углом;
2. Плиты ОСП монтировать с зазором 3-4 мм между плитами. Первый слой при толщине t=12мм крепить к основанию оксидированными саморезами 3,5х41 с шагом не более 250 мм. Второй слой крепить оксидированными саморезами 3,5х20 с шагом не более 200мм. Предусмотреть обязательный сдвиг второго слоя минимум на 400мм относительно первого;
3. Обрешетку 25х100 крепить к контробрешетке гвоздями 3х70 по 2шт.;
4. Контробрешетку 45х95 крепить к стропилам гвоздями 6х200, с шагом 500 мм, перед забивкой предварительно сверлить отв. ⌀4 мм; Схему устройства контробрешетки см. узел Сн, л.10;
5. Нахлесты диффузионной мембраны проклеивать самоклеящейся лентой Delta Multi Band M60. Нахлест не менее 100 мм;
6. Обрешетку контрутепления 45х45, крепить оцинкованным саморезом 5х100;
7. Шаговую обрешетку 18х95 креп. оцинк. саморезом 3х50 по 2 шт.;
8. Стыки пароизоляции проклеить скотчем Inside Tape . К стенам крепить скобой степлера, сплошным швом и проклеить скотчем Inside Tape;
9. Подшивные и лобовые доски, крепить финишными гвоздями типоразмера 18GA 50 под углом.

Изм.	Кол. уч.	Лист	№ док.	Подп.	Дата
Констр.		Москалюк А.Е.			30.09.26
Провер.		Баннов Е.А.			30.09.26
ГИП		Баннов Е.А.			30.09.26

291-КД5

Московская обл., Истринский р-н

Кровля

Стадия	Лист	Листов
Р	6	


Узел С1

ООО "Строй Хауз"


Формат А3

Фальцевое покрытие Кликфальц
Подкладочный ковёр
ОСП δ=12 мм, 2 слоя, см. пр. п. 2
Обрешётка, доска 25х100, шаг 312, см.пр.п.3
Контробрешётка, доска 45х95, шаг по стропилам, см.пр.п.4
Супердиффузионная мембрана Технониколь, см.пр.п.5
Стропило 50х200
Утеплитель 200мм
Обрешётка, брус 45х45, шаг 635, см.пр.п.6
Утеплитель 50мм
Пароизоляция, см.пр.п.8
Обрешётка, доска 18х95, шаг 500, см.пр.п.7

Схема соединения

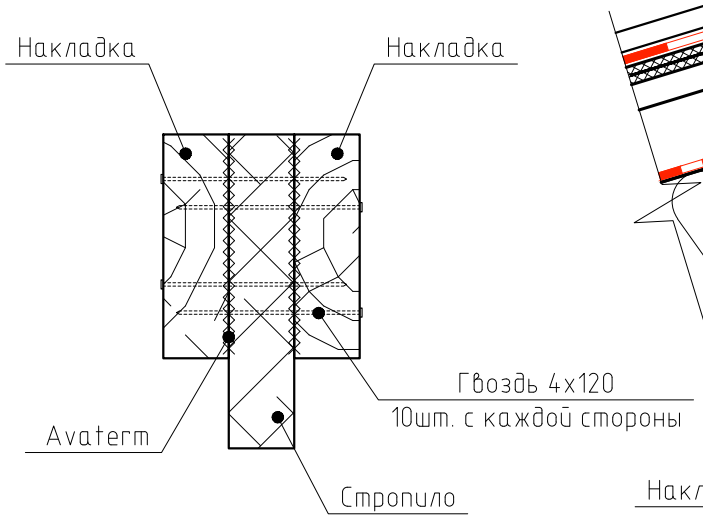


С2
5

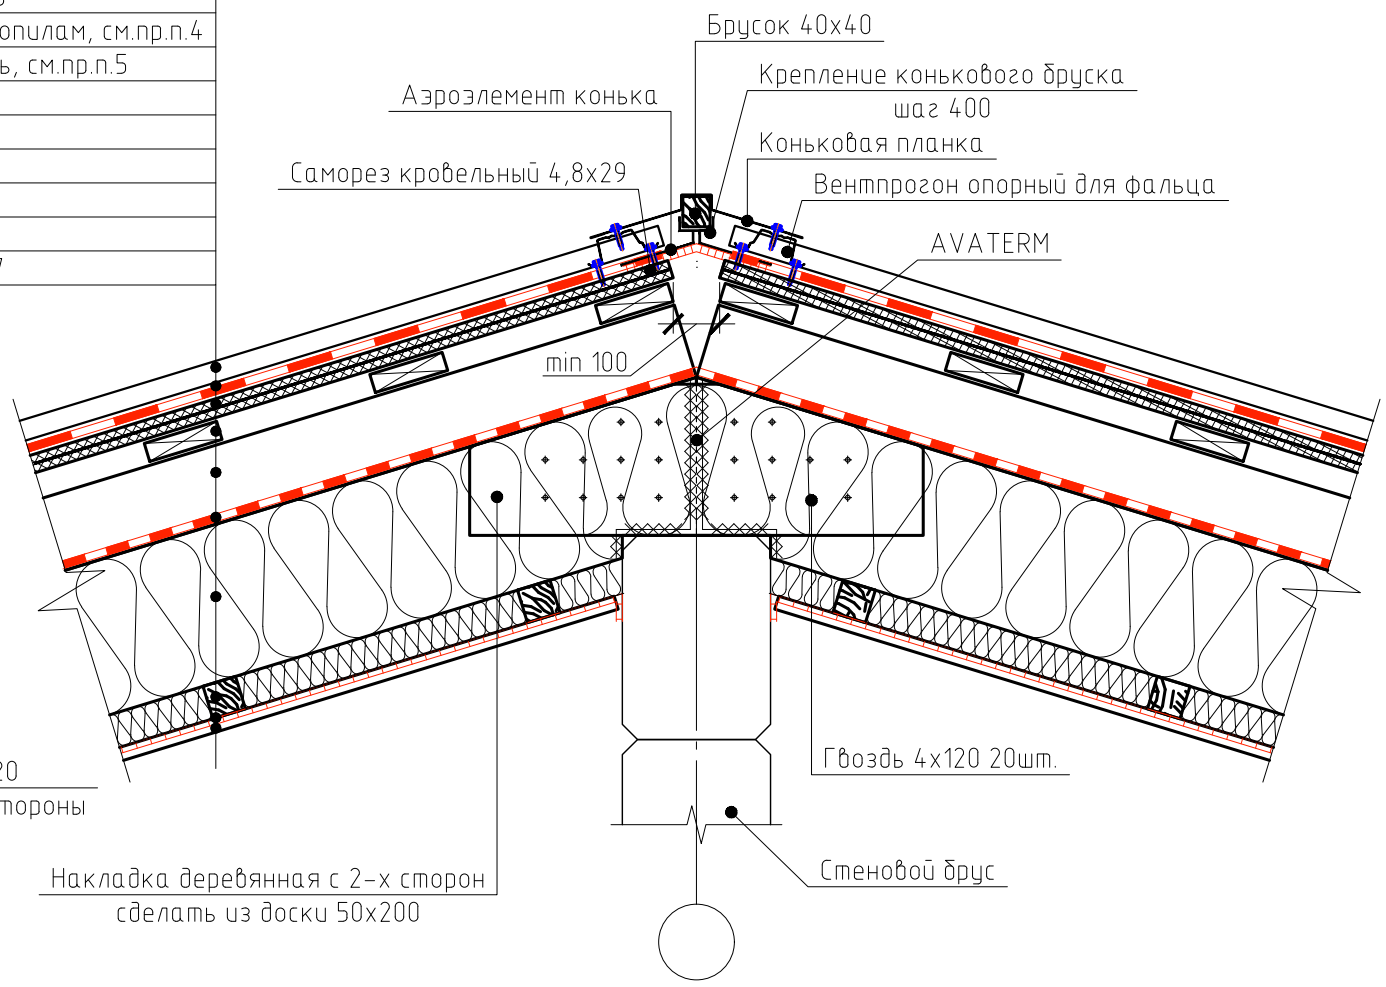

Фальцевое покрытие Кликфальц
Подкладочный ковёр
ОСП δ=12 мм, 2 слоя, см. пр. п. 2
Обрешётка, доска 25х100, шаг 312, см.пр.п.3
Контробрешётка, доска 45х95, шаг по стропилам, см.пр.п.4
Супердиффузионная мембрана Технониколь, см.пр.п.5
Стропило 50х200
Утеплитель 200мм
Обрешётка, брус 45х45, шаг 635, см.пр.п.6
Утеплитель 50мм
Пароизоляция, см.пр.п.8
Обрешётка, доска 18х95, шаг 500, см.пр.п.7

С3
5

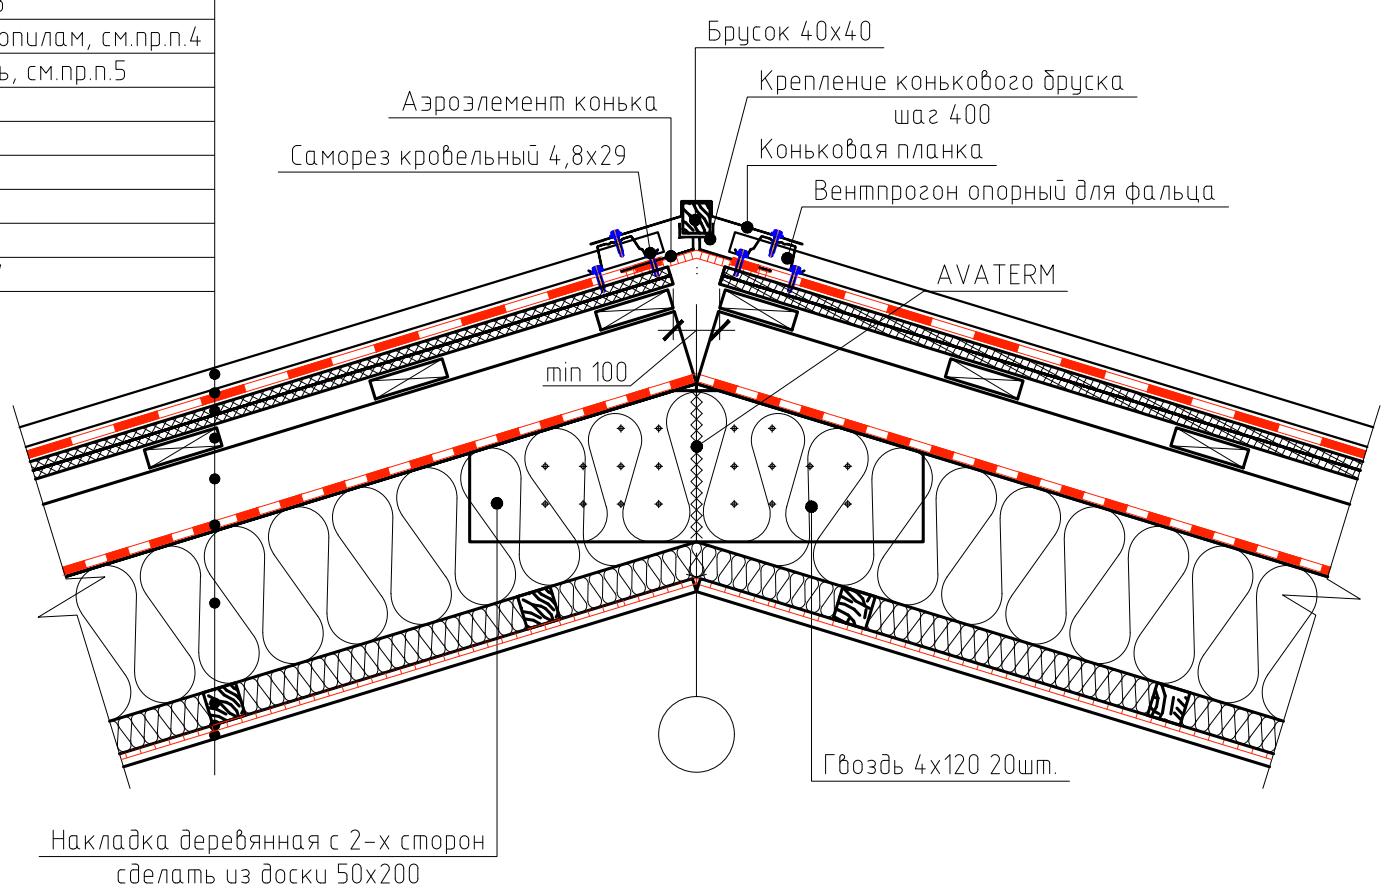

1. Поперечную доску крепить к стропилам гвоздями 4х120, по 2 шт. на сторону под углом;
2. Плиты ОСП монтировать с зазором 3-4 мм между плитами. Первый слой при толщине t=12мм крепить к основанию оксидированными саморезами 3,5х41 с шагом не более 250 мм. Второй слой крепить оксидированными саморезами 3,5х20 с шагом не более 200мм. Предусмотреть обязательный сдвиг второго слоя минимум на 400мм относительно первого;
3. Обрешетку 25х100 крепить к контробрешетка гвоздями 3х70. по 2шт.;
4. Контробрешетку 45х95 крепить к стропилам гвоздями 6х200, с шагом 500 мм, перед забивкой предварительно сверлить отв. ф4 мм. Схему устройства контробрешетки см. узел Сн, л.10;
5. Нахлесты диффузионной мембраны проклеивать самоклеящейся лентой Delta Multi Band M60. Нахлест не менее 100 мм;
6. Обрешетку контрутепления 45х45, крепить оцинкованным саморезом 5х100;
7. Шаговую обрешетку 18х95 креп. оцинк. саморезом 3х50 по 2 шт.;
8. Стыки пароизоляции проклеить скотчем Inside Tape . К стенам крепить скобой степлера, сплошным швом и проклеить скотчем Inside Tape.


Изм.	Кол. уч.	Лист	№ док.	Подп.	Дата	291-КД5			
						Московская обл., Истринский р-н			
Констр.		Москалюк А.Е.			30.09.26	Кровля	Стадия	Лист	Листов
Провер.		Баннов Е.А.			30.09.26		Р	7	
ГИП		Баннов Е.А.			30.09.26	Узлы С2, С3	ООО "Строй Хауз"		

Формат А3

Фальцевое покрытие Кликфальц
Подкладочный ковёр
ОСП δ=12 мм, 2 слоя, см. пр. п. 2
Обрешётка, доска 25х100, шаг 312, см.пр.п.3
Контробрешётка, доска 45х95, шаг по стропилам, см.пр.п.4
Супердиффузионная мембрана Технониколь, см.пр.п.5
Стропило 50х200
Утеплитель 200мм
Обрешётка, брус 45х45, шаг 635, см.пр.п.6
Утеплитель 50мм
Пароизоляция, см.пр.п.8
Обрешётка, доска 18х95, шаг 500, см.пр.п.7


С4
4

а – а (пирог условно не показан)

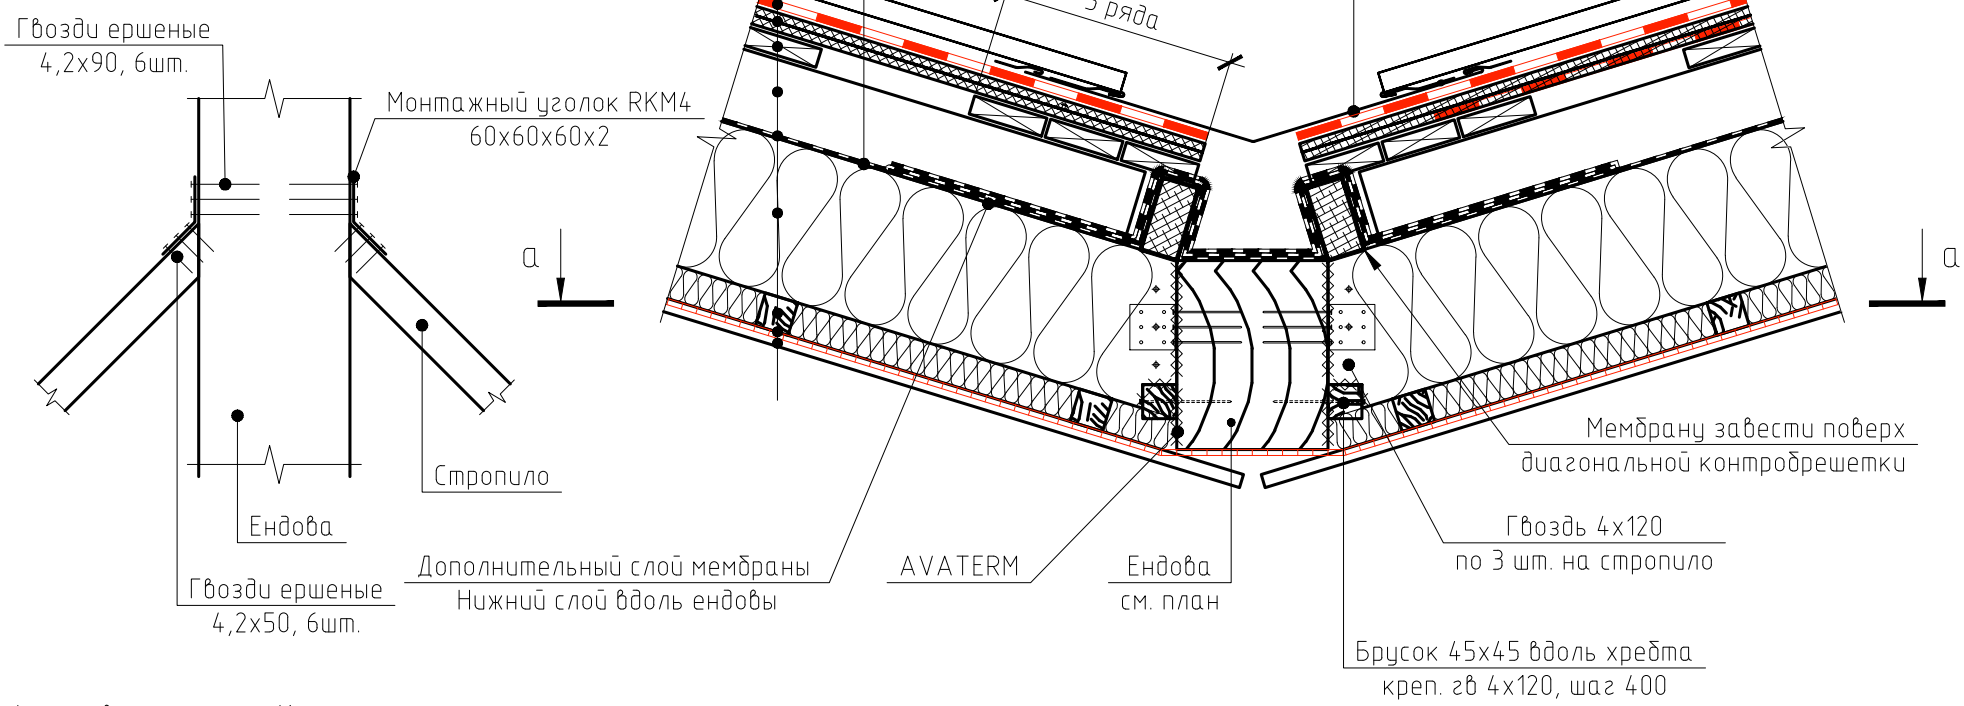

Фальцевое покрытие Кликфальц
Подкладочный ковёр
ОСП δ=12 мм, 2 слоя, см. пр. п. 2
Обрешётка, доска 25х100, шаг 312, см.пр.п.3
Контробрешётка, доска 45х95, шаг по стропилам, см.пр.п.4
Супердиффузионная мембрана Технониколь, см.пр.п.5
Стропило 50х200
Утеплитель 200мм
Обрешётка, брус 45х45, шаг 635, см.пр.п.6
Утеплитель 50мм
Пароизоляция, см.пр.п.8
Обрешётка, доска 18х95, шаг 500, см.пр.п.7

С5
4

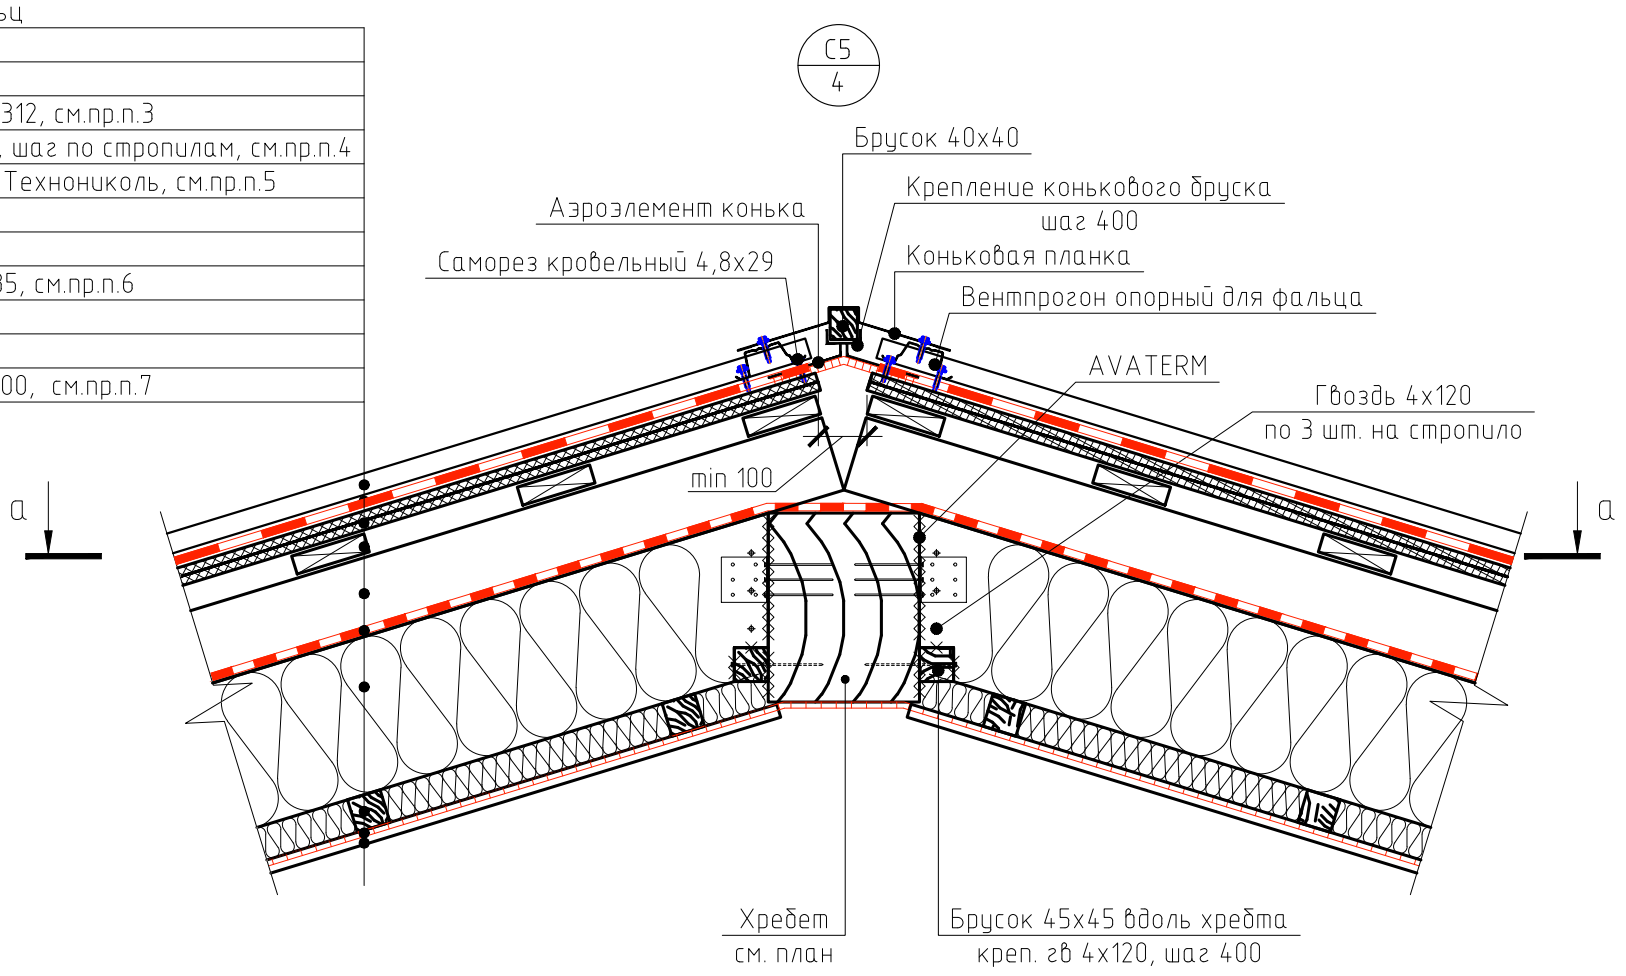


1. Поперечную доску крепить к стропилам гвоздями 4х120, по 2 шт. на сторону под углом;
2. Плиты ОСП монтировать с зазором 3–4 мм между плитами. Первый слой при толщине t=12мм крепить к основанию оксидированными саморезами 3,5х41 с шагом не более 250 мм. Второй слой крепить оксидированными саморезами 3,5х20 с шагом не более 200мм. Предусмотреть обязательный сдвиг второго слоя минимум на 400мм относительно первого;
3. Обрешетку 25х100 крепить к контробрешетка гвоздями 3х70. по 2шт.;
4. Контробрешетку 45х95 крепить к стропилам гвоздями 6х200, с шагом 500 мм, перед забивкой предварительно сверлить отв. ф4 мм. Схему устройства контробрешетки см. узел Сн, л.10;
5. Нахлесты диффузионной мембраны проклеивать самоклеящейся лентой Delta Multi Band M60. Нахлест не менее 100 мм;
6. Обрешетку контрутепления 45х45, крепить оцинкованным саморезом 5х100;
7. Шаговую обрешетку 18х95 креп. оцинк. саморезом 3х50 по 2 шт.;
8. Стыки пароизоляции проклеить скотчем Inside Tape . К стенам крепить скобой степлера, сплошным швом и проклеить скотчем Inside Tape.


Изм.	Кол. уч.	Лист	№ док.	Подп.	Дата	291-КД5			
						Московская обл., Истринский р-н			
Констр.		Москалюк А.Е.			30.09.26	Кровля	Стадия	Лист	Листов
Провер.		Баннов Е.А.			30.09.26		Р	8	
ГИП		Баннов Е.А.			30.09.26	Узлы С4, С5	ООО "Строй Хауз"		

Формат А3

С6
5

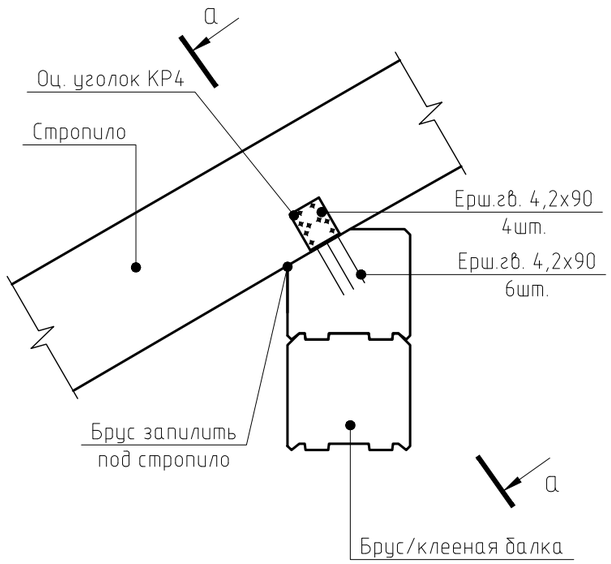


а – а

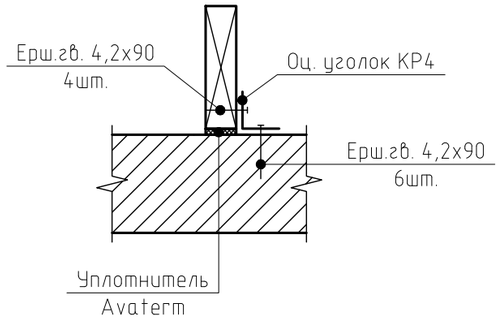

Примечание:
1. Пирог кровли аналогичен узлу С1.

Сд

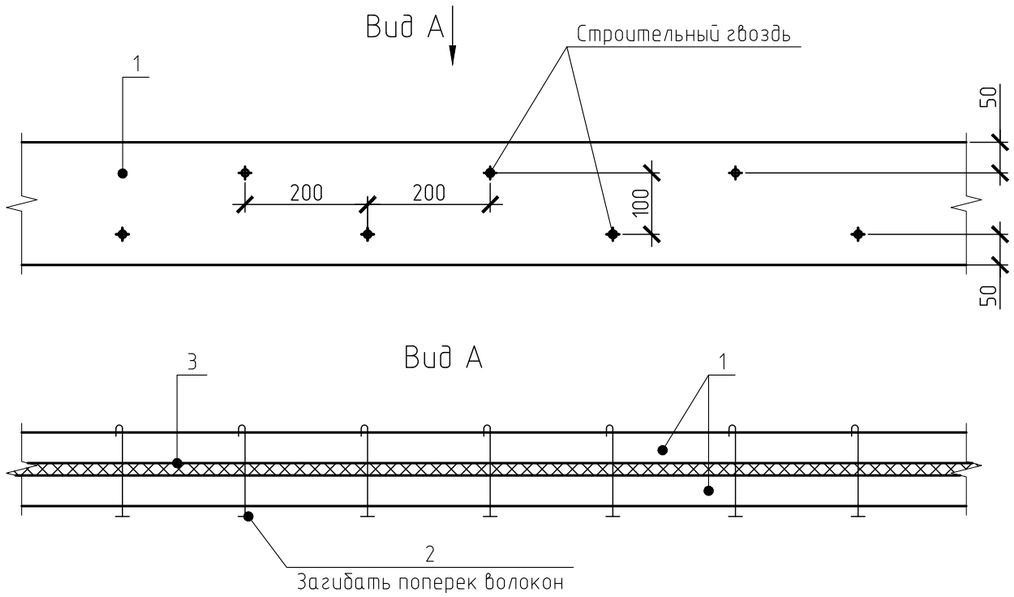


Обозн-е	Наименование	Обозн-е	Наименование
1	Доска 50х200(h)	4	Строительный гвоздь 6х200 шаг 200 в шахм. порядке
2	Строительный гвоздь 4х120 шаг 200 в шахм. порядке		
3	Уплотнитель AVATERM		

Изм.	Кол. уч.	Лист	№ док.	Подп.	Дата				
Констр.		Москалюк А.Е.			30.09.26	291-КД5			
Провер.		Баннов Е.А.			30.09.26	Московская обл., Истринский р-н			
						Кровля	Стадия	Лист	Листов
							Р	9	
ГИП		Баннов Е.А.			30.09.26	Узлы С6, Сд	ООО "Строй Хауз"		

Формат А3

Сн

Схема устройства контробрешетки

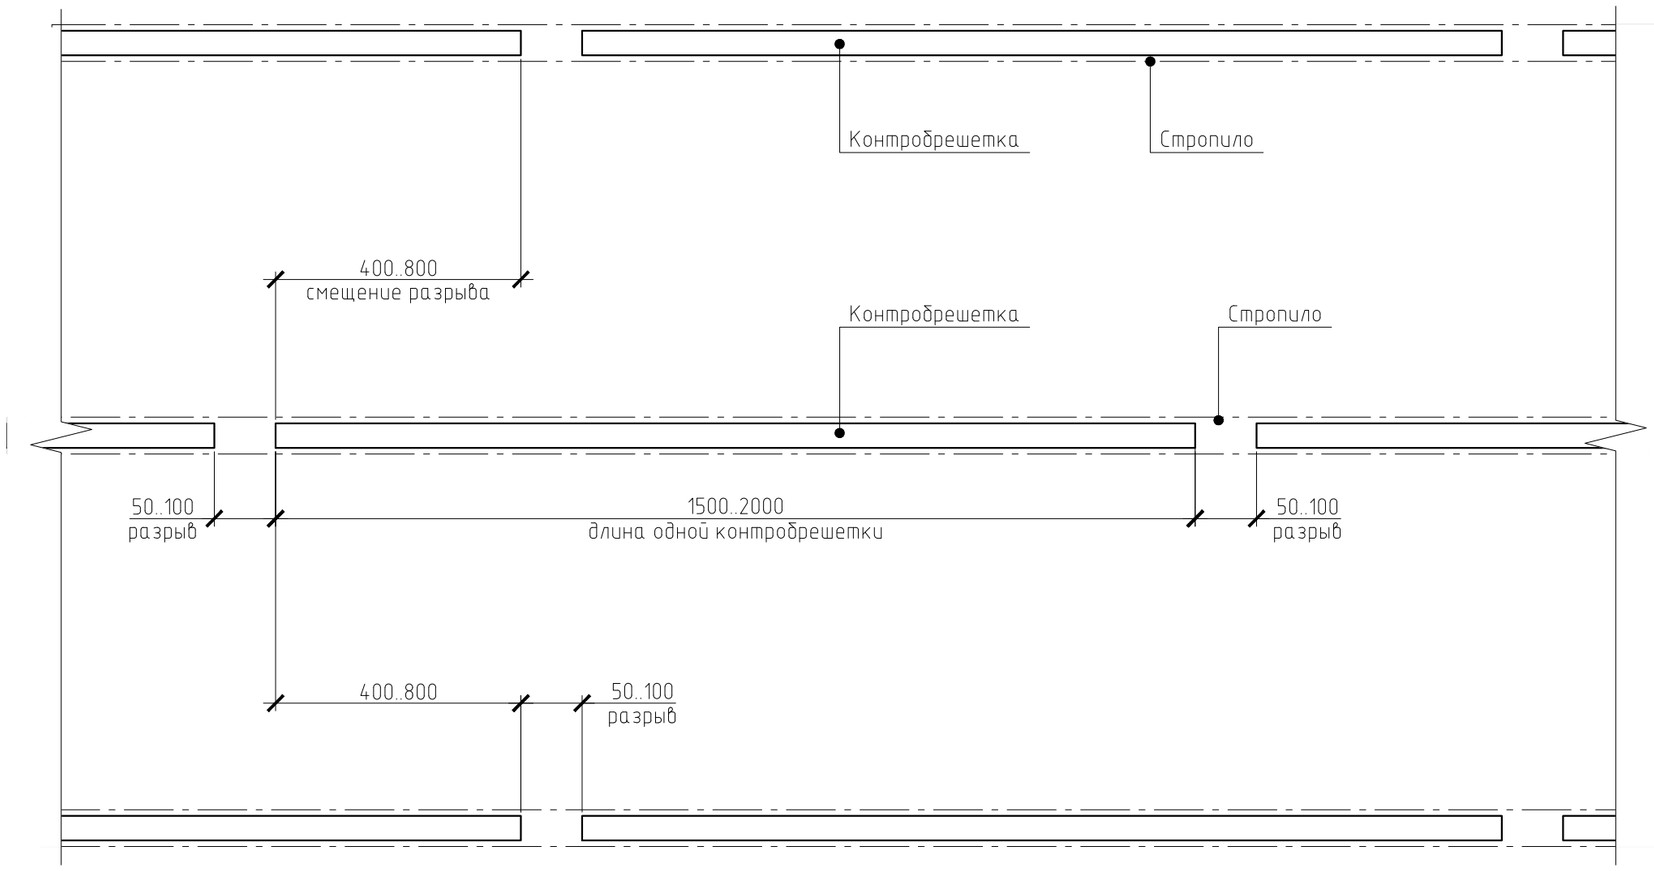

Изм.	Кол. уч.	Лист	№ док.	Подп.	Дата
Констр.		Москалюк А.Е.			30.09.26
Провер.		Баннов Е.А.			30.09.26
ГИП		Баннов Е.А.			30.09.26


291-КД5

Московская обл., Истринский р-н

Кровля	Стадия	Лист	Листов
	Р	10	
Узел Сн	ООО "Строй Хауз"		


Формат А3

Общая схема устройства флюгарки
М1:15

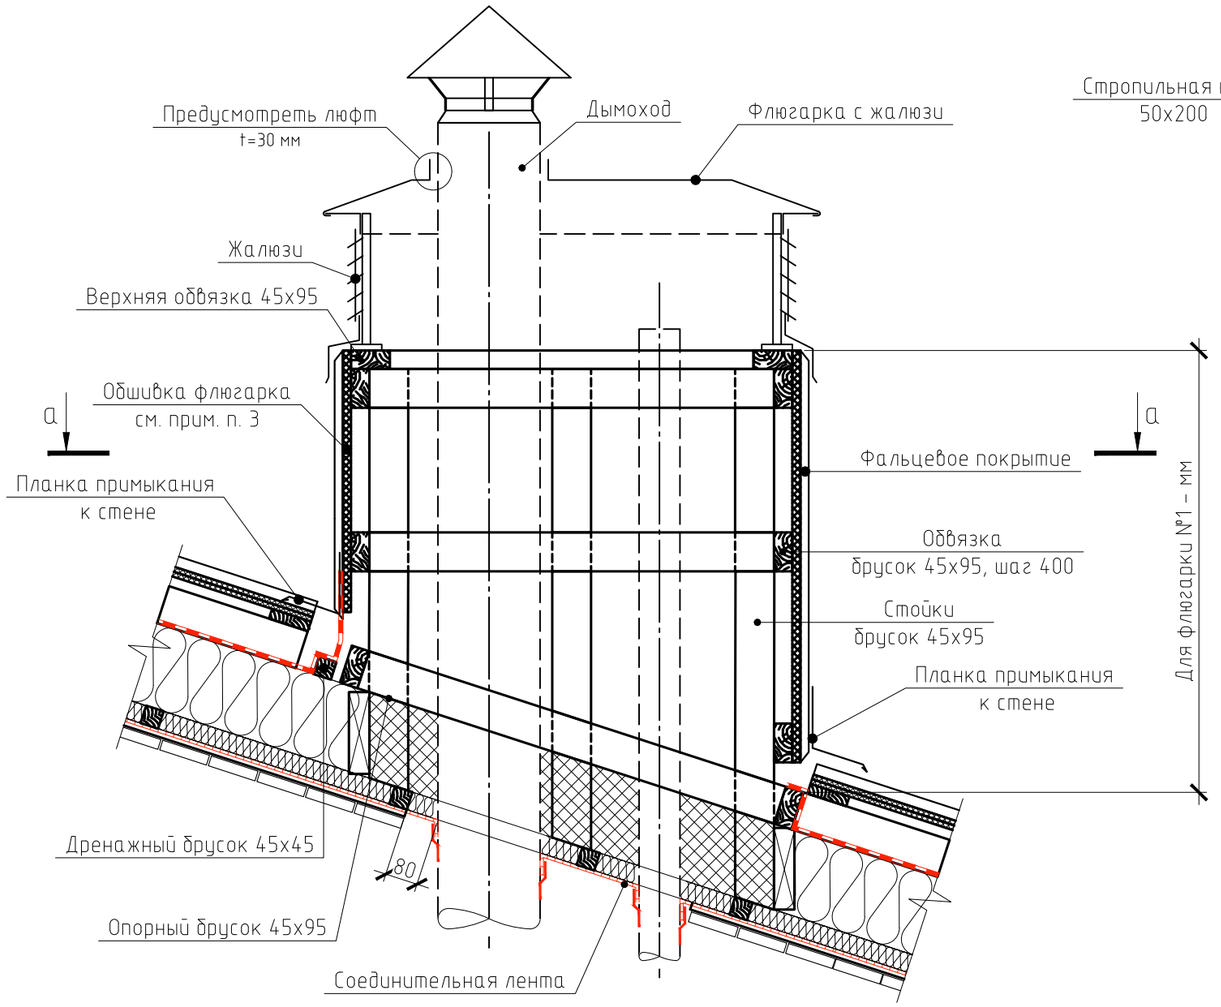

а–а

Развернуто на 90 град.

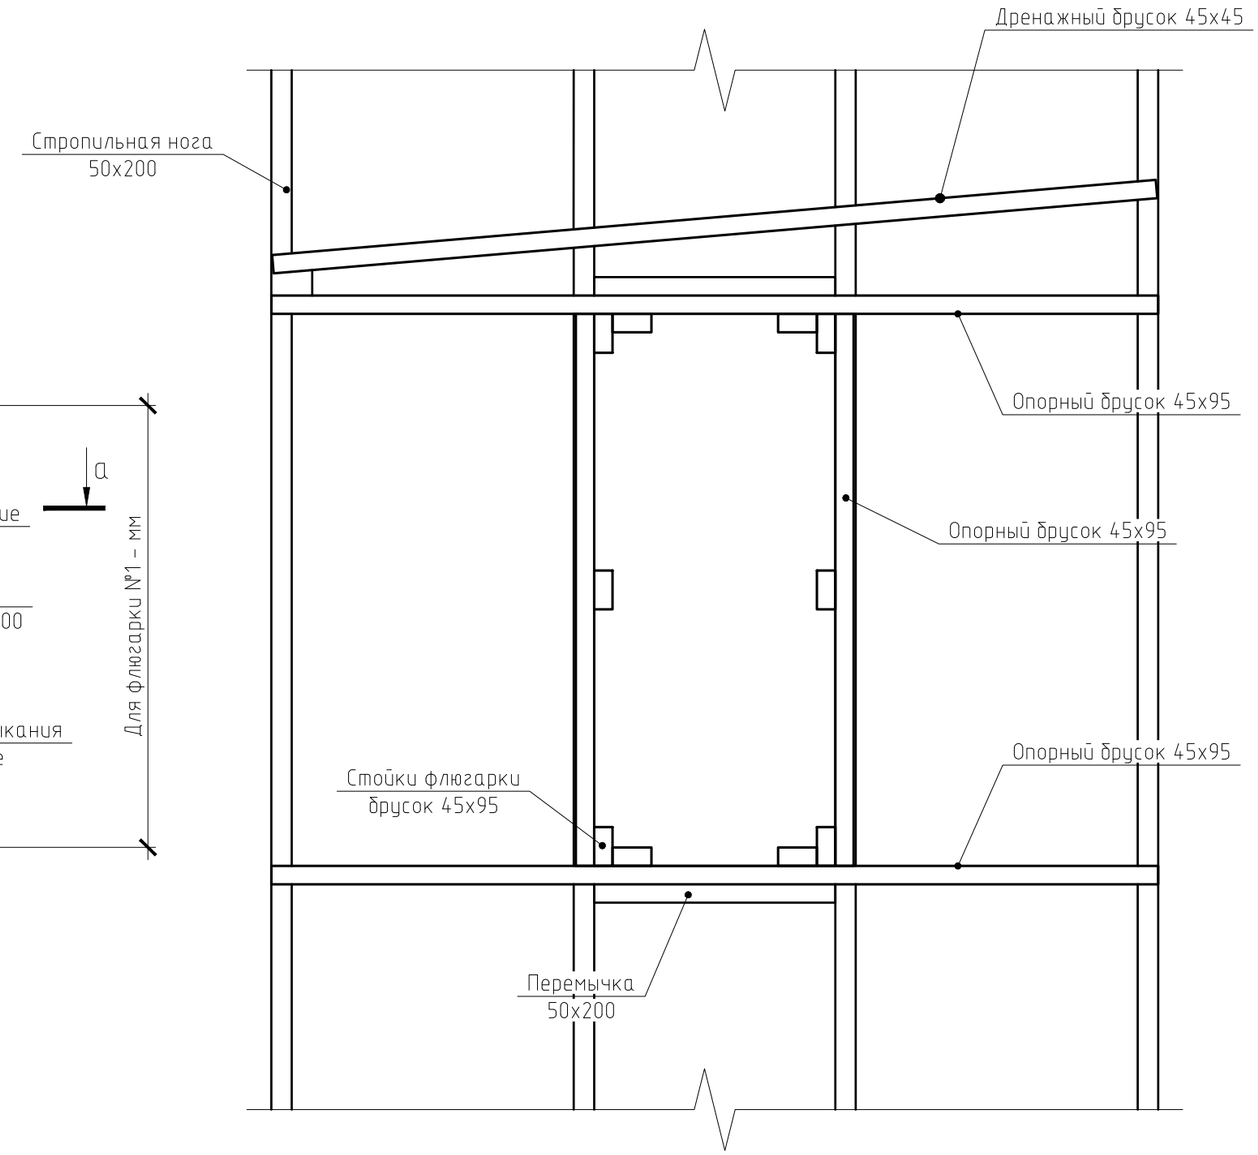

Примечание:

1. Габаритные размеры флюгарок см. план кровли совместно с планом стропильной системы;
2. Обвязку каркаса со стойками крепить между собой на ш/с потай 6х120 по 2шт. на стык;
3. Обшивку выполнять из фанеры ФСФ толщиной не менее 18 мм, в 1 слой. Зазор между листами 3–4 мм. Крепить саморезами желтый цинк 3,5х50 с шагом 250 мм. Возможно использование строганой доски 27х100, шаг установки 150. Крепить саморезами желтый цинк 4х70 по 2 шт. на точку крепления..


Изм.	Кол. уч.	Лист	№ док.	Подп.	Дата
Констр.		Москалюк А.Е.			30.09.26
Провер.		Баннов Е.А.			30.09.26
ГИП		Баннов Е.А.			30.09.26


291–КД5

Московская обл., Истринский р–н

Кровля	Стадия	Лист	Листов
	Р	11	
Устройство флюгарки	ООО "Строй Хауз"		

Формат А3

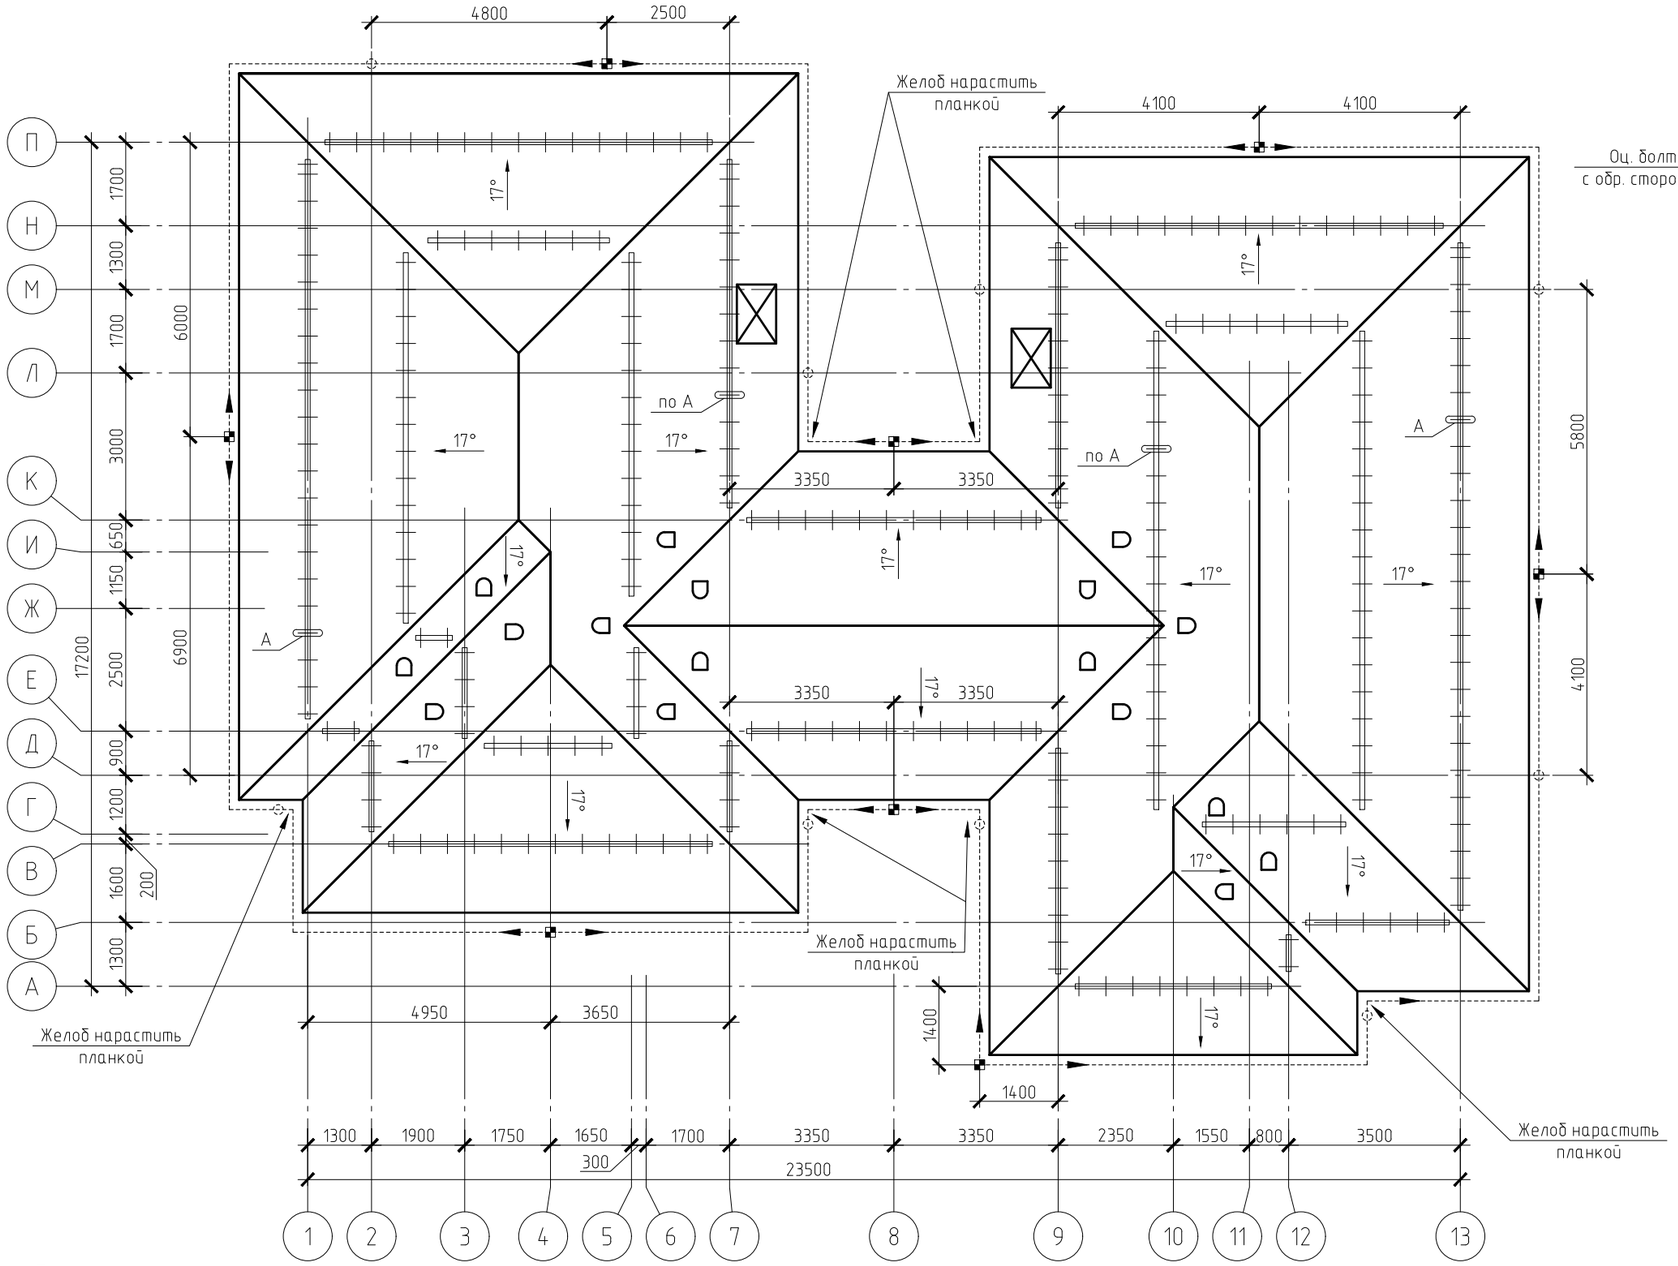

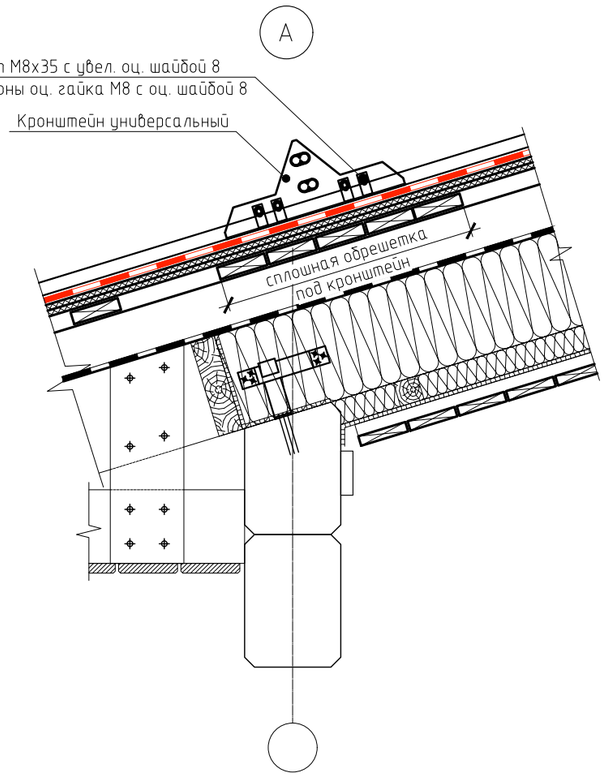

Условные обозначения:

- – дымоход, показан условно
- D – кровельный аэратор, узел монтажа см. Инструкцию по монтажу
- – водосточный желоб с уклоном к трубе 3мм на 1м (диаметр желоба ⌀150)
- – верхняя точка водосточного желоба на данном участке
- – водосточная труба, расположение согласовать с заказчиком (диаметр трубы ⌀100)
- – перепуск водосточной трубы на нижележащую кровлю
- – зона устройства снегозадержания, кронштейны крепить с шагом не больше 550, предусмотреть сплошную обрешетку под кронштейны снегозадержания

Примечание:
1. Расположение проходных элементов уточнять по проекту инженерных коммуникаций.

Изм.	Кол. уч.	Лист	№ док.	Подп.	Дата
Констр.		Москалюк А.Е.			30.09.26
Провер.		Баннов Е.А.			30.09.26
ГИП		Баннов Е.А.			30.09.26

291-КД5

Московская обл., Истринский р-н

Кровля


Стадия	Лист	Листов
Р	12	

План водосточной системы и системы снегозадержания


ООО "Строй Хауз"

Формат А3


Фасады 1 - 13

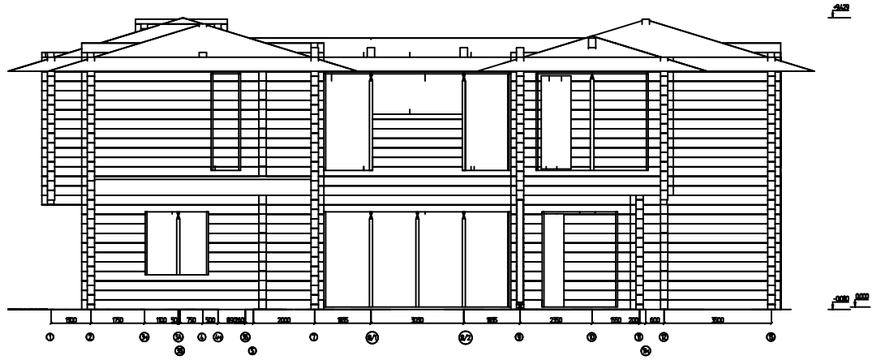


Фасады 13 - 1

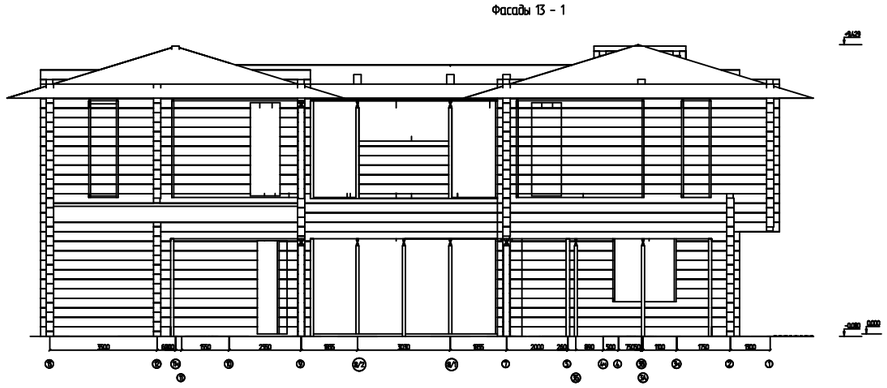

Фасады А - П

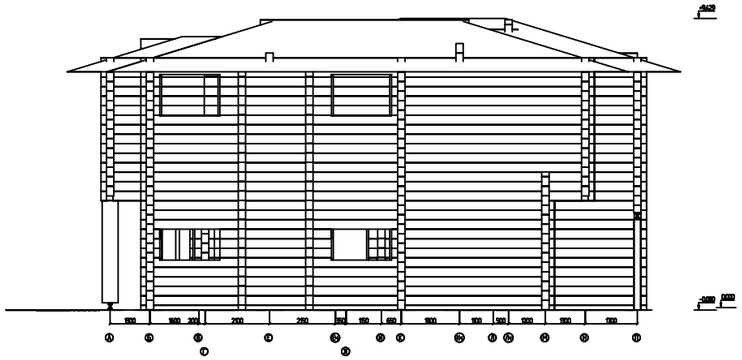



Фасады П - А

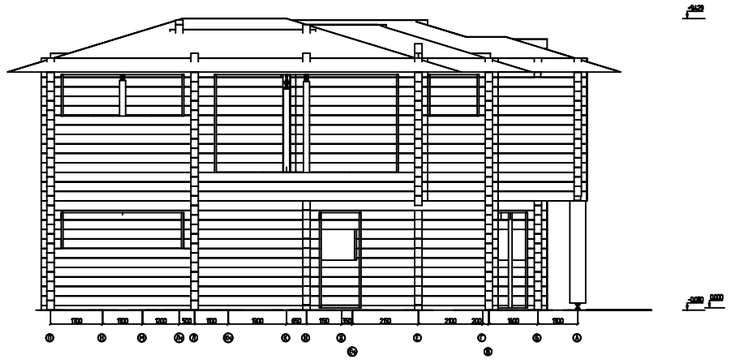

						291-КД5		
						Московская обл., Истринский р-н		
Изм.	Кол. уч.	Лист	№ док.	Подп.	Дата			
Констр.		Москалюк А.Е.			30.09.26	Кровля	Стадия	Лист	Листов
Провер.		Баннов Е.А.			30.09.26		Р	13	
ГИП		Баннов Е.А.			30.09.26	Общие фасады	ООО "Строй Хауз"		

Формат А3

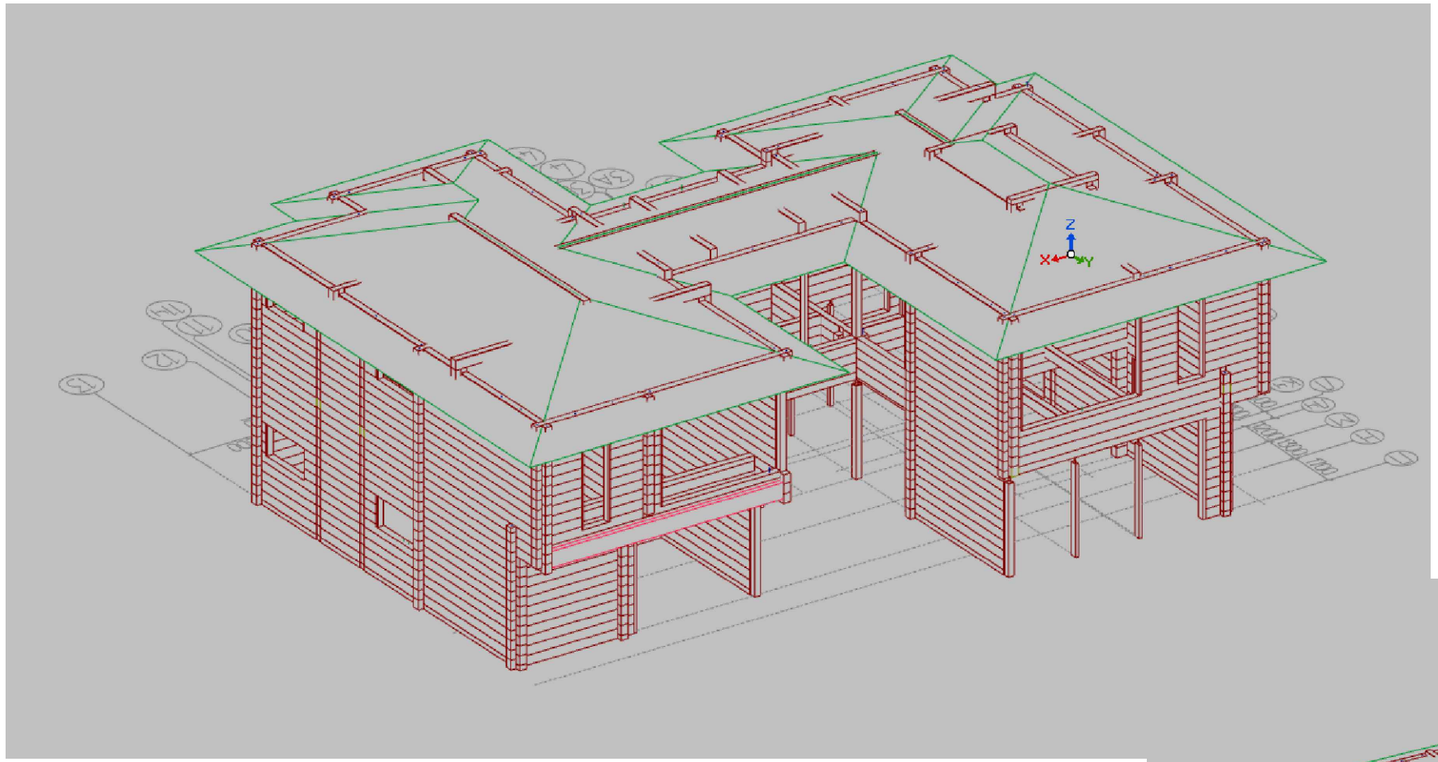

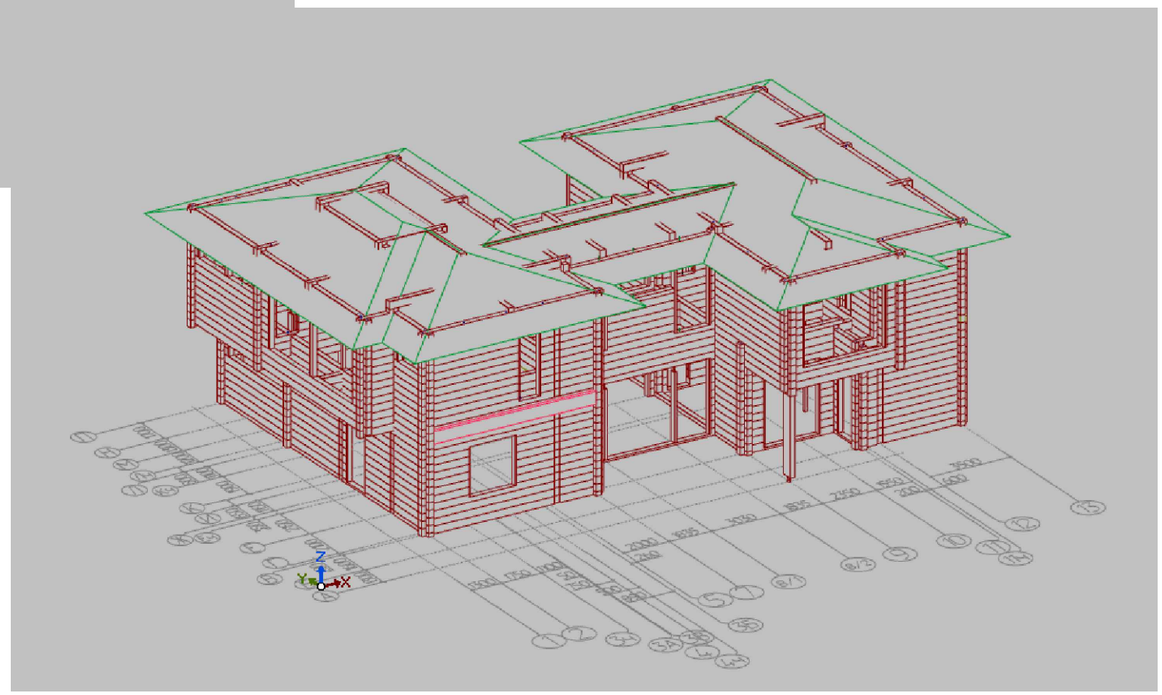

						291-КД5	
						Московская обл., Истринский р-н	
Изм.	Кол. уч.	Лист	№ док.	Подп.	Дата		
Констр.		Москалюк А.Е.			30.09.26	Кровля	Стадия: Р; Лист: 14; Листов:
Провер.		Баннов Е.А.			30.09.26		
ГИП		Баннов Е.А.			30.09.26	Общие виды	ООО "Строй Хауз"

Формат А3

Спецификация материалов КД5.Кровля

Поз.	Обозначение	Наименование	Кол.	Ед.изм.	Приме-чание
		Антисептик Зотекс	600	л	
1		Доска 50х200	12.42	м3	
2		Доска строганая 25х100	6.86	м3	
3		Доска 45х95 строганая	3.33	м3	
4		Доска 45х145 строганая	2.15	м3	
5		Доска 18х95 строганая	1.32	м3	
6		Брусок строганый 45х45	1.49	м3	
7		Брусок строганый 40х40	0.18	м3	
8		Фанера OSB-3 1220х2440х12	321	лист	
9		Уплотнительная лента FarAks Counter	30	рул	
10		Кронштейн Ра3 (опора скользящая)	156	шт	
11		Уголок КР-4	20	шт	
12		Уголок КМ-4	220	шт	
13		Аватерм	64	м2	
14		Гвоздь ершеный 4,2х50	10	кг	
15		Гвоздь ершеный 4,2х90	15	кг	
16		Гвоздь строительный 6х200	135	кг	
17		Гвоздь строительный 4х120	40	кг	
18		Гвоздь строительный 3х70	38	кг	
19		Саморез 3,5х41 жёлтый цинк	16000	шт	
20		Саморез 3,5х20 жёлтый цинк	16000	шт	
21		Саморез 6х120	340	шт	
22		Саморез 5х100	810	шт	
23		Саморез 3х50	4420	шт	
24		Утеплитель Изорок Изолайт, плотность 50	71.07	м3	

Изм.	Кол. уч.	Лист	№ док.	Подп.	Дата	291-КД5		
						Московская обл., Истринский р-н		
Констр.		Москалюк А.Е.			30.09.26	Кровля	Стадия	Лист	Листов
Провер.		Баннов Е.А.			30.09.26		Р	15	
ГИП		Баннов Е.А.			30.09.26	Спецификация (Начало)	ООО "Строй Хауз"		

Формат А4

Спецификация материалов КД5.Кровля

25		Мембрана супердиффузионная JV (1,5х50 м)	750	м2	
26		Лента соединительная односторонняя Delta multi-band m60	21	шт	
27		Пароизоляционная плёнка Ютафол	375	м2	
28		Лента соеденительная Finka Flexy Inside Tape	19	шт	
29		Ковер подкладочный ТЕХНОНИКОЛЬ Anderep Prof	560	м2	
30		Клик фальц Pro Grand Line 0,5 Satin Matt с пленкой на замках RAL 7024 мокрый асфальт	540	м2	
31		Саморез 4,8х28 с прокладкой ЭПДМ	2505	шт	
32		Кровельный герметик Grand Line professional	13	шт	
33		Саморез ПШ 4,2х25	3331	шт	
34		Аэро элемент кровли	17	шт	
35		Вентиляционная лента Hausprofi ПВХ-пластик 0,1х5м	24	шт	
36		Крепление коньковой/хребтовой обрешетки	278	шт	
37		Шумоизолирующая лента под фальц	1032	м\пог	
38		Вент. прогон опорный фальц	208	м\пог	
39		GL планка карнизная	60	шт	
40		GL планка конька плоского	56	шт	
41		Планка ендовы нижняя 2м, М07	19	шт	
42		Планка крепежная фальц 2м	38	шт	
43		Заклепка 4,8х10	400	шт	
44		Аэроэлемент конька/хребта /TOP ROLL/, Алюминий 0.31 х 5м	23	шт	
45		Комплект трубчатого снегозадержания (L-3000мм)	49	шт	
46		Дополнительный кронштейн снегозадержания	76	шт	
47		Лобовая доска	0.58	м3	
48		Карнизная доска	3.62	м3	
49		Финишный гвоздь 18GA50	2	уп	
50		Remmers Avenarius HOLZSCHUTZ-GRUND AQUA (20л) пропитка грунтовочная	65	л	

Изм.	Кол. уч.	Лист	№ док.	Подп.	Дата
Констр.		Москалюк А.Е.			30.09.26
Провер.		Баннов Е.А.			30.09.26
ГИП		Баннов Е.А.			30.09.26

291-КД5

Московская обл., Истринский р-н

Кровля

Стадия	Лист	Листов
Р	16	

Спецификация (Продолжение)

ООО "Строй Хауз"

Формат А4

Спецификация материалов КД5.Кровля

51		Remmers Avenarius WETTERSCHUTZ-LASUR UV FARBLOS	120	л	

Изм.	Кол. уч.	Лист	№ док.	Подп.	Дата	291-КД5			
						Московская обл., Истринский р-н			
Констр.		Москалюк А.Е.			30.09.26	Кровля	Стадия	Лист	Листов
Провер.		Баннов Е.А.			30.09.26		Р	17	
ГИП		Баннов Е.А.			30.09.26	Спецификация (Окончание)	ООО "Строй Хауз"		

Формат А4