ООО "Строй Хауз"

Московская обл., Истринский р-н, д. Веледниково, ул. Живописная, д. 25

Берта Ромарио

по адресу: Московская область, Истринский район

Индивидуальный жилой дом

РАБОЧАЯ ДОКУМЕНТАЦИЯ

Раздел КЖО

(Фундамент)

291-КЖО

Конструктор Москалюк А.
Проверил Баннов Е.
ГИП Баннов Е.

г. Москва 2026г.

Согласовано

Взам. инв. №

Подп. и дата

Инв. № подл.

Формат А4

Ведомость рабочих чертежей основного комплекта

Лист	Наименование	Примечание
1	Ведомость чертежей	А3
2	Общие данные	А3
3	План координационных осей	А2
4	План закладных	А2
5	План свайного поля	А3
6	План плиты перекрытия и подвенечной ленты	А3
7	Схема верхнего и нижнего армирований плиты	А2
8	Устройство фундамента	А3
9	Устройство сваи с ж/б плитой	А3
10	Узлы Ф1 – Ф4	А3
11	Закладная под водоснабжение	А3
12	Закладная под канализацию	А3
13	Закладная под теплотрассу	А3
14	Закладная под электрокабели	А3
15	План армирования с указанием закладных	А2
16	Спецификация	А3

Ведомость основных комплектов рабочих чертежей

Обозначение	Наименование	Примечание
АР	"Архитектурно-планировочное решение"	
КЖ0	Фундамент	
КД1	Разбрусовка	
КД2	Клееный материал	
КД3	Подвенечный оклад	
КД4	Межэтажные перекрытия	
КД5	Кровля	
КД6	Каркасные перегородки	

Согласовано

Взам. инв. №

Подп. и дата

Инв. № подл.

Изм.	Кол. уч.	Лист	№ док.	Подп.	Дата	291-КЖ0			
						Московская область, Истринский район			
Констр.		Москалюк А.			29.09.26	Фундамент	Стадия	Лист	Листов
Проверил		Баннов Е.			29.09.26		Р	1	16
ГИП		Баннов Е.			29.09.26	Ведомость чертежей	ООО "Строй Хауз"		
Изм.									

Формат А3

Общие данные.


1. Настоящий проект разработан на основании комплекта чертежей марки АР;
2. За относительную отм. ±0.000 принята отм. чистого пола;
3. Строительная площадка расположена в I ветровом и III снеговом районах с нормативной глубиной сезонного промерзания:
 – глина или суглинок 1,03м;
 – супесь, пески пылеватые или мелкие – 1,25м;
 – песок средней крупности, крупный или гравелистый – 1,34м;
4. Посадку сооружения смотри чертежи генплана;
5. При производстве работ все поверхностные воды должны быть отведены с участка строительства. Почвенно-растительный слой должен быть снят по всей площади;
6. Коэффициент уплотнения песчаной подушки К=0,95. Для засыпки котлована использовать песок не менее средней крупности. Модуль крупности Мк по ГОСТ 8736-2014 не менее 2;
7. Для теплоизоляции горизонтальных конструкций фундамента использовать экструдированный пенополистирол с прочностью на сжатие не менее 0.2 МПа, для вертикальных конструкций – с прочностью на сжатие не менее 0.1 МПа;
8. При возведении опалубки необходимо очистить контактные поверхности с бетоном от строительного мусора и от снега и льда в зимнее время. Собранная опалубка не должна изменять форму в рабочем положении, а также воспринимать технологические нагрузки и давление бетонной смеси без изменения основных геометрических размеров;
9. Армирование железобетонных конструкций предусмотрено отдельными стержнями классов А500С, А240 объединенными вязальной проволокой. Вязку арматуры производить отожженной проволокой Ø1,2мм. Стыковку арматуры организовывать вразбежку. Соединять стержни дуговой сваркой разрешается только в случаях оговоренных проектом;
10. При армировании необходимо использовать чистые стержни без коррозии. При укладке арматуры обеспечивать требуемую толщину защитного слоя бетона с помощью пластиковых фиксаторов или фиксаторов из цементно-песчаного раствора. Запрещается использовать в качестве фиксаторов обрезки арматуры и деревянные обрезки;
11. Все монолитные конструкции выполнять из тяжелого бетона класса не менее В22,5, W6, F150, П4;
12. Перед бетонированием элементов железобетонных конструкций горизонтальные и наклонные бетонные поверхности рабочих швов должны быть очищены от мусора, грязи, снега, льда и цементной пленки. Бетонные смеси следует укладывать в опалубку горизонтальными слоями одинаковой толщины без разрывов, с последовательным направлением укладки в одну сторону во всех слоях. Укладка следующего слоя бетонной смеси допускается до начала схватывания предыдущего слоя. Поверхность рабочих швов, устраиваемых при укладке бетона с перерывами, должна быть перпендикулярна оси бетонируемых колонн и балок, поверхности плит и стен. При бетонировании запрещается разбавлять бетонную смесь водой;
13. При уплотнении бетонной смеси ручными глубинными вибраторами толщина укладываемых слоев должна быть не более 1,25 длины рабочей части вибратора;
14. Методику определения набора прочности бетона назначать согласно ГОСТ 18105-2018 "Бетоны. Правила контроля прочности";
15. В начальный период твердения бетон необходимо защищать от попадания атмосферных осадков и потерь влаги. В последующем поддерживать температурно-влажностный режим с созданием условий, обеспечивающих нарастание прочности бетона;
16. Отклонения в размерах конструкций не должны превышать предельных значений, приведенных в табл. 4.11 СП 70.13330.2012 "Несущие и ограждающие конструкции";
17. Земляные работы в зимний период производить в соответствии с техническим регламентом по зимней работе. Не допускается промораживание грунта под подошвой фундамента;
18. При выполнении работ в зимний период необходимы специальные мероприятия, обеспечивающие достижение бетоном проектной прочности;
19. Инженерные коммуникации прокладывать согласно специальному проекту;
20. Проектирование свайного фундамента выполнено на основании данных из отчета по результатам инженерно-геологических изысканий 2026-07.840-ИГИ-Т.

Ведомость ссылочных и прилагаемых документов

Обозначение	Наименование	Примечание
СП 22.13330.2016	"Основания зданий и сооружений"	
СП 24.13330.2021	"Свайные фундаменты"	
СП 20.13330.2016	"Нагрузки и воздействия"	
СП 45.13330.2017	"Земляные сооружения, основания и фундаменты"	
СП 63.13330.2018	"Бетонные и железобетонные конструкции"	
СП 70.13330.2012	"Несущие и ограждающие конструкции"	
ГОСТ 3282-74	"Проволока стальная низкоуглеродистая общего назначения"	
ГОСТ 18105-2018	"Бетоны. Правила контроля и оценки прочности"	
ГОСТ 19804-2021	"Сваи железобетонные заводского изготовления"	
ГОСТ 26633-2015	"Бетоны тяжелые и мелкозернистые"	
ГОСТ 34028-2016	"Прокат арматурный для железобетонных конструкций	
ГОСТ 8736-2014	"Песок для строительных работ"	
СТО 72746455-3.3.1-2012	"Плиты пенополистирольные экструзионные ТехноНИКОЛЬ XPS"	
Пособие по проектированию	"Армирование элементов монолитных железобетонных зданий"	
2026-07.840-ИГИ-Т	"Отчет по результатам инженерно-геологических изысканий"	


						291-КЖО			
						Московская область, Истринский район			
Изм.	Кол. уч.	Лист	№ док.	Подп.	Дата				
Констр.		Москалюк А.			29.09.26	Фундамент	Стадия	Лист	Листов
Проверил		Баннов Е.			29.09.26		Р	2	
ГИП		Баннов Е.			29.09.26	Общие данные	ООО "Строй Хауз"		
Изм.									

Формат А3

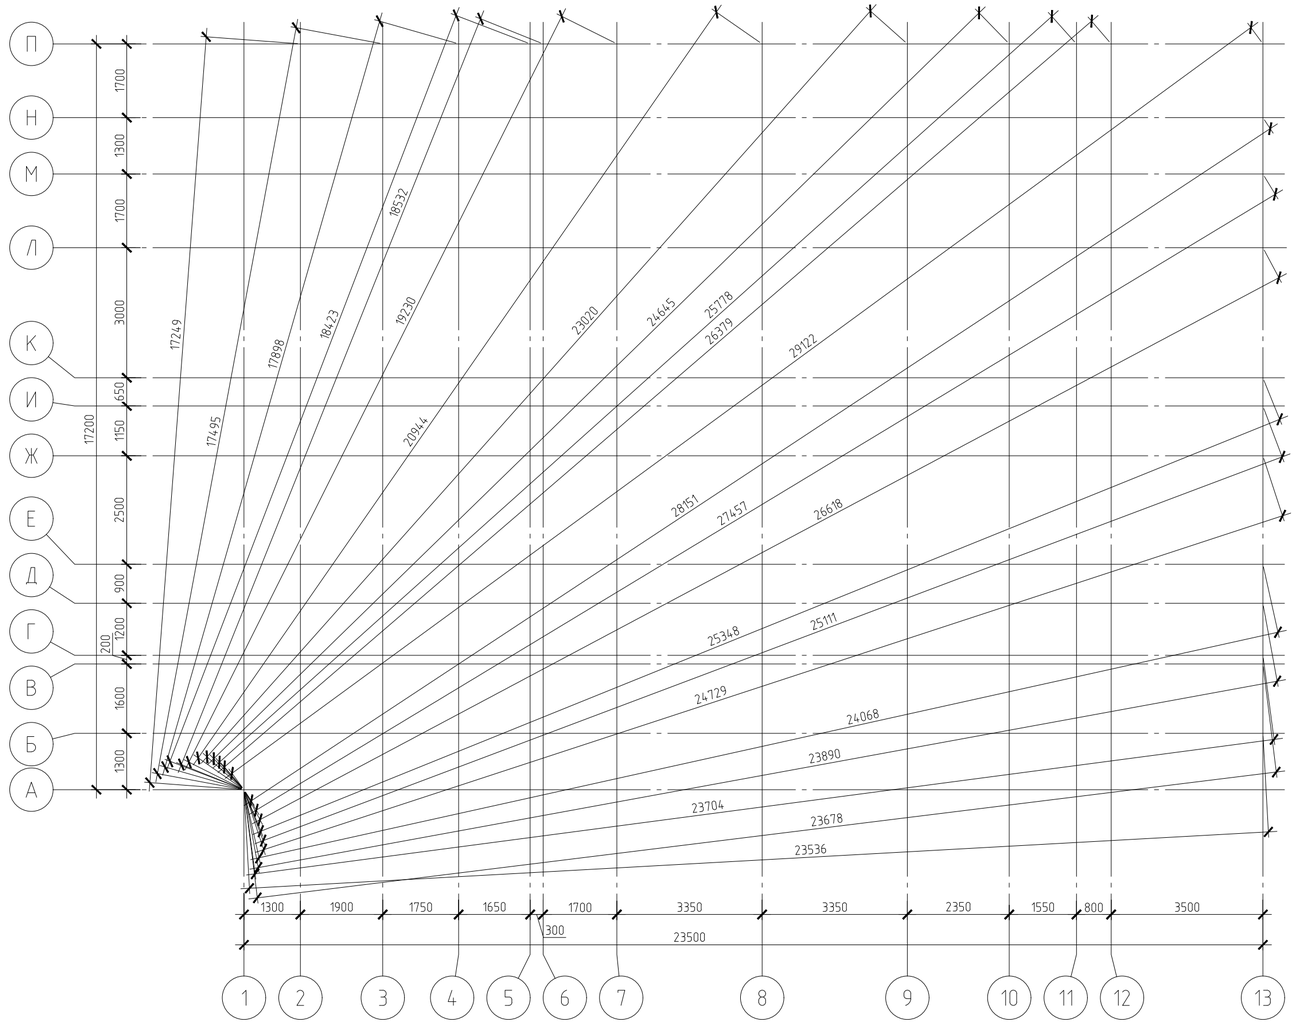

						291-КЖО	
						Московская область, Истринский район	
Изм.	Кол. уч.	Лист	№ док.	Подп.	Дата		
Констр.		Москалюк А.			29.09.26	Фундамент	Стадия: Р; Лист: 3; Листов:
Проверил		Банков Е.			29.09.26		
ГИП		Банков Е.			29.09.26	План координационных осей	ООО "Строй Хауз"
Изм.							


Формат А2

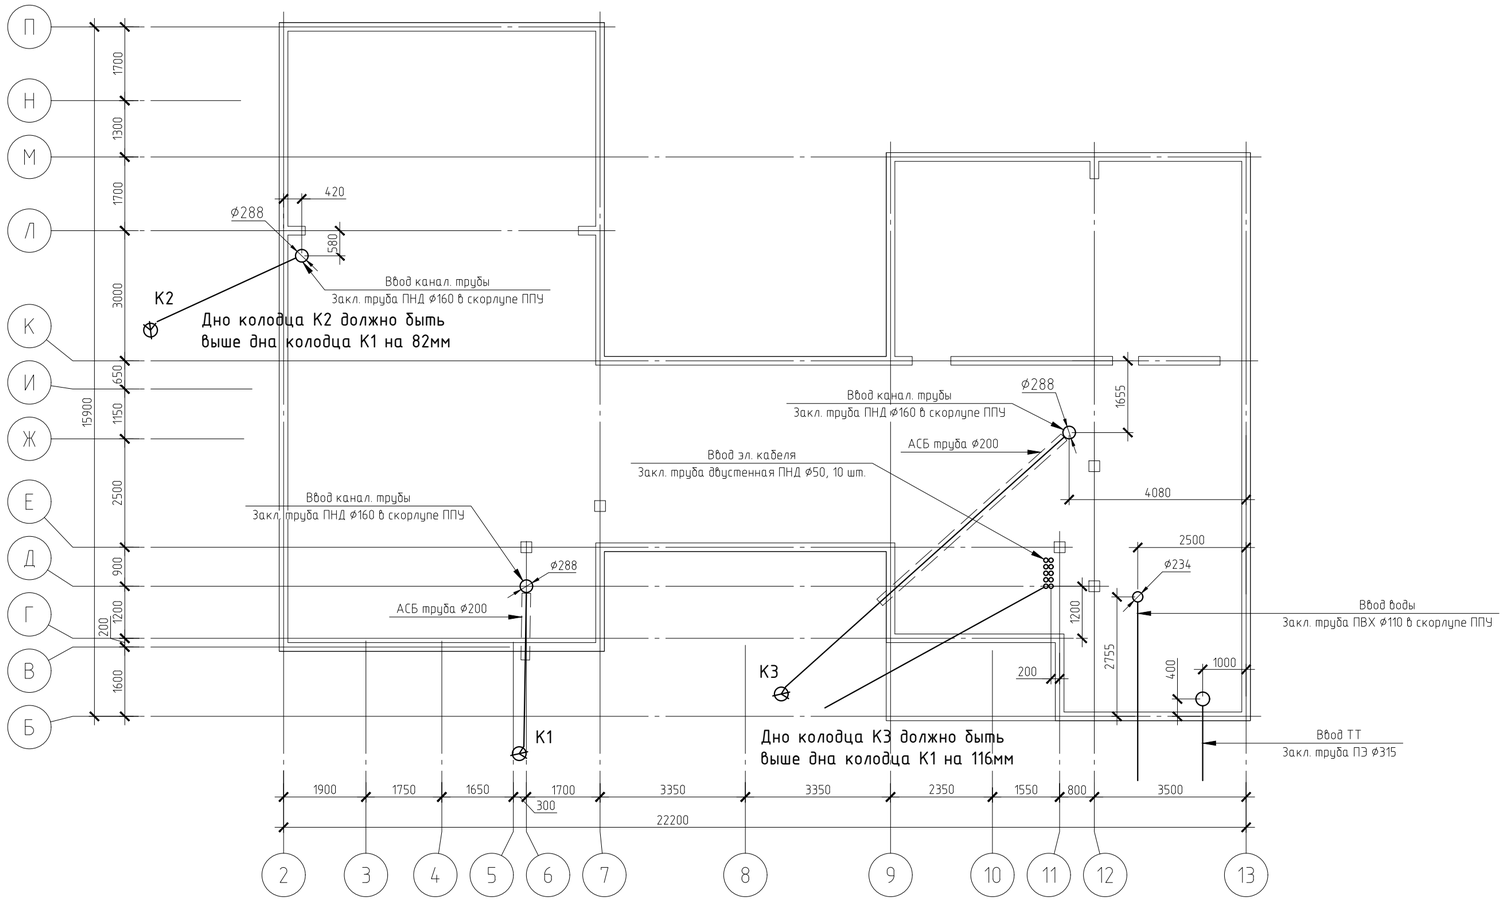

Примечание:
1. Узлы закладных под коммуникации см. на л. 11–14;
2. Под фундаментом канализационную трубу уложить в футляр из асбестоцементной трубы ø200 мм.

						291–КЖО	
						Московская область, Истринский район	
Изм.	Кол. уч.	Лист	№ док.	Подп.	Дата		
Констр.		Москалюк А.			29.09.26	Фундамент	Стадия: Р; Лист: 4; Листов:
Проверил		Банков Е.			29.09.26		
ГИП		Банков Е.			29.09.26	План закладных	ООО "Строй Хаус"
Изм.							

Формат А2

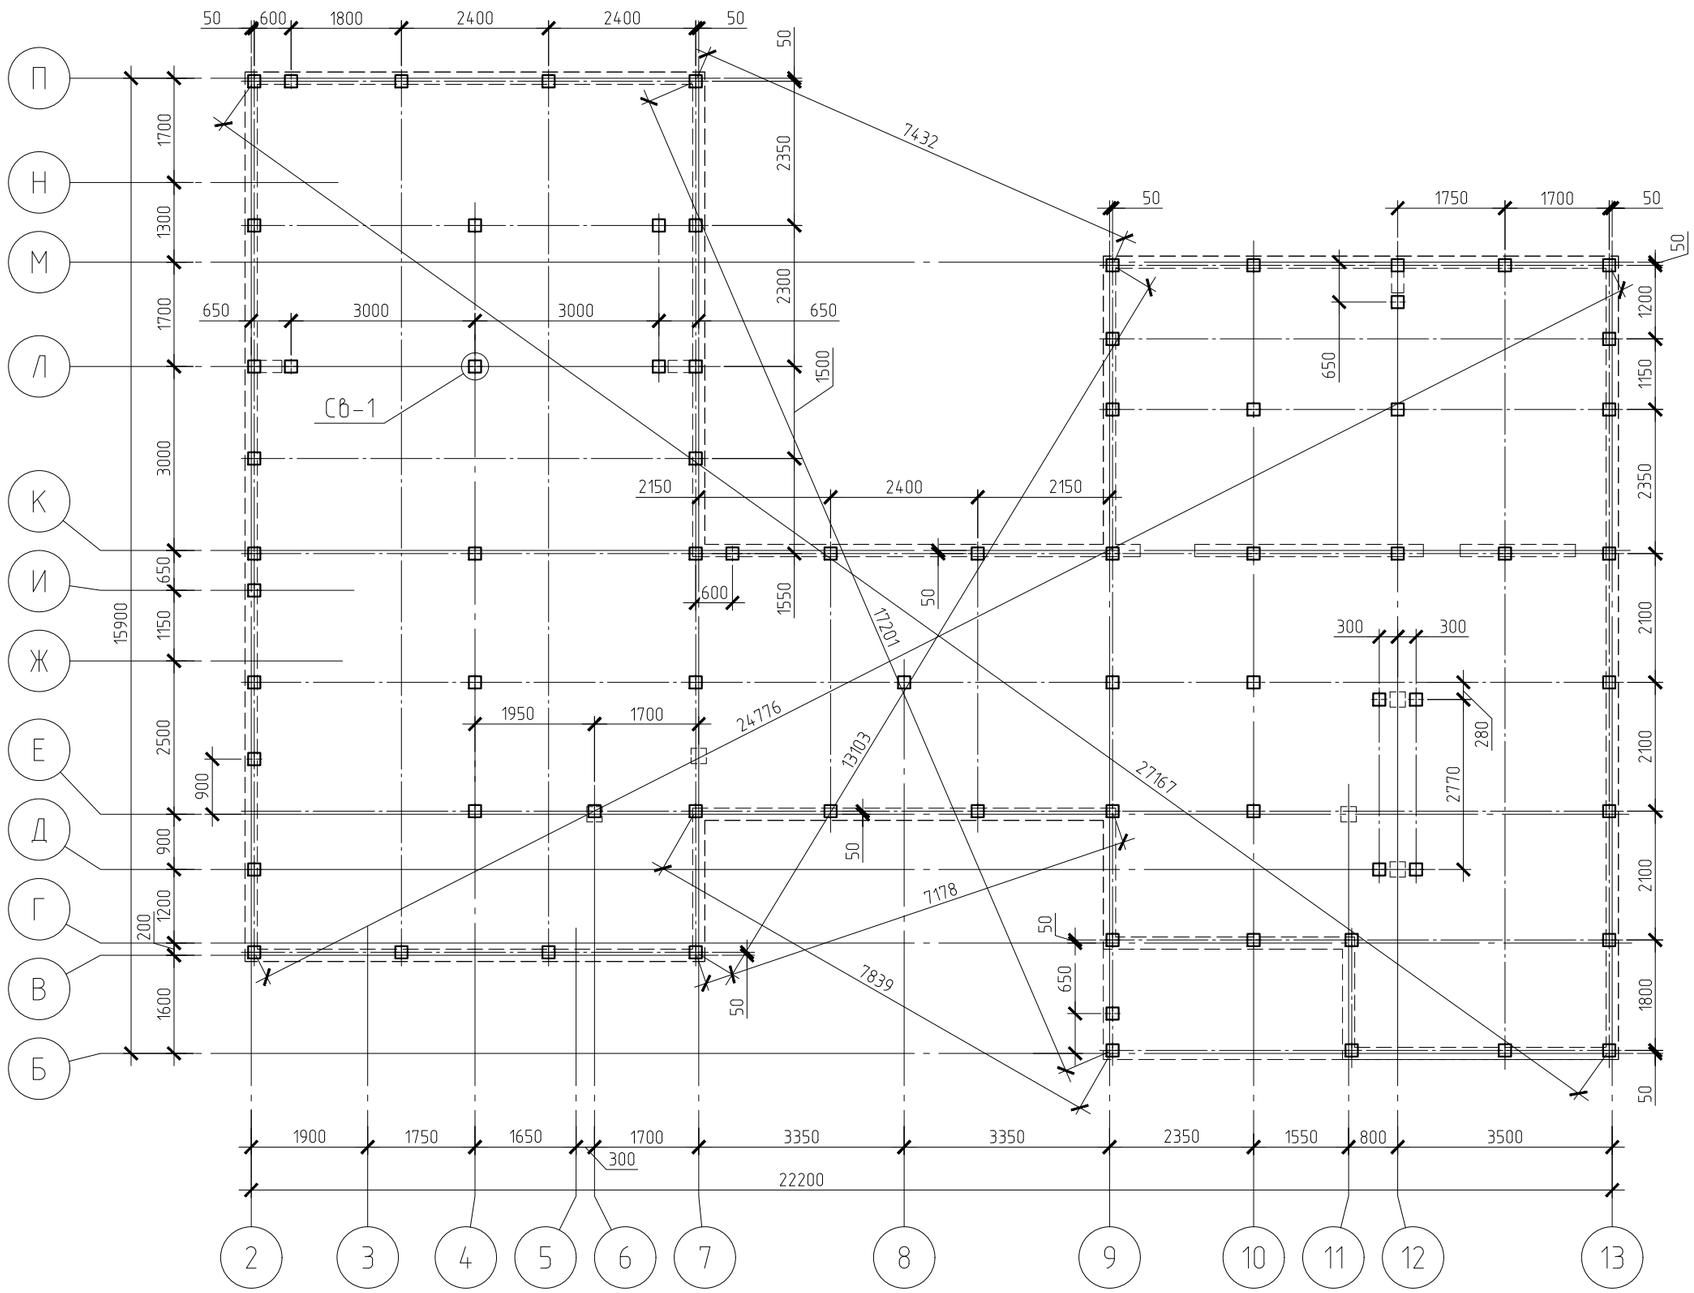

Условные обозначения:

⊞ – забивная железобетонная свая Св-1 (см.л.9)

– – – – контур железобетонной плиты с лентой

Ведомость свай


№ п/п	Обозначение сваи	Маркировка сваи	Отм. верха забитой сваи	Отм. верха распушеной сваи	Кол-во, шт.	Примечание
1	Св-1	С40.20-3	-0,140	-0,540	74	ГОСТ 19804-2021
	Всего				74	

Примечание:

1. Все размеры по сваям, включая диагональные, даны по центру свай.

Изм.	Кол. уч.	Лист	№ док.	Подп.	Дата	291-КЖО			
						Московская область, Истринский район			
Констр.		Москалюк А.			29.09.26	Фундамент	Стадия	Лист	Листов
Проверил		Баннов Е.			29.09.26		Р	5	
ГИП		Баннов Е.			29.09.26	План свайного поля	ООО "Строй Хауз"		
Изм.									

Формат А3

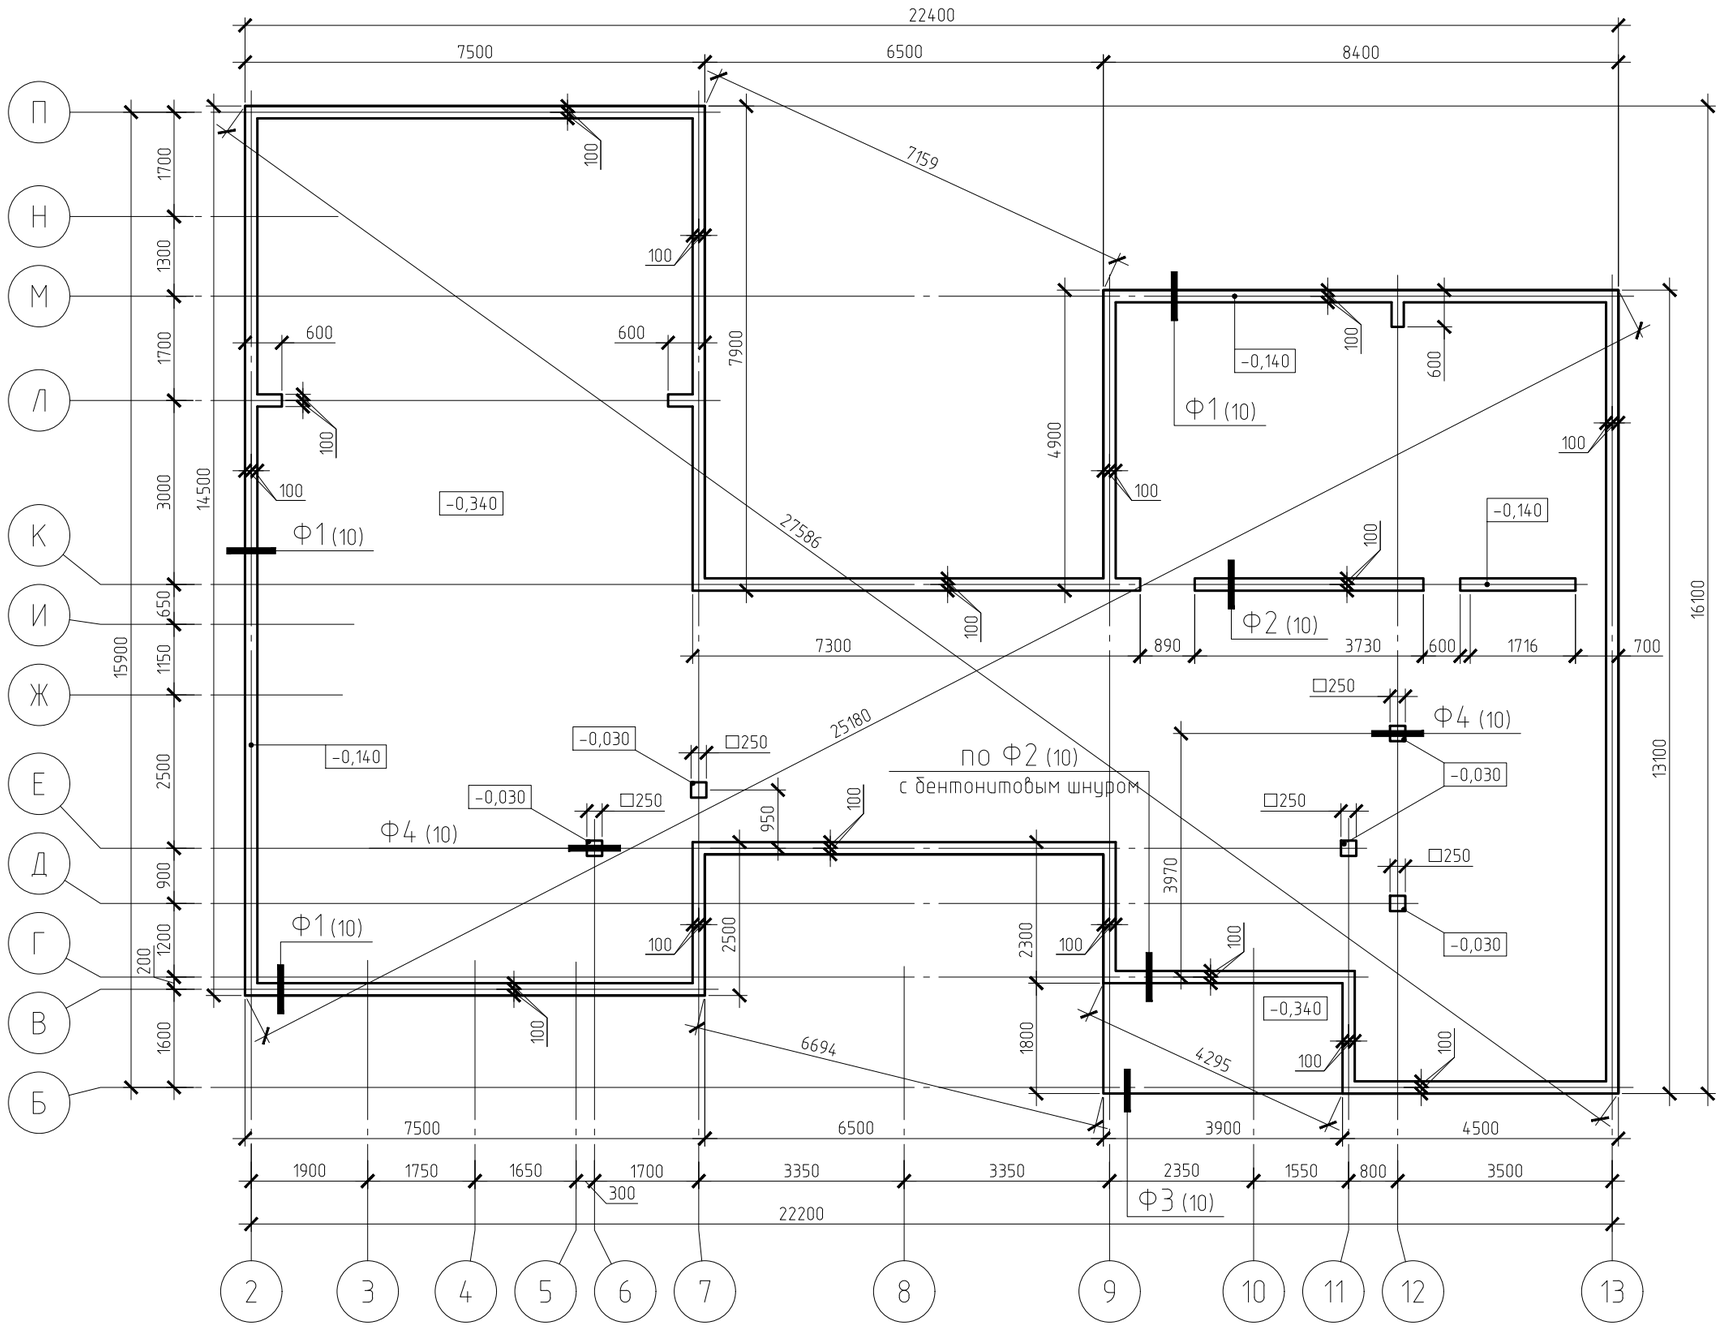

Примечание:

1. Узел устройства фундамента см. л. 8;
2. Габаритные и диагональные размеры даны по бетону.

						291-КЖО		
						Московская область, Истринский район		
Изм.	Кол. уч.	Лист	№ док.	Подп.	Дата			
Констр.		Москалюк А.			29.09.26	Фундамент	Стадия	Лист	Листов
Проверил		Баннов Е.			29.09.26		Р	6	
ГИП		Баннов Е.			29.09.26	План плиты перекрытия и подвенечной ленты	ООО "Строй Хауз"		
Изм.									

Формат А3



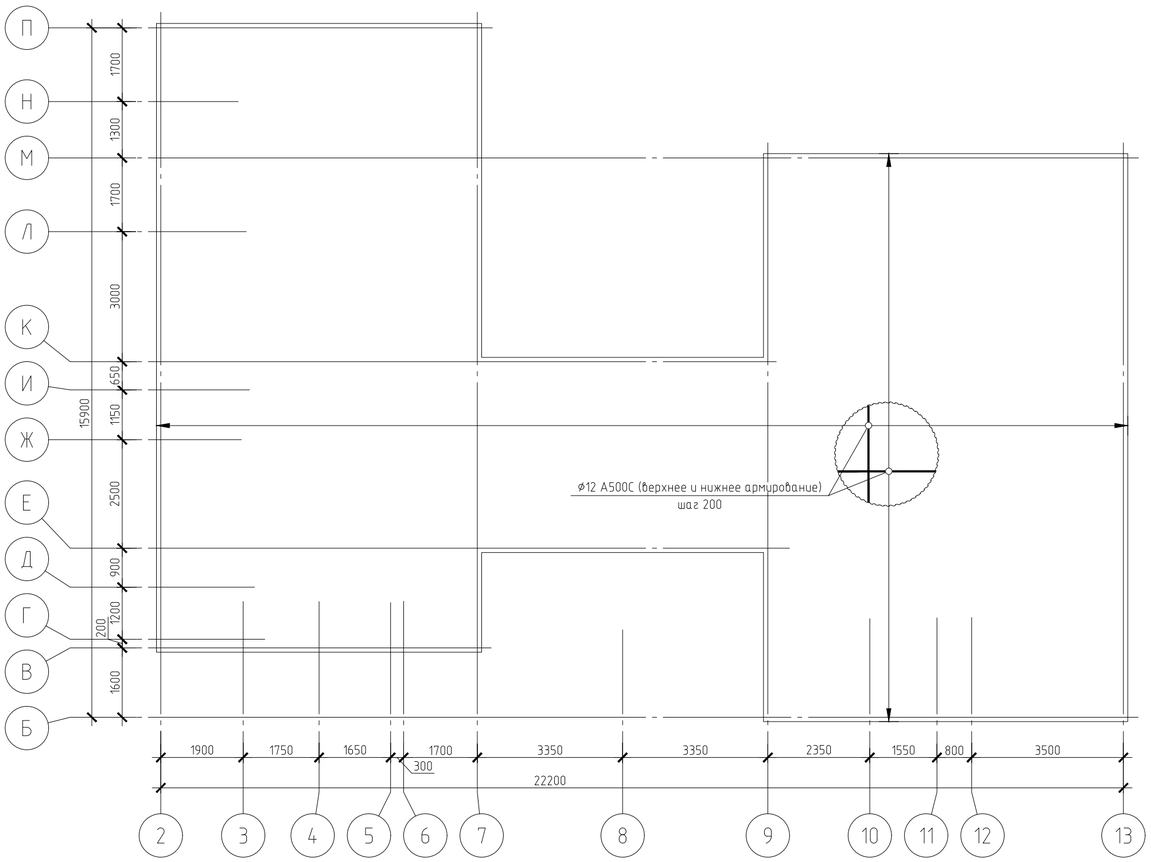



Схема усиления в местах
установки закладных элементов

Внешний диаметр ≤ 160 мм
(схема усиления в случае разрыва сетки)

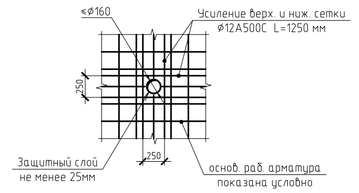


Внешний диаметр > 160 мм
(схема усиления в случае разрыва сетки)

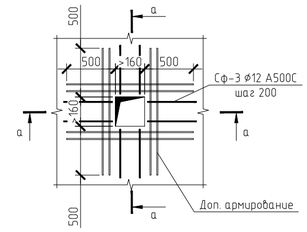

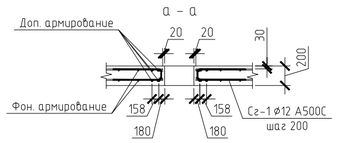

Армирование углов подвенечной ленты

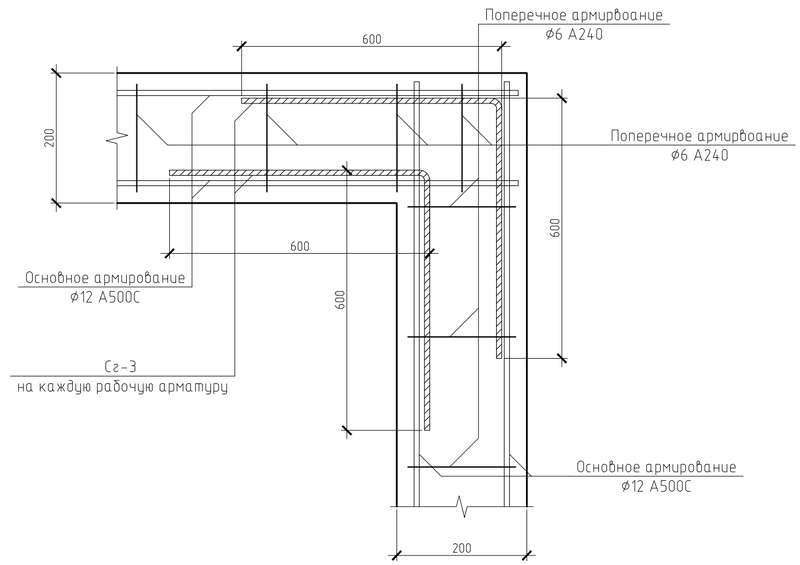

Фрагмент установки
поддерживающих каркасов

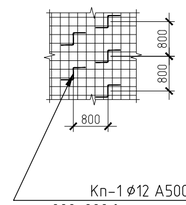


Схема вязки арматурных
каркасов



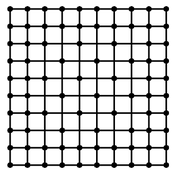


Схема стыковки продольной арматуры

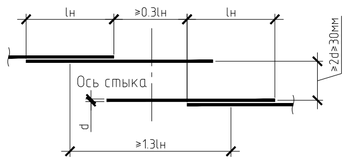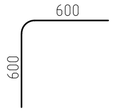

Диаметр арматуры d, мм	Длина нахлёстки lн, мм
12	≥800


Примечание:
1. Крестообразные и нахлесточные соединения стержней арматуры плиты выполнить на скрутках из отожженной вязальной проволоки диаметром 1.2–1.5мм
2. При армировании нижней и верхней зоны фундаментной плиты стержнями ø12 А500С, стыковку по длине необходимо выполнить в разбежку в соответствии с приведенной схемой стыковки арматурных стержней. При этом количество стыкуемой в одном расчетном сечении рабочей арматуры должно быть не более 50%. Допускается стыковать стержни в одном сечении, при этом lн увеличить в два раза.

Ведомость деталей	
Поз.	Эскиз
Сг-3 ø12А500С L=1200	


						291-КЖО	
						Московская область, Истринский район	
Изм.	Кол.уч.	Лист	№ док.	Подп.	Дата		
Констр.		Москалюк А.			29.09.26	Фундамент	Стадия: Р; Лист: 7; Листов:
Проверил		Банков Е.			29.09.26		
ГИП		Банков Е.			29.09.26	Схема верхнего и нижнего армирований плиты	ООО "Строй Хауз"
Изм.							

Формат А2

Устройство фундамента основной части дома

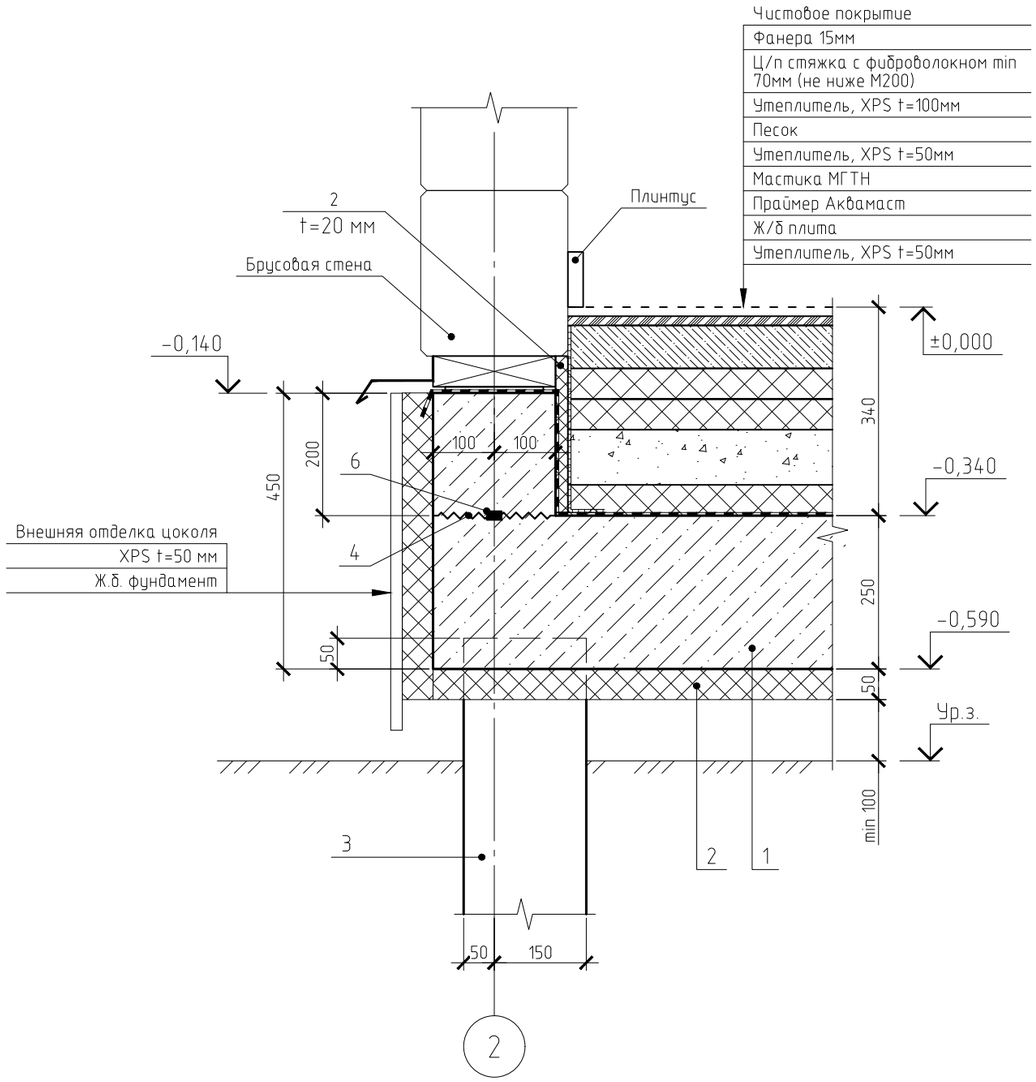

Устройство фундамента крыльца

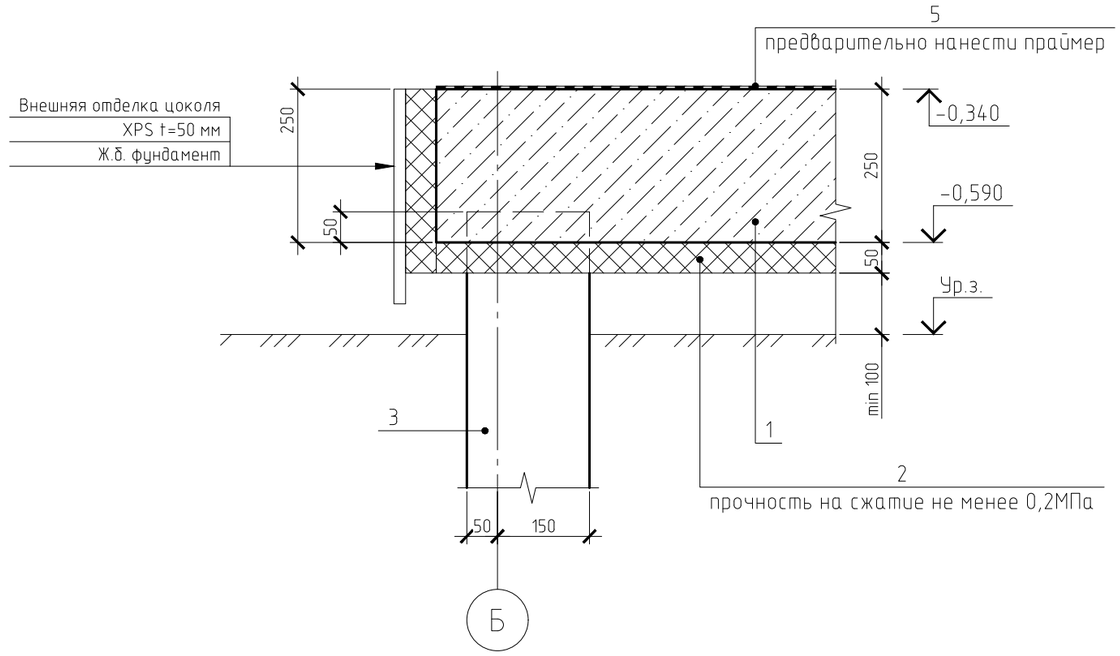


Примечания:
1. В пятне застройки предварительно снять плодородный слой min 15см, уложить геотекстиль и засыпать песком или гравием 15-20см;
2. XPS по периметру плиты, а также под плитой крепить грибками ТехноНИКОЛЬ 5шт. на лист.

Обозн-е	Наименование	Обозн-е	Наименование
1	Фундамент	4	Рабочий шов
2	Экструдированный пенополистирол XPS	5	Мастика МГТН
3	Забивная свая 200х200	6	Бентонитовый шнур

						291-КЖО		
						Московская область, Истринский район		
Изм.	Кол.уч.	Лист	№ док.	Подп.	Дата			
Констр.		Москалюк А.			29.09.26	Фундамент	Стадия: Р	Лист: 8
Проверил		Баннов Е.			29.09.26			Листов:
ГИП		Баннов Е.			29.09.26	Устройство фундамента	ООО "Строй Хауз"	
Изм.								


Формат А3


Устройство сваи с ж/б плитой

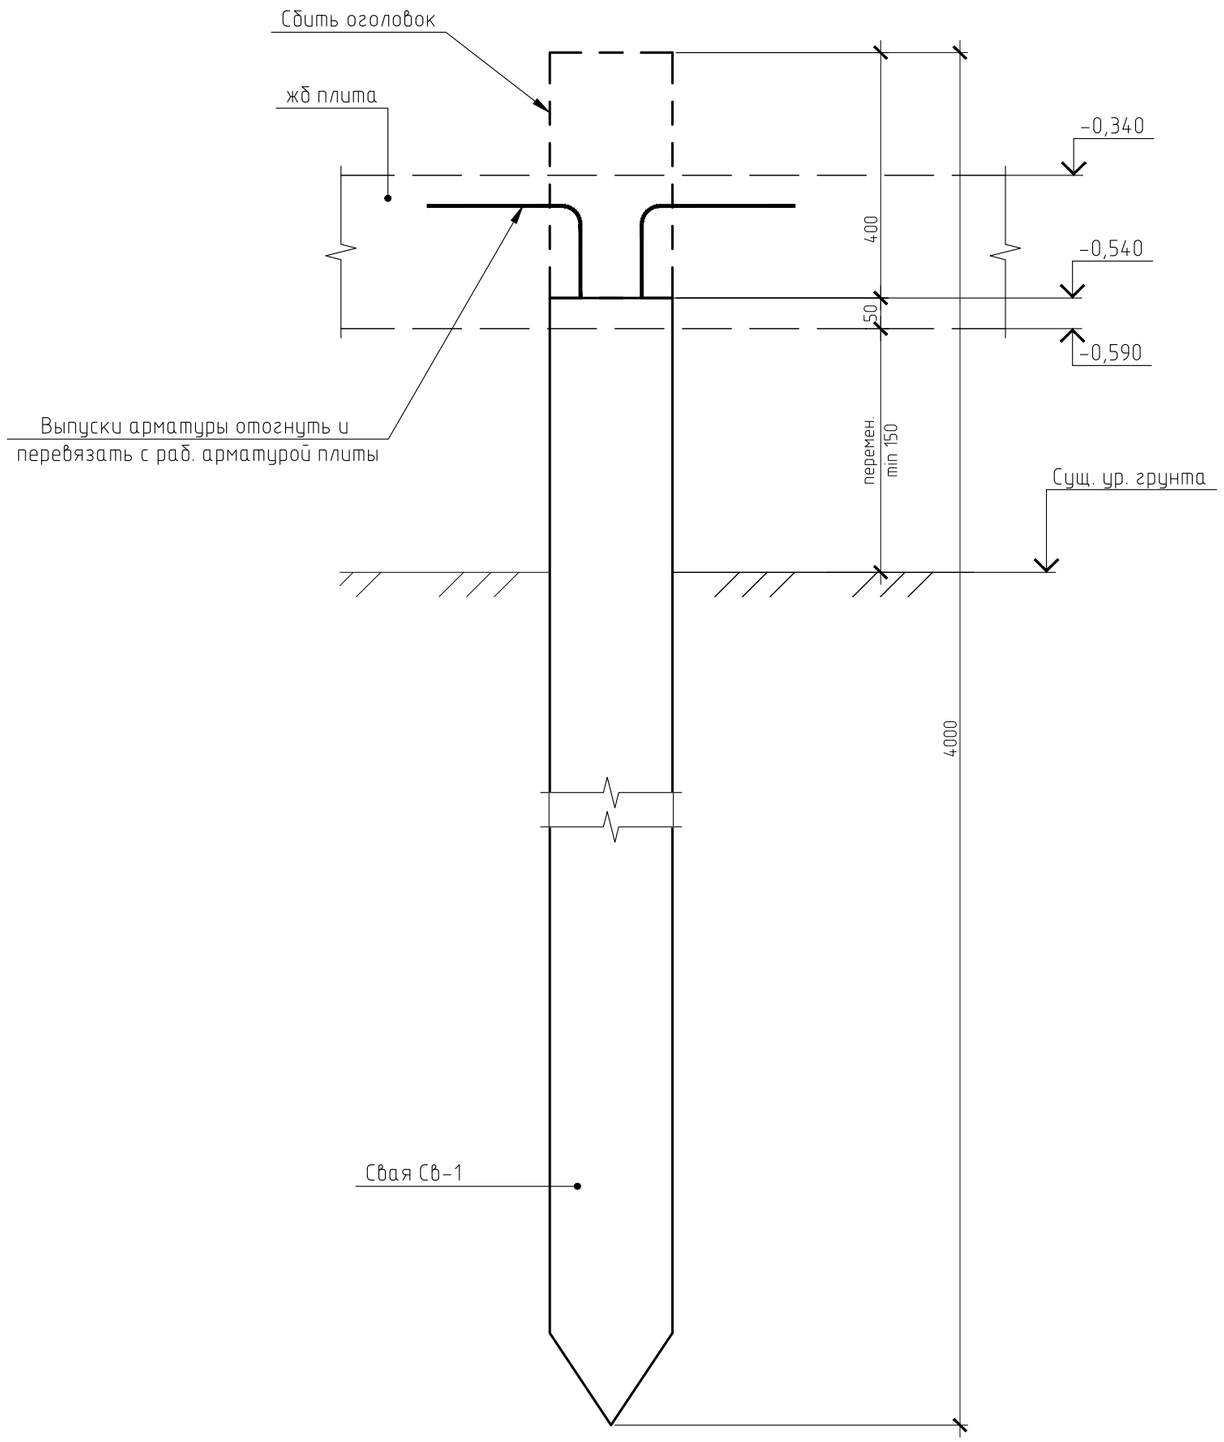



						291-КЖО		
						Московская область, Истринский район		
Изм.	Кол. уч.	Лист	№ док.	Подп.	Дата			
Констр.		Москалюк А.			29.09.26	Фундамент	Стадия	Лист	Листов
Проверил		Баннов Е.			29.09.26		Р	9	
ГИП		Баннов Е.			29.09.26	Устройство сваи с ж/б плитой	ООО "Строй Хауз"		
Изм.									

Формат А3

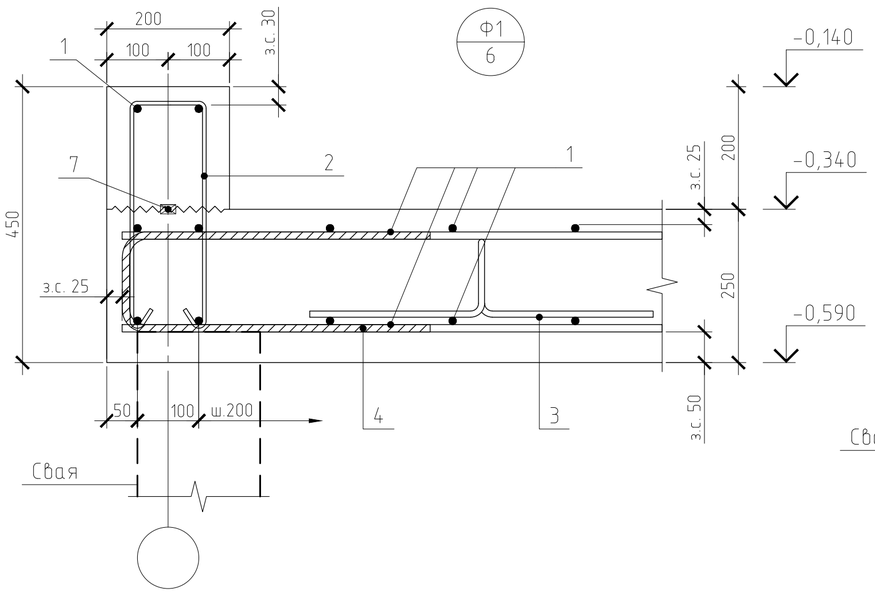


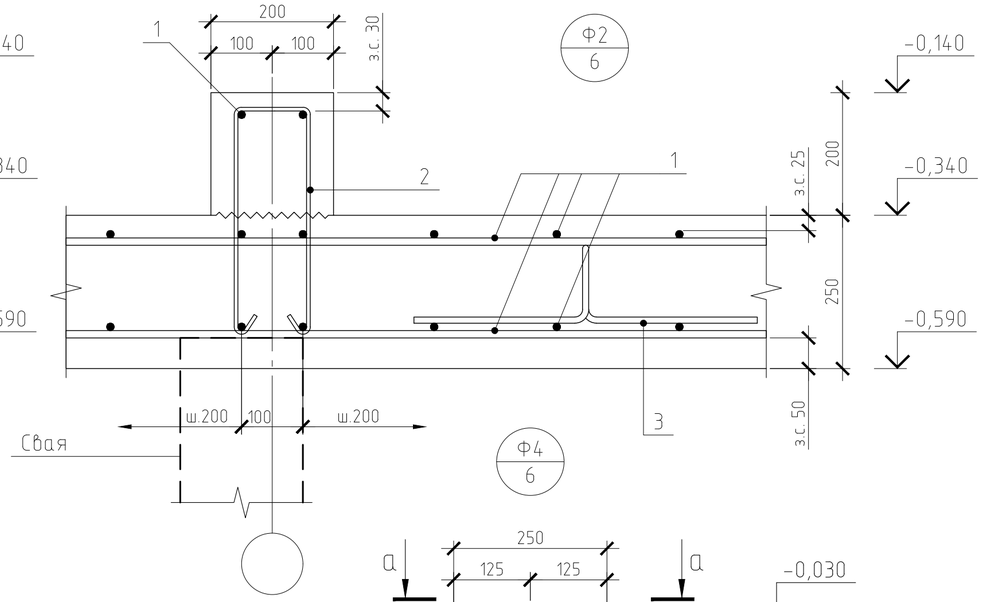

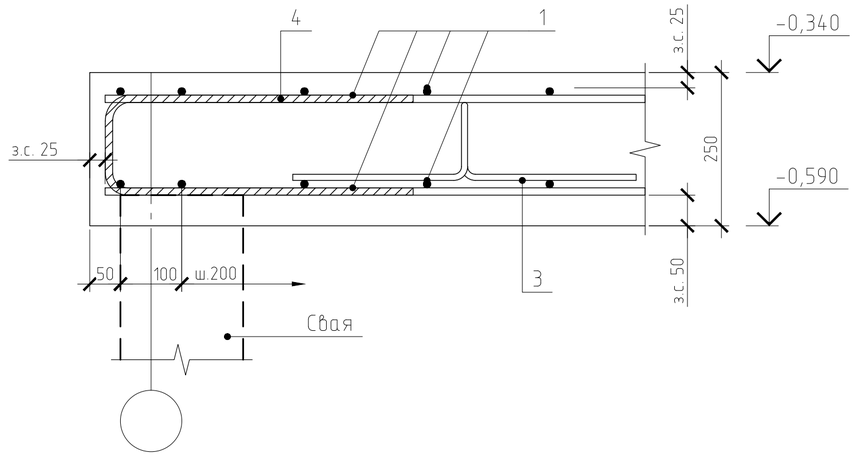

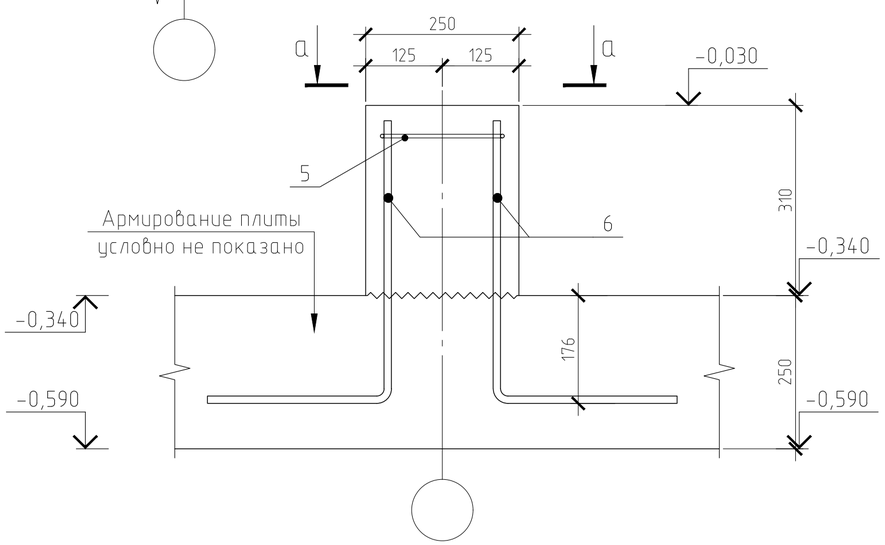

а – а

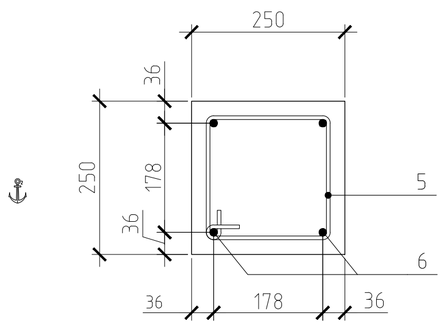




Устройство соединения бентонитового шнура



Концы соединяемых шнуров разрезать вдоль пополам на глубину нахлёста, далее надрезанные концы вложить друг в друга.

Примечания:
1. Защитный слой для рабочей арматуры принимать не менее 25мм кроме мест указанных особо.

Ведомость деталей

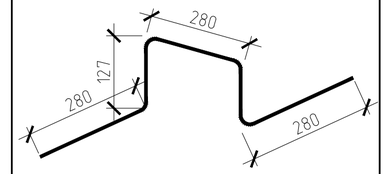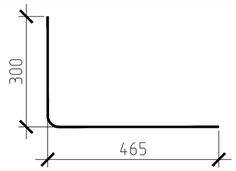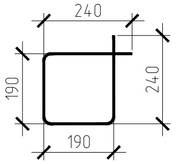
Поз.	Эскиз	Кол-во, шт.
Хп-1 ф6А240 L=944		327
Кп-1 ф12А500С L=1095		388
Сг-1 ф12А500С L=1163		242
Сг-2 ф12А500С L=765		20
Хп-2 ф6А240 L=860		5

Поз.	Обозначение	Поз.	Обозначение
1	Основное армирование ф12 А500С, шаг 200х200	5	Хп-2, см. ведомость деталей
2	Хп-1, шаг 300, см. ведомость деталей	6	Сг-2, 4шт., см. ведомость деталей
3	Кп-1, шаг 800х800, см ведомость деталей	7	Бентонитовый шнур
4	Сг-1, шаг 400, см. ведомость деталей		

						291-КЖО	
						Московская область, Истринский район	
Изм.	Кол. уч.	Лист	№ док.	Подп.	Дата		
Констр.		Москалюк А.			29.09.26	Фундамент	Стадия: Р; Лист: 10; Листов:
Проверил		Баннов Е.			29.09.26		
ГИП		Баннов Е.			29.09.26	Узлы Ф1 – Ф4	ООО "Строй Хауз"
Изм.							

Формат А3

Закладная под водоснабжение

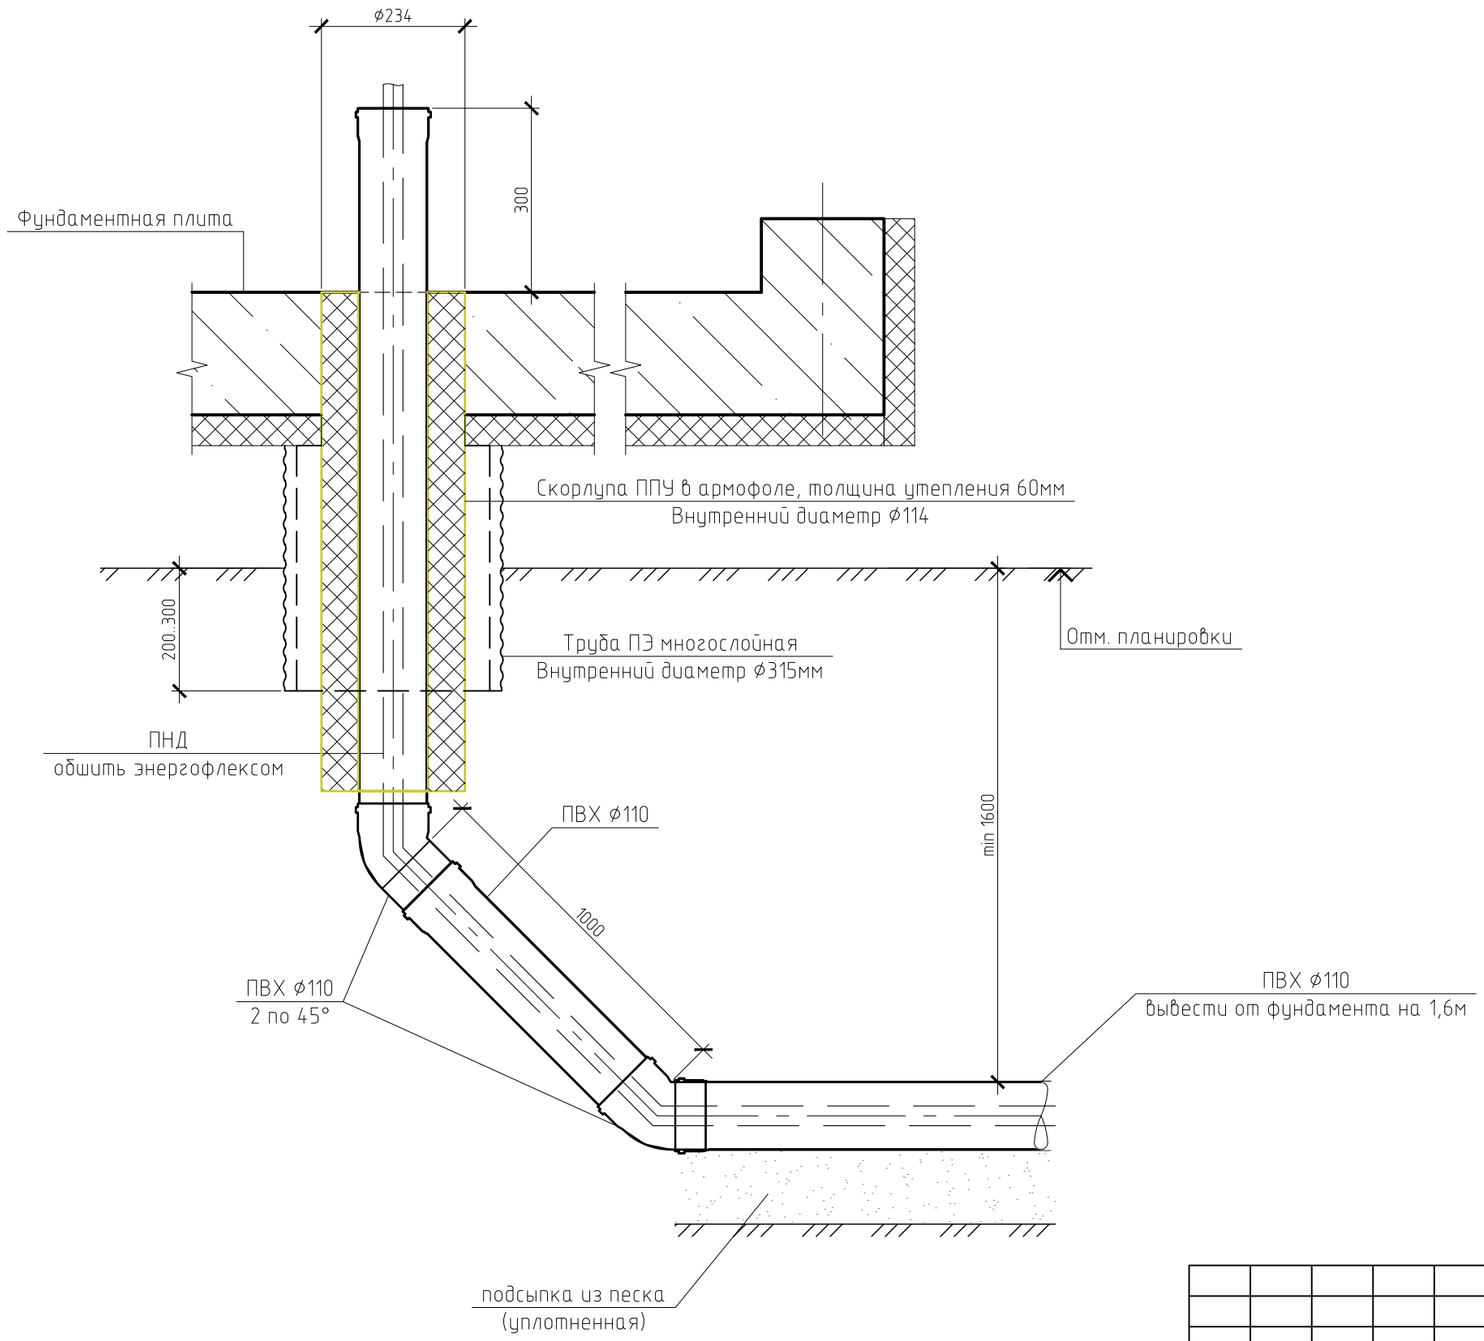


Примечания:

1. Схему расположения коммуникаций см. лист 4.

						291-КЖО		
						Московская область, Истринский район		
Изм.	Кол. уч.	Лист	№ док.	Подп.	Дата			
Констр.		Москалюк А.			29.09.26	Фундамент	Стадия	Лист	Листов
Проверил		Баннов Е.			29.09.26		Р	11	
ГИП		Баннов Е.			29.09.26	Закладная под водоснабжение	ООО "Строй Хауз"		
Изм.									

Формат А3

Закладная под канализацию

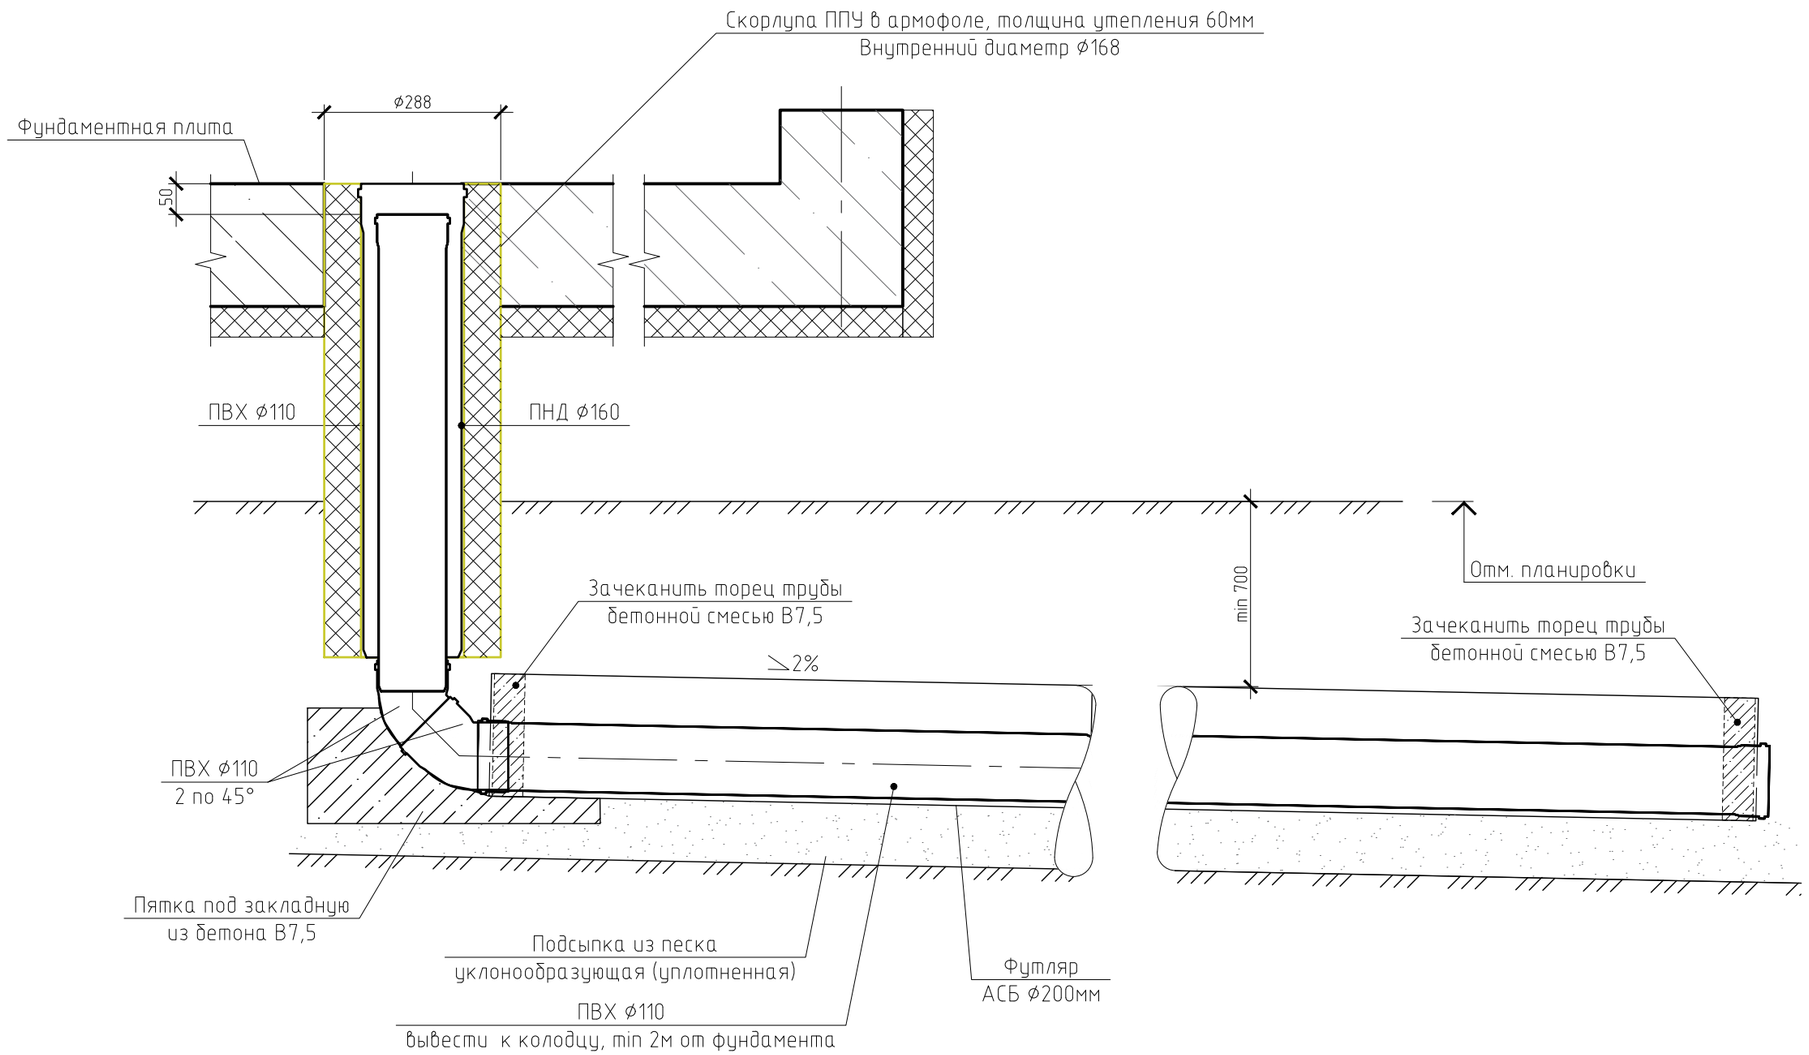


Примечания:

1. Схему расположения коммуникаций см. лист 4.

						291-КЖО		
						Московская область, Истринский район		
Изм.	Кол. уч.	Лист	№ док.	Подп.	Дата			
Констр.		Москалюк А.			29.09.26	Фундамент	Стадия	Лист	Листов
Проверил		Баннов Е.			29.09.26		Р	12	
ГИП		Баннов Е.			29.09.26	Закладная под канализацию	ООО "Строй Хауз"		
Изм.									

Формат А3

Закладная под теплотрассу ⌀ 315мм, труба ПЭ многослойная

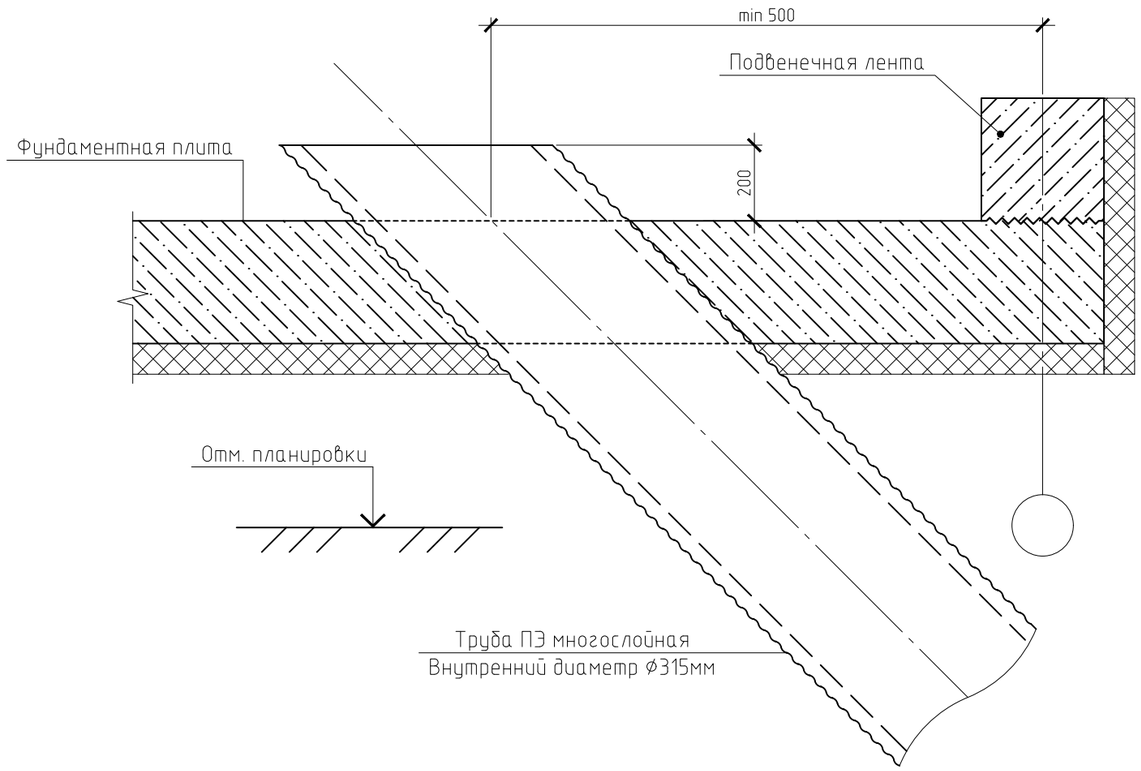


Примечания:

1. Схему расположения коммуникаций см. лист 4.


						291-КЖО		
						Московская область, Истринский район		
Изм.	Кол. уч.	Лист	№ док.	Подп.	Дата			
Констр.		Москалюк А.			29.09.26	Фундамент	Стадия	Лист	Листов
Проверил		Баннов Е.			29.09.26		Р	13	
ГИП		Баннов Е.			29.09.26	Закладная под теплотрассу	ООО "Строй Хауз"		
Изм.									

Формат А3

Закладная под эл. кабели

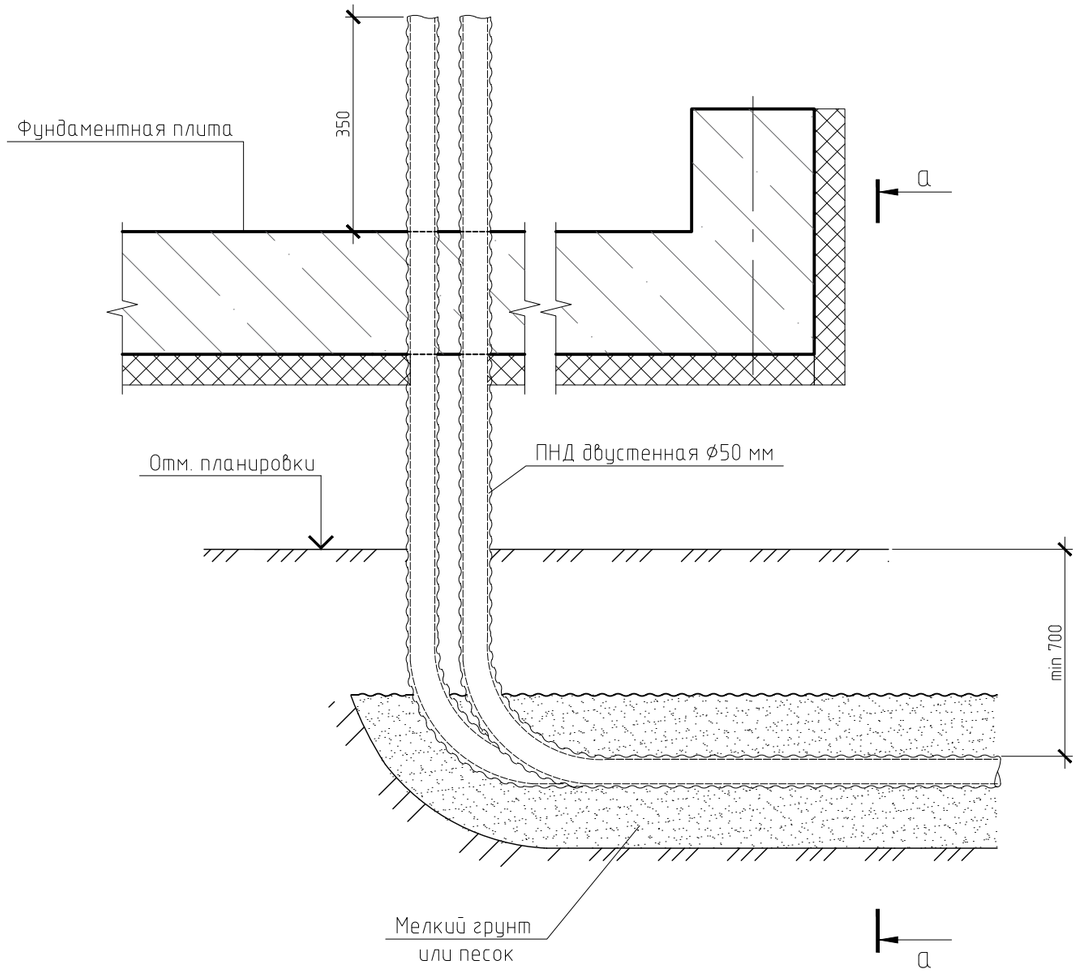

а – а

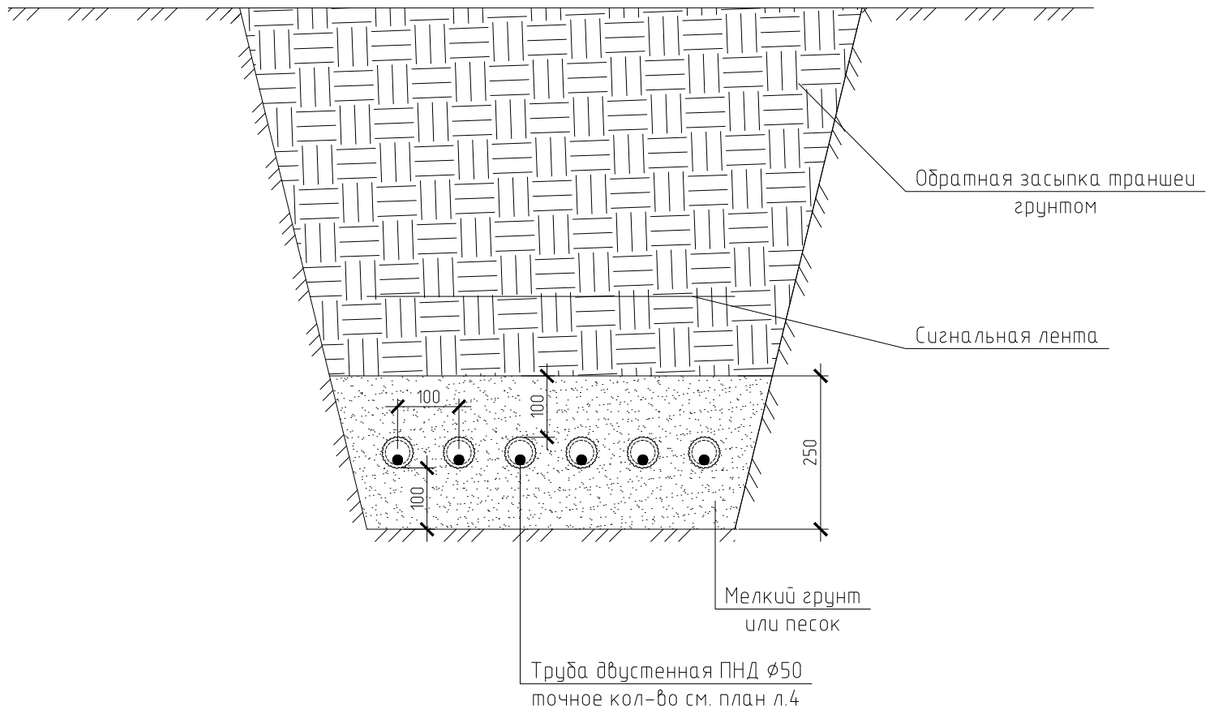

Примечания:
1. Схему расположения коммуникаций см. лист 4.

						291-КЖО		
						Московская область, Истринский район		
Изм.	Кол. уч.	Лист	№ док.	Подп.	Дата			
Констр.		Москалюк А.			29.09.26	Фундамент	Стадия	Лист	Листов
Проверил		Баннов Е.			29.09.26		Р	14	
ГИП		Баннов Е.			29.09.26	Закладная под электрокабели	ООО "Строй Хауз"		
Изм.									

Формат А3



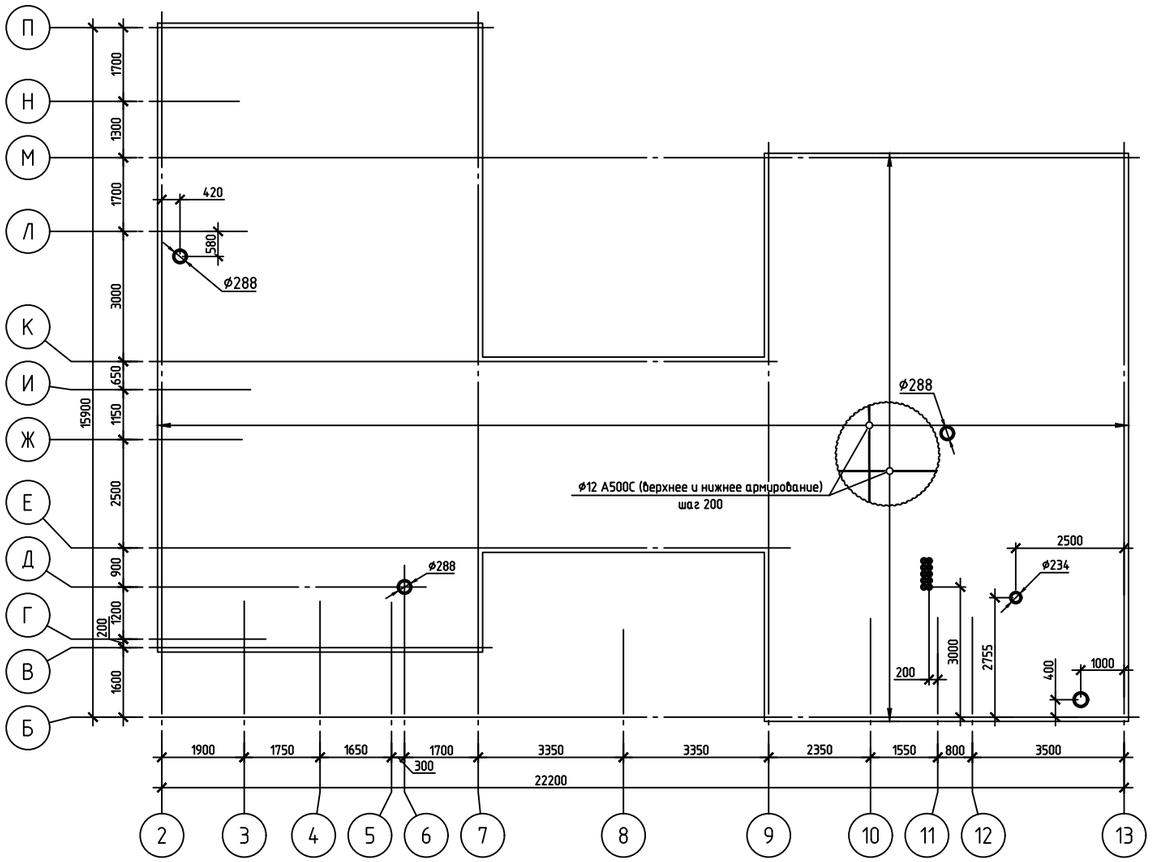



Схема усиления в местах установки закладных элементов

Внешний диаметр ≤ 160 мм (схема усиления в случае разрыва сетки)

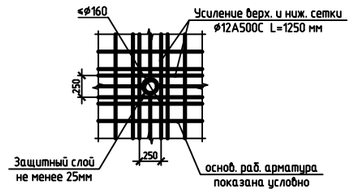


Внешний диаметр > 160 мм (схема усиления в случае разрыва сетки)

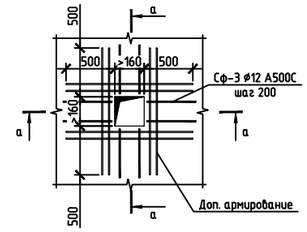

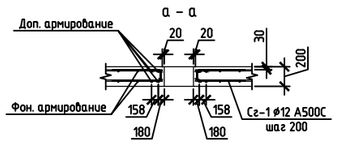

Армирование углов подвенечной ленты

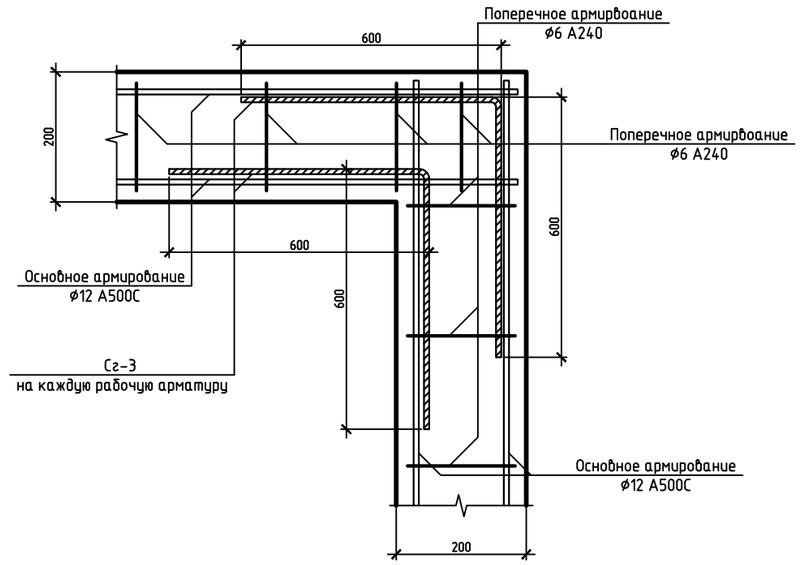

Фрагмент установки поддерживающих каркасов

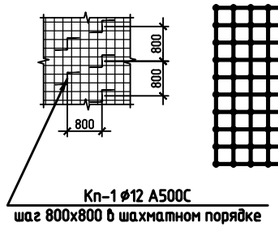


Схема вязки арматурных каркасов


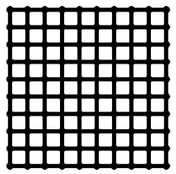


Схема стыковки продольной арматуры

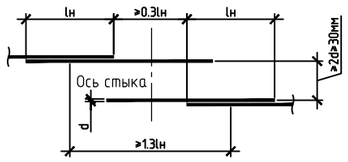

Диаметр арматуры d, мм	Длина нахлёстки lн, мм
12	≥800

Примечание:
1. Крестообразные и нахлесточные соединения стержней арматуры плиты выполнить на скрутках из отожженной вязальной проволоки диаметром 1.2–1.5мм
2. При армирование нижней и верхней зоны фундаментной плиты стержнями ø12 А500С, стыковку по длине необходимо выполнить в разбежку в соответствии с приведенной схемой стыковки арматурных стержней. При этом количество стыкуемой в одном расчетном сечении рабочей арматуры должно быть не более 50%. Допускается стыковать стержни в одном сечении, при этом lн увеличить в два раза.

Ведомость деталей	
Поз.	Эскиз
Сг-3 ø12А500С L=1200	600 / 600

							291-КЖ0
							Московская область, Истринский район
Изм.	Кол.уч.	Лист	№ док.	Подп.	Дата		
Констр.		Москалюк А.			29.09.26	Фундамент	Стадия: Р; Лист: 15; Листов:
Проверил		Баннов Е.			29.09.26		
ГИП		Баннов Е.			29.09.26	План армирования с указанием закладных	ООО "Строй Хаус"
Изм.							

Формат А2

Спецификация элементов фундамента

Поз.	Обозначение	Наименование	Кол.	Ед.изм.	Приме-чание
		Арматура			
1	ГОСТ 34028-2016	⌀12 А500С	7100	кг	
2	ГОСТ 34028-2016	⌀6 А240	200	кг	
		Материалы			
3	ГОСТ 19804-2021	Свая С40.20-3	74	шт.	
4	ГОСТ 26633-2015	Бетон В22,5	72.8	м3	
5	СТО 72746455-3.3.1-2012	Пенополистирол экструдированный	16.24	м3	
6		Геотекстиль	500	м2	
7		Песок	109.6	м3	
8		Дюбель крепежный "Грибок"	2343	шт.	
9		Вязальная проволока ⌀1,2	150	кг	
10		Стульчик с подкладкой	1380	шт.	
11		Звездочка	600	шт.	
12		Бентонитовый шнур	95	п.м.	
13		Труба канализационная ПВХ ⌀110мм L=1000мм	5	шт	
14		Труба канализационная ПВХ ⌀110мм L=2000мм	3	шт	
15		Труба канализационная ПВХ ⌀110мм L=3000мм	7	шт	
16		Отвод ⌀110мм 45 градусов	17	шт	
17		Заглушка трубы ПВХ ⌀110мм	14	шт	
18		Труба двустенная гофрированная ПНД d315/276 мм 2 м SN8 с раструбом терракот	3	шт	
19		Дно универсальное ⌀300мм	3	шт	
20		Крышка колодца ⌀300мм	3	шт	
21		Труба двустенная гофрированная ПНД/ПВД d63/52 мм SN6 с протяжкой	100	п.м.	
22		Труба ПВХ ⌀315мм L=1000мм	1	шт	
23		Труба ПВХ ⌀315мм L=2000мм	1	шт	
24		Труба ПНД ⌀160мм L=2000мм	3	шт	
25		Труба асбестоцементная ⌀200мм L=5000 мм	2	шт	
26		Муфта асбестоцементной трубы	1	шт	
27		Скорлупа ППУ в армофоле внутр. Ø114мм, внешн.Ø234мм	2	п.м.	
28		Скорлупа ППУ в армофоле внутр. Ø168мм, внешн.Ø288мм	6	п.м.	
29		Сигнальная лента	100	п.м.	
30		Пескобетон М150	200	кг	

Изм.	Кол. уч.	Лист	№ док.	Подп.	Дата	291-КЖО			
						Московская область, Истринский район			
Констр.		Москалюк А.			29.09.26	Фундамент	Стадия	Лист	Листов
Проверил		Баннов Е.			29.09.26		Р	16	
ГИП		Баннов Е.			29.09.26	Спецификация	ООО "Строй Хауз"		
Изм.									

Формат А3